



This 2D drawing is extracted from 3D BIM Model

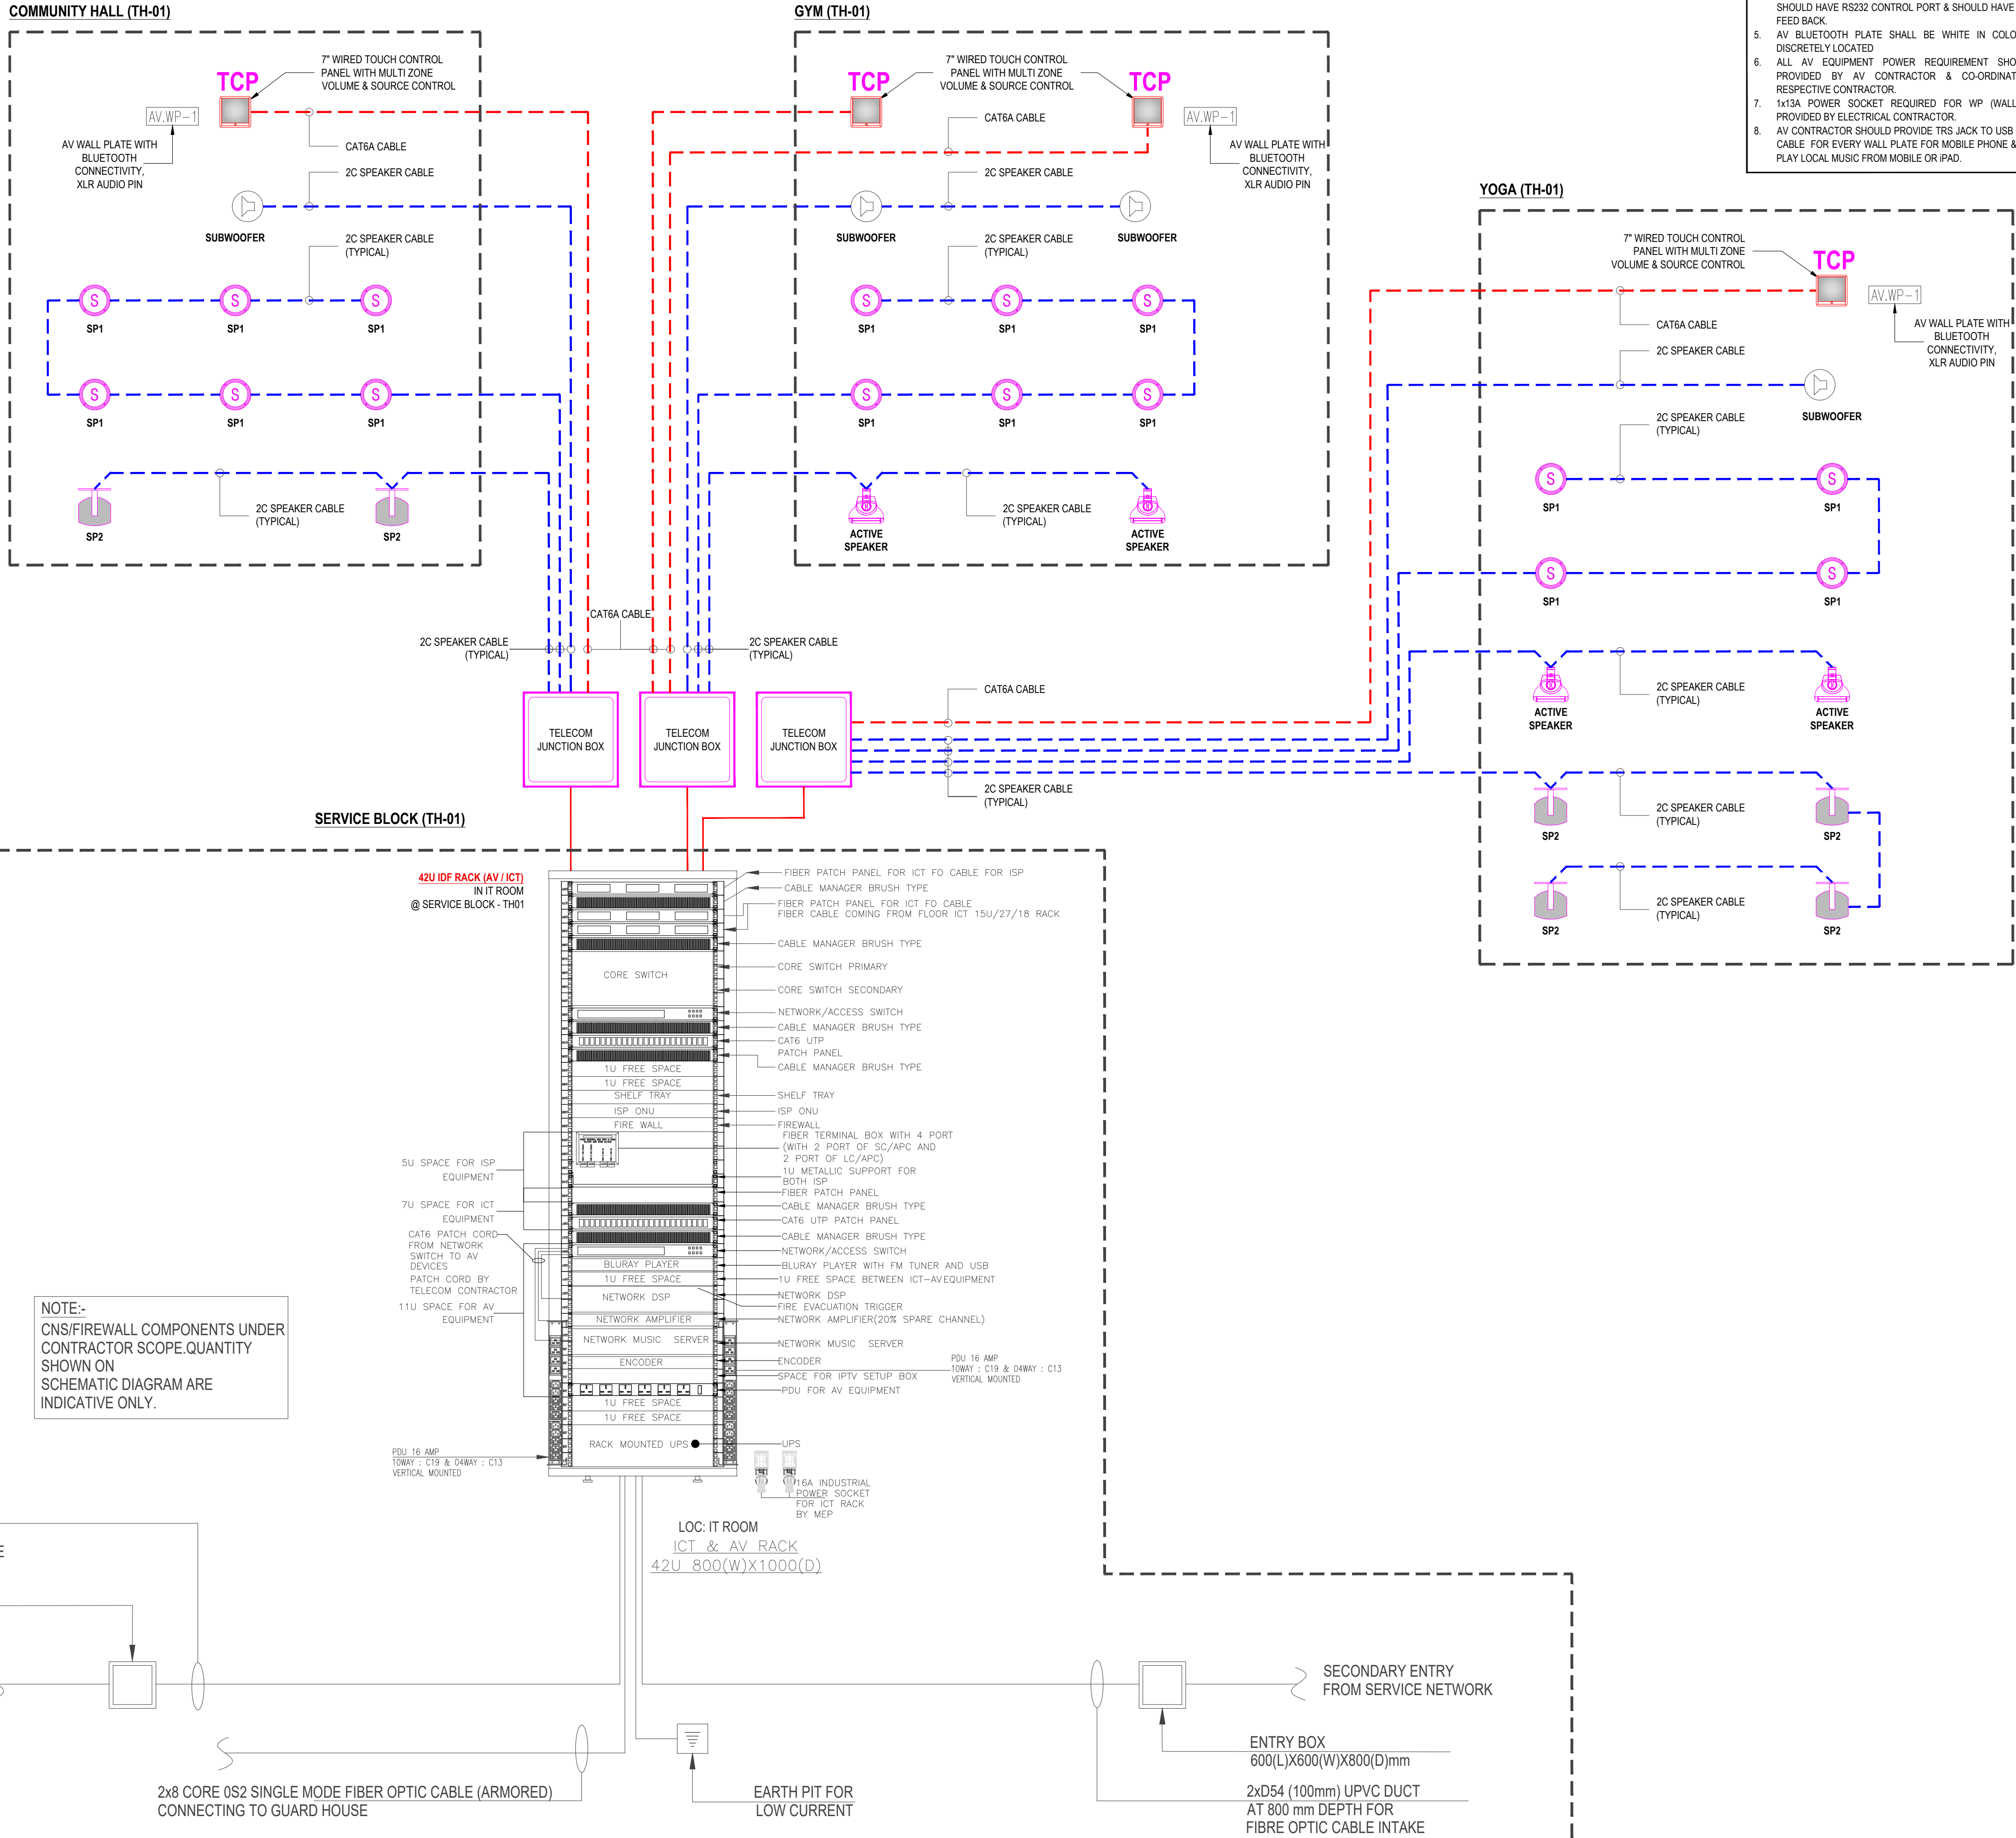

Key Plan

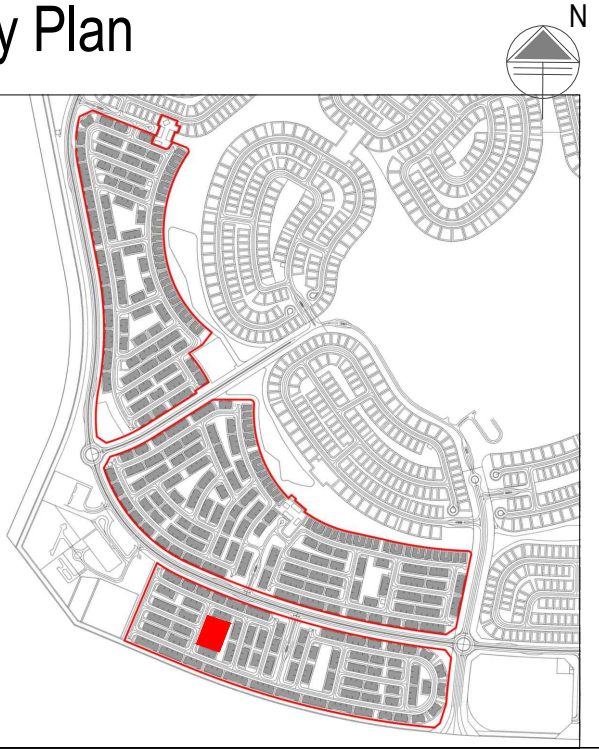

General Notes

01. Do not Scale The Drawings. Follow (The MM) Written Dimensions Unless Otherwise Mentioned.
02. Each Drawing Shall be Read in Conjunction With all Other Drawings, Specification & the General Standard Details. In Case of Any Discrepancies Bring it to the Knowledge of Engineer and Same to be Resolved Prior to Execution of Work.
03. Dimensions Shown on These Drawings are Structural Dimensions Unless Noted Otherwise.
04. All Levels Indicated On These Drawings are Levels as per the the Survey Datum, Same Should be Verified at Site Prior to Execution of Work.
05. All Levels Indicated On These Drawings are Based On Design Level, Which is Equivalent to Datum Level and Same Should be Verified at Site Prior to Execution of Work.



09	10/03/2026	JP	TENDER SUBMISSION
No.	Date	Initials	Description
REVISIONS / ISSUE			
THIS DRAWING MUST NOT BE REPRODUCED IN WHOLE OR IN PART WITHOUT THE PRIOR APPROVAL OF ARIF & BINTOAK			
Status			
TENDER SUBMISSION			
Client			
EMAAR			
Lead Consultant			
عارف وبن طوق Arif & BintOak consulting architects & engineers POST BOX 3676 DUBAI UAE TEL: 04-3972886 FAX: 04-3973652 POST BOX 42961 ABU DHABI UAE TEL: 02-4346691 -arifaab@arifaab.net.ae			
Security Consultant			
INTERNATIONAL ELECTRONIC SECURITY TEL: 04 397 0757, FAX: 04 397 0754 P.O. BOX 12734 DUBAI - U.A.E ENQUIRIES@IESCONSULTING.AE AUDIT@IESCONSULTING.AE WWW.IESCONSULTING.AE			
Project Title:			

Standalone Villas TH-1, TH-2, and TH-3
at Grand Polo Club & Resort, Dubai,
UAE

Discipline : AUDIO VISUAL (AV)			
Drawing title: AUDIO VISUAL (AV) SYSTEM SINGLE LINE DIAGRAM COMMUNITY CENTER - TH-01			
Architectural Engineer	Electrical Engineer	Structural Engineer	
MUSTAFA ABID	MARWAN MOHD.	RIHAM RAMADAN	
Registration # 5847	Registration # 80102	Registration # 105092	
Scale(s): NTS	Date drawn: 10/03/2026	Project no: 1857	
Drawn by: JP	Checked: MM	Approved : JR	
Drawing Number : GPCR-TH01-IES-CC1-SLD-AVC-AV-2000-00			