


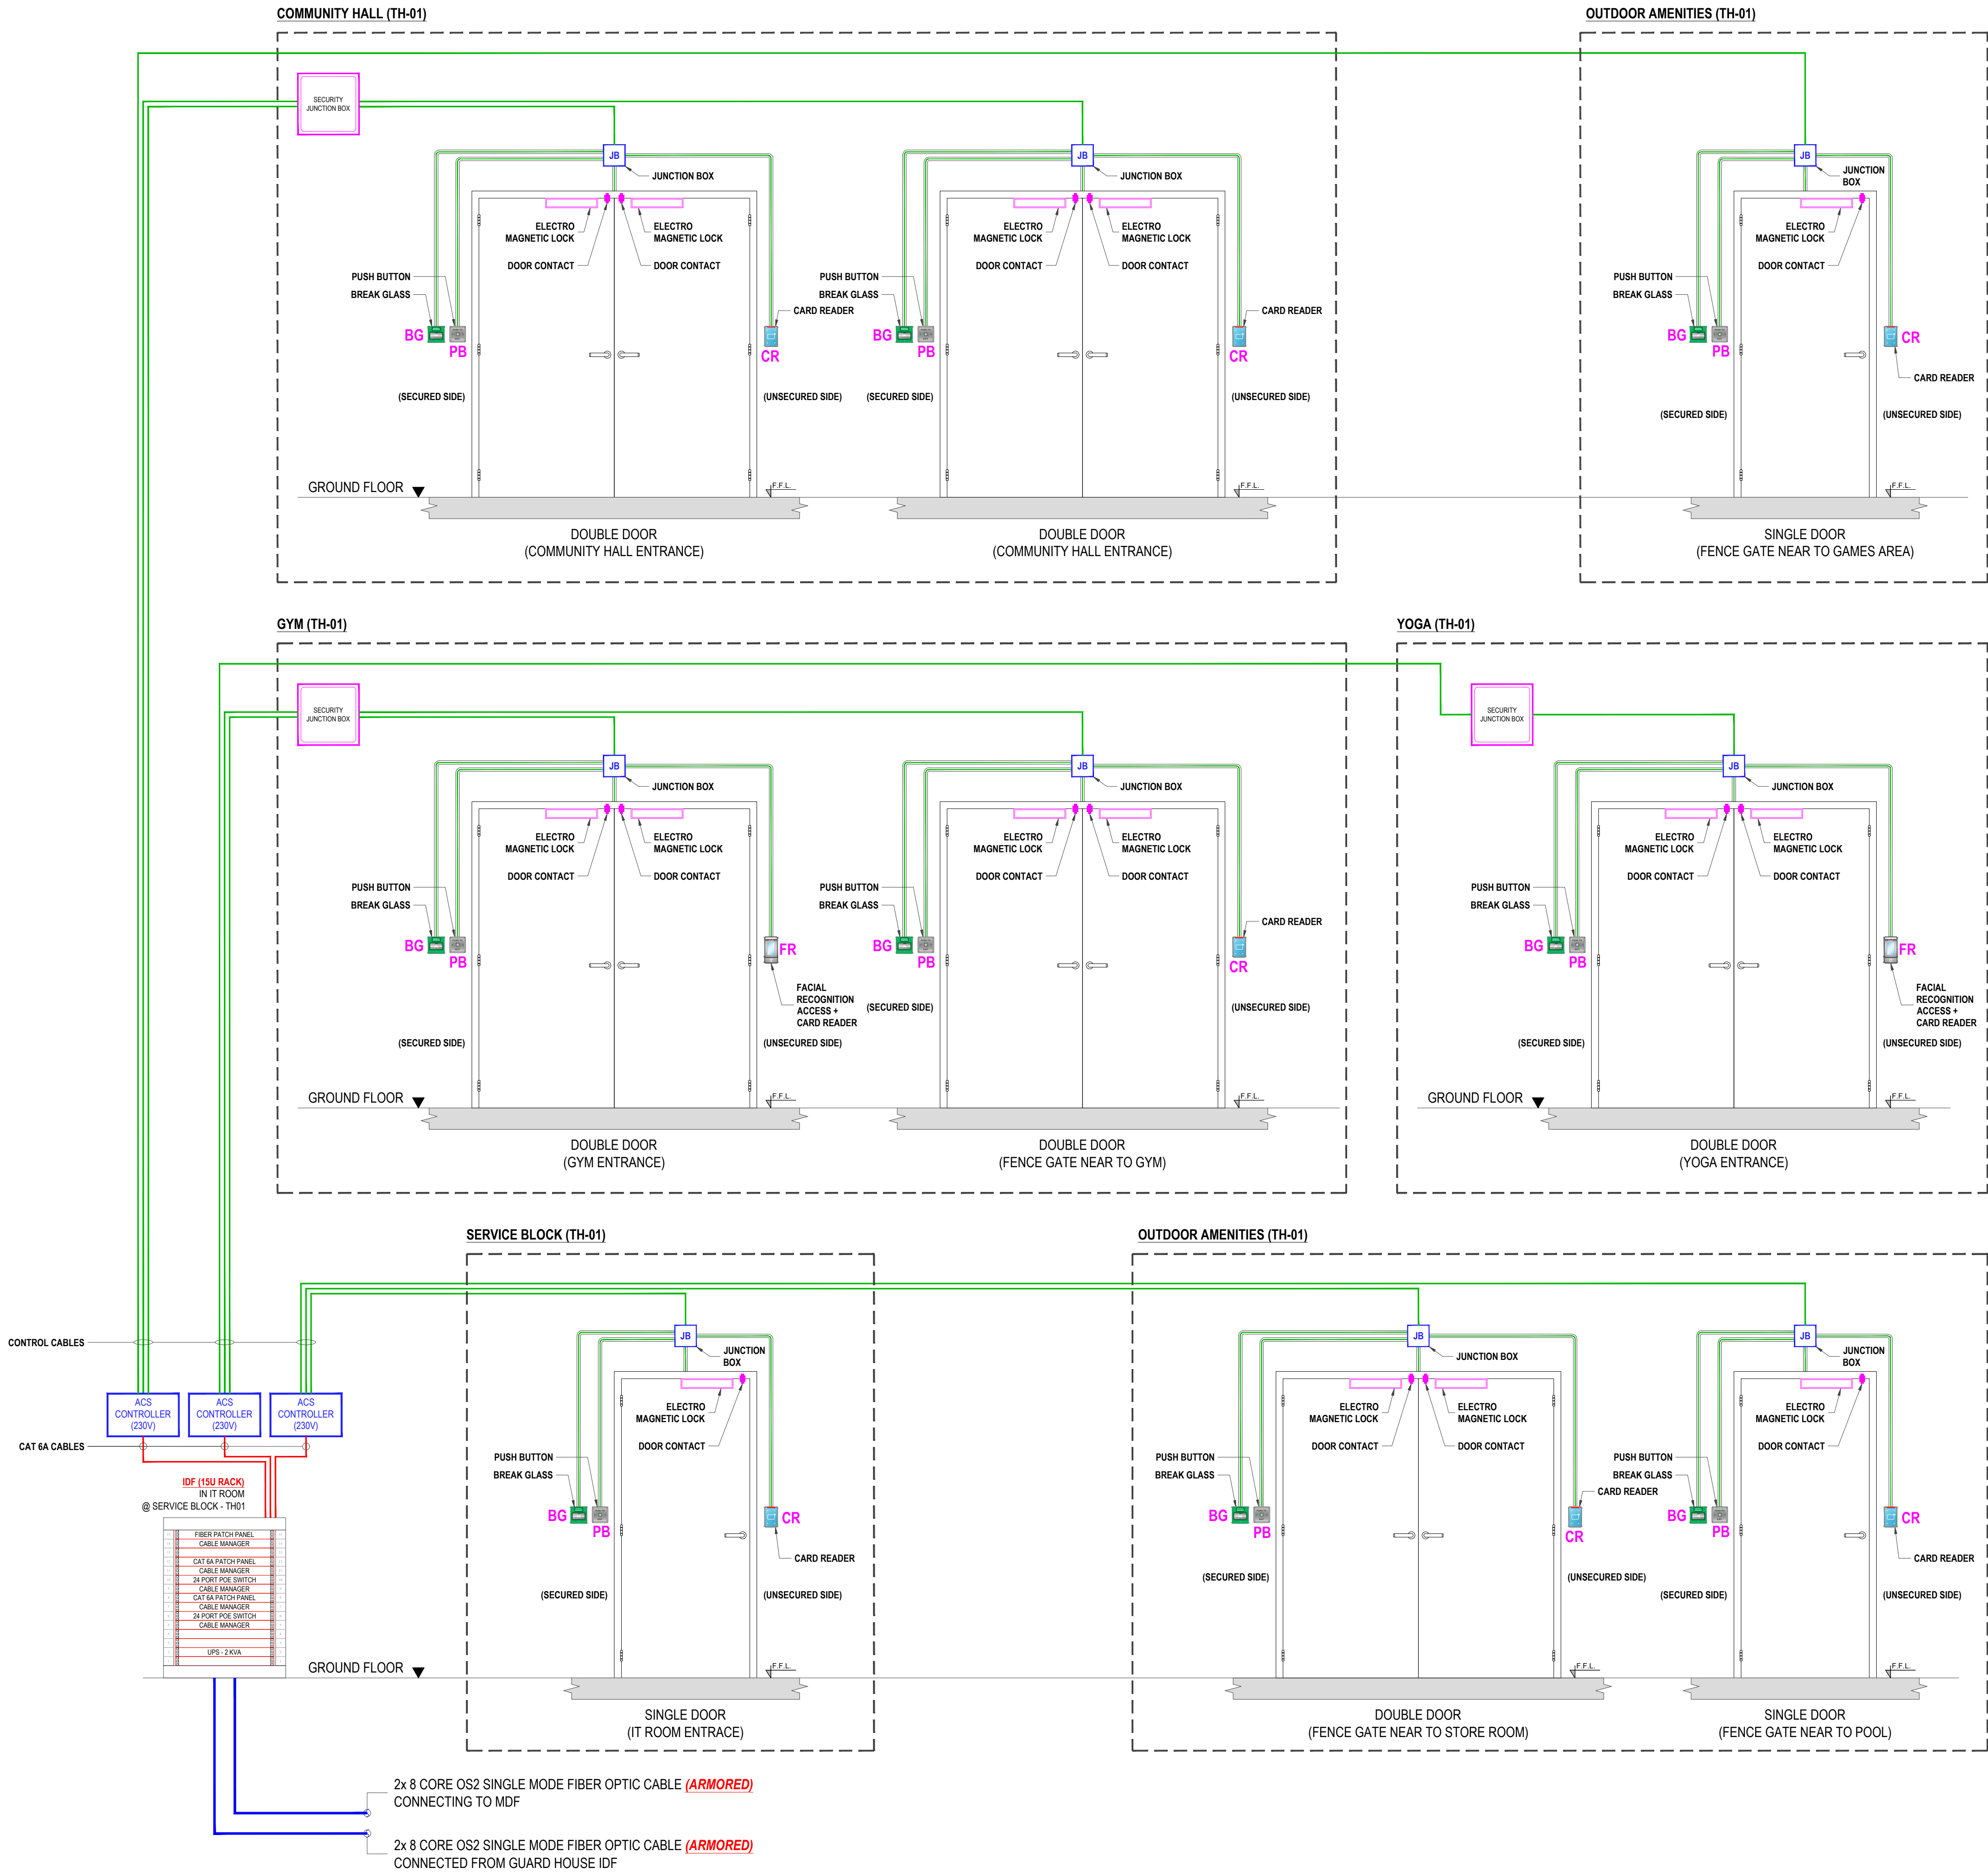


Key Plan

- IES NOTE: CCTV + INTRUSION + ACCESS CONTROL**
- THE LOCATIONS OF CCTV, ALARM, AND ACS COMPONENTS ARE INDICATED APPROXIMATELY ON THE DRAWINGS AND ARE SUBJECT TO ON-SITE VERIFICATION.
 - EXACT LOCATIONS AND HEIGHTS OF COMPONENTS WILL BE FINALIZED IN COORDINATION WITH THE CONTRACTOR ON-SITE, CONSIDERING BUILDING LAYOUT, INTERIOR DESIGN, DECORATION, AND ANY OTHER RELEVANT SERVICES OR COMPONENTS.
 - ON-SITE, COORDINATION WITH THE CONTRACTOR IS ESSENTIAL TO ADDRESS ANY POTENTIAL OBSTRUCTIONS TO THE CAMERA'S FIELD OF VIEW, IN COMPLIANCE WITH DUBAI LAW 12/2016, AS WELL AS TO MITIGATE ELECTROMAGNETIC INTERFERENCE (EMI) IMPACTING ELECTRONIC SECURITY COMPONENTS.
 - THIS DESIGN WILL BECOME INVALID IF THERE ARE ANY MODIFICATIONS TO THE ARCHITECTURAL PLANS OR CHANGES IN LEGAL REQUIREMENTS.
 - LOW-LIGHT AREAS SHOULD BE EQUIPPED WITH INFRARED (IR) OR NIGHT VISION CAMERAS TO ENSURE PROPER COVERAGE AND VISIBILITY.

ACCESS CONTROL SYSTEM SCHEDULE				
SYMBOL	DESCRIPTION	ACS QTY.	NO. OF FLOOR	TOTAL NO. OF ACS
CR	CARD READER	7	1	7
FR	FACE RECOGNITION ACCESS + CARD READER	2	1	2
BG	BREAK GLASS	9	1	9
PB	PUSH BUTTON	9	1	9
DC	DOOR CONTACT	15	1	15
EML	ELECTRO MAGNETIC LOCK	15	1	15
ACP	ACCESS CONTROL SYSTEM PANEL	3	1	3

LEGEND		
SYMBOL	DESCRIPTION	TOTAL NO.
	JUNCTION BOX FOR SECURITY (300mm x 150mm x 150mm)	3
	15U SECURITY RACK (WALL MOUNTED)	1

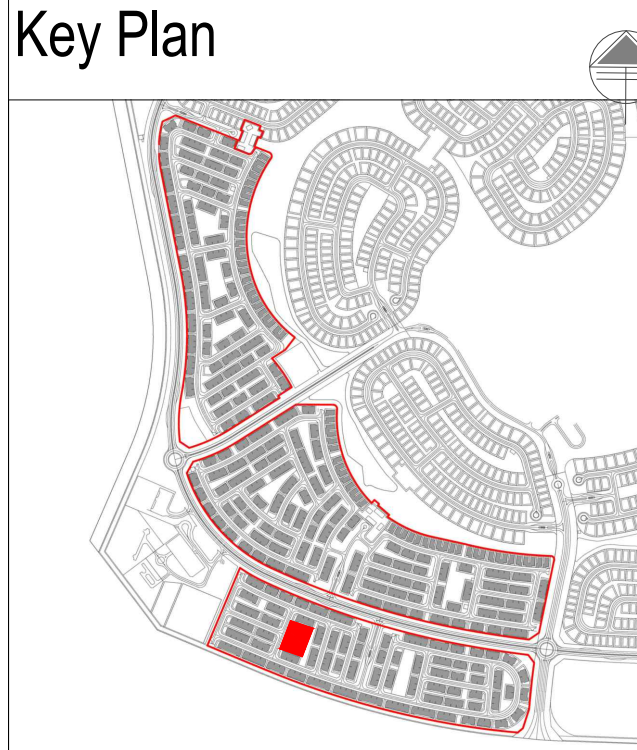

- General Notes**
- Do not Scale The Drawings. Follow (The MM) Written Dimensions Unless Otherwise Mentioned.
 - Each Drawing Shall be Read in Conjunction With all Other Drawings, Specification & the General Standard Details. In Case of Any Discrepancies Bring it to the Knowledge of Engineer and Same to be Resolved Prior to Execution of Work.
 - Dimensions Shown on These Drawings are Structural Dimensions. Unless Noted Otherwise.
 - All Levels Indicated On These Drawings are Levels as per the the Survey Datum, Same Should be Verified at Site Prior to Execution of Work.
 - All Levels Indicated On These Drawings are Based On Design Level, Which is Equivalent to Datum Level and Same Should be Verified at Site Prior to Execution of Work.

10/9/2025 3:20:21 PM

© AB 1 A1 Title Block. BIM Standard Ver. 2.0

10/9/2025 3:20:21 PM

© AB 1 A1 Title Block. BIM Standard Ver. 2.0

