


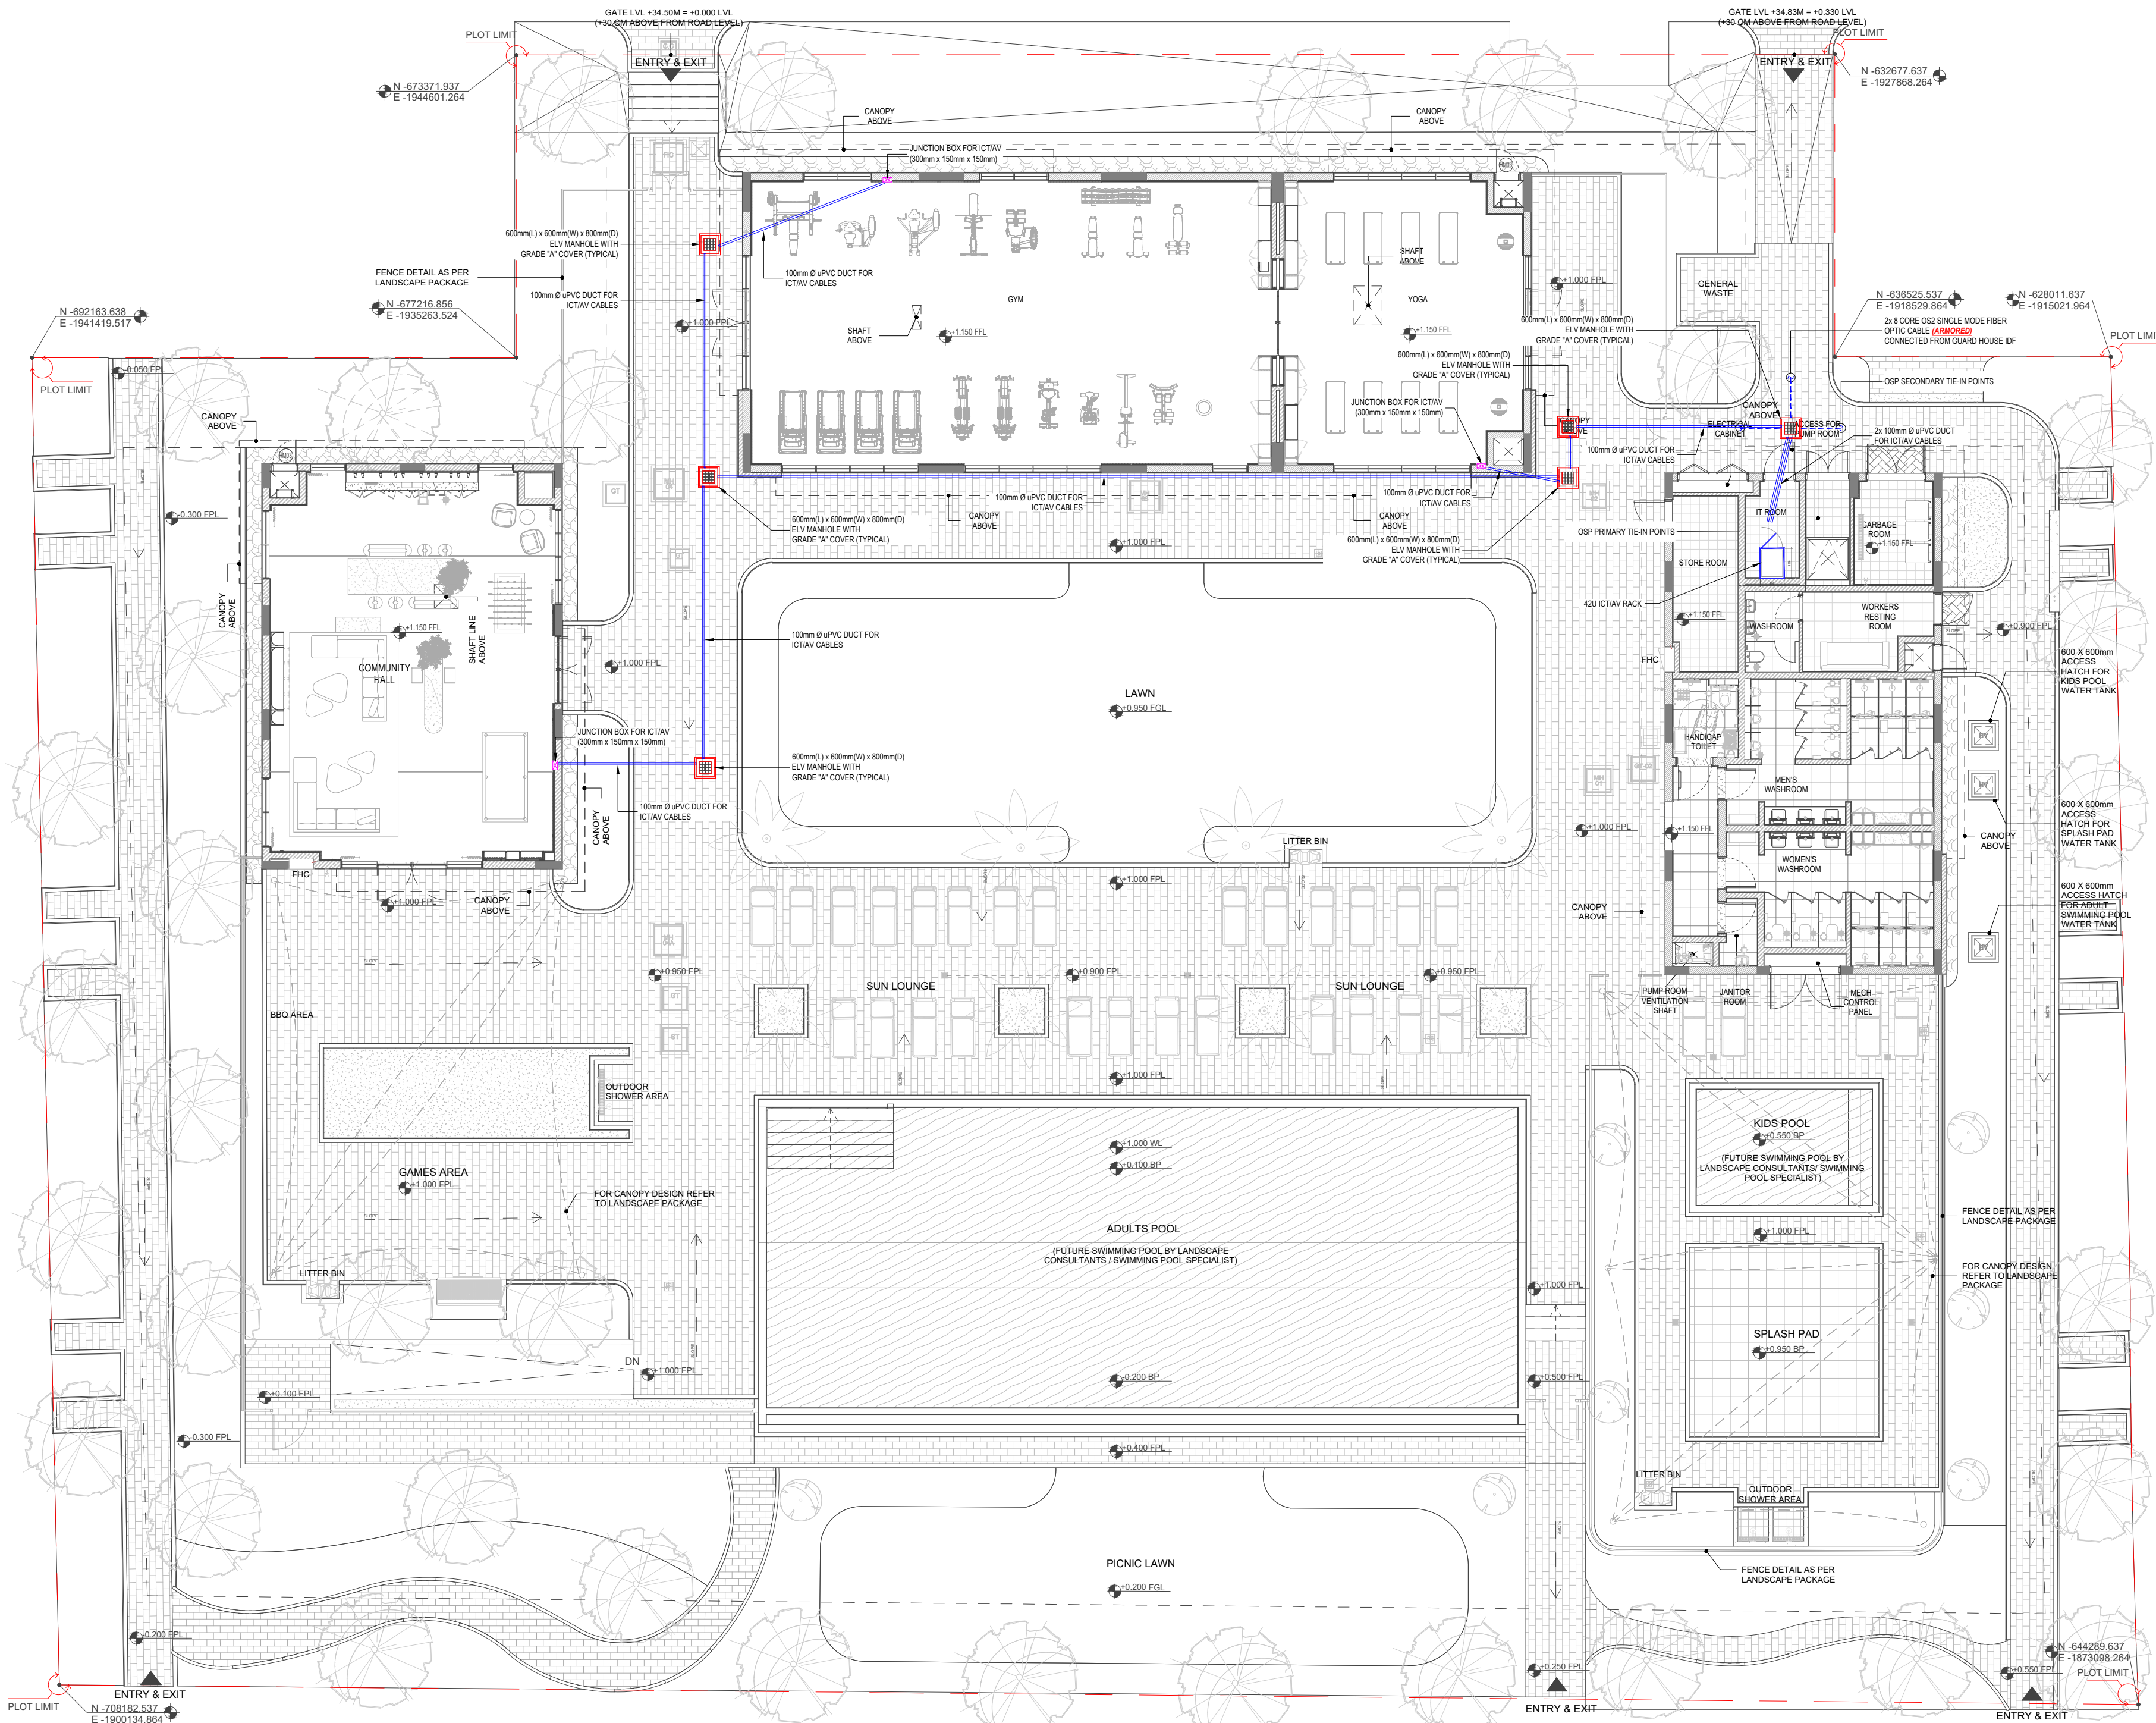

LEGEND:	
	PLOT LIMIT
	BUILDING DETACH LIMIT

Key Plan



General Notes

- Do not Scale The Drawings. Follow (The MM) Written Dimensions Unless Otherwise Mentioned.
- Each Drawing Shall be Read in Conjunction With all Other Drawings, Specification & the General Standard Details. In Case of Any Discrepancies Bring it to the Knowledge of Engineer and Same to be Resolved Prior to Execution of Work.
- Dimensions Shown on These Drawings are Structural Dimensions Unless Noted Otherwise.
- All Levels Indicated On These Drawings are Levels as per the the Survey Datum, Same Should be Verified at Site Prior to Execution of Work.
- All Levels Indicated On These Drawings are Based On Design Level, Which is Equivalent to Datum Level and Same Should be Verified at Site Prior to Execution of Work.



No.	Date	Initials	Description
09	10/03/2026	JP	TENDER SUBMISSION

REVISIONS / ISSUE

THIS DRAWING MUST NOT BE REPRODUCED IN WHOLE OR IN PART WITHOUT THE PRIOR APPROVAL OF ARIF & BINTOAK

TENDER SUBMISSION

Client
EMAAR

Lead Consultant
عارف وبن طوق
Arif&Bintoak
consulting architects & engineers
POST BOX 3676 DUBAI UAE TEL: 04-3727886 FAX: 04-3727887
POST BOX 42981 ABU DHABI UAE TEL: 02-434669 arif@arifa-bintoak.net.ae

Security Consultant
INTERNATIONAL ELECTRONIC SECURITY
TEL 04 397 0757, FAX 04 397 0754
P.O. BOX 12734 DUBAI - U.A.E
ENQUIRIES@IESCONSULTING.AE
AUDIT@IESCONSULTING.AE
WWW.IESCONSULTING.AE

Project Title:

Proposed Residential Townhouses and Standalone Villas TH-1, TH-2, and TH-3 at Grand Polo Club & Resort, Dubai, UAE

Discipline : ICT / AV

Drawing title:
SETTING-OUT PLAN
ICT/AV SYSTEM LAYOUT
COMMUNITY CENTER - TH-01

Architectural Engineer	Electrical Engineer	Structural Engineer
MUSTAFA ABID	MARWAN MOHD.	RIHAM RAMADAN
Registration # 5847	Registration # 80102	Registration # 105092
Scale(s):	Date drawn:	Project no:
1 : 150	10/03/2026	1857
Drawn by:	Checked:	Approved:
JP	MM	JR

Drawing Number : GPCR-TH01-IES-PL-CC-1-ICT-IT-0000-00