



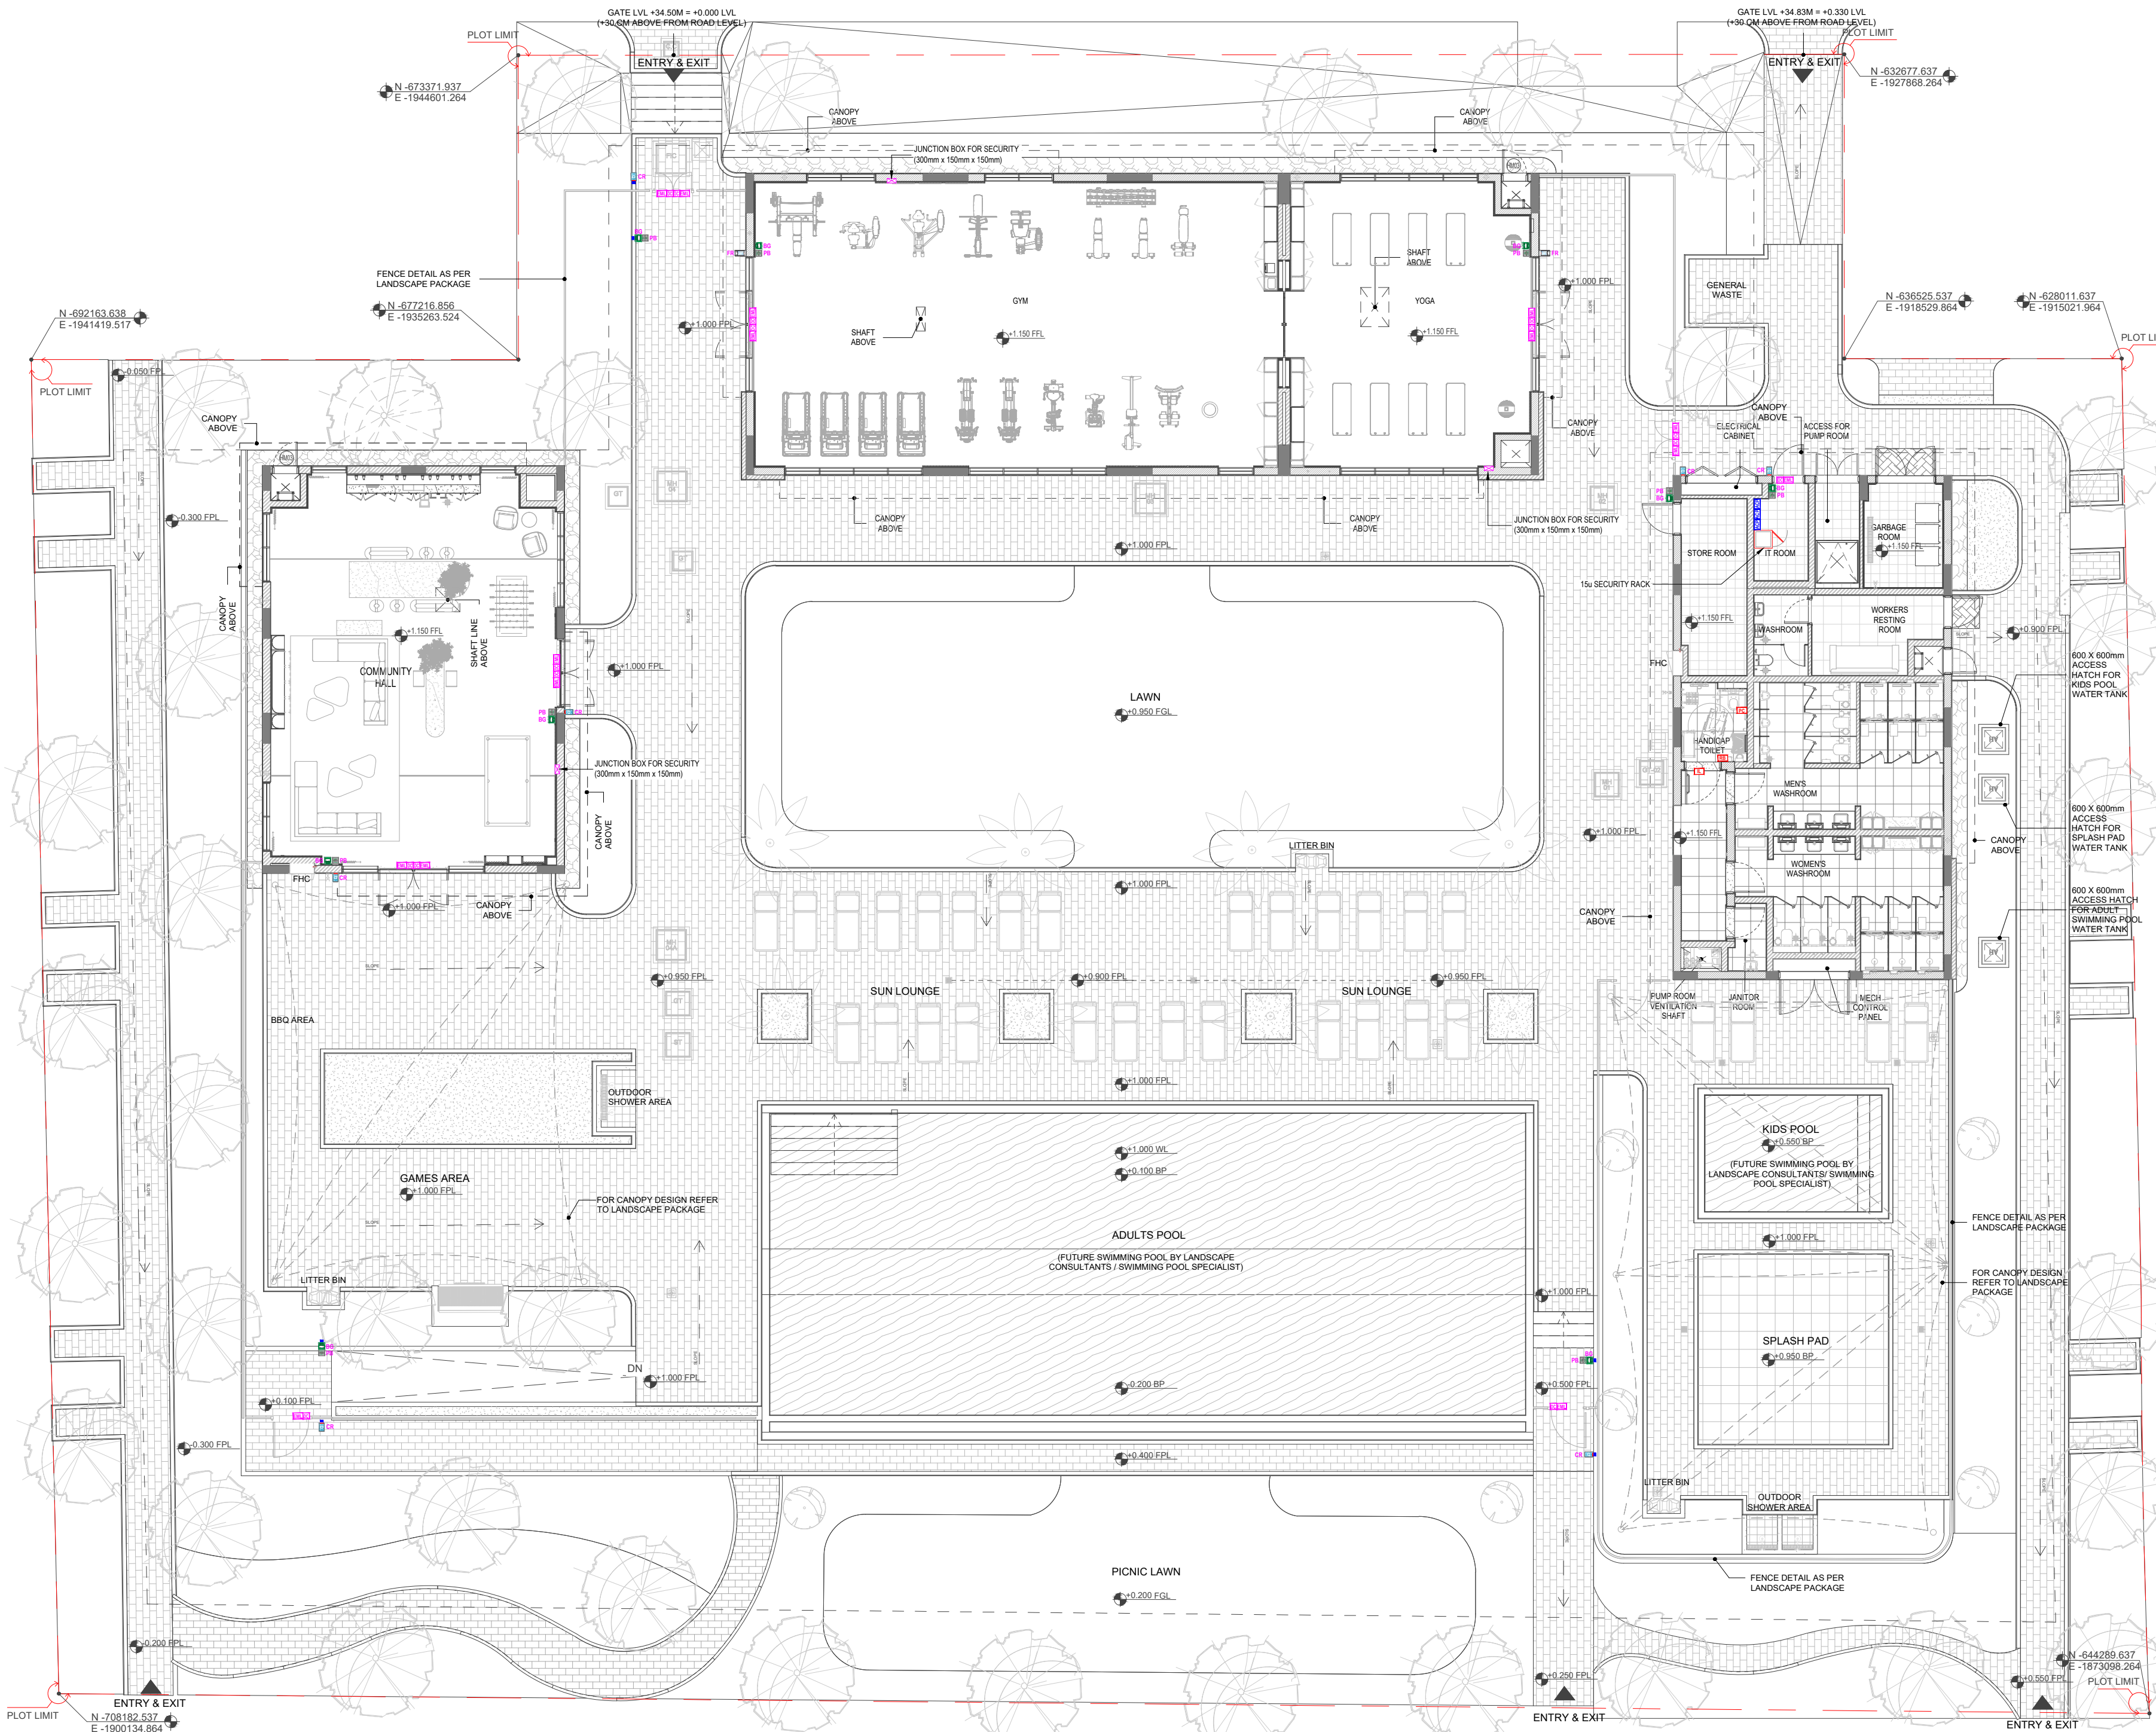

- IES NOTE: CCTV + INTRUSION + ACCESS CONTROL**
- THE LOCATIONS OF CCTV, ALARM, AND ACS COMPONENTS ARE INDICATED APPROXIMATELY ON THE DRAWINGS AND ARE SUBJECT TO ON-SITE VERIFICATION.
 - EXACT LOCATIONS AND HEIGHTS OF COMPONENTS WILL BE FINALIZED IN COORDINATION WITH THE CONTRACTOR ON-SITE, CONSIDERING BUILDING LAYOUT, INTERIOR DESIGN, DECORATION, AND ANY OTHER RELEVANT SERVICES OR COMPONENTS.
 - ON-SITE COORDINATION WITH THE CONTRACTOR IS ESSENTIAL TO ADDRESS ANY POTENTIAL OBSTRUCTIONS TO THE CAMERA'S FIELD OF VIEW, IN COMPLIANCE WITH DUBAI LAW 12/2016, AS WELL AS TO MITIGATE ELECTROMAGNETIC INTERFERENCE (EMI) IMPACTING ELECTRONIC SECURITY COMPONENTS.
 - THIS DESIGN WILL BECOME INVALID IF THERE ARE ANY MODIFICATIONS TO THE ARCHITECTURAL PLANS OR CHANGES IN LEGAL REQUIREMENTS.
 - LOW-LIGHT AREAS SHOULD BE EQUIPPED WITH INFRARED (IR) OR NIGHT VISION CAMERAS TO ENSURE PROPER COVERAGE AND VISIBILITY.

ACCESS CONTROL SYSTEM SCHEDULE				
SYMBOL	DESCRIPTION	ACS QTY.	NO. OF FLOOR	TOTAL NO. OF ACS
CR	CARD READER	7	1	7
FR	FACE RECOGNITION ACCESS + CARD READER	2	1	2
BG	BREAK GLASS	9	1	9
PB	PUSH BUTTON	9	1	9
DC	DOOR CONTACT	15	1	15
EML	ELECTRO MAGNETIC LOCK	15	1	15
ACP	ACCESS CONTROL SYSTEM PANEL	3	1	3
PC	DTA PULL CORD	1	1	1
RB	DTA RESET BUTTON	1	1	1
IL	DTA INDICATION LIGHT	1	1	1

LEGEND		
SYMBOL	DESCRIPTION	TOTAL NO.
	ACCESS CONTROL POLE	6
	JUNCTION BOX FOR SECURITY (300mm x 150mm x 150mm)	3
	15U SECURITY RACK (WALL MOUNTED)	1

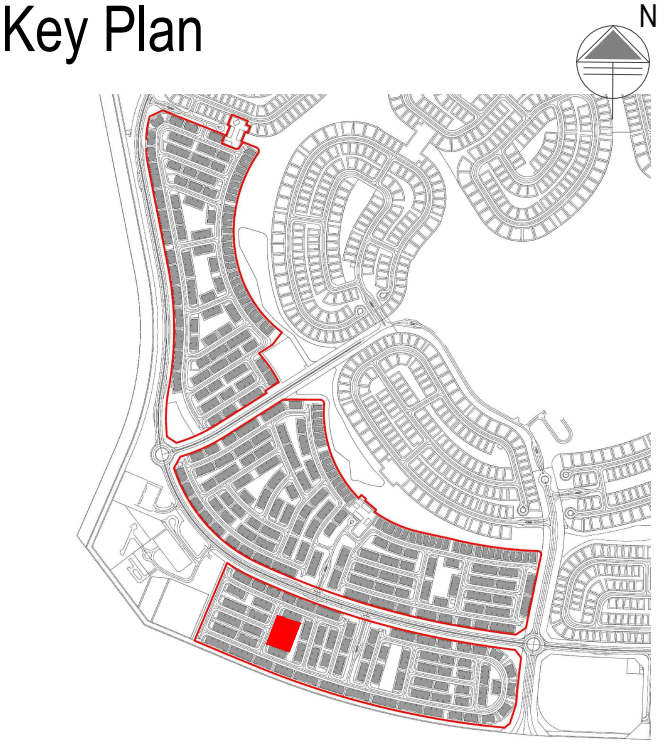

- General Notes**
- Do not Scale The Drawings. Follow (The MM) Written Dimensions Unless Otherwise Mentioned.
 - Each Drawing Shall be Read in Conjunction With all Other Drawings, Specification & the General Standard Details. In Case of Any Discrepancies Bring it to the Knowledge of Engineer and Same to be Resolved Prior to Execution of Work.
 - Dimensions Shown on These Drawings are Structural Dimensions, Unless Noted Otherwise.
 - All Levels Indicated On These Drawings are Levels as per the Survey Datum, Same Should be Verified at Site Prior to Execution of Work.
 - All Levels Indicated On These Drawings are Based On Design Level, Which is Equivalent to Datum Level and Same Should be Verified at Site Prior to Execution of Work.



09	10/03/2026	JP	TENDER SUBMISSION
No.	Date	Initials	Description

REVISIONS / ISSUE

THIS DRAWING MUST NOT BE REPRODUCED IN WHOLE OR IN PART WITHOUT THE PRIOR APPROVAL OF ARIF & BINTOAK

Status: TENDER SUBMISSION

Client: EMAAR

Lead Consultant: عارف وبن طوق
Arif & Bintok
consulting architects & engineers
POST BOX 3676 DUBAI, UAE TEL: 04-3972886 FAX: 04-3973982
POST BOX 42981 ABU DHABI, UAE TEL: 02-434669 arifbintok@emirates.net.ae

Security Consultant: INTERNATIONAL ELECTRONIC SECURITY
TEL 04 397 0757, FAX 04 397 0754
P.O. BOX 12734 DUBAI - U.A.E
ENQUIRIES@IESCONSULTING.AE
AUDIT@IESCONSULTING.AE
WWW.IESCONSULTING.AE

Project Title:

Proposed Residential Townhouses and Standalone Villas TH-1, TH-2, and TH-3 at Grand Polo Club & Resort, Dubai, UAE

Discipline: SECURITY

Drawing title: OVERALL GROUND FLOOR PLAN ACS SYSTEM LAYOUT
COMMUNITY CENTER - TH-01

Architectural Engineer	Electrical Engineer	Structural Engineer
MUSTAFA ABID	MARWAN MOHD.	RIHAM RAMADAN
Registration # 5847	Registration # 80102	Registration # 105092
Scale(s): 1 : 150	Date drawn: 10/03/2026	Project no: 1857
Drawn by: JP	Checked: MM	Approved: JR

Drawing Number: GPCR-TH01-IES-PL-CC1-SEC-ACS-0001-00