


This 2D drawing is extracted from 3D BIM Model

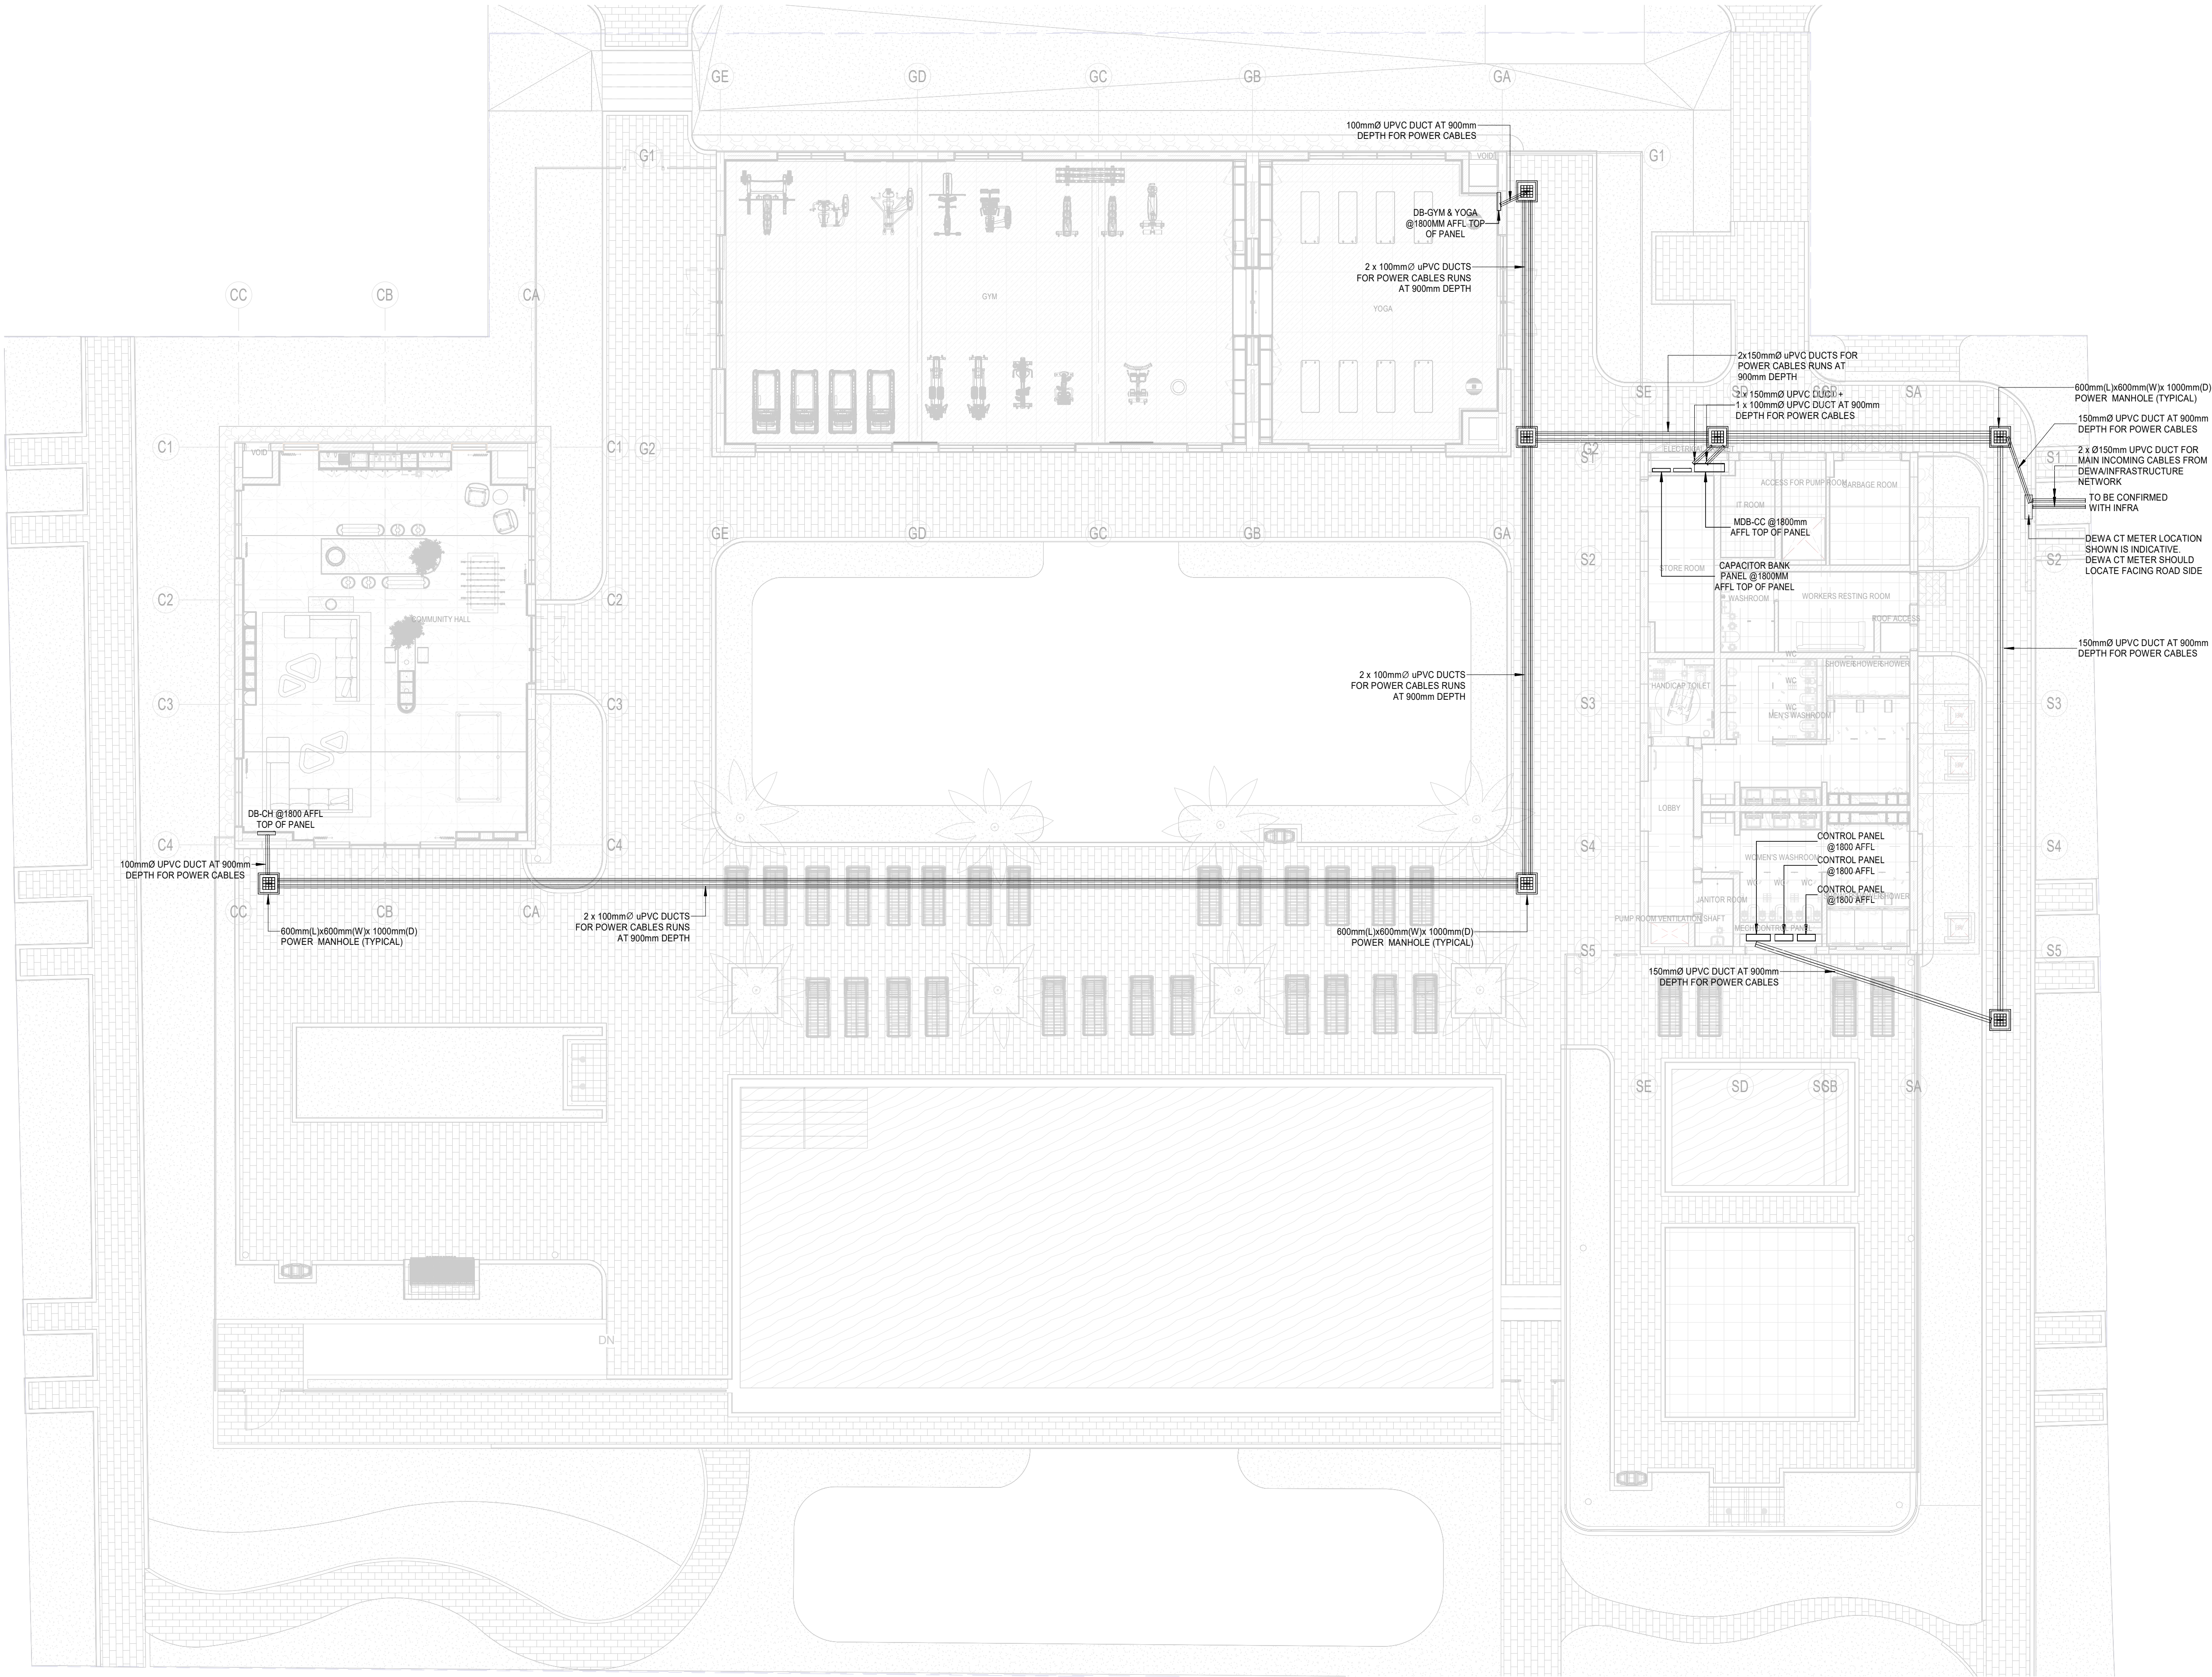

1 COMMUNITY CENTRE POWER SETTING OUT PLAN
1 : 110



- General Notes :**
- Do not Scale The Drawings. Follow (The MM) Written Dimensions Unless Otherwise Mentioned.
 - Each Drawing Shall be Read in Conjunction With all Other Drawings, Specification & the General Standard Details. In Case of Any Discrepancies Bring it to the Knowledge of Engineer and Same to be Resolved Prior to Execution of Work.
 - Dimensions Shown on These Drawings are Structural Dimensions Unless Noted Otherwise.
 - All Levels Indicated On These Drawings are Levels as per the the Survey Datum, Same Should be Verified at Site Prior to Execution of Work.
 - All Levels Indicated On These Drawings are Based On Design Level, Which is Equivalent to Datum Level and Same Should be Verified at Site Prior to Execution of Work.



No.	Date	Initials	Description
00	10/03/2026	VPA	TENDER SUBMISSION

REVISIONS / ISSUE	
THIS DRAWING MUST NOT BE REPRODUCED IN WHOLE OR IN PART WITHOUT THE PRIOR APPROVAL OF ARIF & BINTOAK	
Status	TENDER SUBMISSION

Client
EMAAR

Lead Consultant
Arif & Bint oak
اريف وبن طوق
consulting architects & engineers
PLOT NO. 2001, NEW INTERNATIONAL TOWER, 14th FLOOR, P.O. BOX 127950, DUBAI, U.A.E.
POST BOX 12081, ABU DHABI, U.A.E. TEL: 02-824668 FAX: 02-824668 arif@arifbintoak.com.ae

Project Title:
**COMMUNITY CENTER -TH01
GRANDPOLP CLUB & RESORT, UAE**

Discipline : **ELECTRICAL**

Drawing title:
**COMMUNITY CENTRE POWER
SETTING OUT PLAN**

Architectural Engineer	Electrical Engineer	Structural Engineer
MUSTAFA ABID	MARWAN MOHD.	RIHAM RAMADAN
Registration # 5847	Registration # 80102	Registration # 105092
Scale(s): 1 : 110	Date drawn: 10/03/2026	Project no: 1857
Drawn by: VPA	Checked: HAE	Approved: MRM

Drawing Number : GPCR-TH01-AB-DRG-GFL-ELE-EP-3017-00