



This 2D drawing is extracted from 3D BIM Model

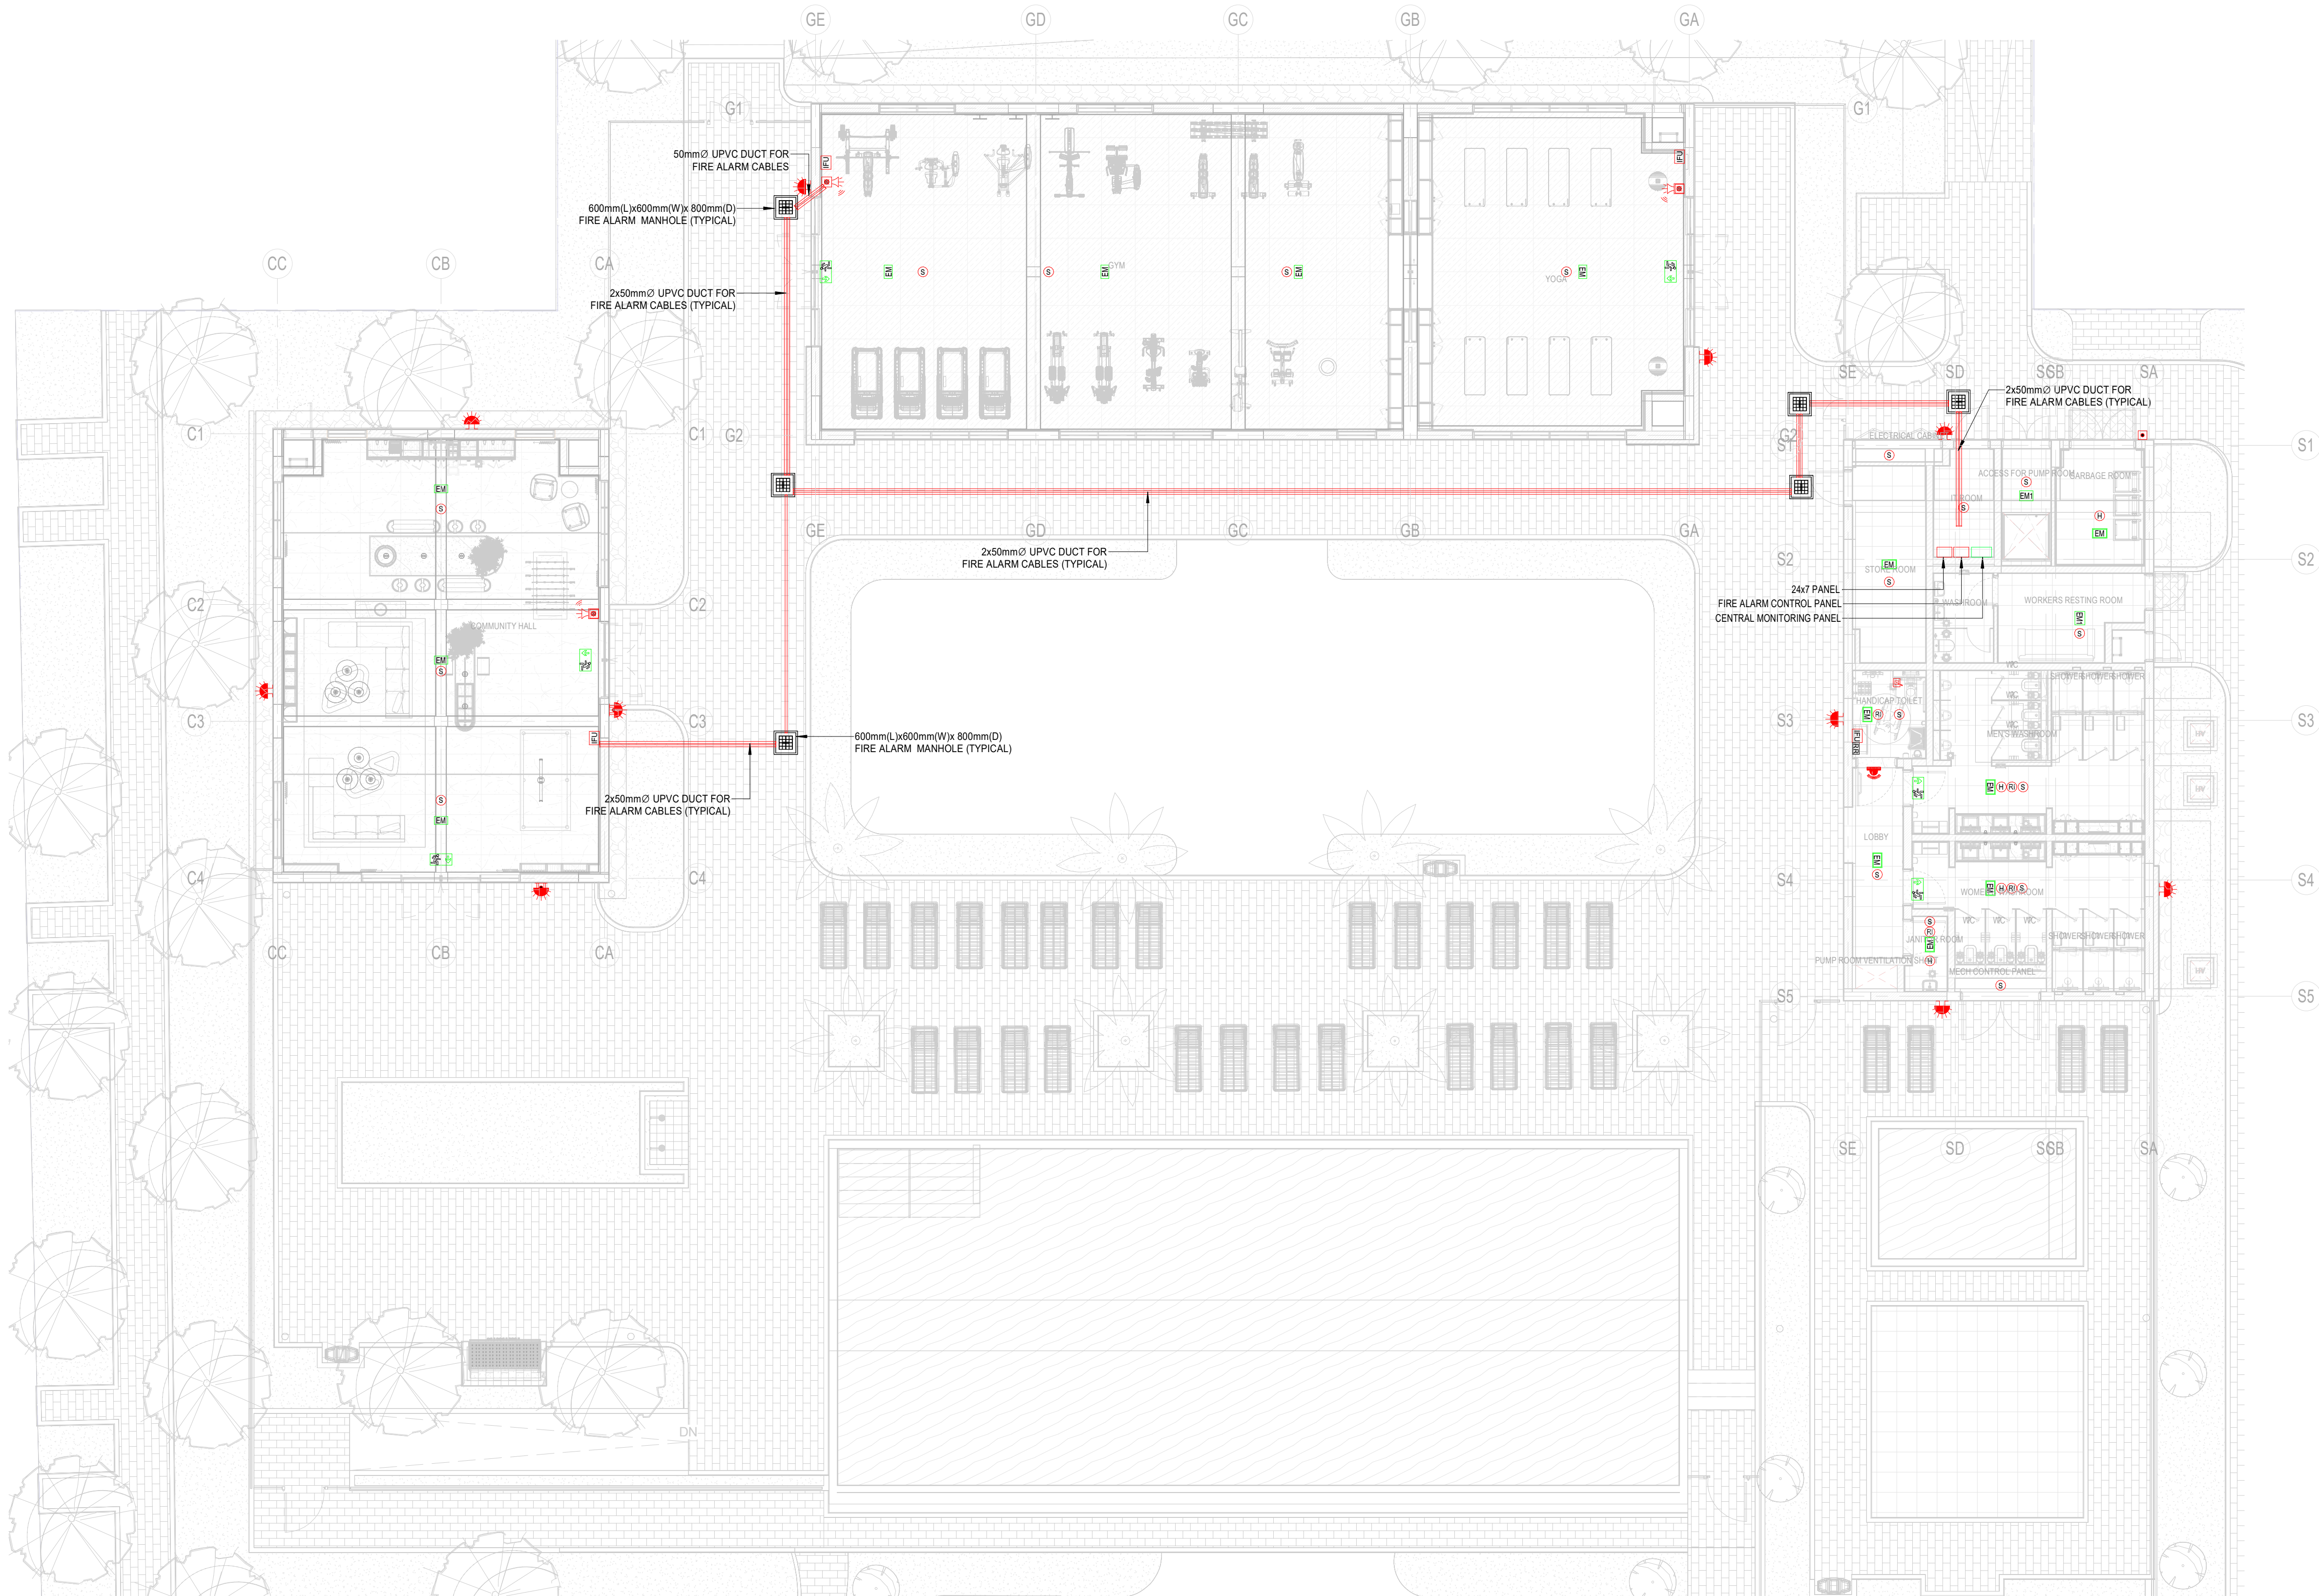

1 GROUND FLOOR FIRE ALARM OVERALL PLAN
1 : 110



- General Notes :**
01. Do not Scale The Drawings. Follow (The MM) Written Dimensions Unless Otherwise Mentioned.
 02. Each Drawing Shall be Read in Conjunction With all Other Drawings, Specification & the General Standard Details. In Case of Any Discrepancies Bring it to the Knowledge of Engineer and Same to be Resolved Prior to Execution of Work.
 03. Dimensions Shown on These Drawings are Structural Dimensions Unless Noted Otherwise.
 04. All Levels Indicated On These Drawings are Levels as per the Survey Datum, Same Should be Verified at Site Prior to Execution of Work.
 05. All Levels Indicated On These Drawings are Based On Design Level, Which is Equivalent to Datum Level and Same Should be Verified at Site Prior to Execution of Work.

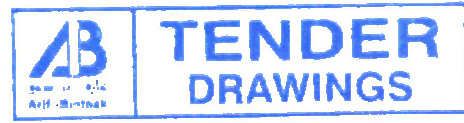

No.	Date	Initials	Description
00	10/03/2026	VPA	TENDER SUBMISSION

REVISIONS / ISSUE

THIS DRAWING MUST NOT BE REPRODUCED IN WHOLE OR IN PART WITHOUT THE PRIOR APPROVAL OF ARIF & BINTOAK

Status: TENDER SUBMISSION

Client: EMAAR

Lead Consultant: Arif & BintOak

Project Title: COMMUNITY CENTRE - TH01

Grandpulp Club & Resort, UAE

Discipline: ELECTRICAL

Drawing title: COMMUNITY CENTRE FIRE ALARM SETTING OUT PLAN

Architectural Engineer: MUSTAFA ABID

Electrical Engineer: MARWAN MOHD.

Structural Engineer: RIHAM RAMADAN

Registration # 5847

Registration # 80102

Registration # 105092

Scale(s): 1 : 110

Date drawn: 10/03/2026

Project no: 1857

Drawn by: VPA

Checked: HAE

Approved: MRM

Drawing Number: GPCR-TH01-AB-DRG-GFL-ELE-FA-3019-00