



This 2D drawing is extracted from 3D BIM Model

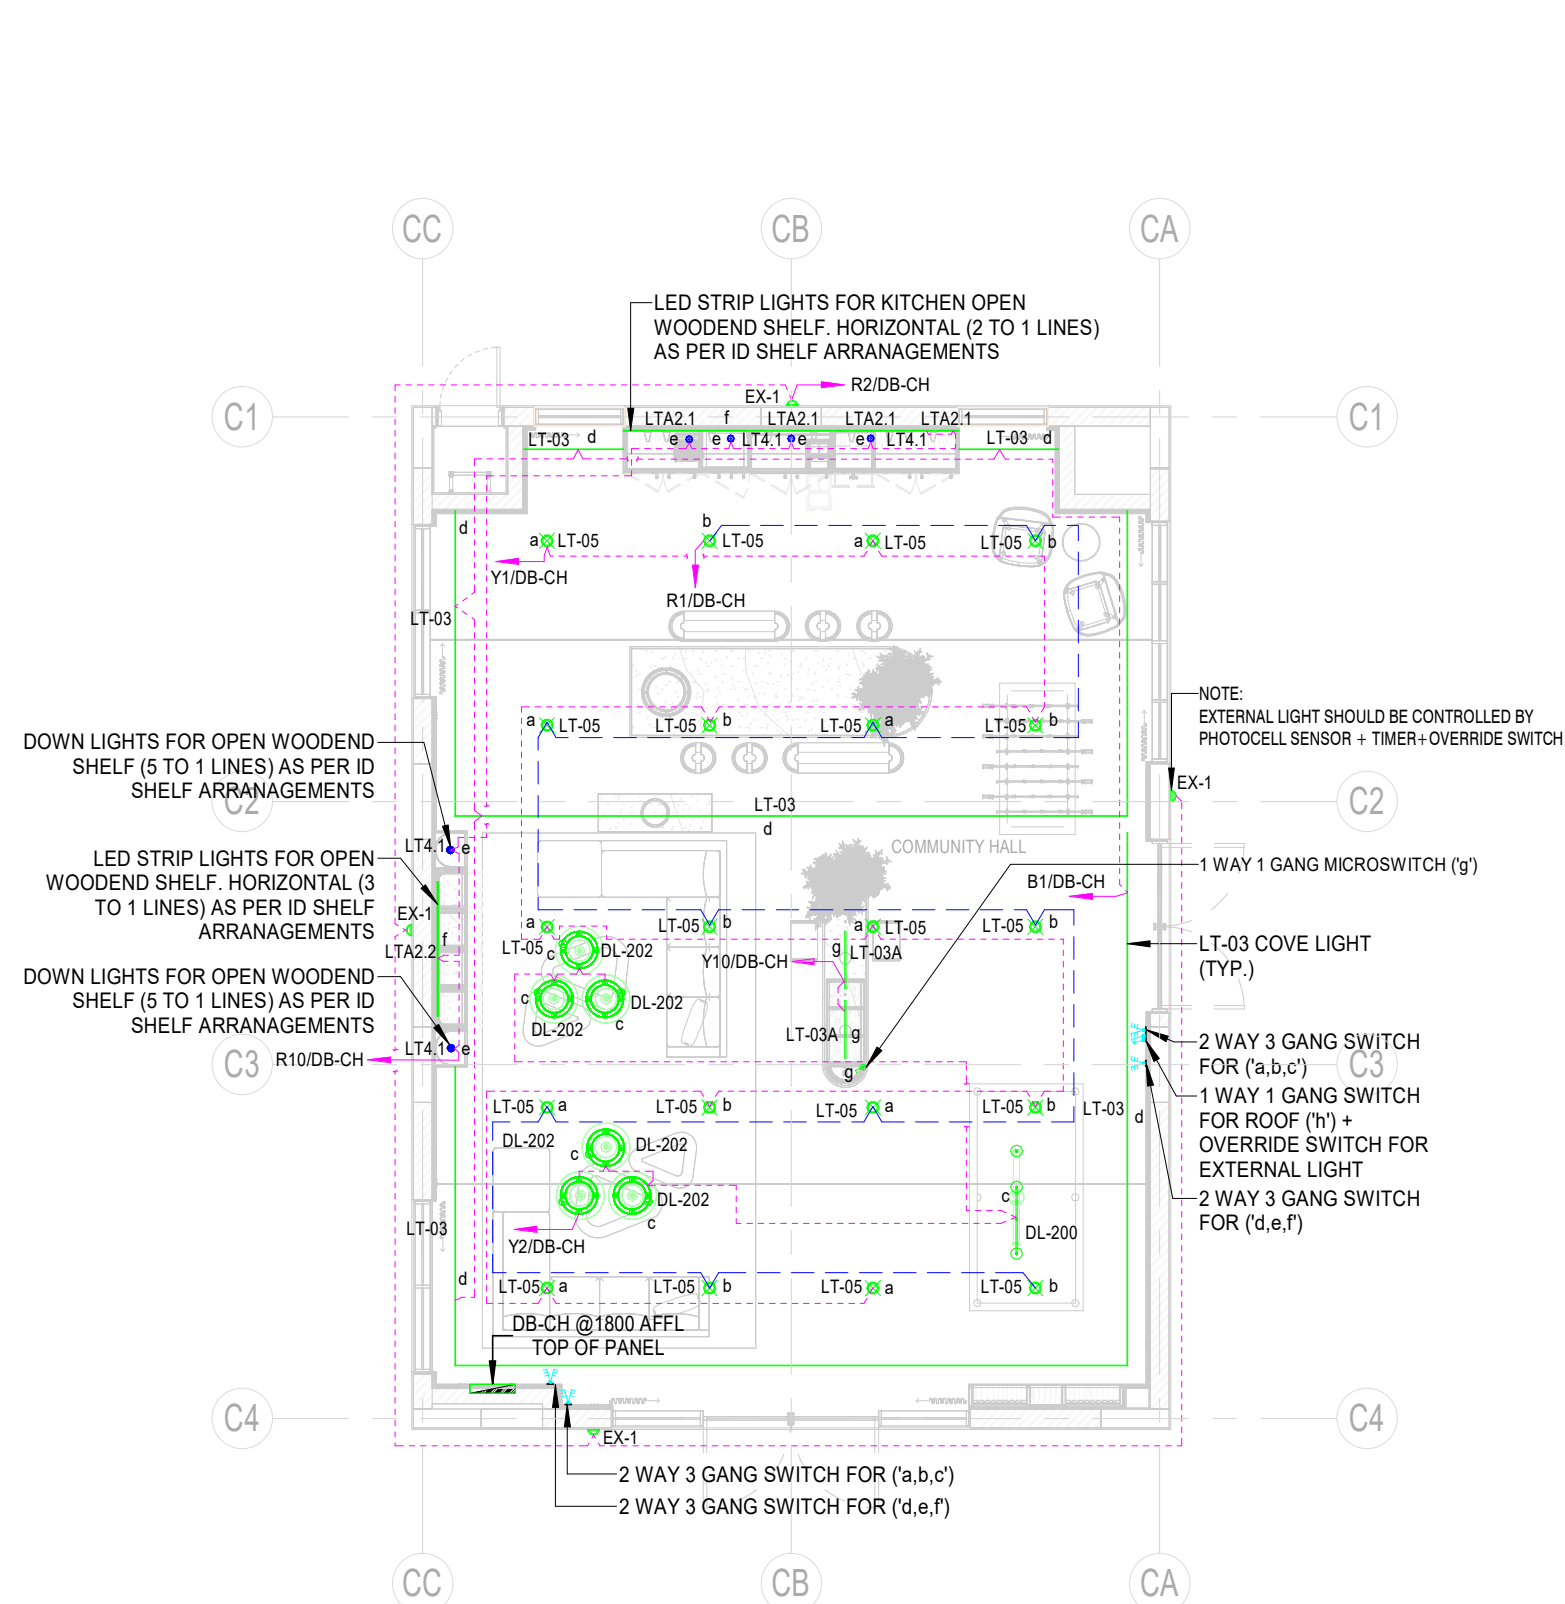

1 01-GROUND FLOOR COMMUNITY HALL LIGHTING
1 : 100

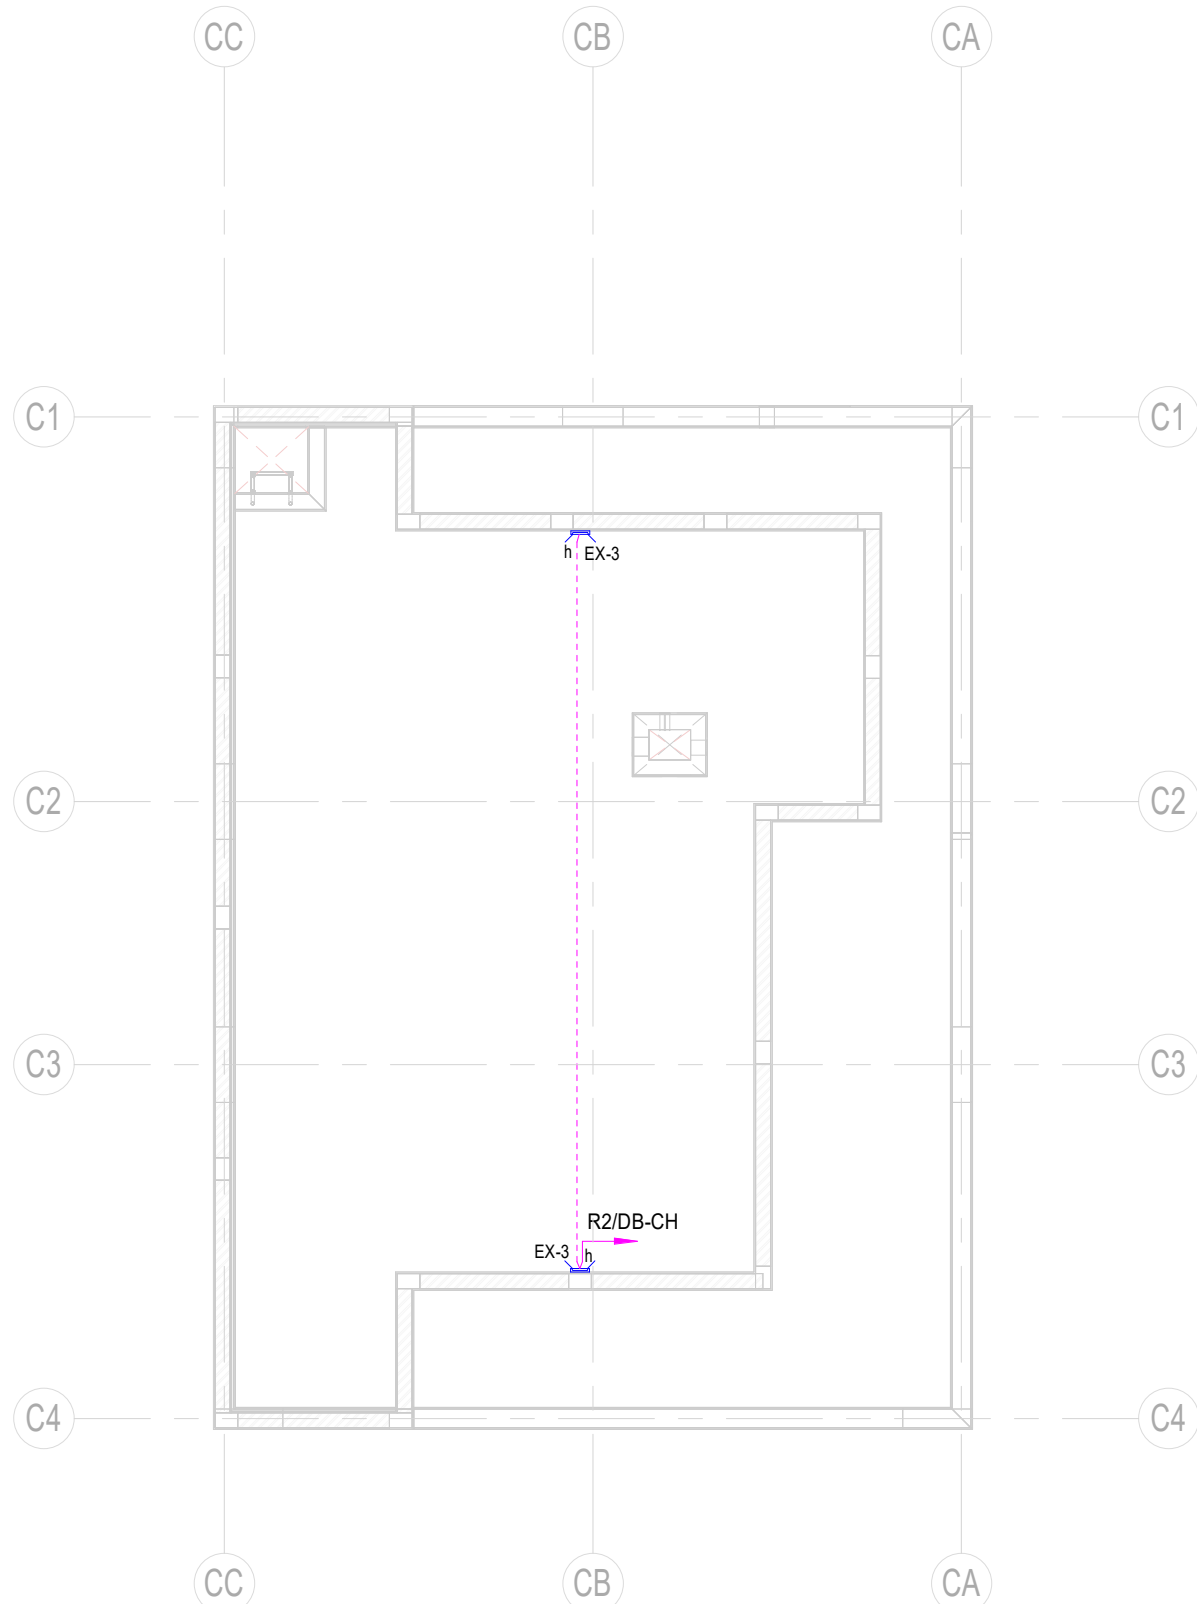

2 02-ROOF COMMUNITY HALL LIGHTING
1 : 100

LIGHTING LEGENDS

SYMBOL	DESCRIPTION
LT-03	10W LED STRIP LINEAR LIGHT
LT-03	10W LED STRIP LINEAR LIGHT
LT-03	15W LED DECORATIVE TUBE LIGHT
LT-03A	10W LED DECORATIVE TUBE LIGHT
LT-05	15W LED SURFACE MOUNTED LIGHT
DL-202	DECORATIVE PENDANT LIGHT
EX-3	15W LED, WALL MOUNTED LIGHT DIE CAST ALUMINIUM
DL-200	DECORATIVE PENDANT LIGHT
EX-1	15W LED, WALL MOUNTED EXTERNAL DECORATIVE LIGHTS 3000°K (7W)
LT-05	15W LED, 1500mm, 3000°K, IP44 WALL MOUNTED LIGHT FIXTURE
	13Amp - 2 WAY 3 GANG LIGHTING SWITCH.
	13Amp - 1 WAY 1 GANG SWITCH + OVERRIDE SWITCH
	13Amp - 1 WAY 1 GANG LIGHTING MICROSWITCH.
DB-X-X	ELECTRICAL FINAL DISTRIBUTION BOARD (DB) 'X' INDICATING FLOOR REF. 'Y' INDICATING FLAT REF.

NOTE:
EXTERNAL LIGHT SHOULD BE CONTROLLED BY PHOTOCELL SENSOR + TIMER+ OVERRIDE SWITCH

Key Plan

General Notes :
01. Do not Scale The Drawings. Follow (The MM) Written Dimensions Unless Otherwise Mentioned.
02. Each Drawing Shall be Read in Conjunction With all Other Drawings, Specification & the General Standard Details. In Case of Any Discrepancies Bring it to the Knowledge of Engineer and Same to be Resolved Prior to Execution of Work.
03. Dimensions Shown on These Drawings are Structural Dimensions Unless Noted Otherwise.
04. All Levels Indicated On These Drawings are Levels as per the Survey Datum, Same Should be Verified at Site Prior to Execution of Work.
05. All Levels Indicated On These Drawings are Based On Design Level, Which is Equivalent to Datum Level and Same Should be Verified at Site Prior to Execution of Work.

TENDER DRAWINGS

00	10/03/2026	VPA	TENDER SUBMISSION
No.	Date	Initials	Description
REVISIONS / ISSUE			
THIS DRAWING MUST NOT BE REPRODUCED IN WHOLE OR IN PART WITHOUT THE PRIOR APPROVAL OF ARIF & BINTOAK			
Status	TENDER SUBMISSION		
Client	EMAAR		
Lead Consultant	المستشارين: عارف وبن طوق Arif & Bint oak consulting architects & engineers P.O. BOX 20161 RAS AL KHAYMA, U.A.E. TEL: 03-5222888 FAX: 03-5222832 POST BOX 42061 ABU DHABI, U.A.E. TEL: 02-624668 - contact@arifbintoak.com.ae		
Project Title:	COMMUNITY CENTER - TH01 GRANDPOLP CLUB & RESORT, UAE		
Discipline :	ELECTRICAL		
Drawing title:	COMMUNITY CENTRE GROUND & ROOF FLOOR PLAN LIGHTING LAYOUT		
Architectural Engineer	Electrical Engineer	Structural Engineer	
MUSTAFA ABID	MARWAN MOHD.	RIHAM RAMADAN	
Registration # 5847	Registration # 80102	Registration # 105092	
Scale(s): 1 : 100	Date drawn: 10/03/2026	Project no: 1857	
Drawn by: VPA	Checked: HAE	Approved: MRM	
Drawing Number :		GPCR-TH01-AB-DRG-ZZZ-ELE-EL-3000-00	

© AB 1 A1 Title Block - BIM Standard Ver. 2.0

04/03/2026 1:50:14 PM