




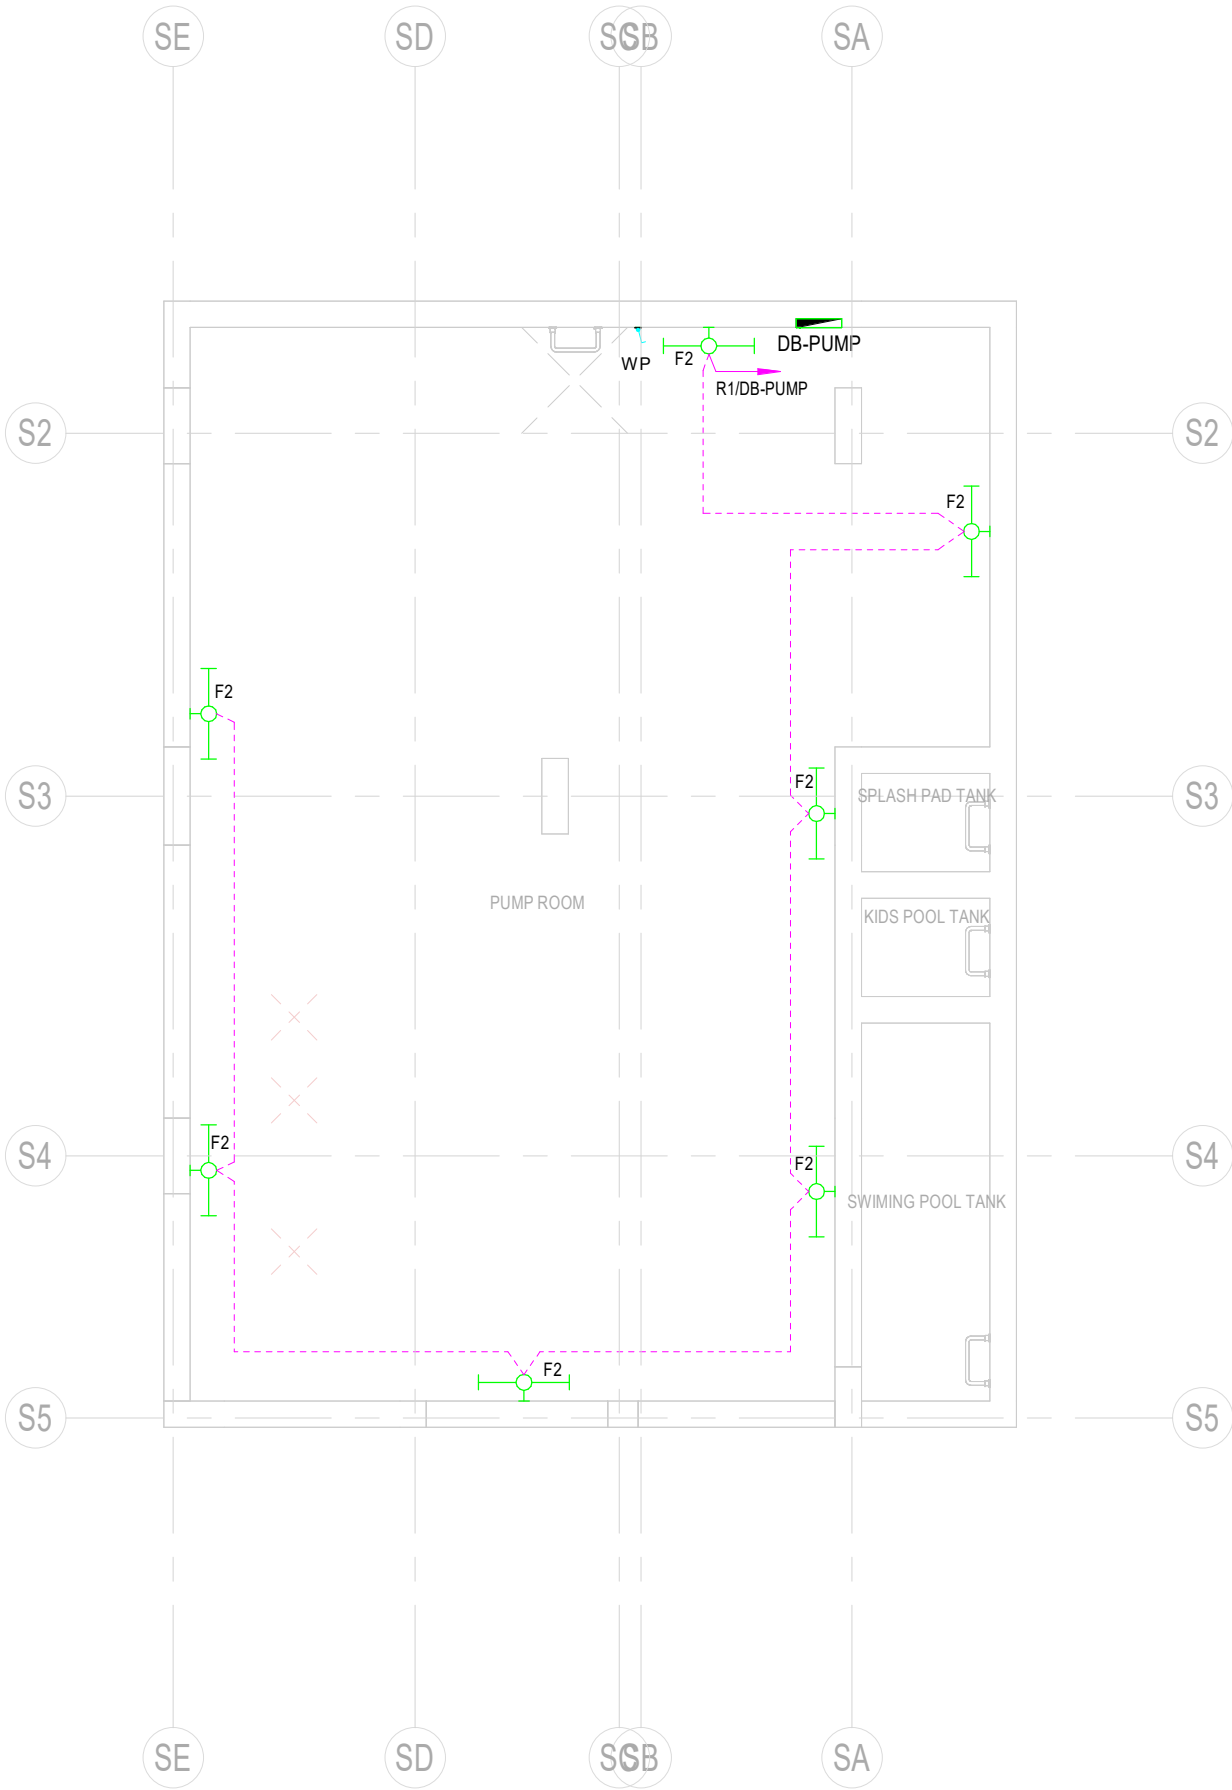

1 00-U.W.T SERVICE BLOCK LIGHTING
1 : 100

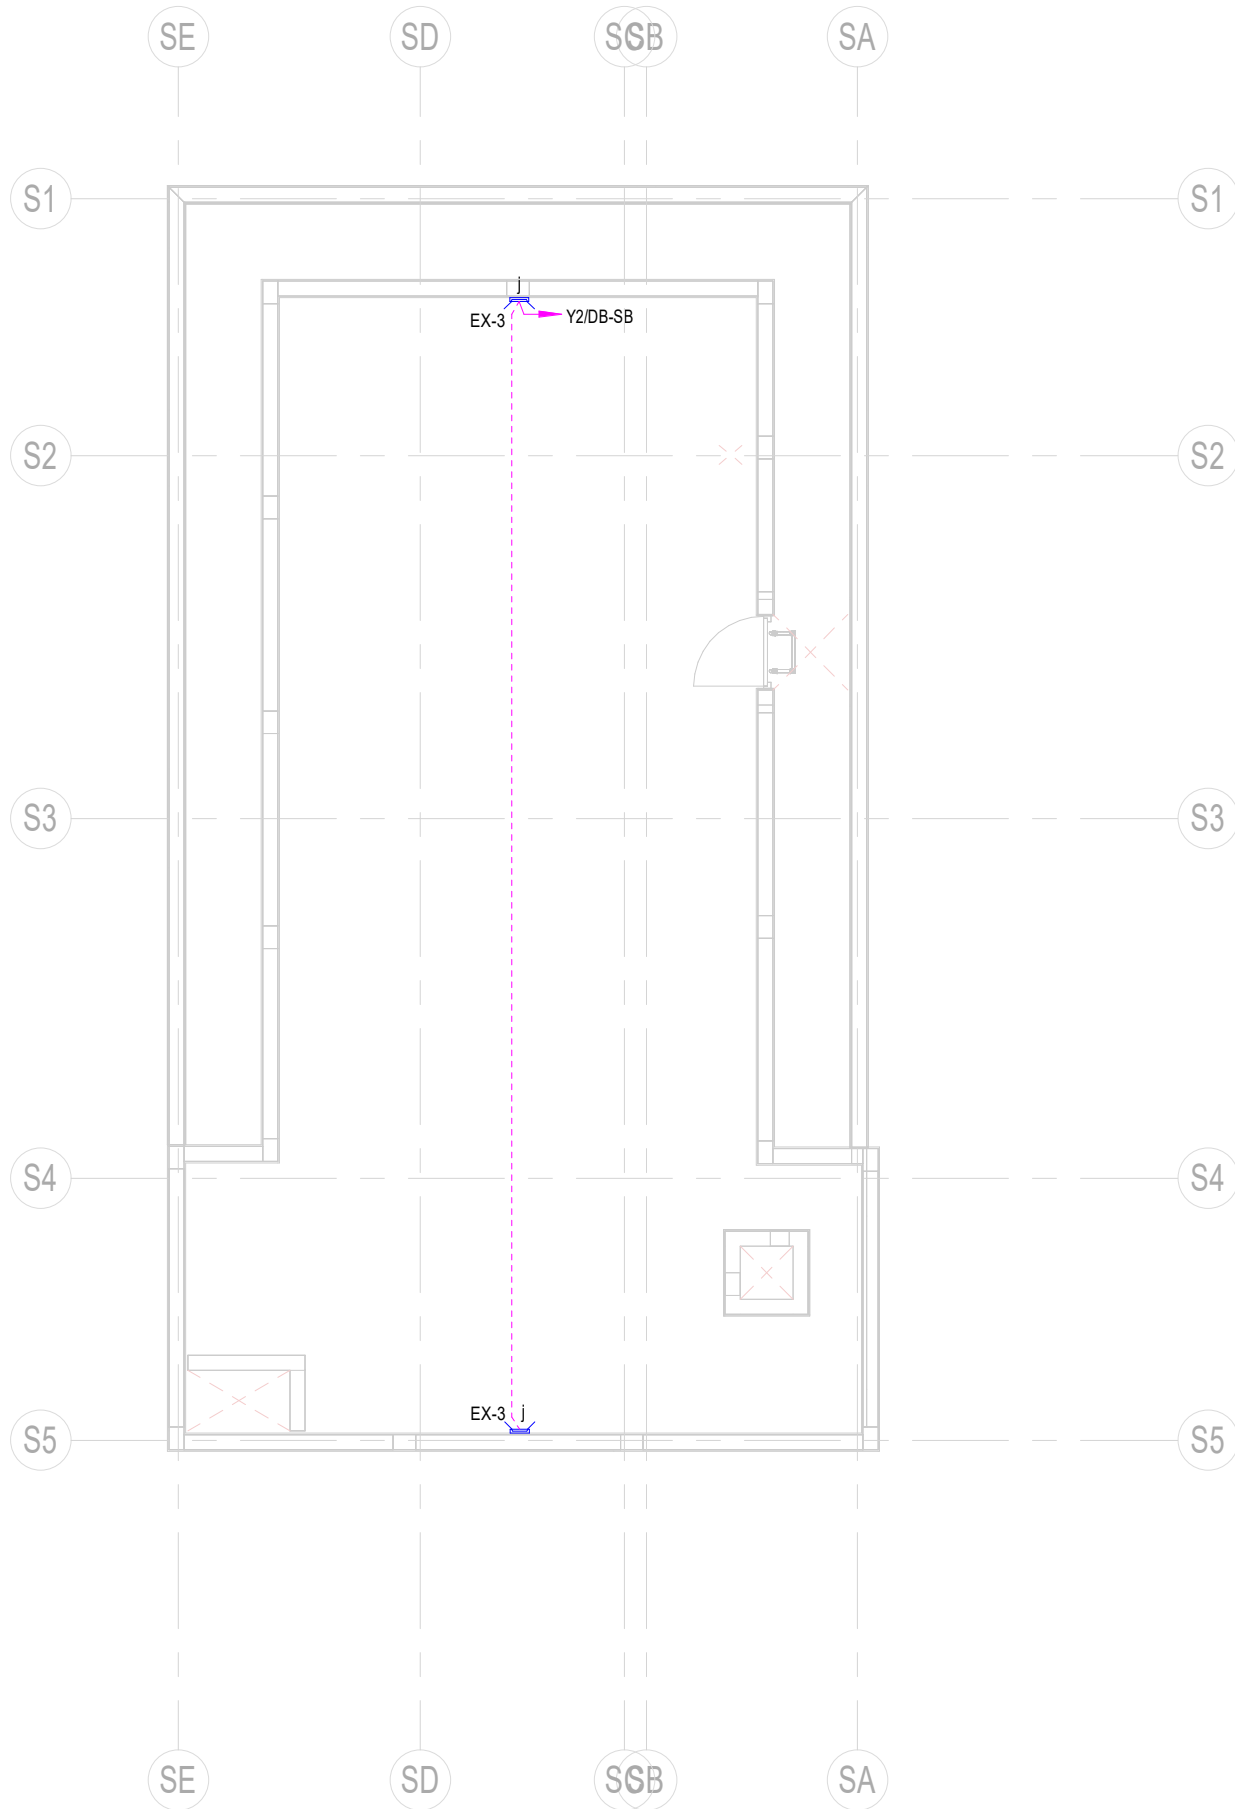

3 02-ROOF SERVICE BLOCK LIGHTING
1 : 100

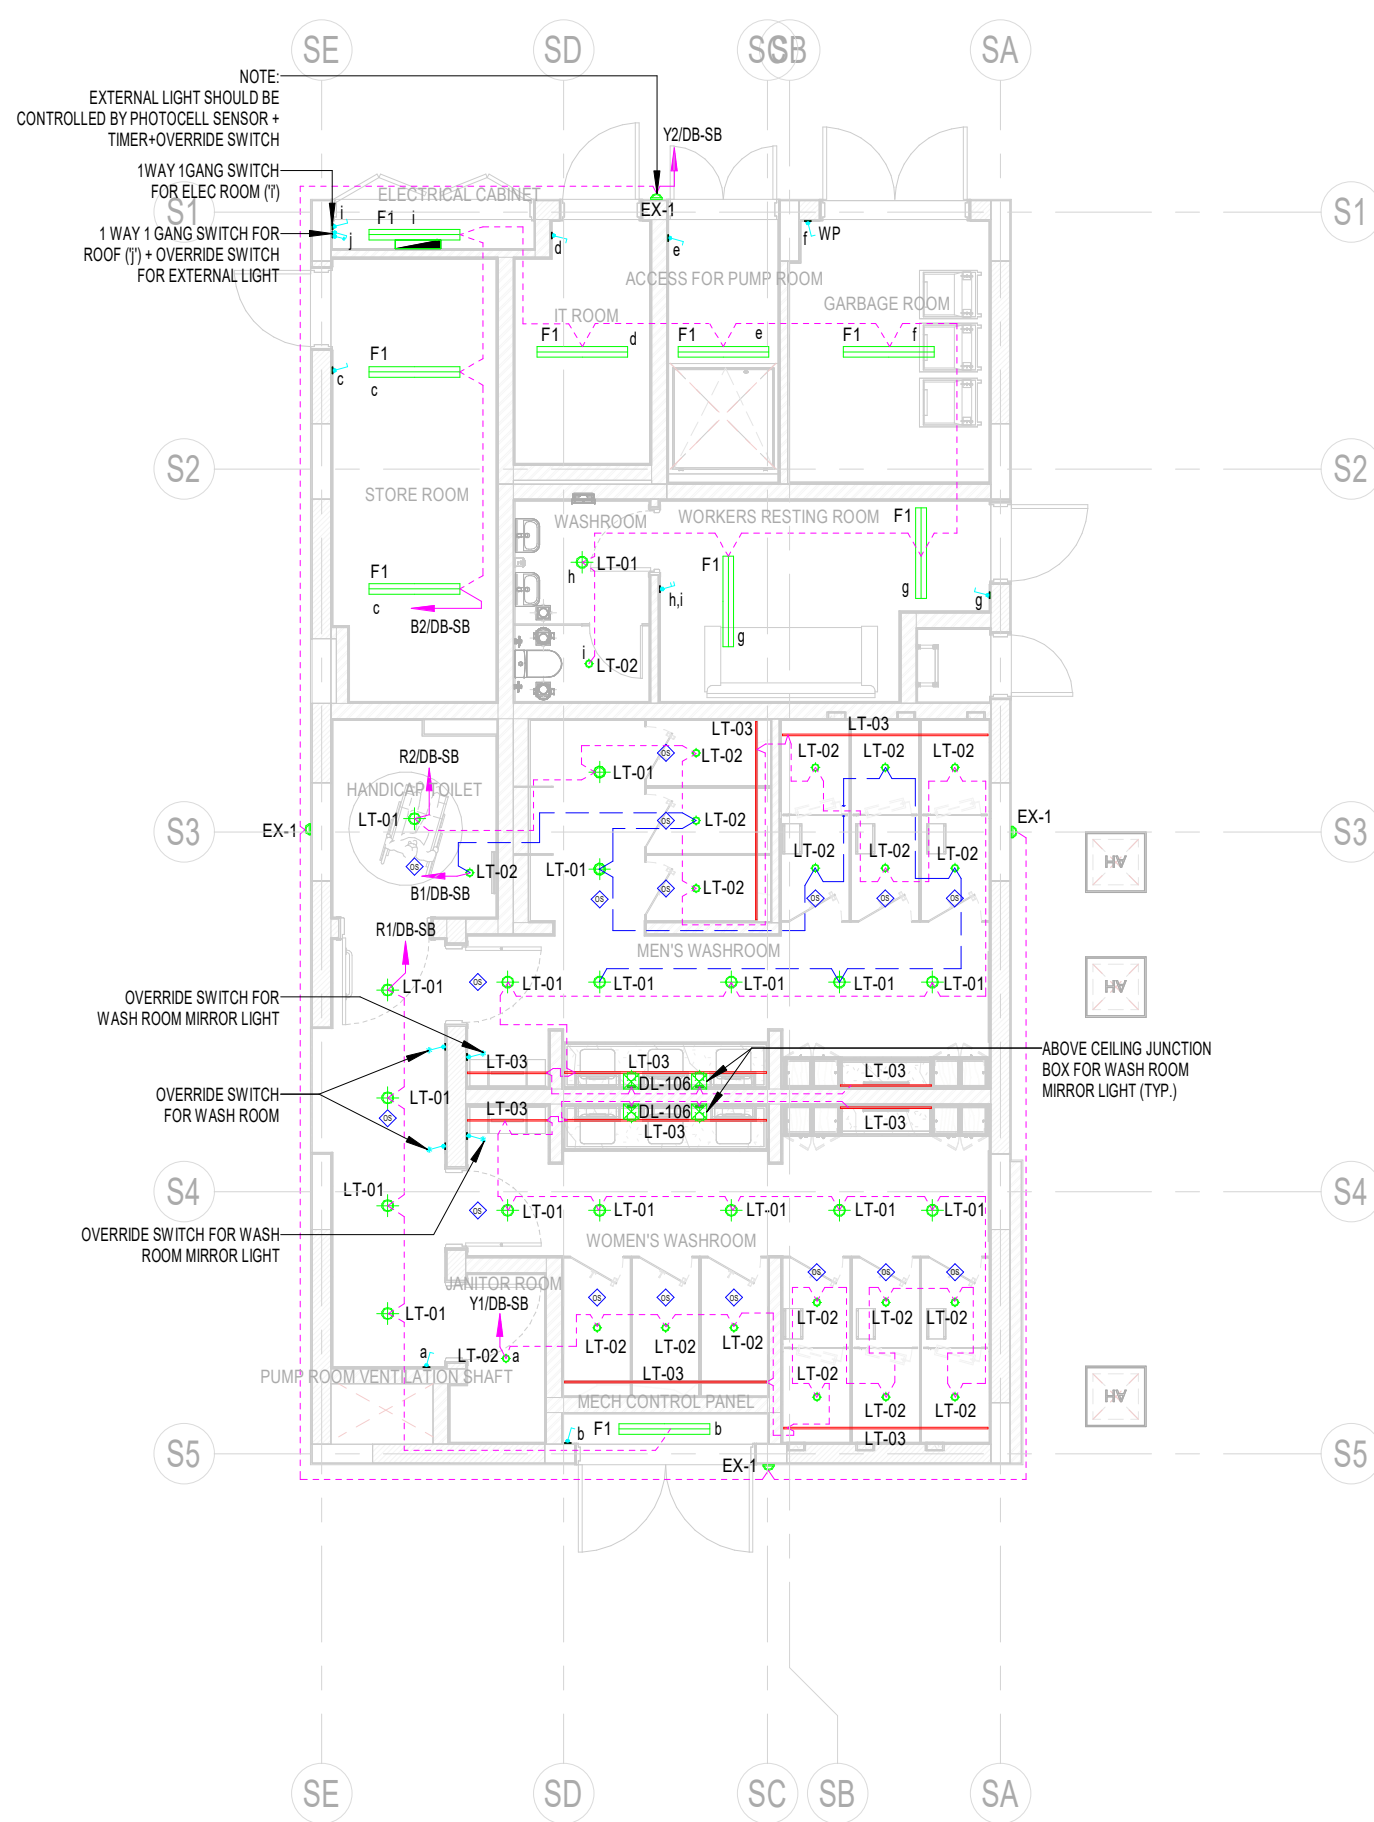

2 01-GROUND FLOOR SERVICE BLOCK LIGHTING
1 : 100

LIGHTING LEGENDS	
SYMBOL	DESCRIPTION
EX-1	15W LED, WALL MOUNTED EXTERNAL DECORATIVE LIGHTS 3000°K (7W)
F2	25W WEATHER-PROOF LED SURFACE (WALL) MOUNTED LUMINAIRE, IP66
LT-01	10W LED RECESSED DOWNLIGHT, IP65
LT-02	10W LED RECESSED DOWNLIGHT, IP65
DL-100	15W LED SCANDAL MINI WALL MOUNTED LIGHT, IP65
F1	36W LED LIGHT FIXTURE, 4450 LUMENS, IP-54
OS	OCCUPANCY / PRESENCE SENSOR (HIGH COVERAGE AREA)
EX-3	15W LED, WALL MOUNTED LIGHT DIE CAST ALUMINUM
LT-03	10W LED STRIP LINEAR LIGHT
	13Amp - 1 WAY 1 GANG LIGHTING SWITCH
	13Amp - 1 WAY 2 GANG LIGHTING SWITCH
	13Amp - 1 WAY 1 GANG SWITCH + OVERRIDE SWITCH
	ELECTRICAL FINAL DISTRIBUTION BOARD (DB) V INDICATING FLOOR REF, Y INDICATING FLAT REF.

NOTE:
EXTERNAL LIGHT SHOULD BE CONTROLLED BY PHOTOCELL SENSOR + TIMER+OVERRIDE SWITCH



- General Notes :**
- Do not Scale The Drawings. Follow (The MM) Written Dimensions Unless Otherwise Mentioned.
 - Each Drawing Shall be Read in Conjunction With all Other Drawings, Specification & the General Standard Details. In Case of Any Discrepancies Bring it to the Knowledge of Engineer and Same to be Resolved Prior to Execution of Work.
 - Dimensions Shown on These Drawings are Structural Dimensions Unless Noted Otherwise.
 - All Levels Indicated On These Drawings are Levels as per the Survey Datum, Same Should be Verified at Site Prior to Execution of Work.
 - All Levels Indicated On These Drawings are Based On Design Level, Which is Equivalent to Datum Level and Same Should be Verified at Site Prior to Execution of Work.



00	10/03/2026	VPA	TENDER SUBMISSION
No.	Date	Initials	Description

REVISIONS / ISSUE

THIS DRAWING MUST NOT BE REPRODUCED IN WHOLE OR IN PART WITHOUT THE PRIOR APPROVAL OF ARIF & BINTOAK

Status
TENDER SUBMISSION

Client

EMAAR

Lead Consultant



Project Title:

COMMUNITY CENTER - TH01
GRANDPOLP CLUB & RESORT, UAE

Discipline :
ELECTRICAL

Drawing title:
SERVICE BLOCK U.W.T,
GROUND & ROOF FLOOR PLAN
LIGHTING LAYOUT

Architectural Engineer	Electrical Engineer	Structural Engineer
MUSTAFA ABID	MARWAN MOHD.	RIHAM RAMADAN
Registration # 5847	Registration # 80102	Registration # 105092

Scale(s): 1 : 100	Date drawn: 10/03/2026	Project no: 1857
----------------------	---------------------------	---------------------

Drawn by: VPA	Checked: HAE	Approved: MRM
------------------	-----------------	------------------

Drawing Number : GPCR-TH01-AB-DRG-ZZZ-ELE-EL-3001-00