




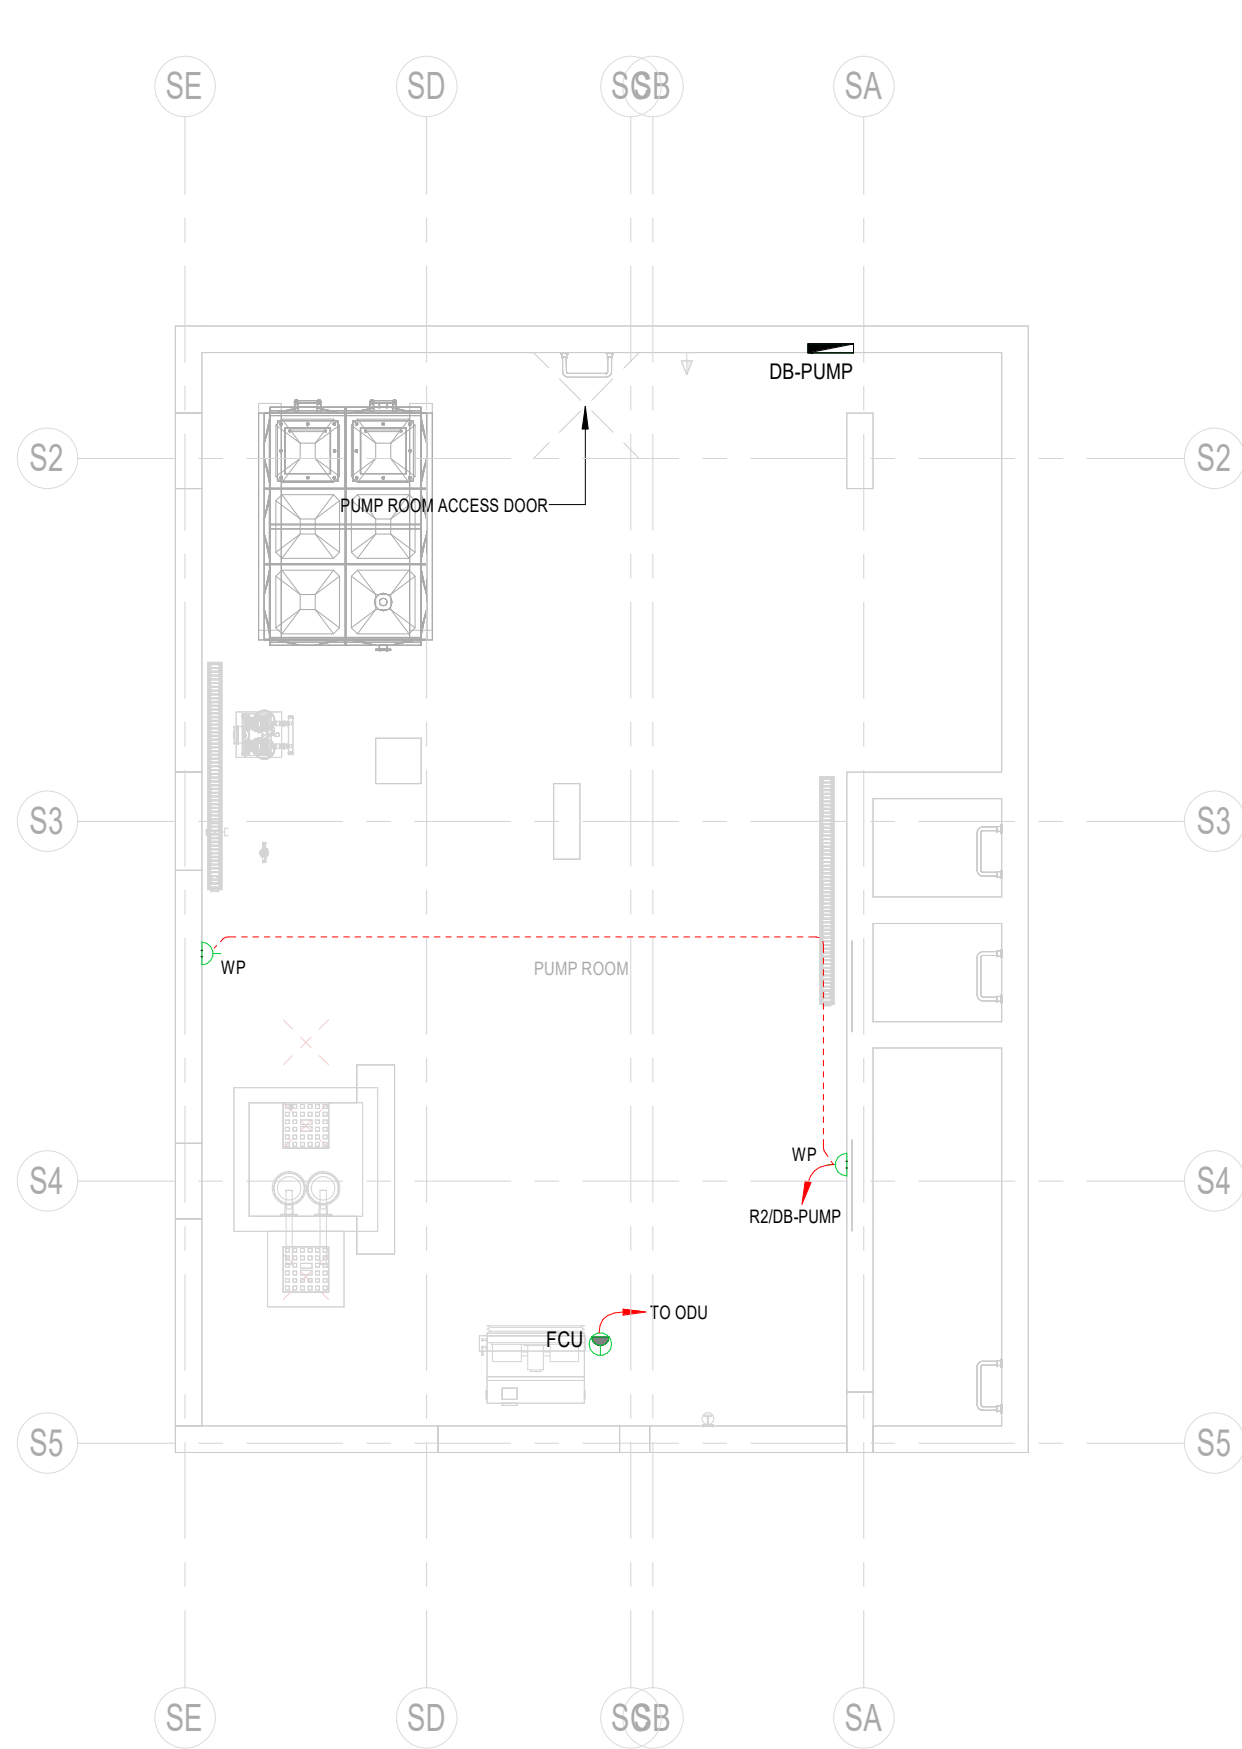


1 00-U.W.T SERVICE BLOCK POWER
1 : 100

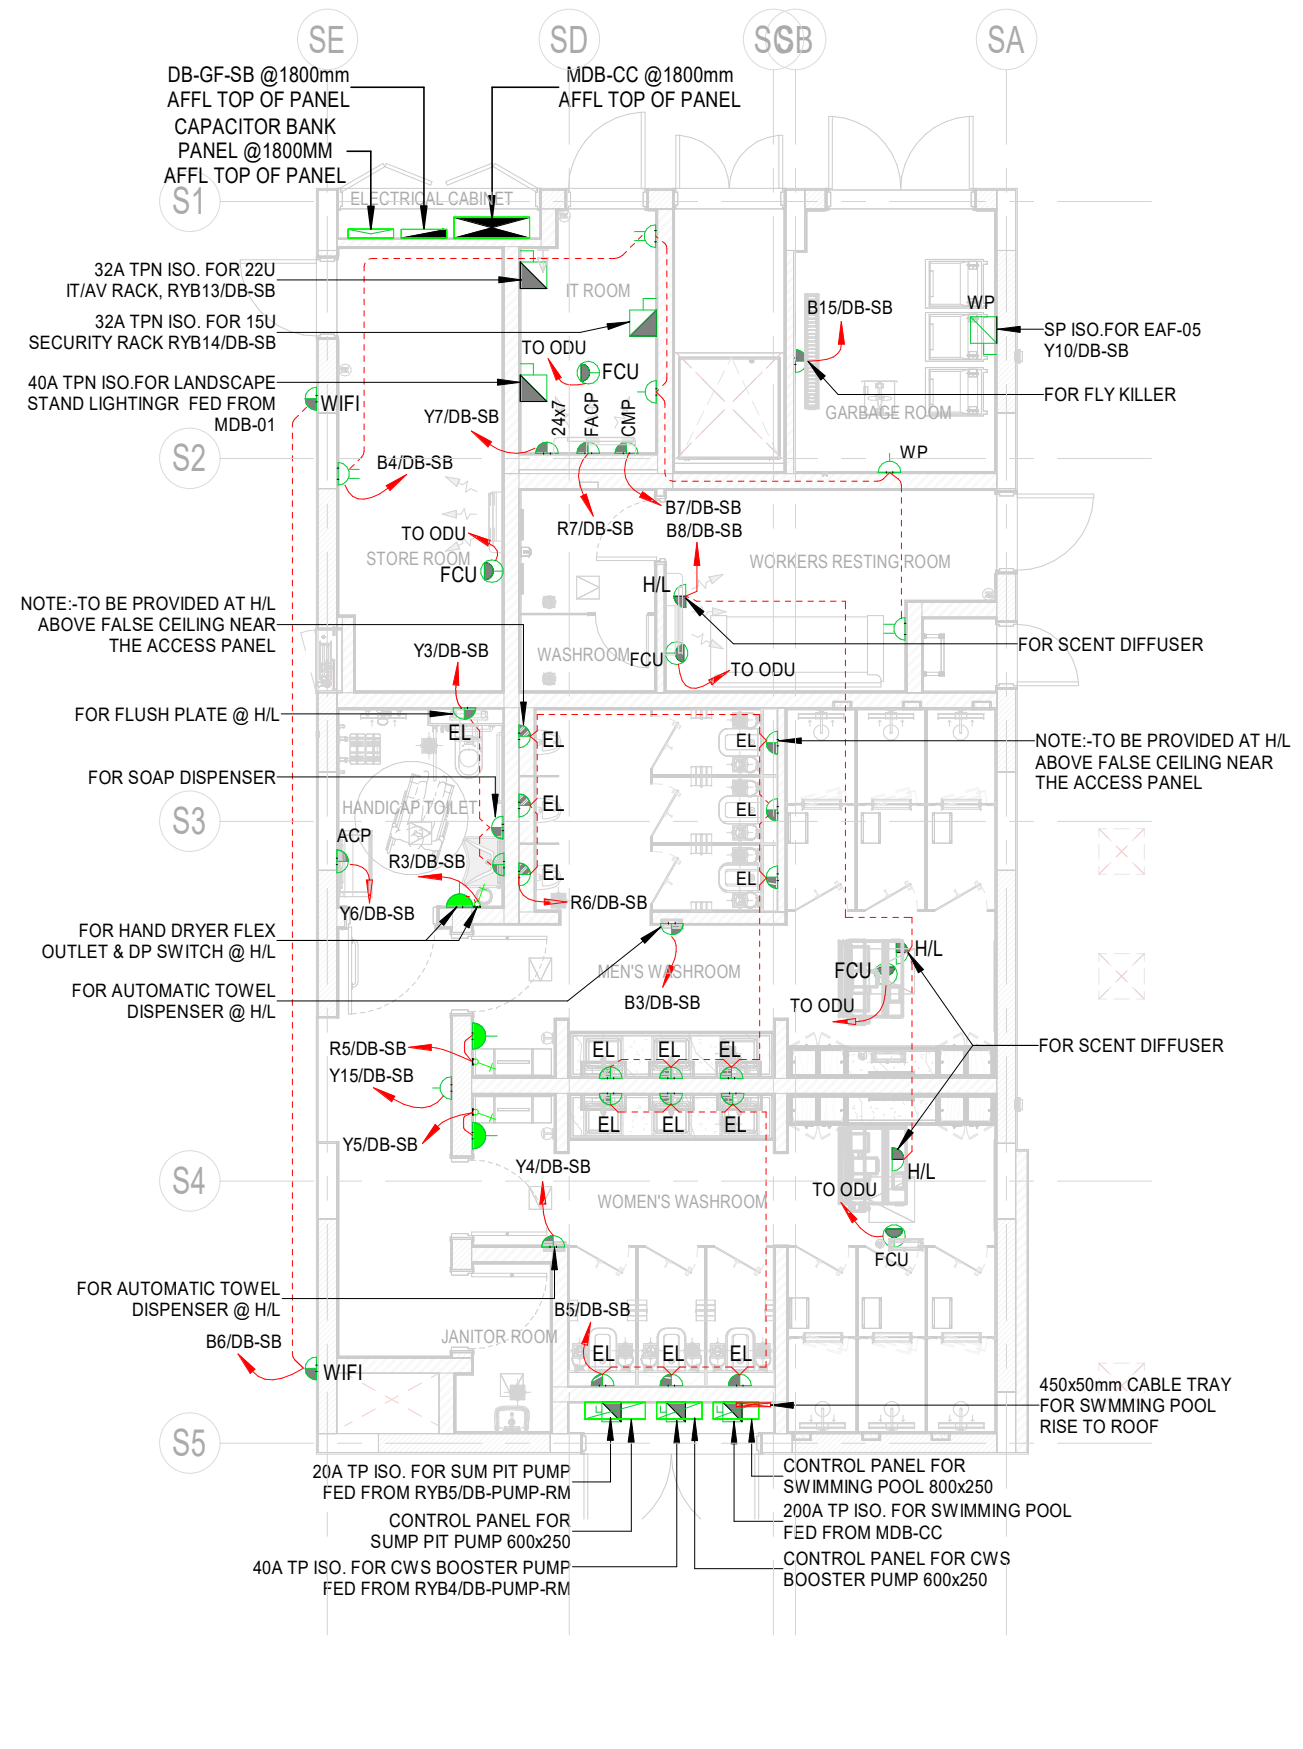


2 01-GROUND FLOOR SERVICE BLOCK POWER
1 : 100

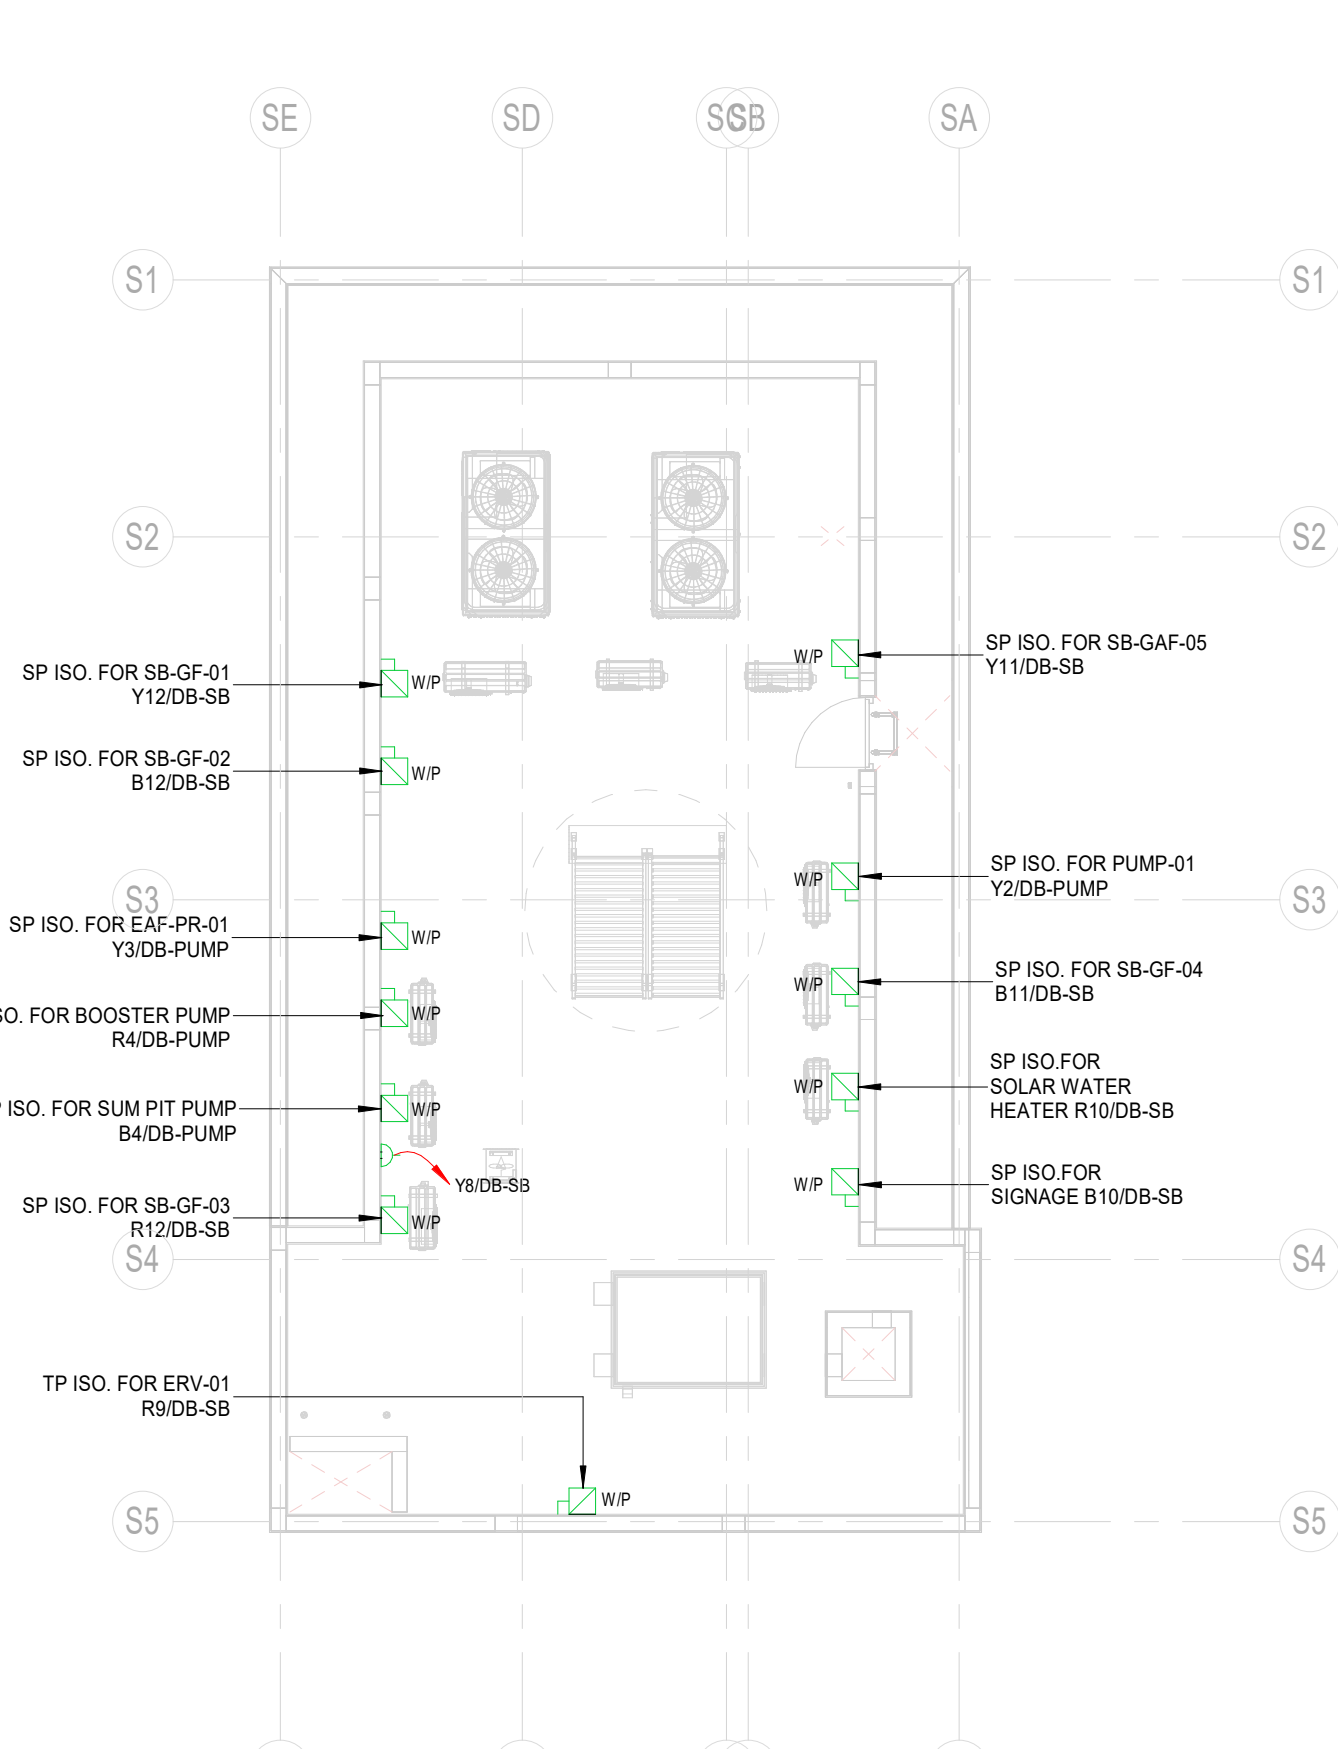


3 02-ROOF SERVICE BLOCK POWER
1 : 100

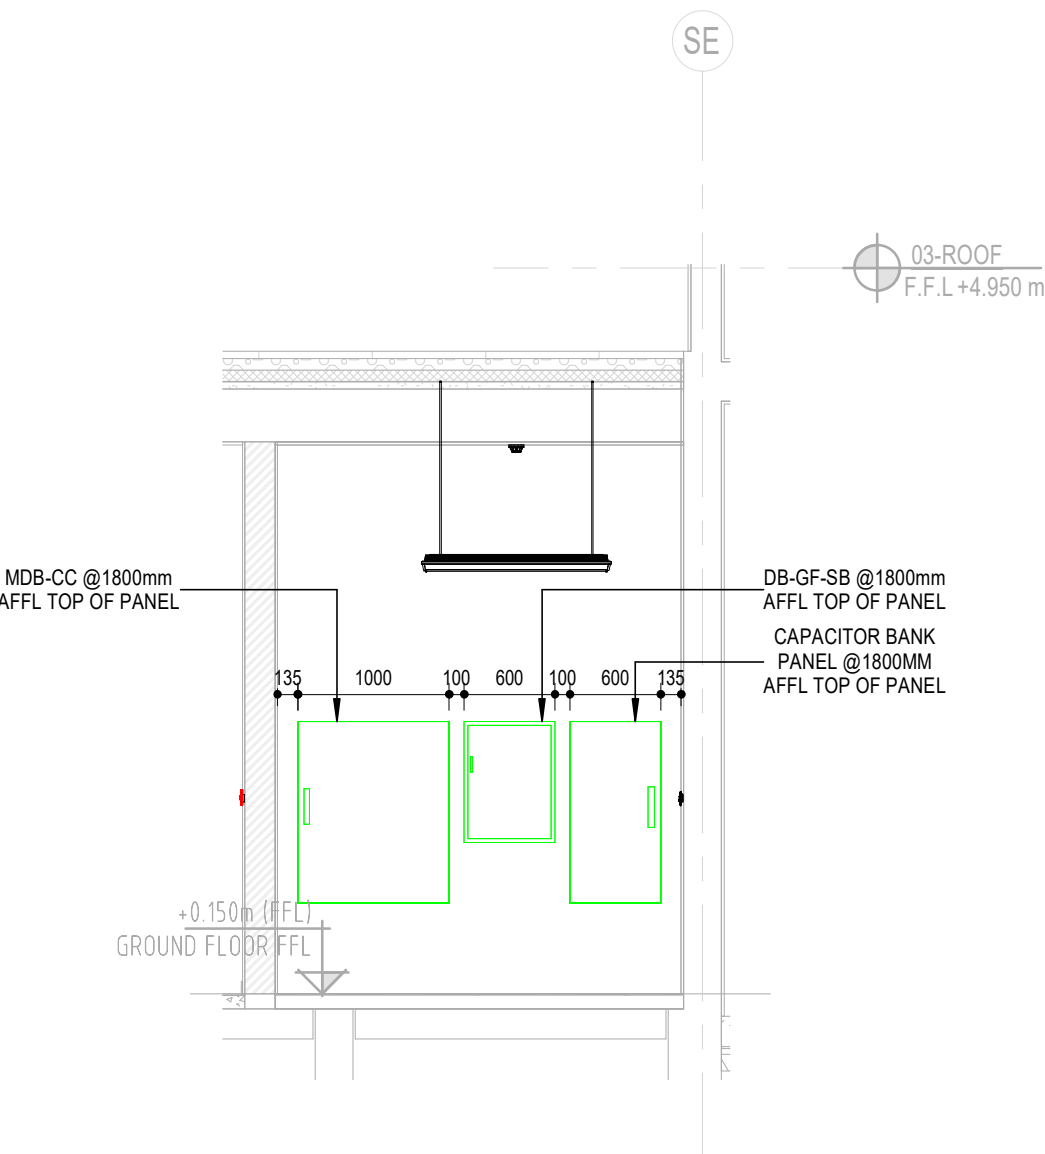


4 ELE.CABINET DETAILS SECTION
1 : 50

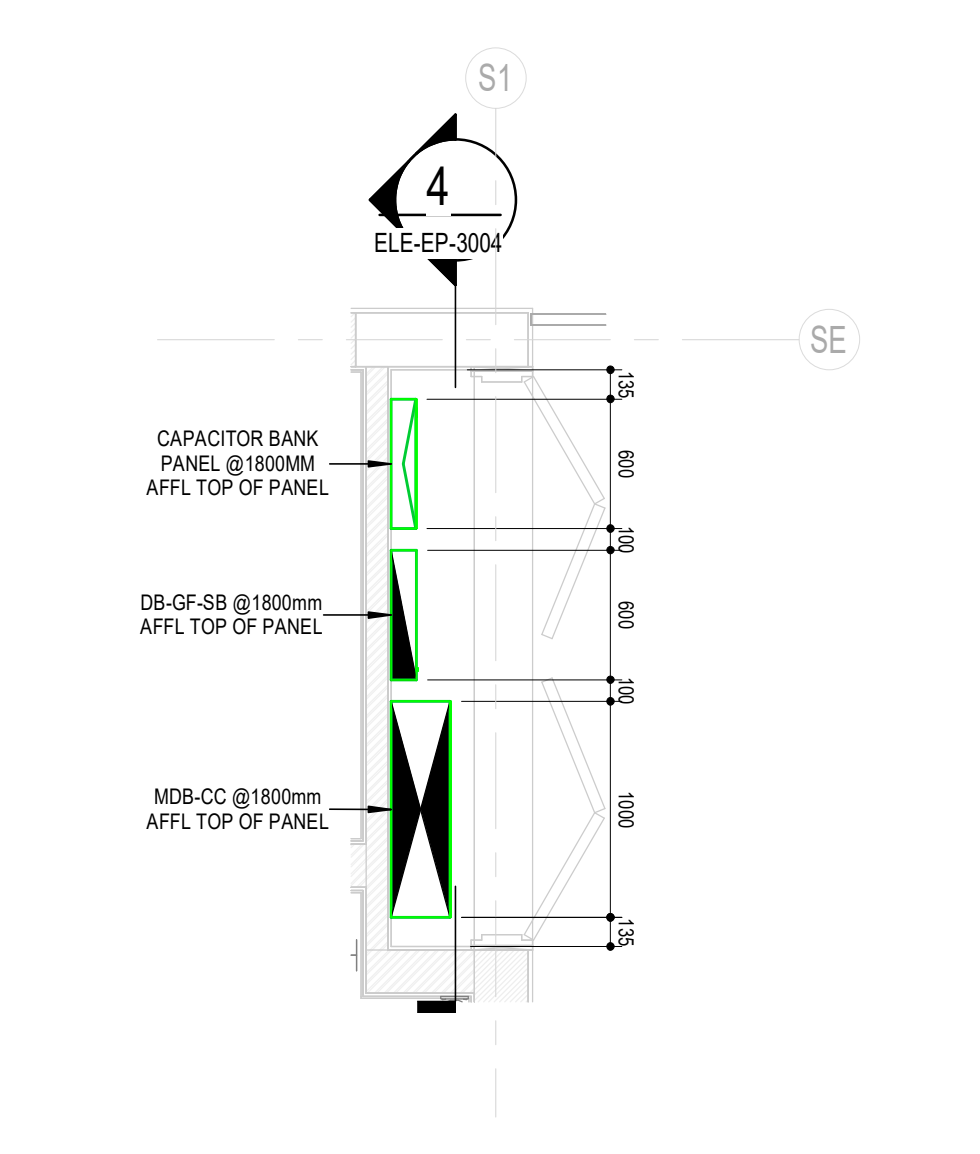

SERVICE BLOCK ELE.CABINET DETAILS

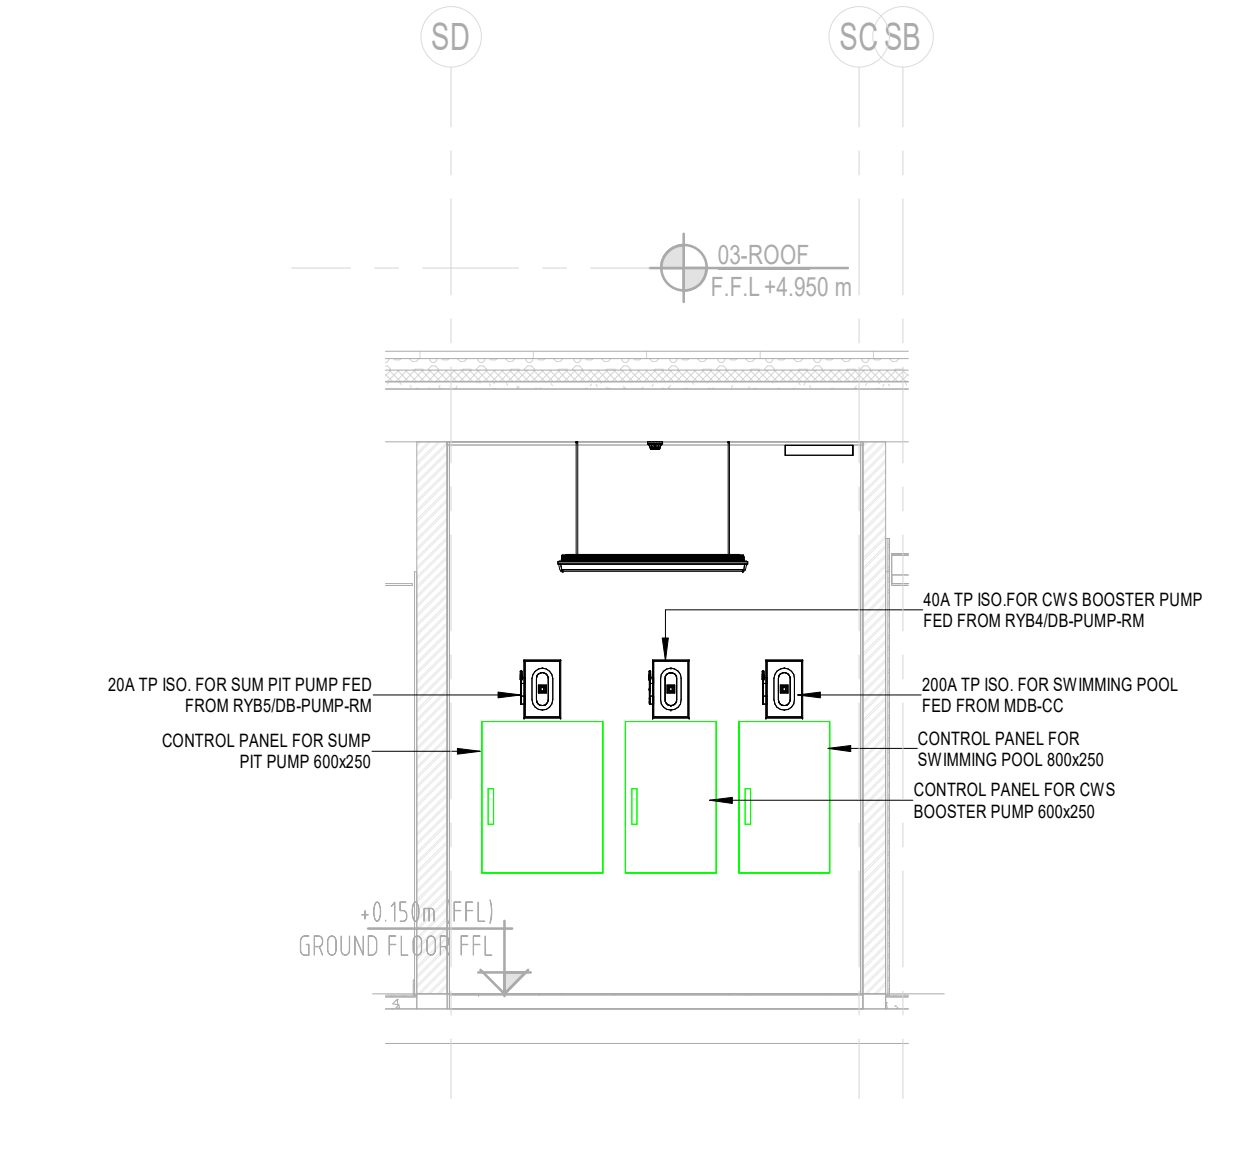


5 PUMP ROOM ELE.CABINET DETAILS SECTION
1 : 50

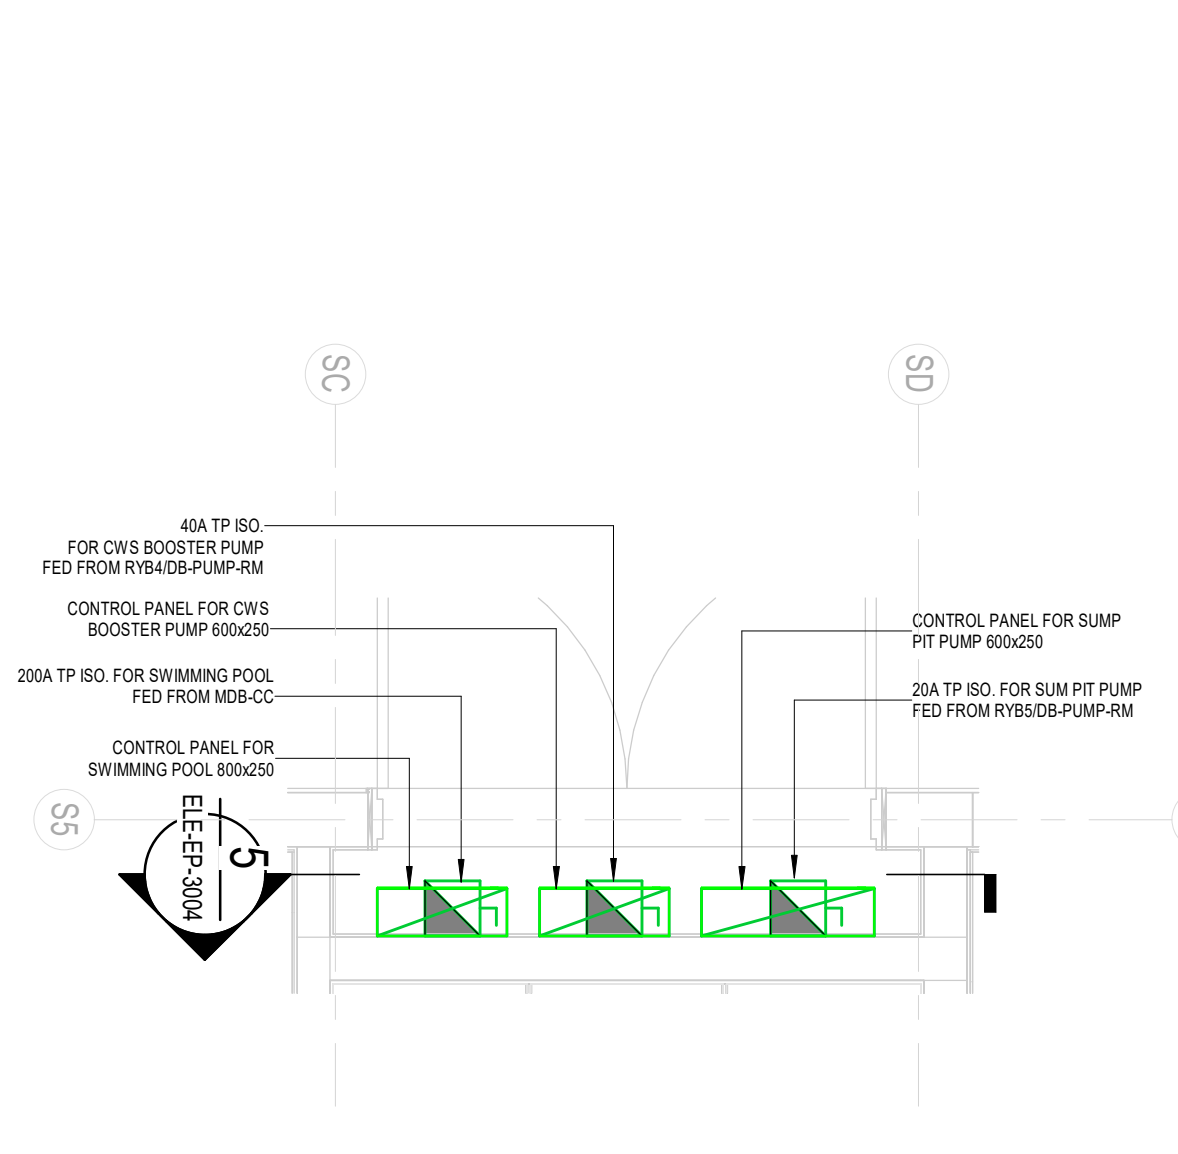


PUMP ROOM ELE.CABINET DETAILS

POWER LEGENDS	
	13A SINGLE SWITCHED SOCKET OUTLET
	13A TWIN SWITCHED SOCKET OUTLET
	FLEX OUTLET
	13A UN SWITCHED FUSED SPUR OUTLET
	13A SWITCHED FUSED SPUR OUTLET
	20A DP SWITCH WITH NEON SIGN INDICATOR
	20A FLEX OUTLET
	13A SWITCHED SPUR OUTLET WITH NEON INDICATOR FOR A/C UNIT
	SINGLE PHASE ISOLATOR IP 65 (RATING AS INDICATED)
	THREE PHASE ISOLATOR IP 65 (RATING AS INDICATED)
	ELECTRICAL FINAL DISTRIBUTION BOARD (DB) 'X' INDICATING FLOOR REF, 'Y' INDICATING FLAT REF.
	ELECTRICAL MAIN DISTRIBUTION BOARD (MDB)
ABBREVIATION	
'WP' - WEATHER PROOF	
'HD' - HAND DRYER	

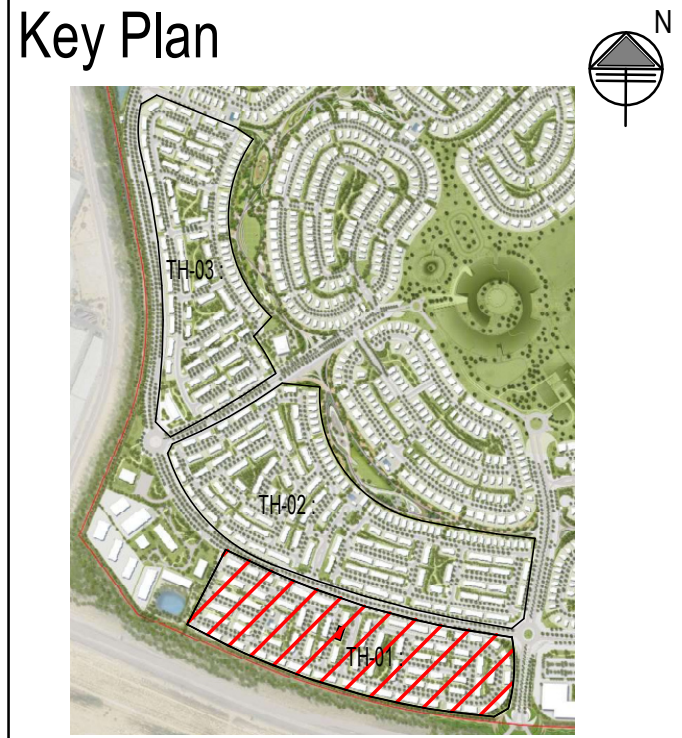

- General Notes :**
- Do not Scale The Drawings. Follow (The MM) Written Dimensions Unless Otherwise Mentioned.
 - Each Drawing Shall be Read in Conjunction With all Other Drawings, Specification & the General Standard Details. In Case of Any Discrepancies Bring it to the Knowledge of Engineer and Same to be Resolved Prior to Execution of Work.
 - Dimensions Shown on These Drawings are Structural Dimensions Unless Noted Otherwise.
 - All Levels Indicated On These Drawings are Levels as per the Survey Datum, Same Should be Verified at Site Prior to Execution of Work.
 - All Levels Indicated On These Drawings are Based On Design Level, Which is Equivalent to Datum Level and Same Should be Verified at Site Prior to Execution of Work.

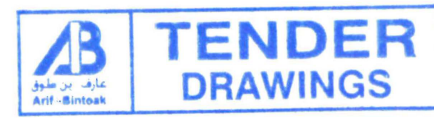

No.	Date	Initials	Description
-----	------	----------	-------------

REVISIONS / ISSUE

THIS DRAWING MUST NOT BE REPRODUCED IN WHOLE OR IN PART WITHOUT THE PRIOR APPROVAL OF ARIF & BINTOAK

TENDER SUBMISSION

Client
EMAAR

Lead Consultant
Arif & BintOak
consulting architects & engineers
P.O. BOX 420181 ABU DHABI, UAE TEL: 02-6246688 FAX: 02-6246688
POST BOX 420181 ABU DHABI, UAE TEL: 02-6246688 FAX: 02-6246688

Project Title:
**COMMUNITY CENTER - TH01
GRANDPOLP CLUB & RESORT, UAE**

Discipline: **ELECTRICAL**

Drawing title:
**SERVICE BLOCK U.W.T,
GROUND & ROOF FLOOR PLAN
POWER LAYOUT**

Architectural Engineer	Electrical Engineer	Structural Engineer
MUSTAFA ABID	MARWAN MOHD.	RIHAM RAMADAN
Registration # 5847	Registration # 80102	Registration # 105092
Scale(s): As indicated	Date drawn: 10/03/2026	Project no: 1857
Drawn by: VPA	Checked: HAE	Approved: MRM

Drawing Number: **GPCR-TH01-AB-DRG-ZZZ-ELE-EP-3004-00**