



This 2D drawing is extracted from 3D BIM Model

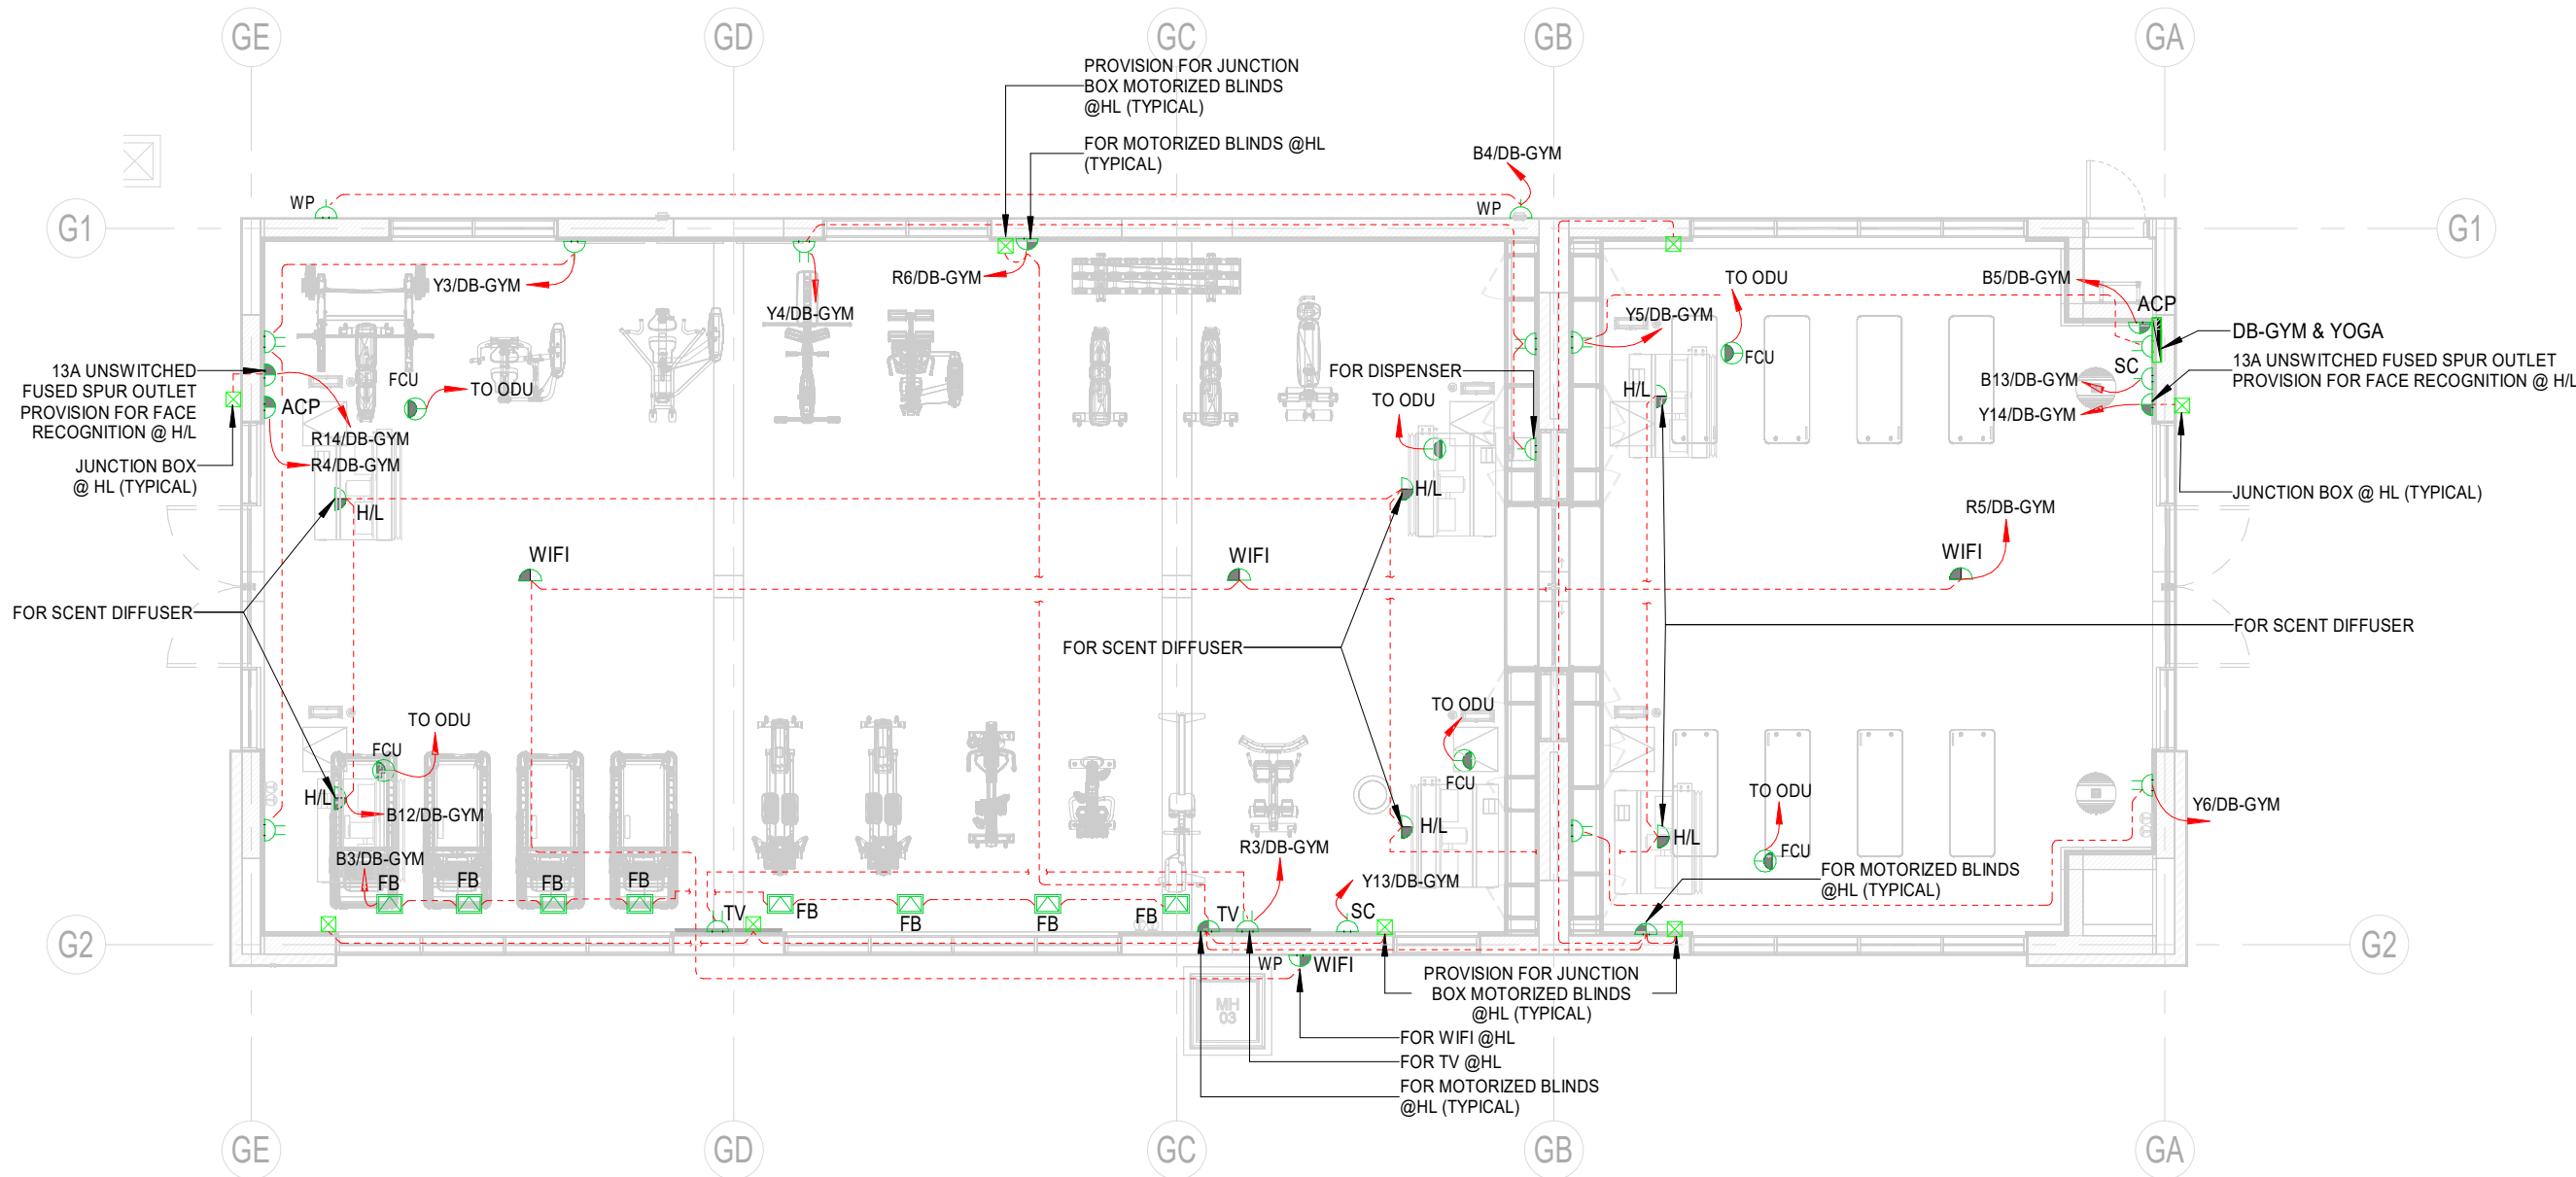

1 01-GROUND FLOOR GYM POWER
1 : 100

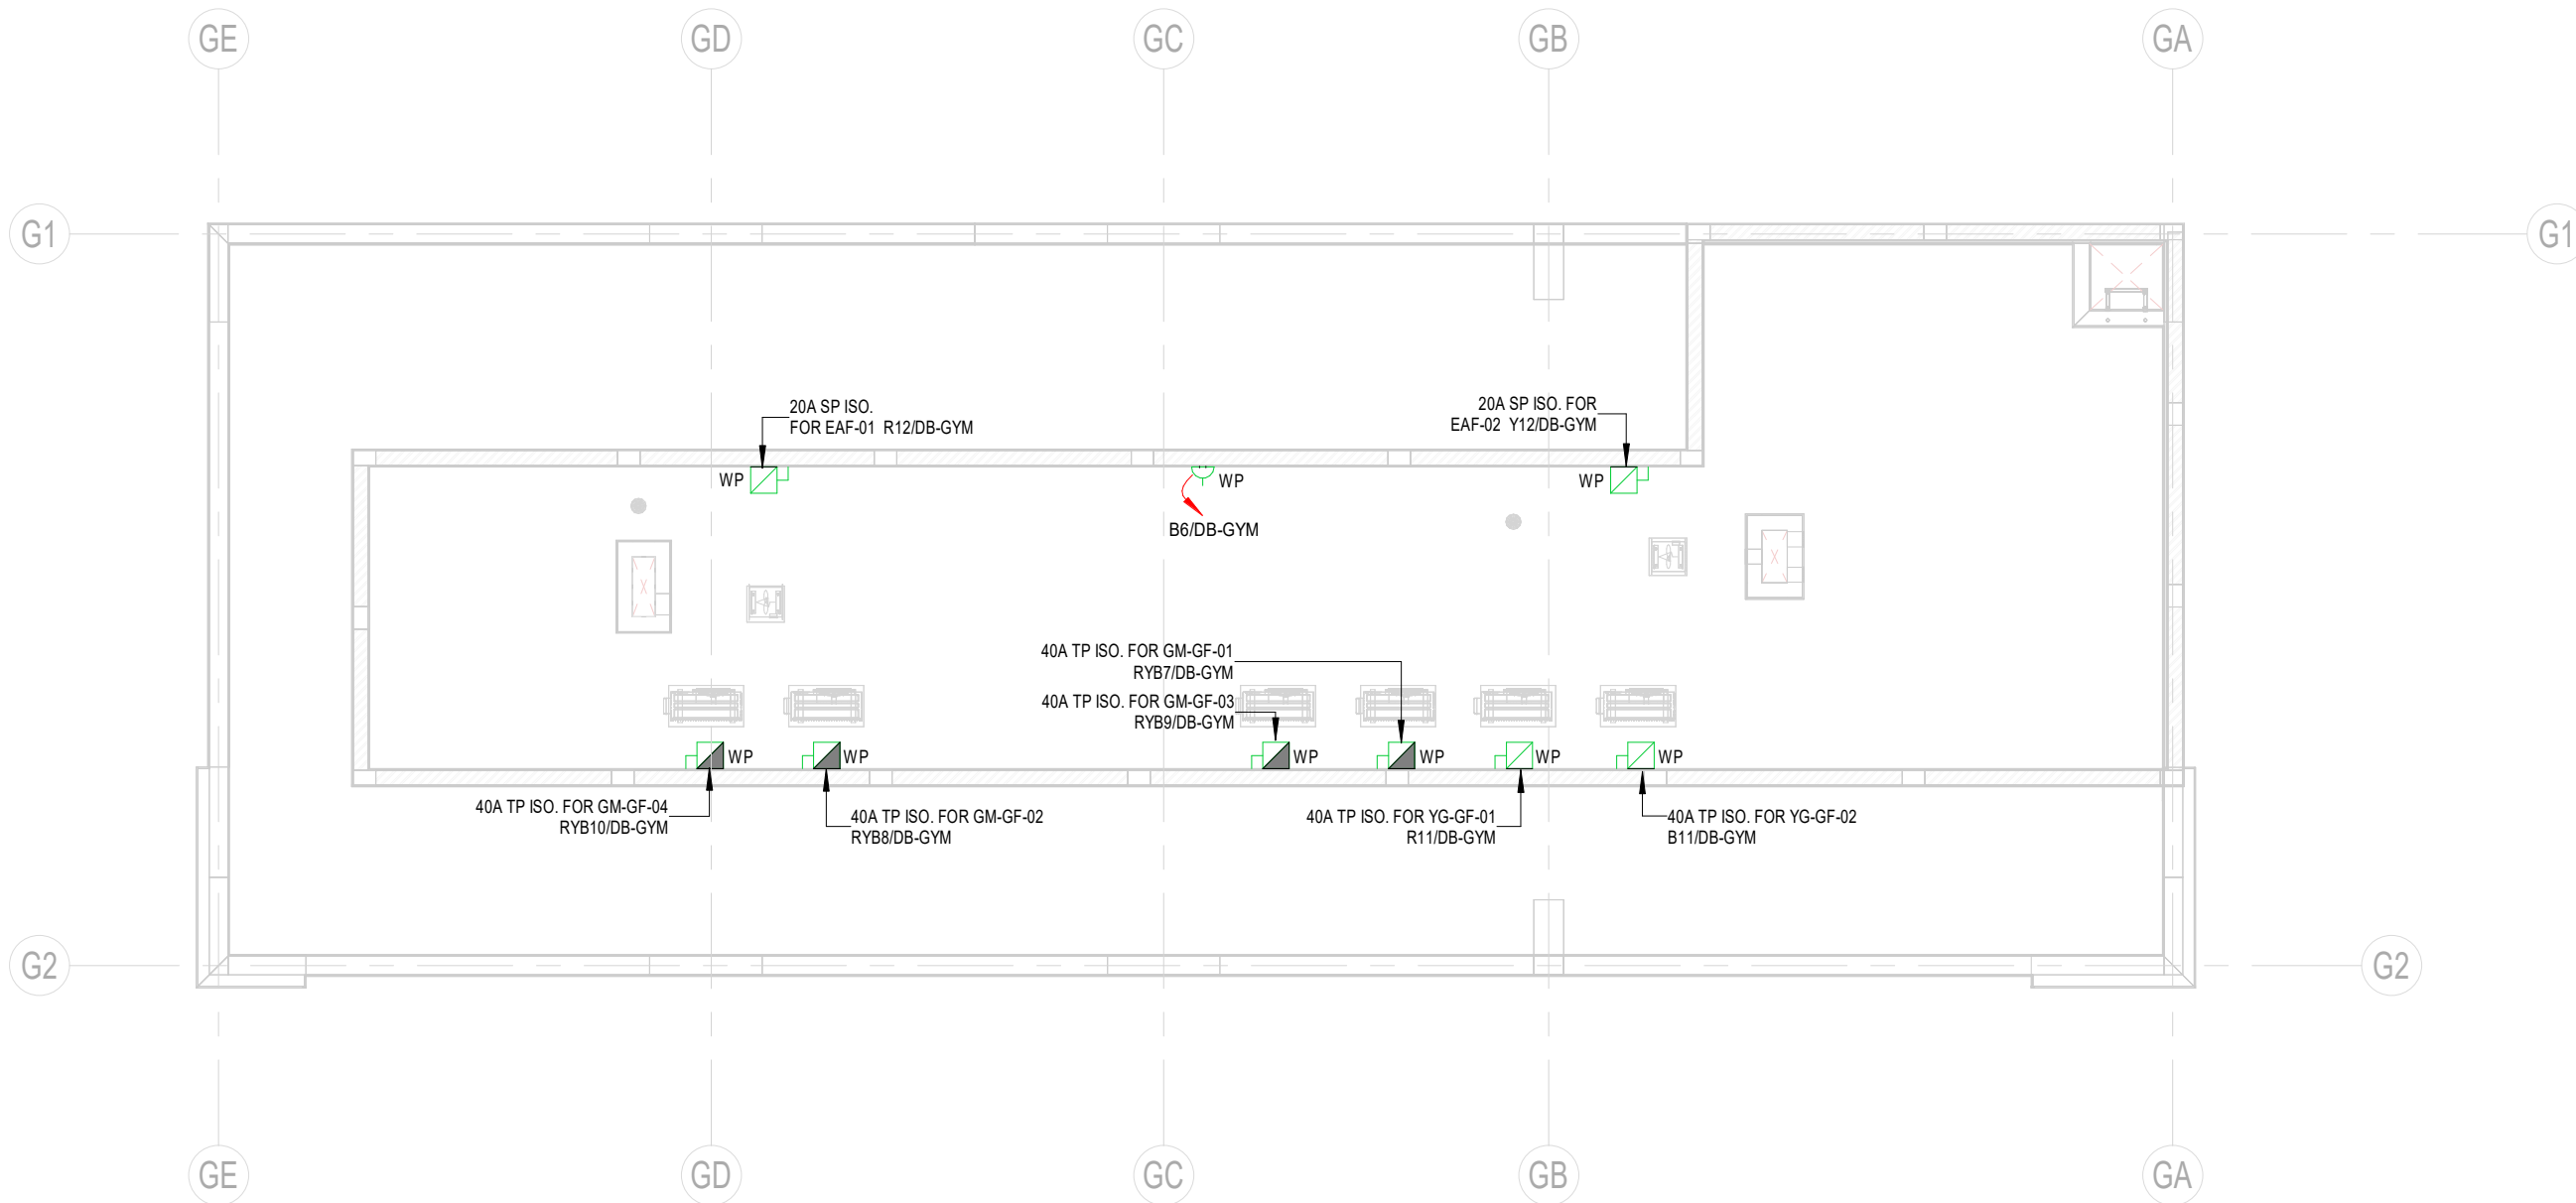

2 02-ROOF GYM POWER
1 : 100

POWER LEGENDS	
	13A SINGLE SWITCHED SOCKET OUTLET
	13A TWIN SWITCHED SOCKET OUTLET
	FLOOR BOX (13A SINGLE SOCKET)
	FLEX OUTLET
	13A UN SWITCHED FUSED SPUR OUTLET
	13A SWITCHED FUSED SPUR OUTLET
	20A DP SWITCH WITH NEON SIGN INDICATOR.
	20A FLEX OUTLET
	13A SWITCHED SPUR OUTLET WITH NEON INDICATOR FOR A/C UNIT.
	SINGLE PHASE ISOLATOR IP 65 (RATING AS INDICATED)
	THREE PHASE ISOLATOR IP 65 (RATING AS INDICATED)
	ELECTRICAL FINAL DISTRIBUTION BOARD (DB)
	'X' INDICATING FLOOR REF, 'X' INDICATING FLAT REF.
ABBREVIATION	
'WP'	- WEATHER PROOF
'HD'	- HAND DRYER



- General Notes :**
- Do not Scale The Drawings. Follow (The MM) Written Dimensions Unless Otherwise Mentioned.
 - Each Drawing Shall be Read in Conjunction With all Other Drawings, Specification & the General Standard Details. In Case of Any Discrepancies Bring it to the Knowledge of Engineer and Same to be Resolved Prior to Execution of Work.
 - Dimensions Shown on These Drawings are Structural Dimensions Unless Noted Otherwise.
 - All Levels Indicated On These Drawings are Levels as per the the Survey Datum, Same Should be Verified at Site Prior to Execution of Work.
 - All Levels Indicated On These Drawings are Based On Design Level, Which is Equivalent to Datum Level and Same Should be Verified at Site Prior to Execution of Work.

00 10/03/2026 VPA TENDER SUBMISSION

No.	Date	Initials	Description
REVISIONS / ISSUE			
THIS DRAWING MUST NOT BE REPRODUCED IN WHOLE OR IN PART WITHOUT THE PRIOR APPROVAL OF ARIF & BINTOAK			
Status	TENDER SUBMISSION		
Client	EMAAR		
Lead Consultant	المستشارين: عارف وبن طوق Arif & BintOak consulting architects & engineers P.O. BOX 4201 ABU DHABI, UAE TEL: 02-454668 FAX: 02-454669 P.O. BOX 4201 ABU DHABI, UAE TEL: 02-454668 FAX: 02-454669		
Project Title:	COMMUNITY CENTER - TH01 GRANDPOLP CLUB & RESORT, UAE		
Discipline :	ELECTRICAL		
Drawing title:	GYM GROUND & ROOF FLOOR PLAN POWER LAYOUT		
Architectural Engineer	Electrical Engineer	Structural Engineer	
MUSTAFA ABID	MARWAN MOHD.	RIHAM RAMADAN	
Registration # 5847	Registration # 80102	Registration # 105092	
Scale(s): 1 : 100	Date drawn: 10/03/2026	Project no: 1857	
Drawn by: VPA	Checked: HAE	Approved: MRM	
Drawing Number:	GPCR-TH01-AB-DRG-ZZZ-ELE-EP-3005-00		

© AB 1 A1 Title Block - BIM Standard Ver. 2.0

04/03/2026 1:50:43 PM