


SMDB-CC

LOC.: ELEC. CABINET
TOTAL CONN. LOAD = 220.00 kW
DIVERSITY FACTOR = 0.90 kW
MAXIMUM DEMAND = 198.00kW

Key Plan

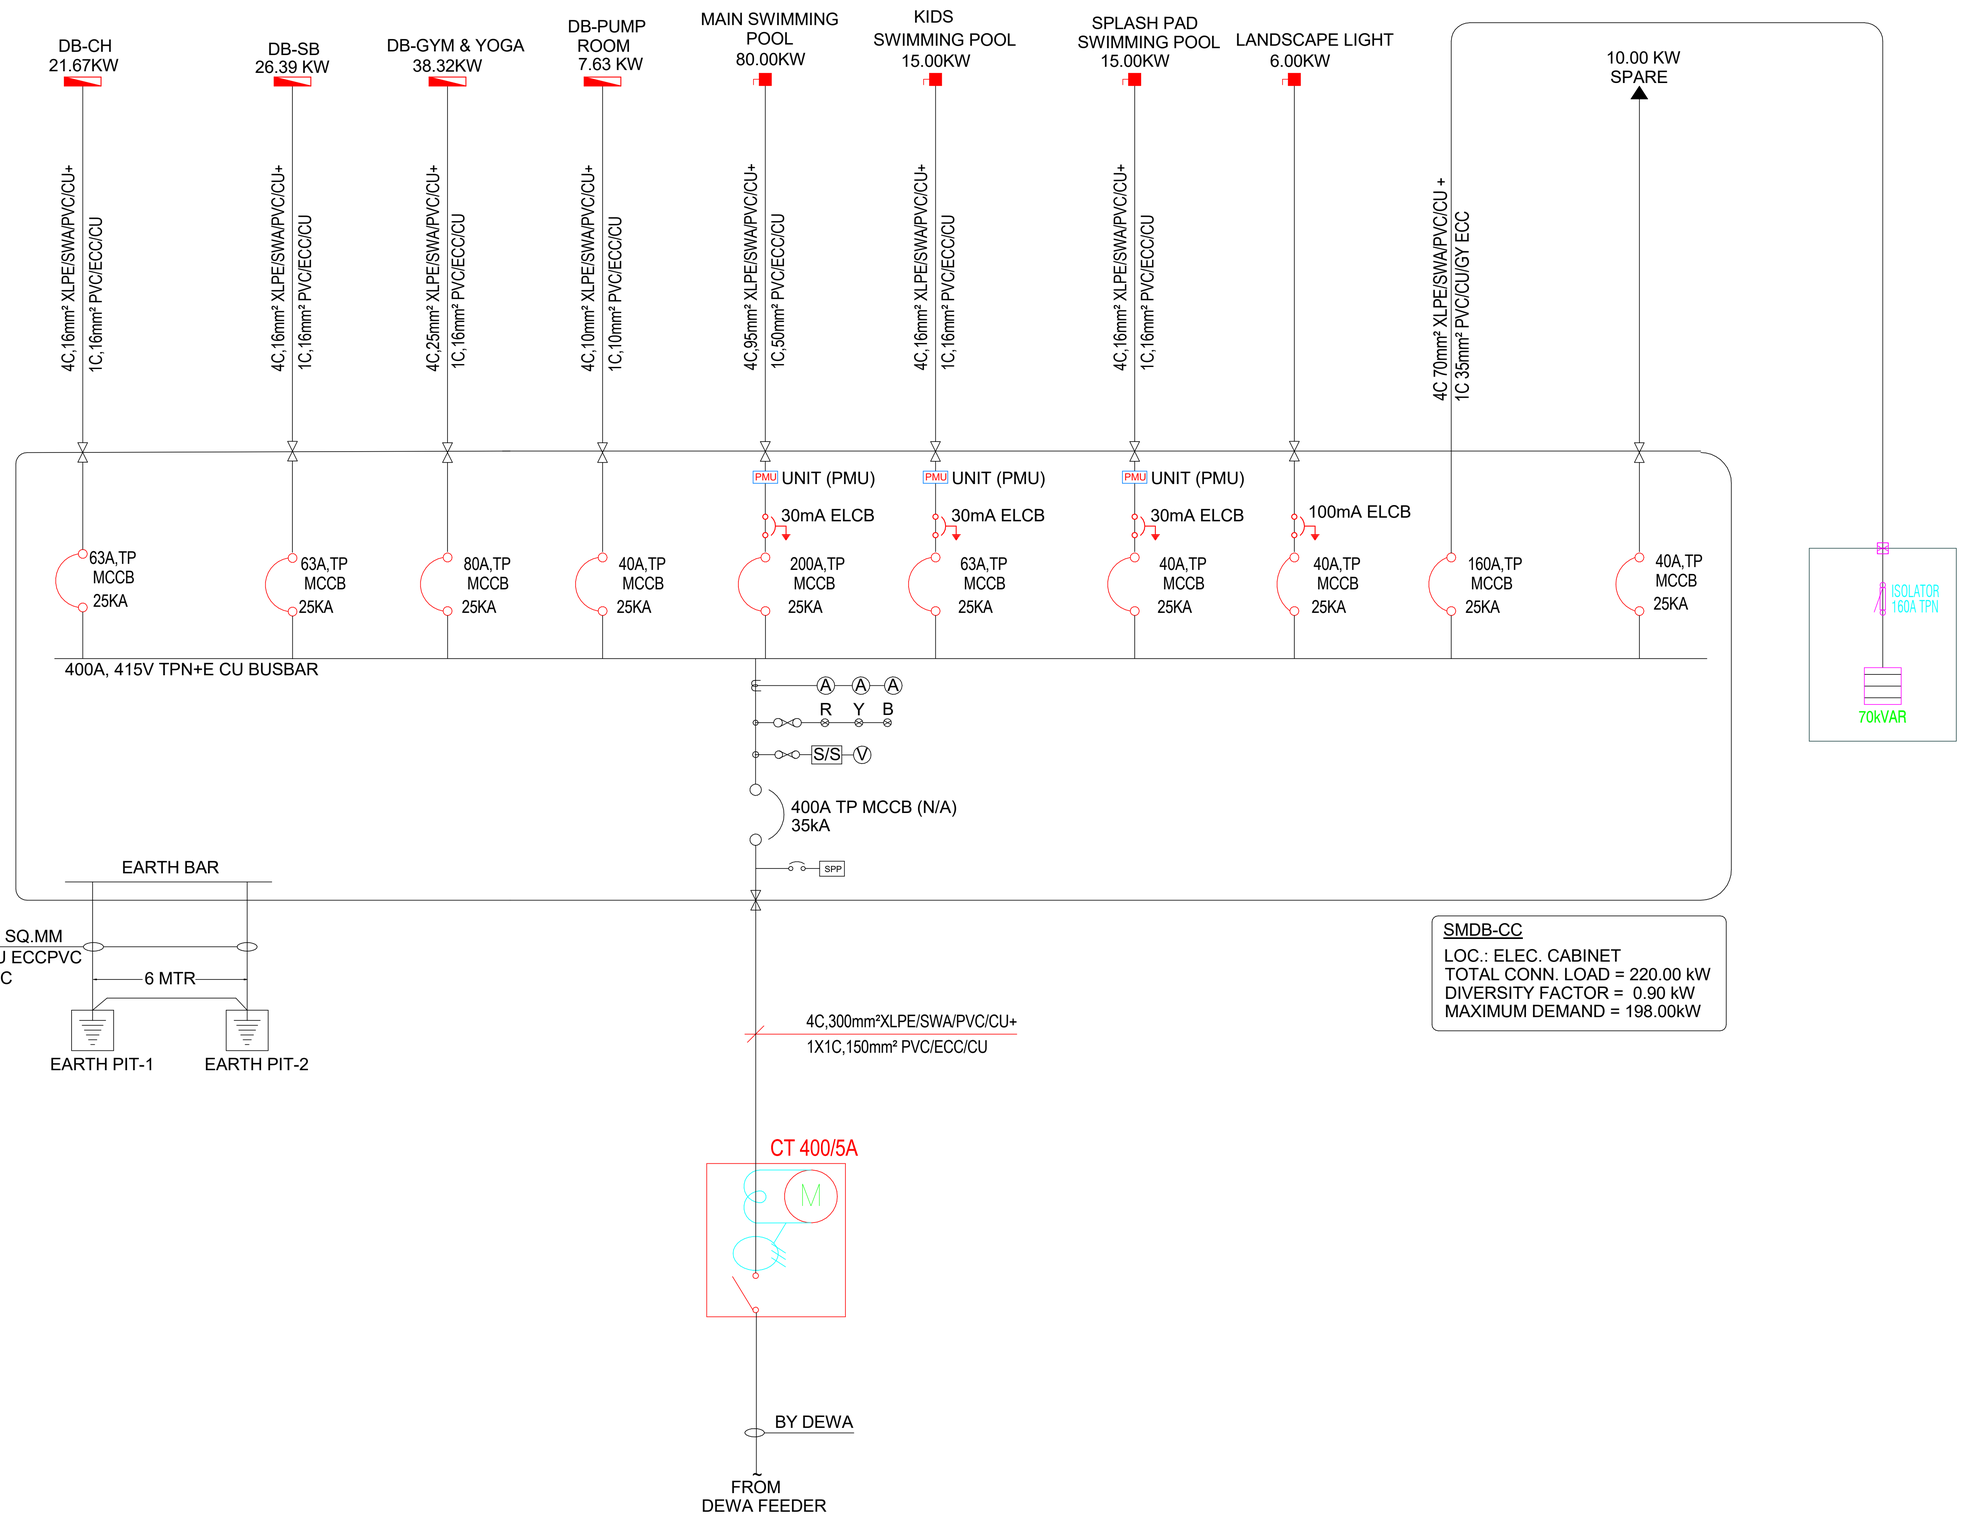

General Notes :

01. Do not Scale The Drawings. Follow (The MM) Written Dimensions Unless Otherwise Mentioned.
02. Each Drawing Shall be Read in Conjunction With all Other Drawings,Specification & the General Standard Details. In Case of Any Discrepancies Bring it to the Knowledge of Engineer and Same to be Resolved Prior to Execution of Work.
03. Dimensions Shown on These Drawings are Structural Dimensions. Unless Noted Otherwise.
04. All Levels Indicated On These Drawings are Levels as per the the Survey Datum, Same Should be Verified at Site Prior to Execution of Work.
05. All Levels Indicated On These Drawings are Based On Design Level, Which is Equivalent to Datum Level and Same Should be Verified at Site Prior to Execution of Work.

TENDER DRAWINGS

No.	Date	Initials	Description
00	10/03/2026	VPA	TENDER SUBMISSION

REVISIONS / ISSUE

THIS DRAWING MUST NOT BE REPRODUCED IN WHOLE OR IN PART WITHOUT THE PRIOR APPROVAL OF ARIF & BINTOAK

Status: TENDER SUBMISSION

Client: EMAAR

Lead Consultant
الاستشاري:
عارف وبن طوق
Arif&Bintoak
consulting architects & engineers
POST BOX 3670 DUBAI,UAE TEL 04-3372866 FAX 04-3370932
POST BOX 42981 ABU DHABI,UAE TEL 02-634669 artoak@emirates.net.ae

Project Title:

COMMUNITY CENTER -TH01
GRANDPOLP CLUB & RESORT, UAE

Discipline : ELECTRICAL

Drawing title:

COMMUNITY CENTER POWER SINGLE LINE DIAGRAM

Architectural Engineer	Electrical Engineer	Structural Engineer
MUSTAFA ABID	MARWAN MOHD.	RIHAM RAMADAN
Registration # 5847	Registration # 80102	Registration # 105092
Scale(s): 1 : 50	Date drawn: 10/03/2026	Project no: 1857
Drawn by: VPA	Checked : HAE	Approved : MRM

Drawing Number : GPCR-TH01-AB-DRG-ZZZ-ELE-EP-3020-00

This 2D drawing is extracted from 3D BIM Model

04/03/2026 1:50:52 PM

© AB I A1 Title Block . BIM Standard Ver. 2.0