



This 2D drawing is extracted from 3D BIM Model

1 01-GROUND FLOOR SERVICE BLOCK FIRE ALARM & EMERGENCY  
1 : 100

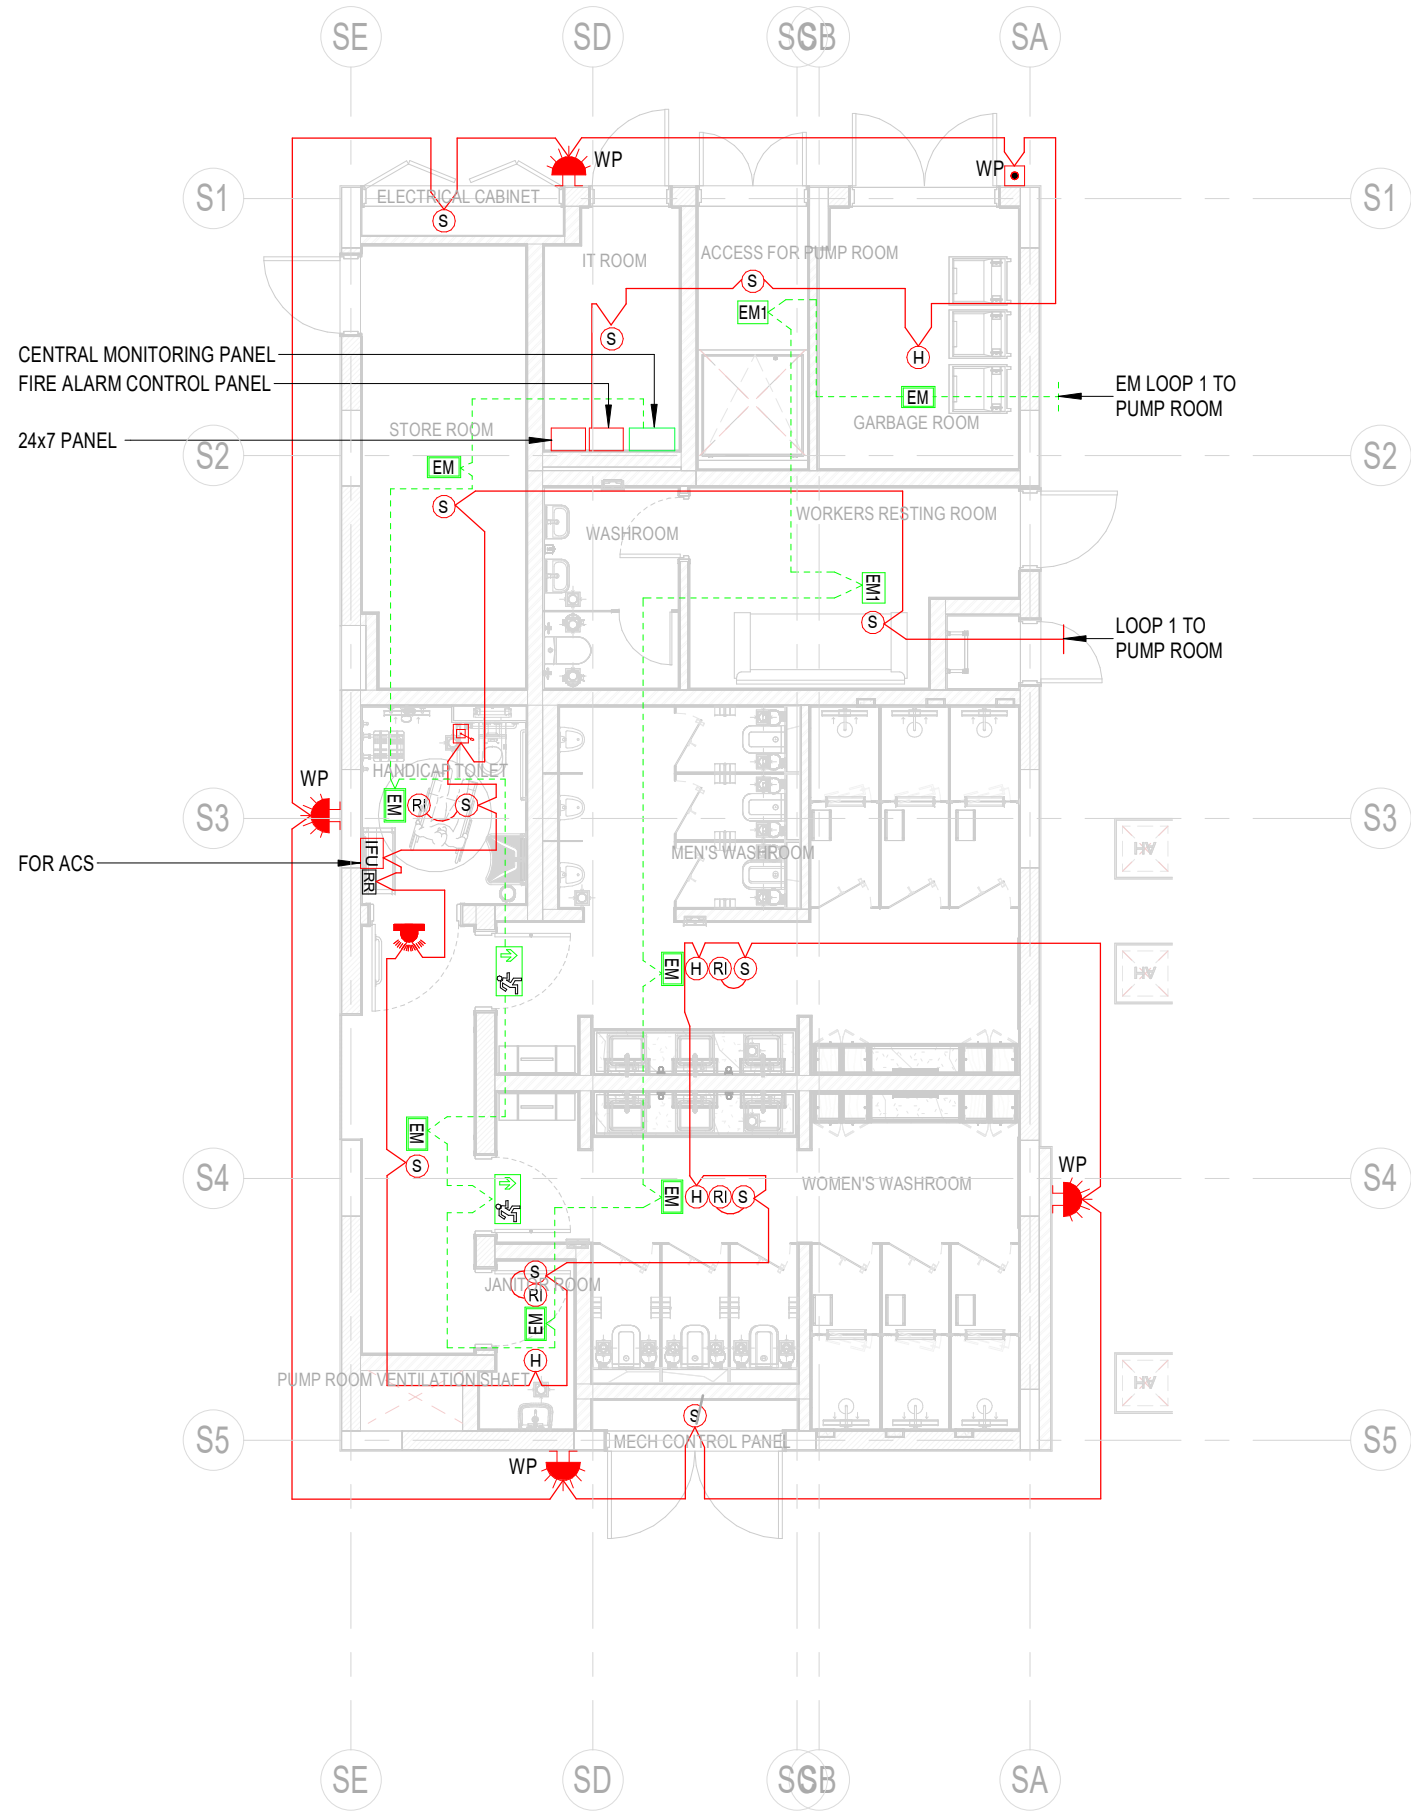

2 00-U.W.T SERVICE BLOCK FIRE ALARM & EMERGENCY  
1 : 100

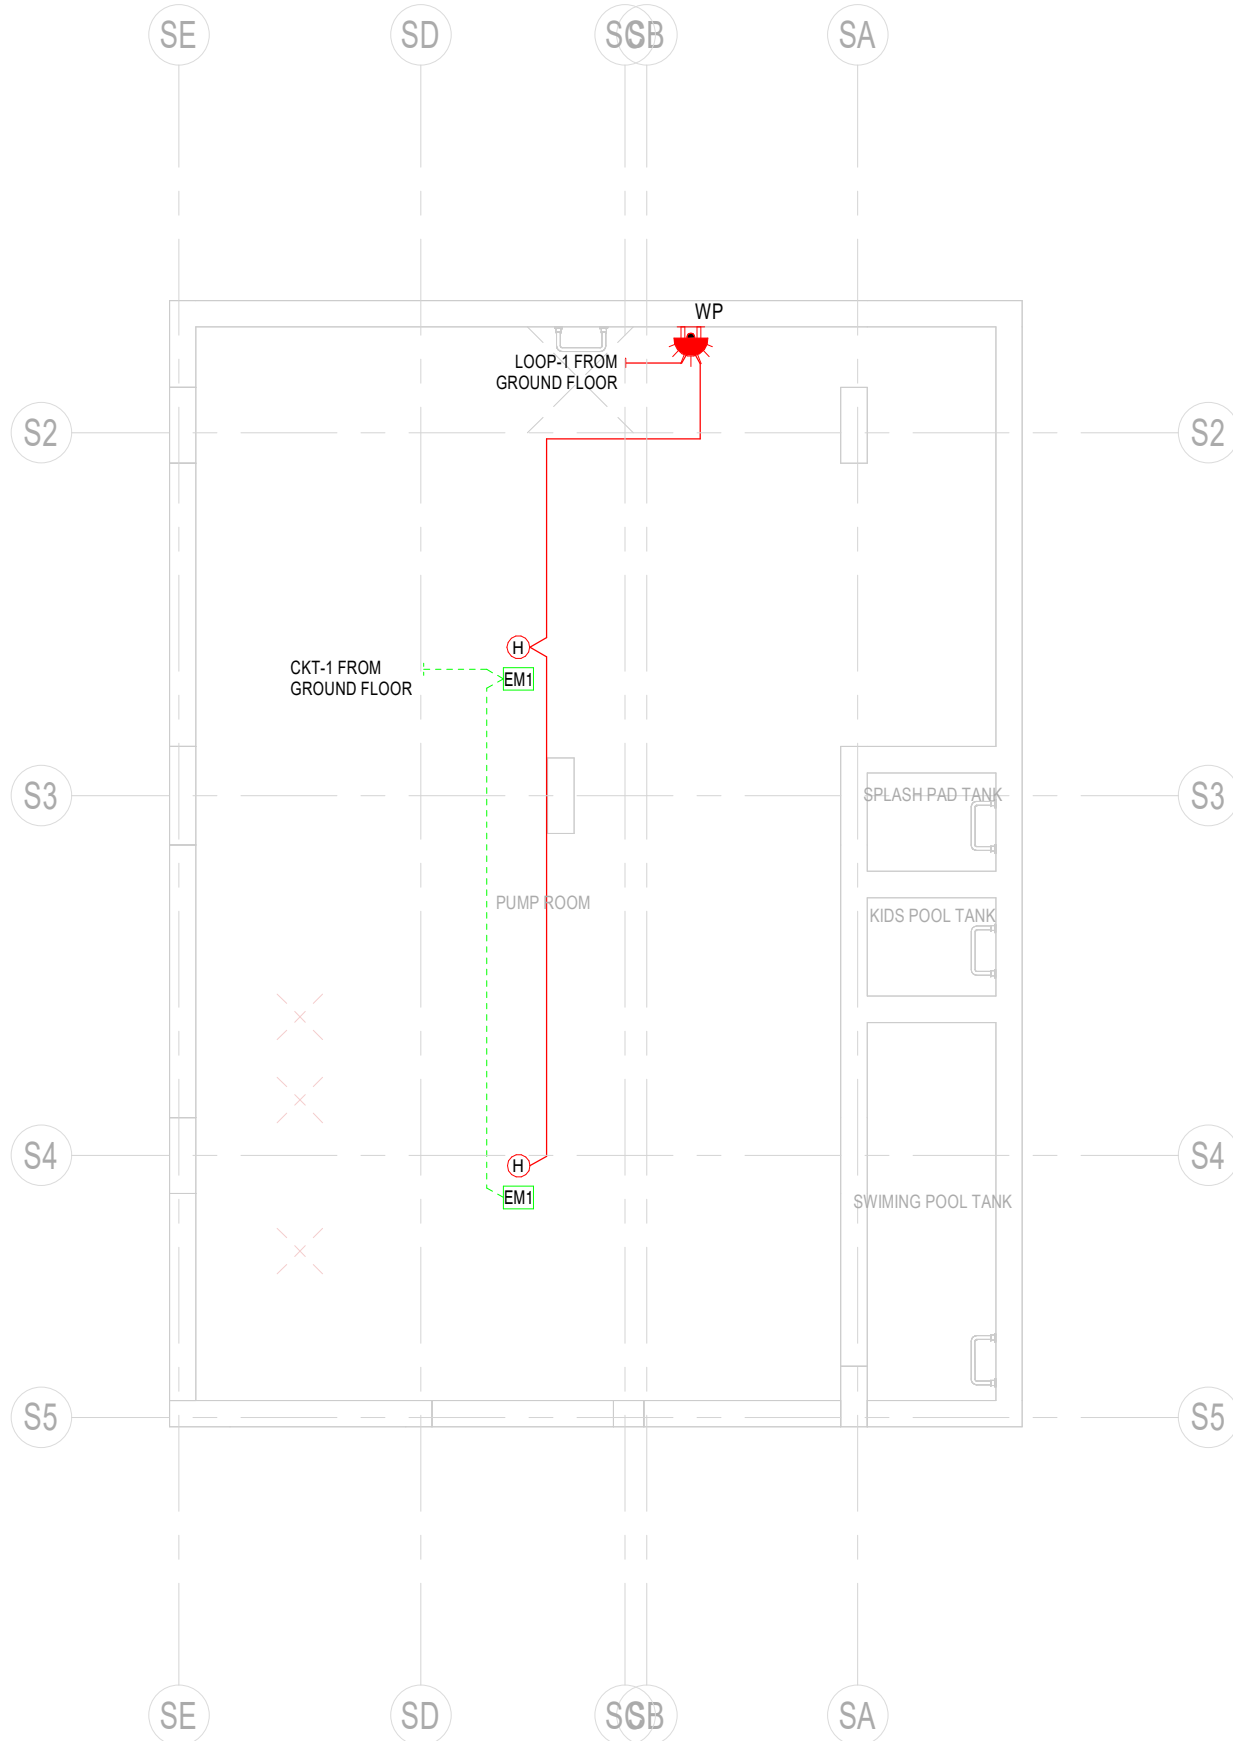

| LIFE SAFETY                                        |   |
|----------------------------------------------------|---|
| FIRE DETECTION & ALARM SYSTEM & EMERGENCY LIGHTING |   |
|                                                    | INTELLIGENT OPTICAL SMOKE DETECTOR WITH BUILT IN ISOLATOR   |
|                                                    | INTELLIGENT HEAT DETECTOR WITH STANDARD BASE   |
|                                                    | SMOKE DETECTOR WITH REMOTE INDICATOR FOR VOID AREA   |
|                                                    | FIRE ALARM SOUNDER WITH FLASHER (W/P)   |
|                                                    | FIRE ALARM SOUNDER OR HORN WITH FLASHER BUILT IN ISOLATOR   |
|                                                    | INTERFACE UNIT WITH DUAL INPUT/OUTPUT CONTROL & MONITOR MODULE   |
|                                                    | PULL CORD FOR DISABLED TOILETS WITH RESET BUTTON   |
|                                                    | VISUAL ANNUNCIATOR FOR DISABLED TOILET ALARM   |
|                                                    | REMOTE RESET BUTTON FOR TOILET WEATHER PROOF   |
|                                                    | FIRE ALARM CONTROL PANEL   |
|                                                    | 24x7 PANEL   |
|                                                    | ADDRESSABLE COMPACT & DECORATIVE EDGE LIGHT EXIT LIGHT, MAINTAINED, HANGING (OR) RECESS MOUNTED TYPE, WITH (SINGLE SIDED) GLASS FINISH LEGEND LASER PRINTED, IP20 |
|                                                    | ADDRESSABLE EMERGENCY LIGHT, NON-MAINTAINED, COMPACT TYPE, CIRCULAR IN SHAPE RECESS MOUNTED, IP55                                                                 |
|                                                    | ADDRESSABLE EMERGENCY LIGHT, NON-MAINTAINED, COMPACT TYPE, SQUARE (OR) CIRCULAR IN SHAPE SURFACE (OR) SEMI-RECESS MOUNTED, IP55                                   |
|                                                    | CENTRAL MONITORING PANEL   |

Key Plan

General Notes :

01. Do not Scale The Drawings. Follow (The MM) Written Dimensions Unless Otherwise Mentioned.

02. Each Drawing Shall be Read in Conjunction With all Other Drawings, Specification & the General Standard Details. In Case of Any Discrepancies Bring it to the Knowledge of Engineer and Same to be Resolved Prior to Execution of Work.

03. Dimensions Shown on These Drawings are Structural Dimensions Unless Noted Otherwise.

04. All Levels Indicated On These Drawings are Levels as per the the Survey Datum, Same Should be Verified at Site Prior to Execution of Work.

05. All Levels Indicated On These Drawings are Based On Design Level, Which is Equivalent to Datum Level and Same Should be Verified at Site Prior to Execution of Work.

AB

TENDER DRAWINGS

00

10/03/2026

VPA

TENDER SUBMISSION

| No.   | Date | Initials                            | Description |
|---|------|-------------------------------------|-------------|
| REVISIONS / ISSUE   |      |                                     |             |
| THIS DRAWING MUST NOT BE REPRODUCED IN WHOLE OR IN PART WITHOUT THE PRIOR APPROVAL OF ARIF & BINTOAK   |      |                                     |             |
| Status   |      |                                     |             |
| TENDER SUBMISSION   |      |                                     |             |
| Client   |      |                                     |             |
| EMAAR   |      |                                     |             |
| Lead Consultant   |      |                                     |             |
| <div><div>المستشار:</div><div><div>عارف وبن طوق</div><div>Arif &amp; BintOak</div><div>consulting architects &amp; engineers</div></div></div> <div><div>PROJECT BOX WITH OVERALL LANE TEL: 94-02-22888 FAX: 94-02-274332</div><div>POST BOX 42061 ABU DHABI, UAE TEL: 02-4246668 -arifa@arifbintoak.net.ae</div></div> |      |                                     |             |
| Project Title:   |      |                                     |             |
| COMMUNITY CENTER - TH01<br>GRANDPOLP CLUB & RESORT, UAE   |      |                                     |             |
| Discipline :   |      |                                     |             |
| ELECTRICAL   |      |                                     |             |
| Drawing title:   |      |                                     |             |
| SERVICE BLOCK U.W.T &<br>GROUND FLOOR PLAN FIRE<br>ALARM & EMERGENCY LAYOUT   |      |                                     |             |
| Architectural Engineer   |      | Electrical Engineer                 |             |
| MUSTAFA ABID   |      | MARWAN MOHD.                        |             |
| Registration # 5847   |      | Registration # 80102                |             |
| Scale(s):   |      | Date drawn:                         |             |
| 1 : 100   |      | 10/03/2026                          |             |
| Project no:   |      | 1857                                |             |
| Drawn by:   |      | Checked:                            |             |
| VPA   |      | HAE                                 |             |
| Approved:   |      | MRM                                 |             |
| Drawing Number :   |      | GPCR-TH01-AB-DRG-ZZZ-ELE-FA-3008-00 |             |

© AB | A1 Title Block - BIM Standard Ver. 2.0

04/03/2026 1:51:02 PM