


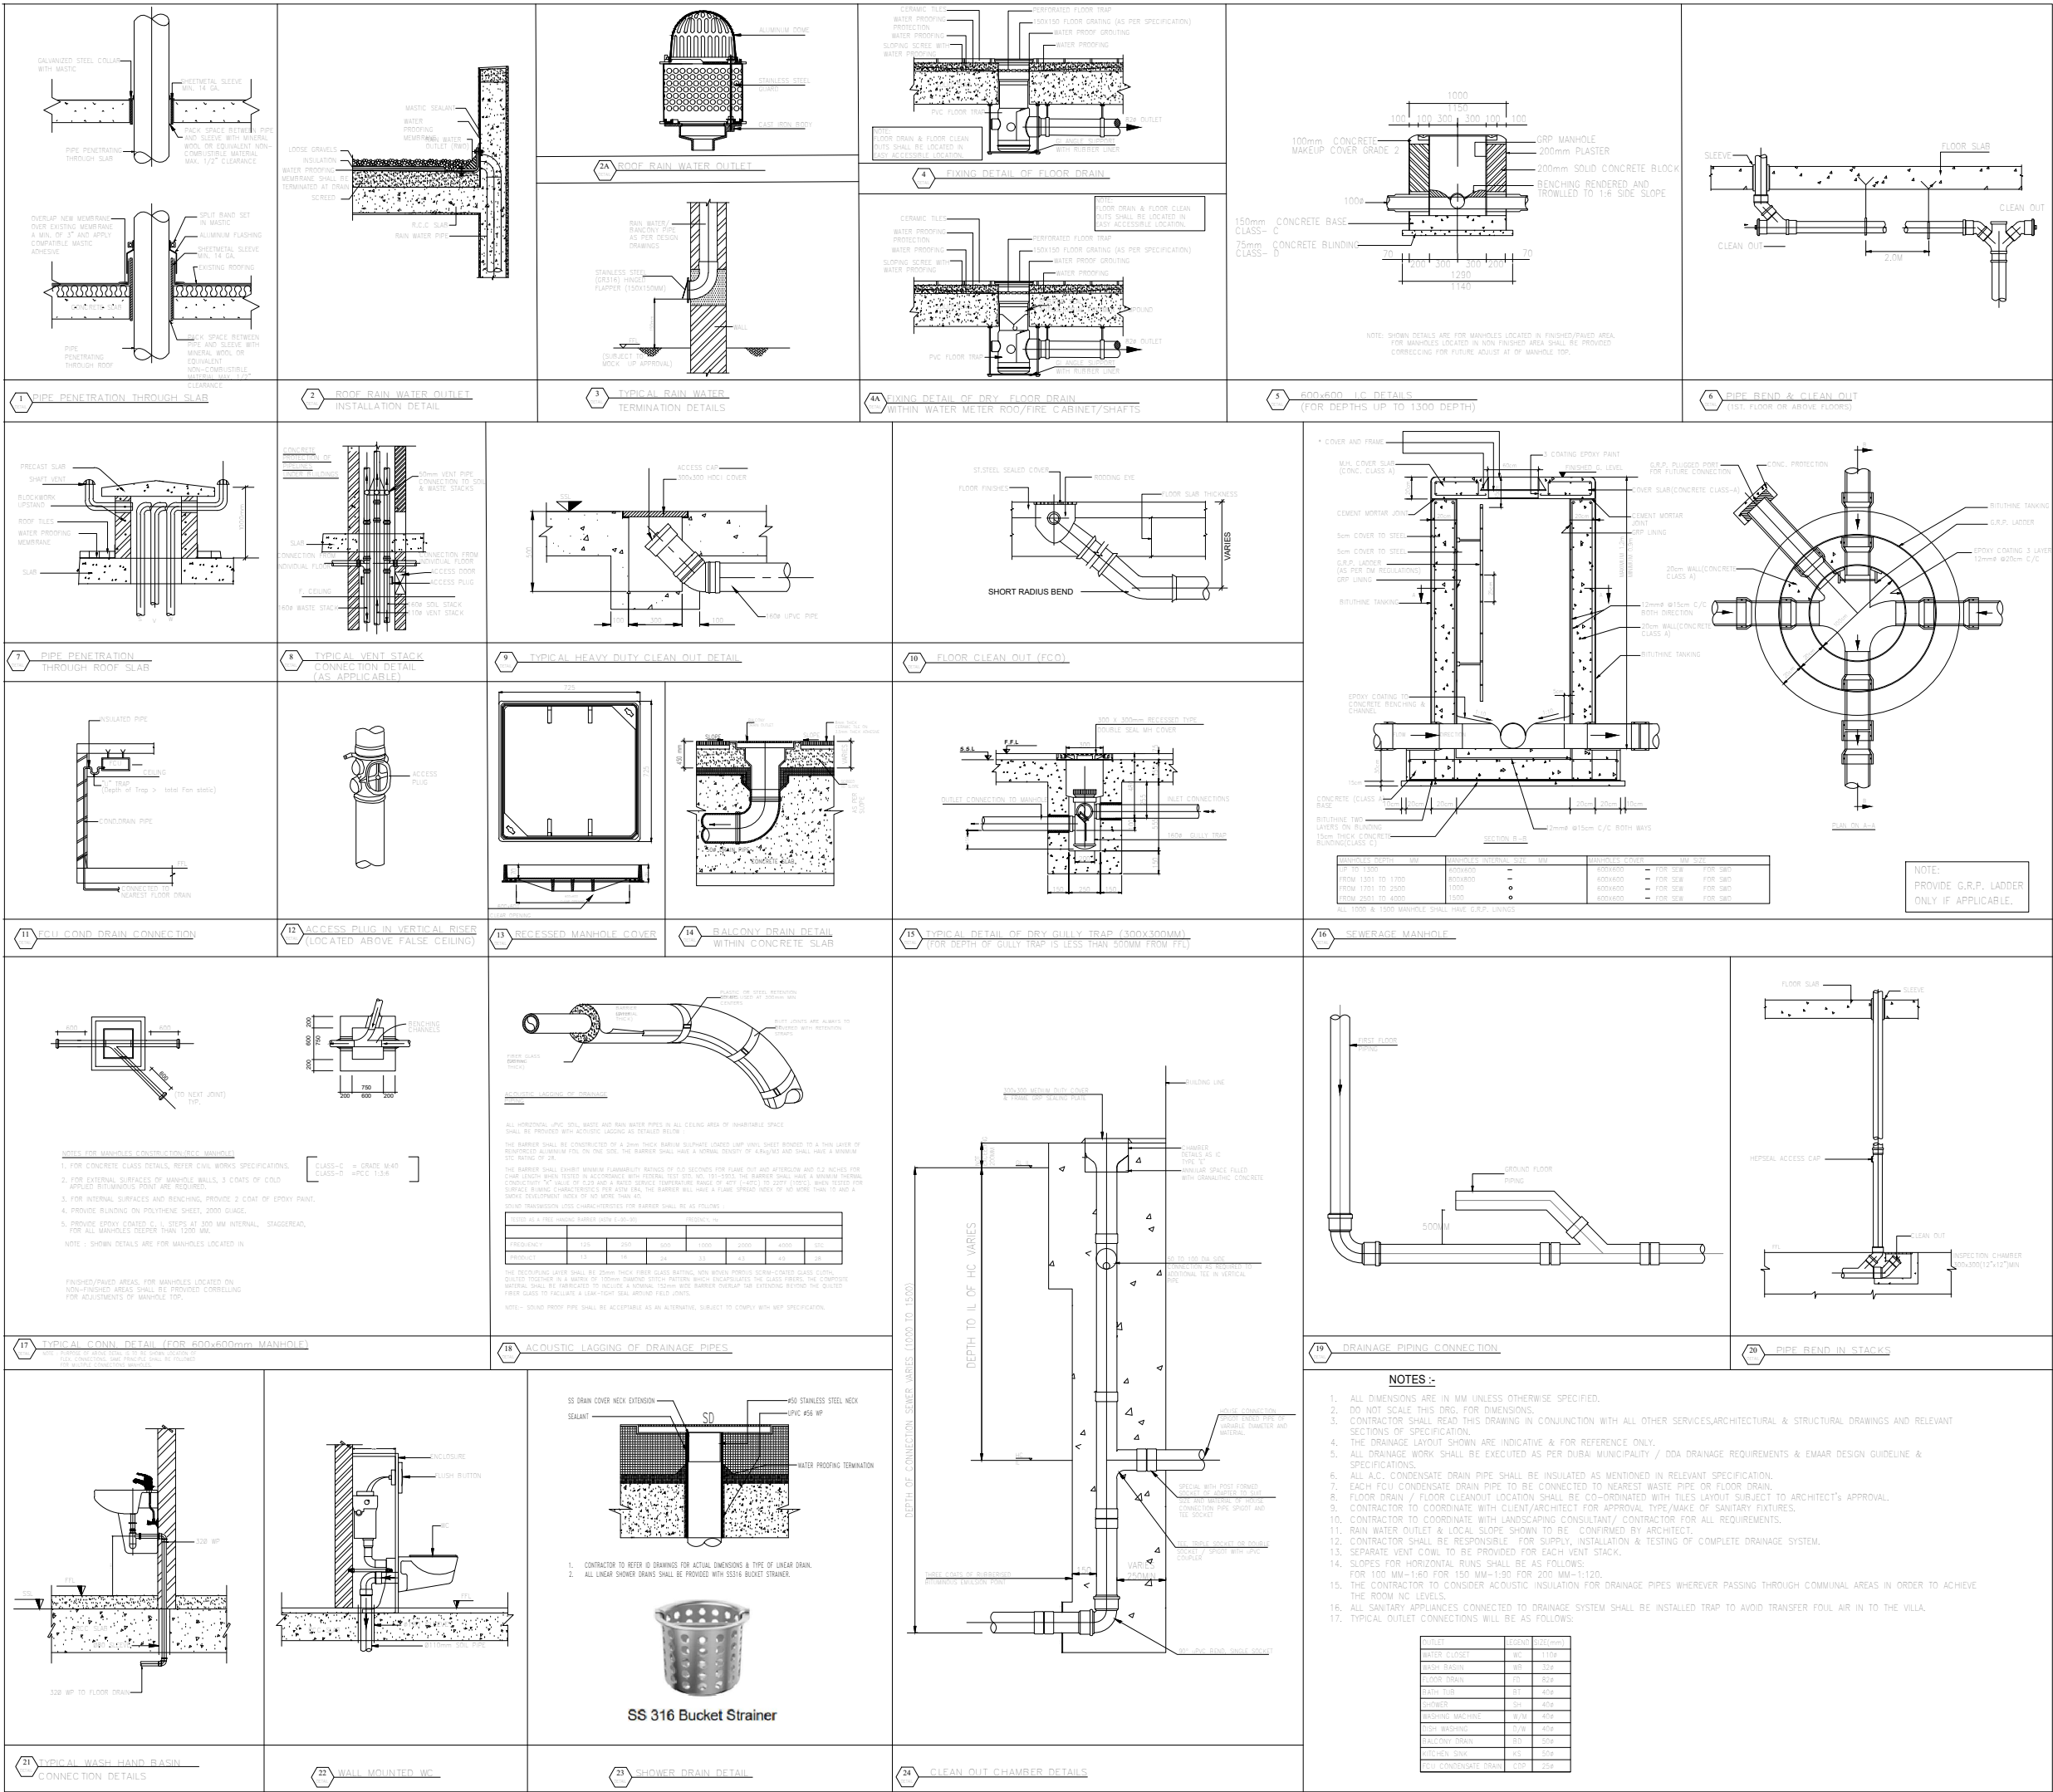

Key Plan



General Notes :

- Do not Scale The Drawings. Follow (The MM) Written Dimensions Unless Otherwise Mentioned.
- Each Drawing Shall be Read in Conjunction With all Other Drawings, Specification & the General Standard Details. In Case of Any Discrepancies Bring it to the Knowledge of Engineer and Same to be Resolved Prior to Execution of Work.
- Dimensions Shown on These Drawings are Structural Dimensions. Unless Noted Otherwise.
- All Levels Indicated On These Drawings are Levels as per the the Survey Datum. Same Should be Verified at Site Prior to Execution of Work.
- All Levels Indicated On These Drawings are Based On Design Level, Which is Equivalent to Datum Level and Same Should be Verified at Site Prior to Execution of Work.



No.	Date	Initials	Description
00	10/03/2026	LSG	TENDER SUBMISSION
00	16/01/2026	LSG	DETAILED DESIGN SUBMISSION
00	31/10/2025	LSG	SCHEMATIC DESIGN SUBMISSION
00	35/10/2025	LSG	SCHEMATIC SUBMISSION-50%
00	01/03/2025	LSG	CONCEPT DESIGN SUBMISSION

REVISIONS / ISSUE

THIS DRAWING MUST NOT BE REPRODUCED IN WHOLE OR IN PART WITHOUT THE PRIOR APPROVAL OF ARIF & BINTOAK

Status

TENDER SUBMISSION

Client

EMAAR

Lead Consultant



Project Title:

Proposed Residential Townhouses and Standalone Villas
TH-1, TH-2, and TH-3 at Grand Polo Club & Resort, Dubai, UAE

Discipline:

MECHANICAL

Drawing title:

DRAINAGE STANDARD DETAILS

Architectural Engineer	Electrical Engineer	Structural Engineer
MUSTAFA ABID	MARWAN MOHD.	RIHAM RAMADAN
Registration # 5847	Registration # 8102	Registration # 10592
Scale(s)	Date	Project no.
NTS	10/03/2026	1857
Drawn by:	Checked:	Approved:
LSG	MAV	MRM
Drawing Number:	GPCR-TH01-AB-DRG-ZZZ-MEC-DR-3001-00	