


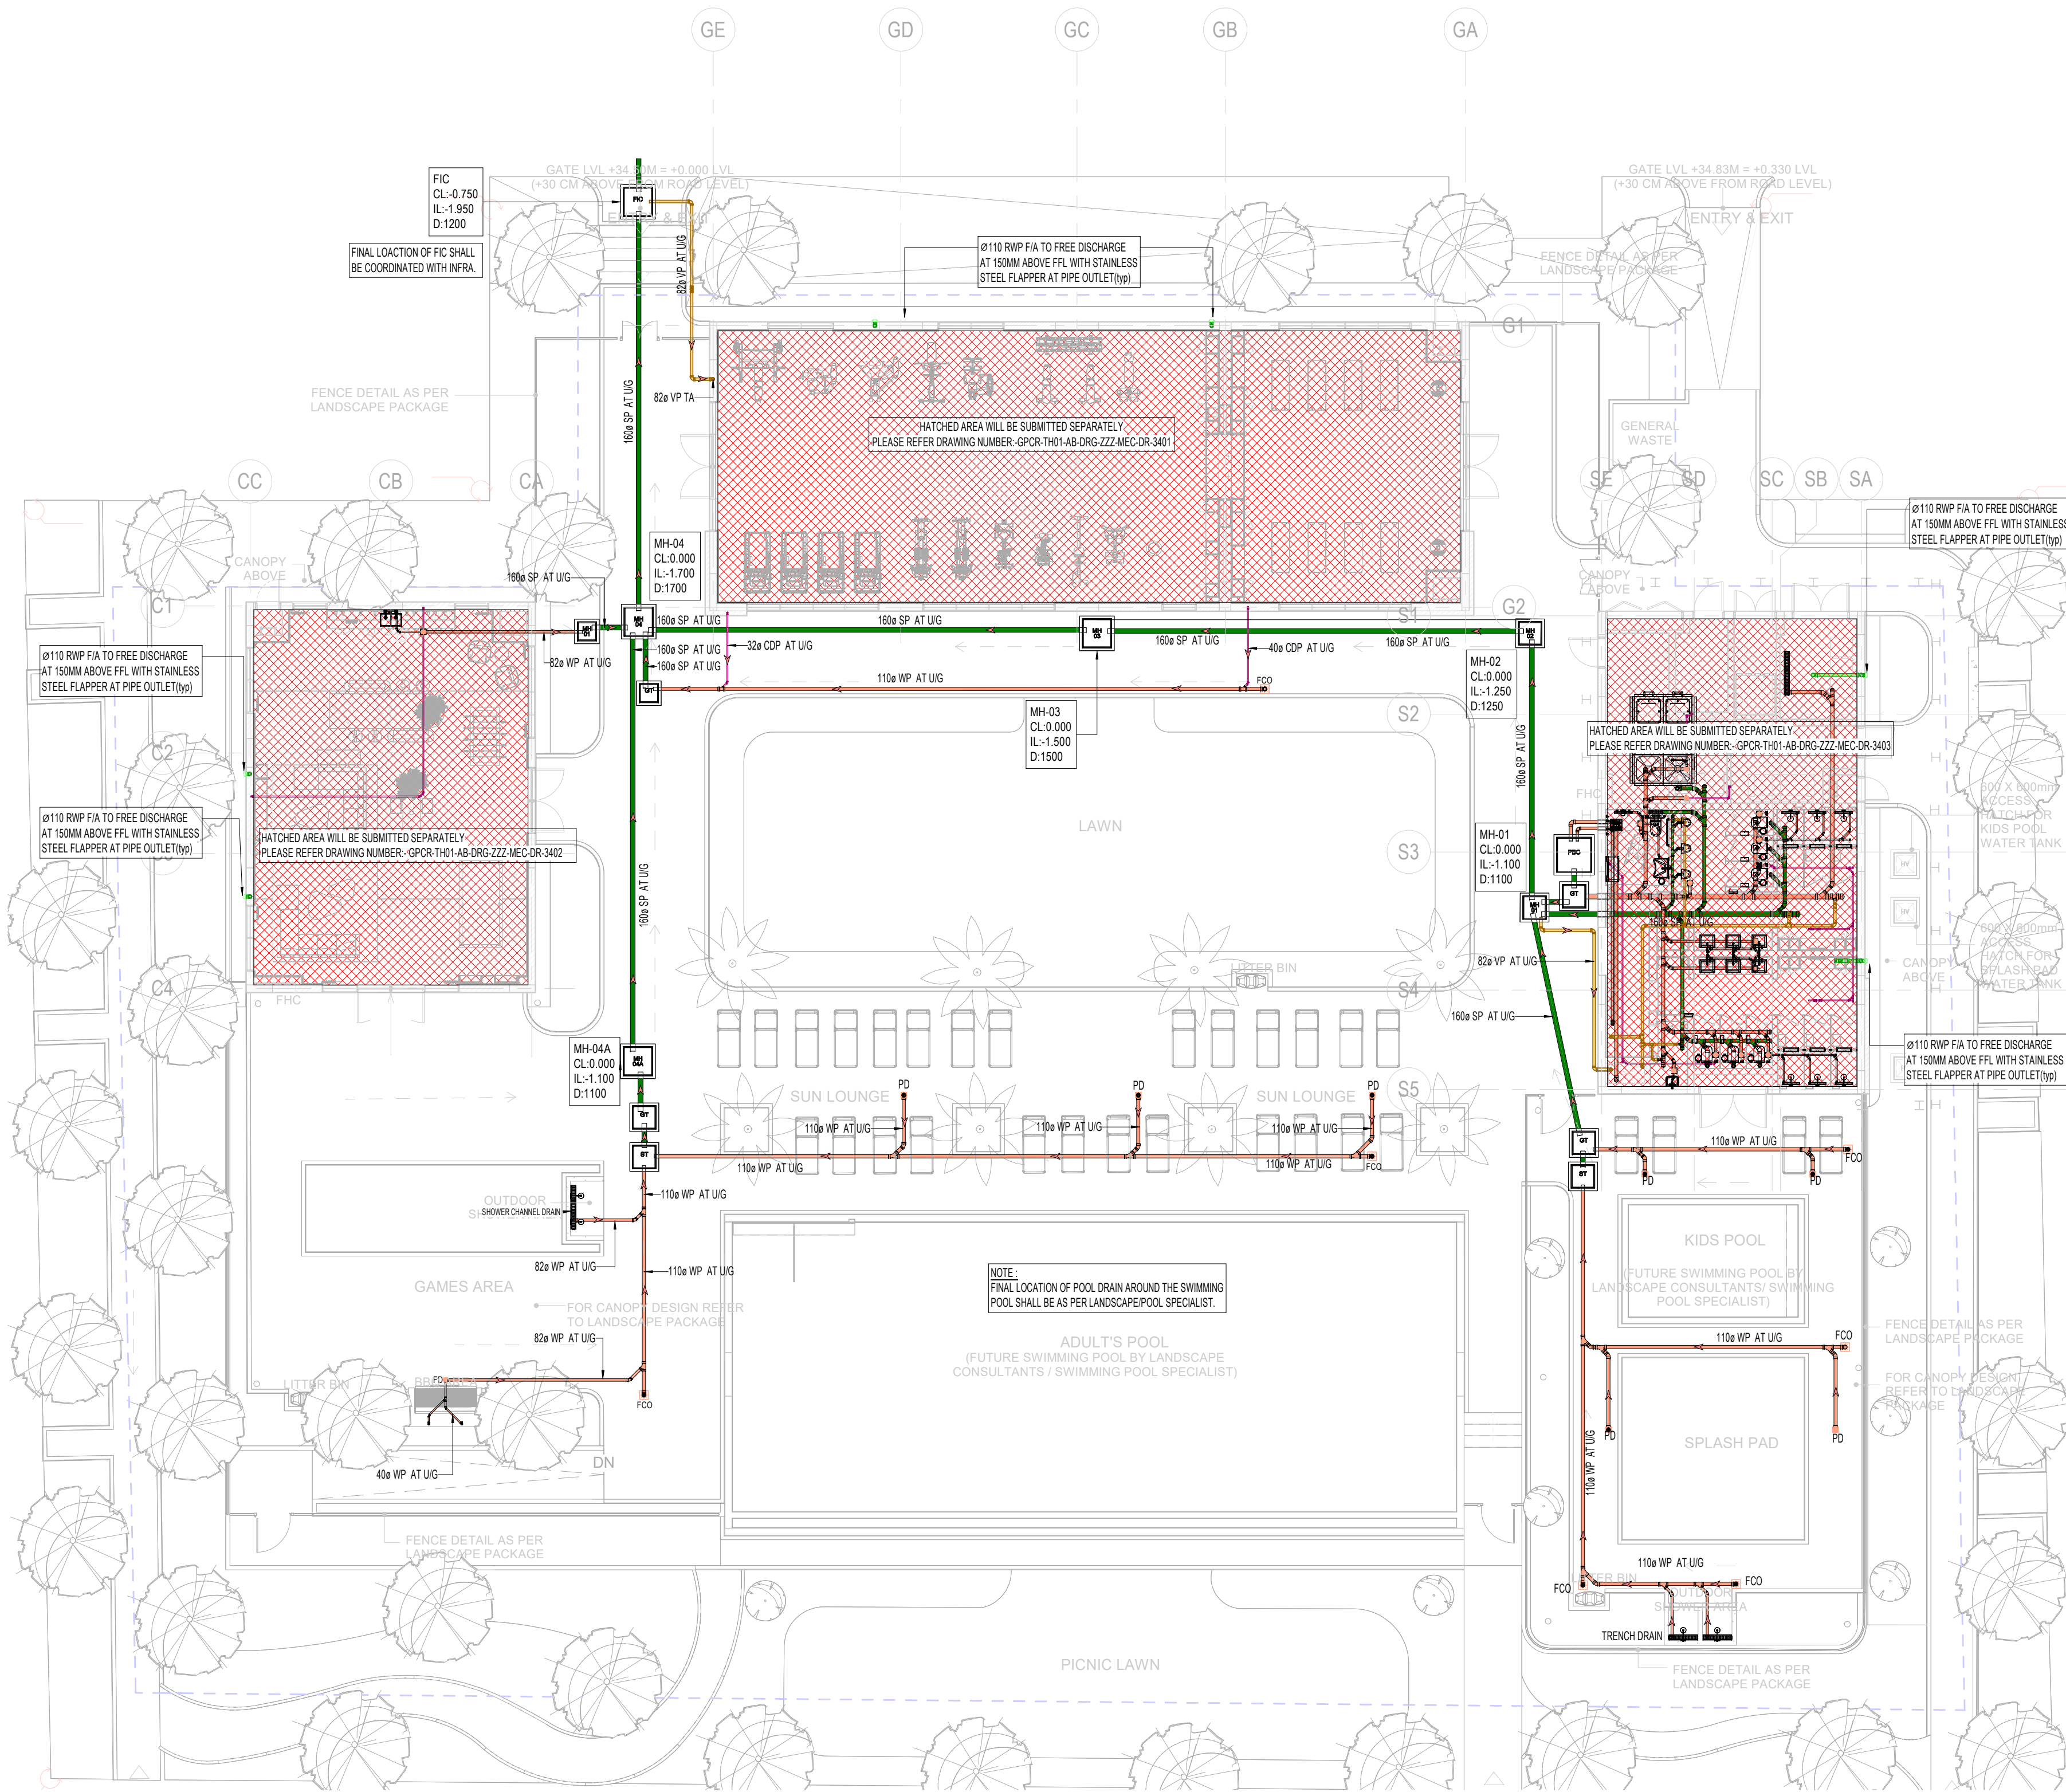


1 OVERALL GROUND FLOOR DRAINAGE LAYOUT  
1 : 150

NOTES :-  
1. ALL LEVELS,MH & DGT SHOWN IN LAYOUT ARE TENTATIVE FINAL SIZES & DEPTH TO BE COORDINATED BY CONTRACTOR AS PER SITE CONDITION.  
2. VENT PIPE CONNECTION SHALL BE PROVIDED AS PER AUTHORITY REGULATIONS.  
3. CONTRACTOR SHALL DO THE NECESSARY EXTERNAL CONNECTION TO A MA. 10m OUTSIDE THE VILLA PLOT BOUNDARY.  
4. ALL MANHOLES WITH IN THE VILLA PLOT PAVED HANDSCAPED AREAS BE RECESSED TYPE, AND LEVEL SHALL BE COORDINATED WITH THE FINISHES ON SITE AS PER ARCHITECT DRAWINGS

NOTES:-  
• ALL DIMENSIONS ARE IN MILLIMETERS UNLESS OTHERWISE SPECIFIED  
• ALL SERVICES OUTLETS ON THIS DRAWINGS ARE INDICATIVE ONLY. THE CONTRACTOR SHALL PREPARE DETAILED SHOP DRAWINGS AFTER COORDINATING PRIOR TO EXECUTION OF WORK.


| LEGEND |                             |
|--------|-----------------------------|
|        | SOIL PIPE (SP)              |
|        | WASTE PIPE (WP)             |
|        | VENT PIPE (VP)              |
|        | RAIN WATER PIPE (RWP)       |
|        | CONDENSATE DRAIN PIPE (CDP) |
|        | PALNTER DRAIN PIPE (PDP)    |
|        | PRESSURE PIPE (HPP)         |
| MH     | MANHOLE                     |
| GT     | GULLY TRAP                  |
| SD     | SHOWER DRAIN                |
| FD     | FLOOR DRAIN                 |
| CB     | CATCH BASIN                 |
| PBMH   | PRESSURE BREAKING MANHOLE   |
| ST     | SAND TRAP                   |
| PDO    | PLANTER DRAIN OUTLET        |
| RWO    | RAIN WATER OUTLET           |
| FCO    | FLOOR CLEAN OUT             |
| CO     | CLEAN OUT                   |
| F/A    | FROM ABOVE                  |
| F/B    | FROM BELOW                  |
| T/A    | TO ABOVE                    |
| T/B    | TO BELOW                    |
| HL     | HIGH LEVEL                  |
| L/L    | LOW LEVEL                   |
| DTLL   | DROP TO LOW LEVEL           |

| MANHOLE SCHEDULE |              |                 |                  |                         |            |                |
|------------------|--------------|-----------------|------------------|-------------------------|------------|----------------|
| MH REF           | MH SIZE (mm) | COVER LEVEL (m) | INVERT LEVEL (m) | DISTANCE TO NEXT MH (m) | DEPTH (mm) | COVER SIZE(mm) |
| MH-01            | 600x600      | 0.000 mm        | -1.10 m          | 9.5 m                   | 0.95 m     | 600x600        |
| MH-02            | 600x600      | 0.000 mm        | -1.25 m          | 15.0 m                  | 1.25 m     | 600x600        |
| MH-03            | 800x800      | 0.000 mm        | -1.50 m          | 15.3 m                  | 1.50 m     | 600x600        |
| MH-04A           | 800x800      | 0.000 mm        | -1.10 m          | 15.2 m                  | 1.10 m     | 600x600        |
| MH-04            | 600x600      | 0.000 mm        | -1.70 m          | 14.5 m                  | 1.70 m     | 600x600        |
| FIC              | 800x800      | -0.750 mm       | -1.950 m         |                         | 1.20 m     | 600x600        |
|                  |              |                 |                  |                         |            | VENTED         |

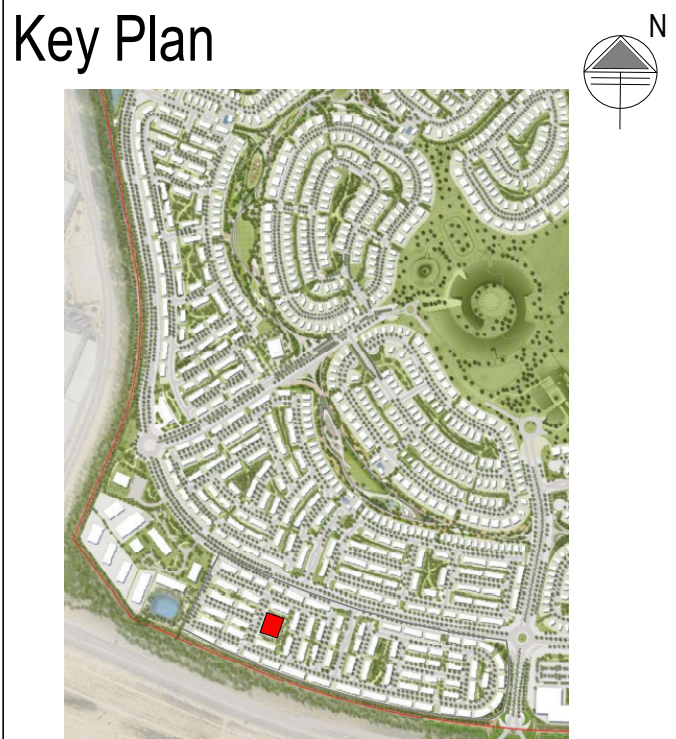

General Notes :

- Do not Scale The Drawings. Follow (The MM) Written Dimensions Unless Otherwise Mentioned.
- Each Drawing Shall be Read in Conjunction With all Other Drawings Specification & the General Standard Details. In Case of Any Discrepancies Bring it to the Knowledge of Engineer and Same to be Resolved Prior to Execution of Work.
- Dimensions Shown on These Drawings are Structural Dimensions. Unless Noted Otherwise.
- All Levels Indicated On These Drawings are Levels as per the the Survey Datum, Same Should be Verified at Site Prior to Execution of Work.
- All Levels Indicated On These Drawings are Based On Design Level, Which is Equivalent to Datum Level and Same Should be Verified at Site Prior to Execution of Work.

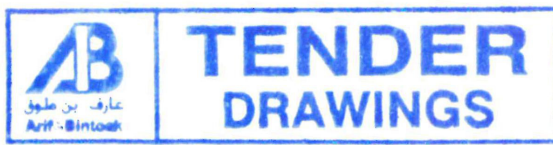

|    |            |     |                             |
|----|------------|-----|-----------------------------|
| 00 | 10/03/2026 | LSG | TENDER SUBMISSION           |
| 00 | 16/01/2026 | LSG | DETAILED DESIGN SUBMISSION  |
| 00 | 31/10/2025 | LSG | SCHEMATIC DESIGN SUBMISSION |
| 00 | 15/10/2025 | LSG | SCHEMATIC SUBMISSION-50%    |
| 00 | 01/09/2025 | LSG | CONCEPT DESIGN SUBMISSION   |

REVISIONS / ISSUE

THIS DRAWING MUST NOT BE REPRODUCED IN WHOLE OR IN PART WITHOUT THE PRIOR APPROVAL OF ARIF & BINTOAK

TENDER SUBMISSION

Client



Lead Consultant



Project Title:  
Proposed Residential Townhouses and Standalone Villas  
TH-01, TH-02, and TH-03 at Grand Polo Club & Resort, Dubai, UAE

Discipline : MECHANICAL

OVERALL GROUND FLOOR COMMUNITY CENTER DRAINAGE LAYOUT

|                        |                      |                       |
|------------------------|----------------------|-----------------------|
| Architectural Engineer | Electrical Engineer  | Structural Engineer   |
| MUSTAFA ABID           | MARWAN MOHD.         | RIHAM RAMADAN         |
| Registration # 5847    | Registration # 80102 | Registration # 105892 |
| Scale(s): As indicated | Date: 10/03/2026     | Project no: 1857      |
| Drawn by: LSG          | Checked: MAV         | Approved: MRM         |

Drawing Number : GPCR-TH01-AB-DRG-ZZZ-MEC-DR-3400-00