




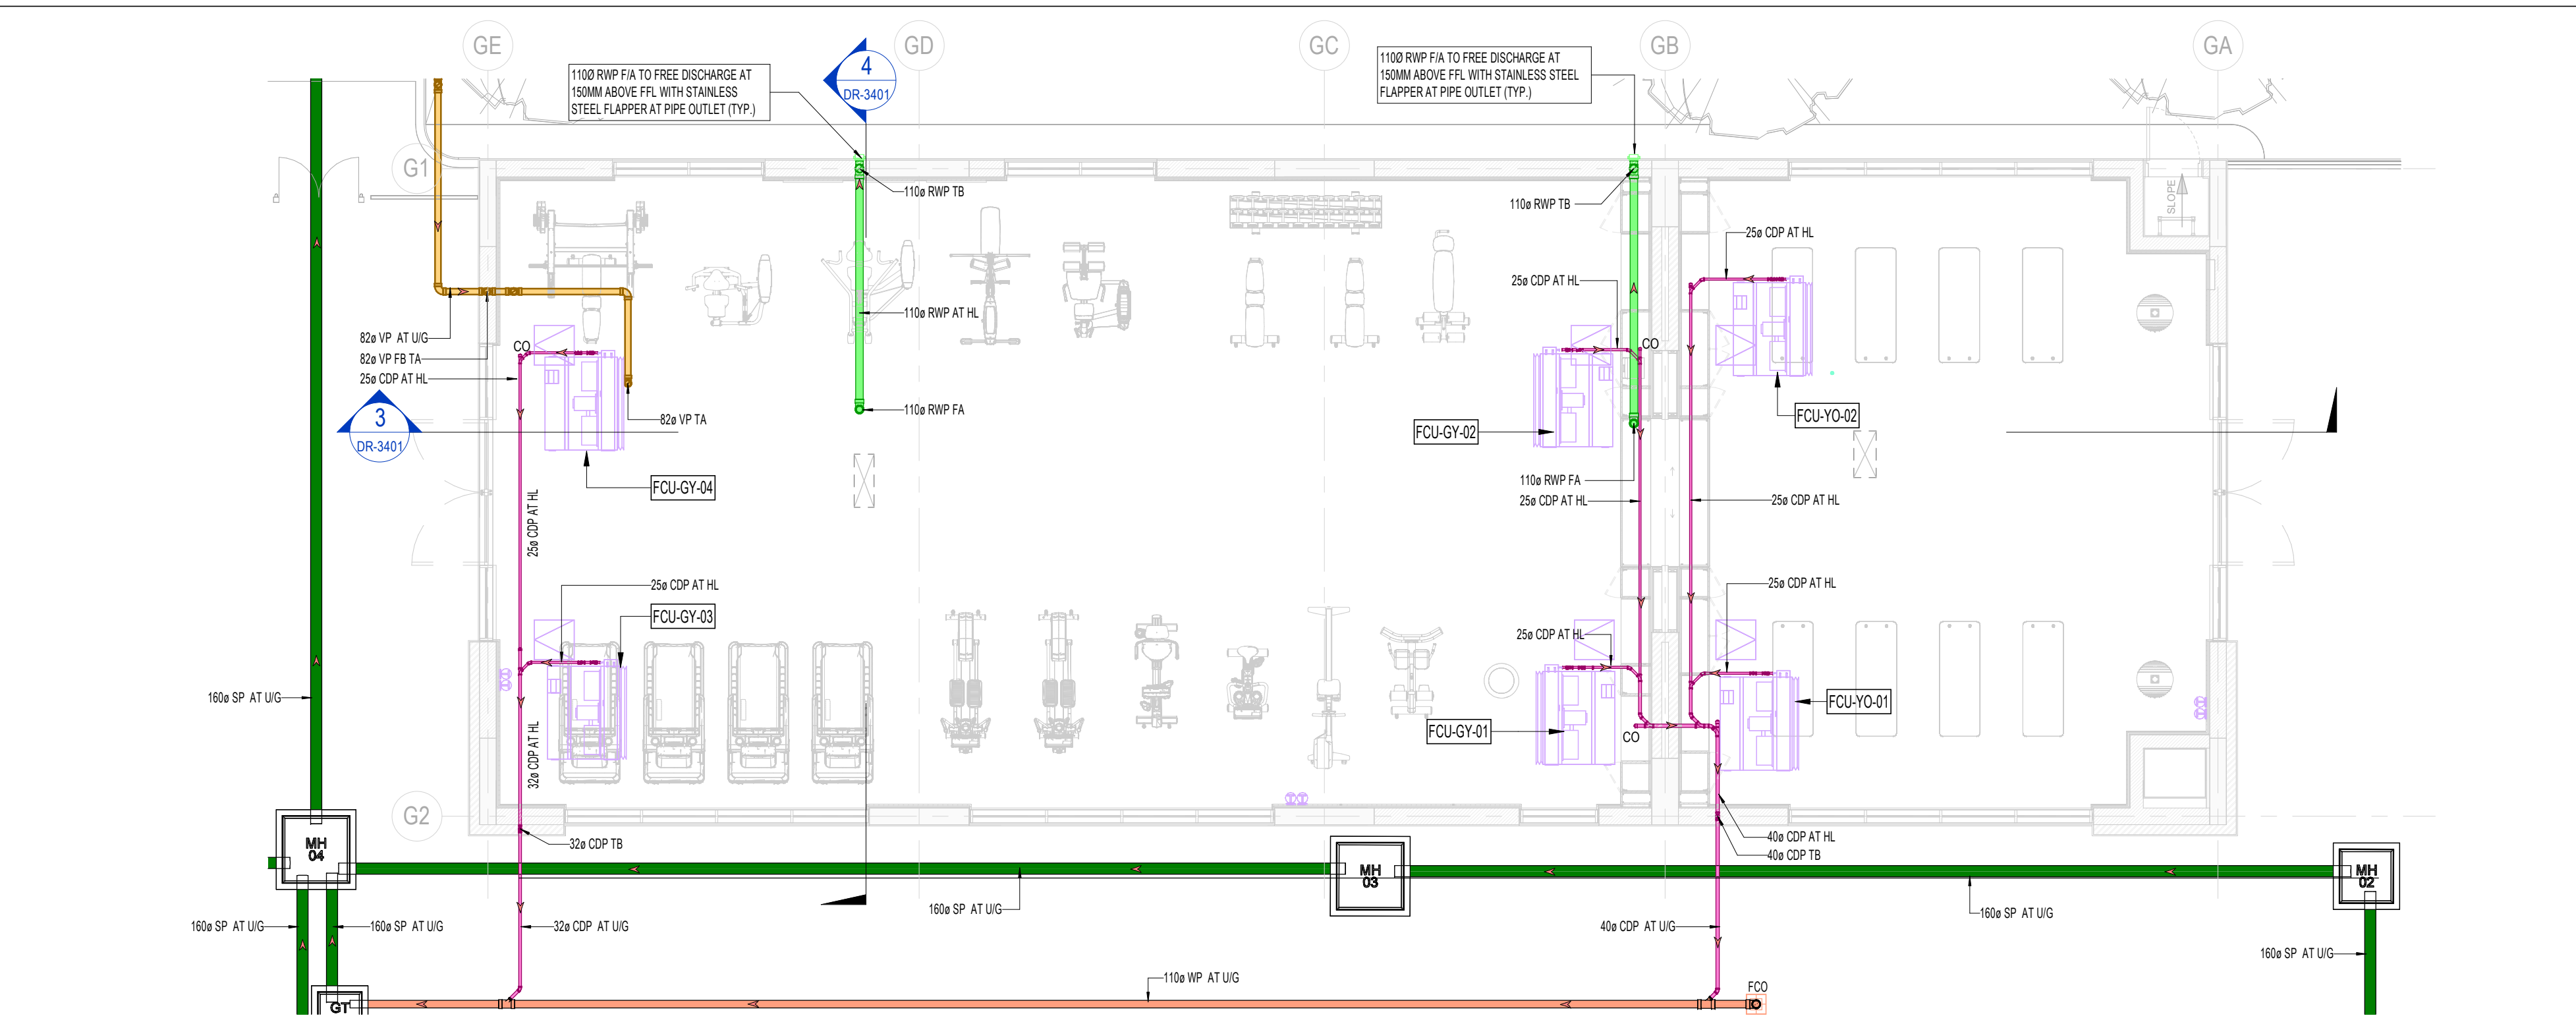


1 GROUND FLOOR DRAINAGE LAYOUT-GYM&YOGA
1 : 75

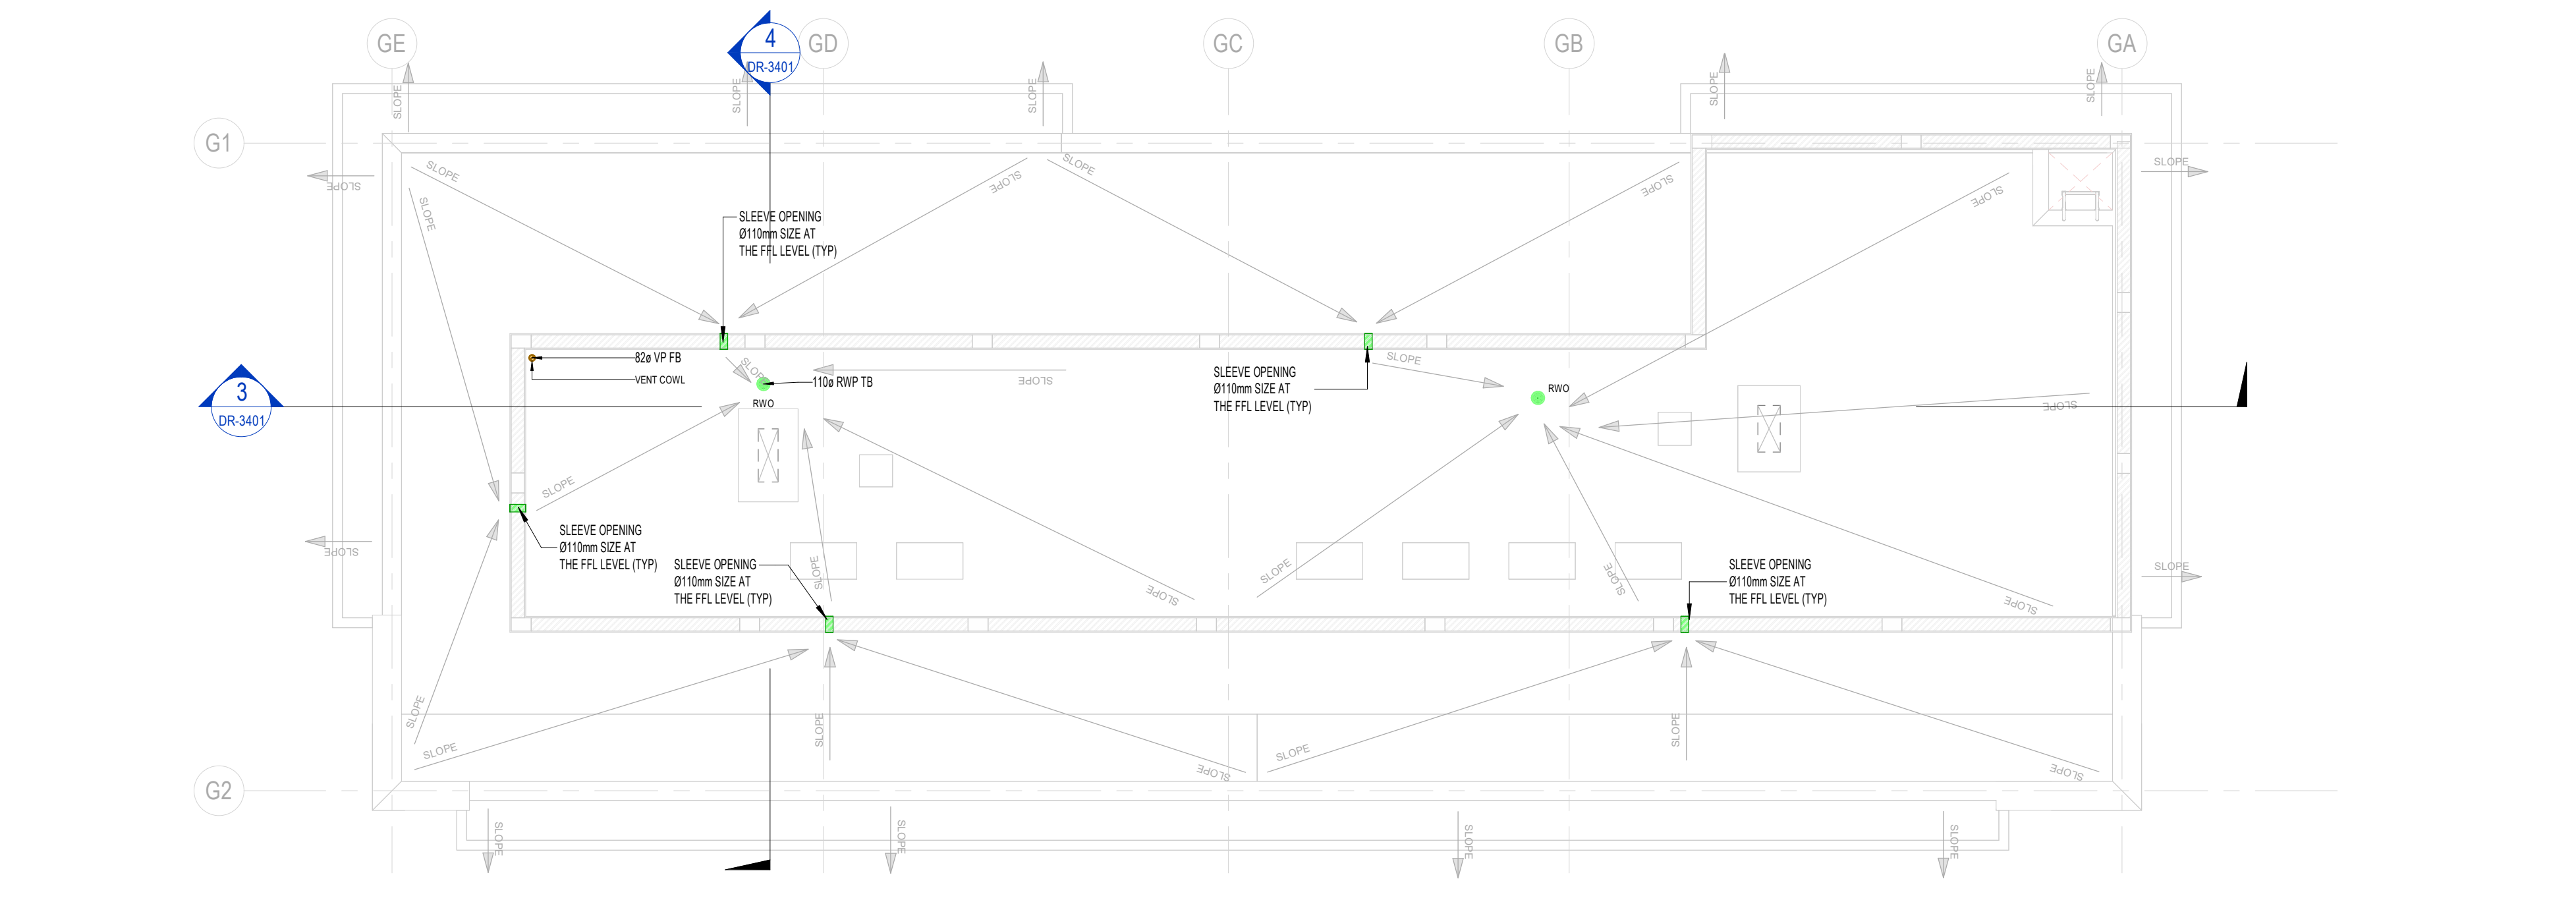

2 ROOF FLOOR DRAINAGE LAYOUT-GYM&YOGA
1 : 75

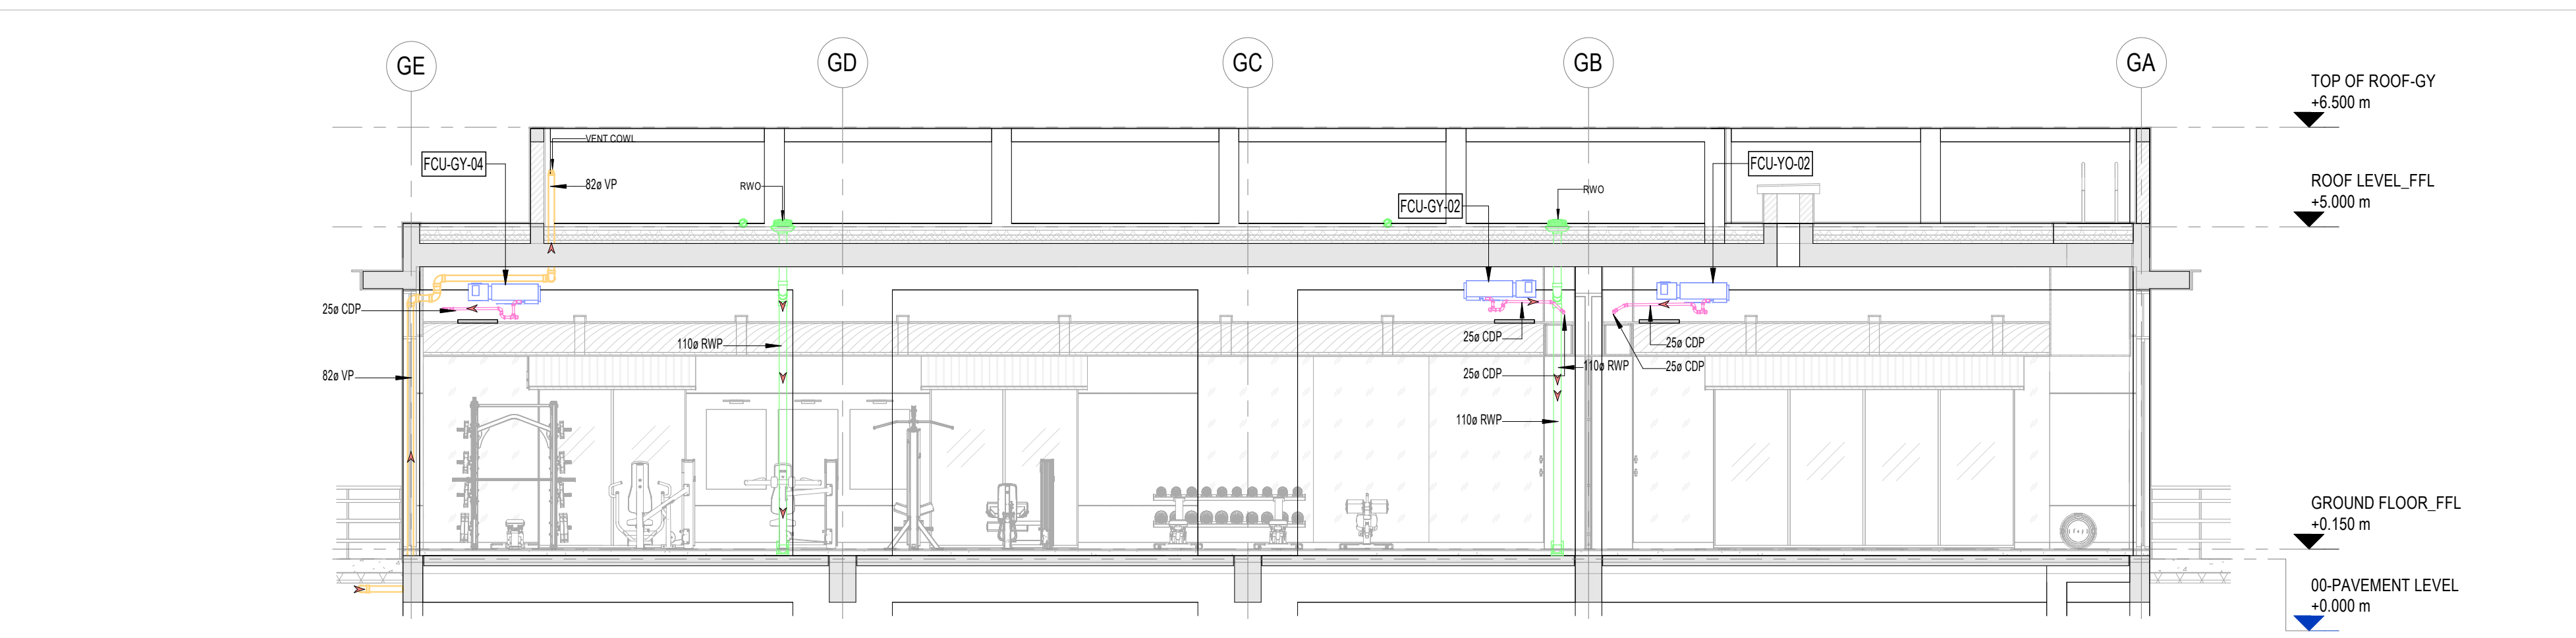

3 GYM&YOGA DRAINAGE SECTION 01
1 : 75

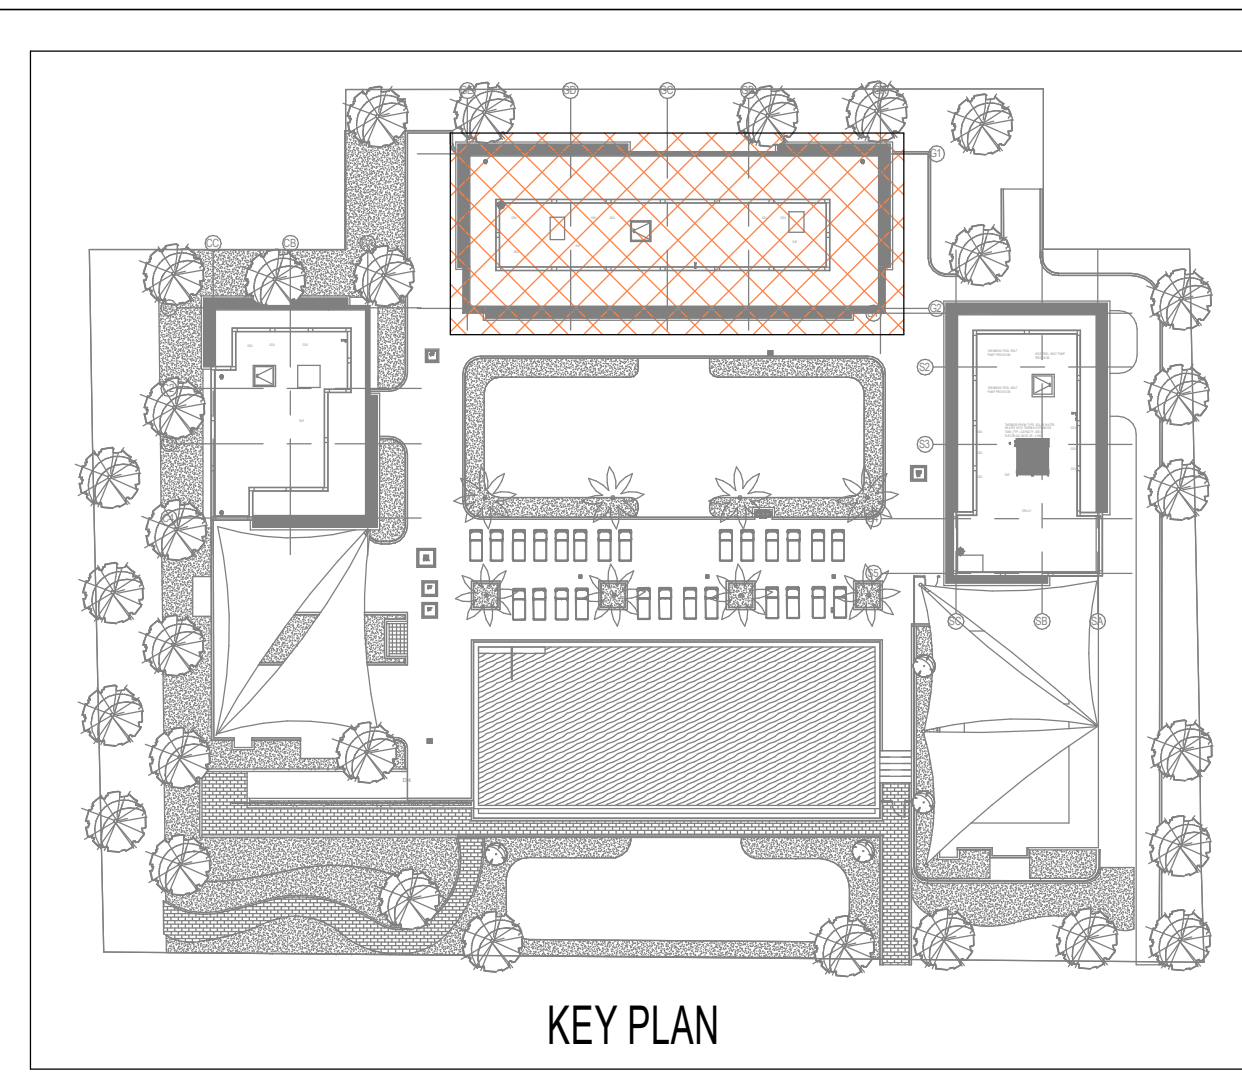

KEY PLAN


NOTES :-
1. ALL LEVELS MH & DGT SHOWN IN LAYOUT ARE TENTATIVE FINAL SIZES & DEPTH TO BE COORDINATED BY CONTRACTOR AS PER SITE CONDITION.
2. VENT PIPE CONNECTION SHALL BE PROVIDED AS PER AUTHORITY REGULATIONS.
3. CONTRACTOR SHALL DO THE NECESSARY EXTERNAL CONNECTION TO A MA. 10m OUTSIDE THE VILLA PLOT BOUNDARY.
4. ALL MANHOLES WITH IN THE VILLA PLOT PAVED HANDSCAPED AREAS BE RECESSED TYPE, AND LEVEL SHALL BE COORDINATED WITH THE FINISHES ON SITE AS PER ARCHITECT DRAWINGS

NOTES:-


- ALL DIMENSIONS ARE IN MILLIMETERS UNLESS OTHERWISE SPECIFIED
- ALL SERVICES OUTLETS ON THIS DRAWINGS ARE INDICATIVE ONLY. THE CONTRACTOR SHALL PREPARE DETAILED SHOP DRAWINGS AFTER COORDINATING PRIOR TO EXECUTION OF WORK.

LEGEND

SOIL PIPE (SP)	WASTE PIPE (WP)	VENT PIPE (VP)	RAIN WATER PIPE (RWP)	CONDENSATE DRAIN PIPE (CDP)	PALNTER DRAIN PIPE (PDP)	PRESSURE PIPE (HPP)											
MH	GT	SD	FD	CB	PBMH	ST	PDO	RWO	FCO	CO	F/A	F/B	T/A	T/B	H/L	L/L	DTLL
MANHOLE	GULLY TRAP	SHOWER DRAIN	FLOOR DRAIN	CATCH BASIN	PRESSURE BREAKING MANHOLE	SAND TRAP	PLANTER DRAIN OUTLET	RAIN WATER OUTLET	FLOOR CLEAN OUT	CLEAN OUT	FROM ABOVE	FROM BELOW	TO ABOVE	TO BELOW	HIGH LEVEL	LOW LEVEL	DROP TO LOW LEVEL

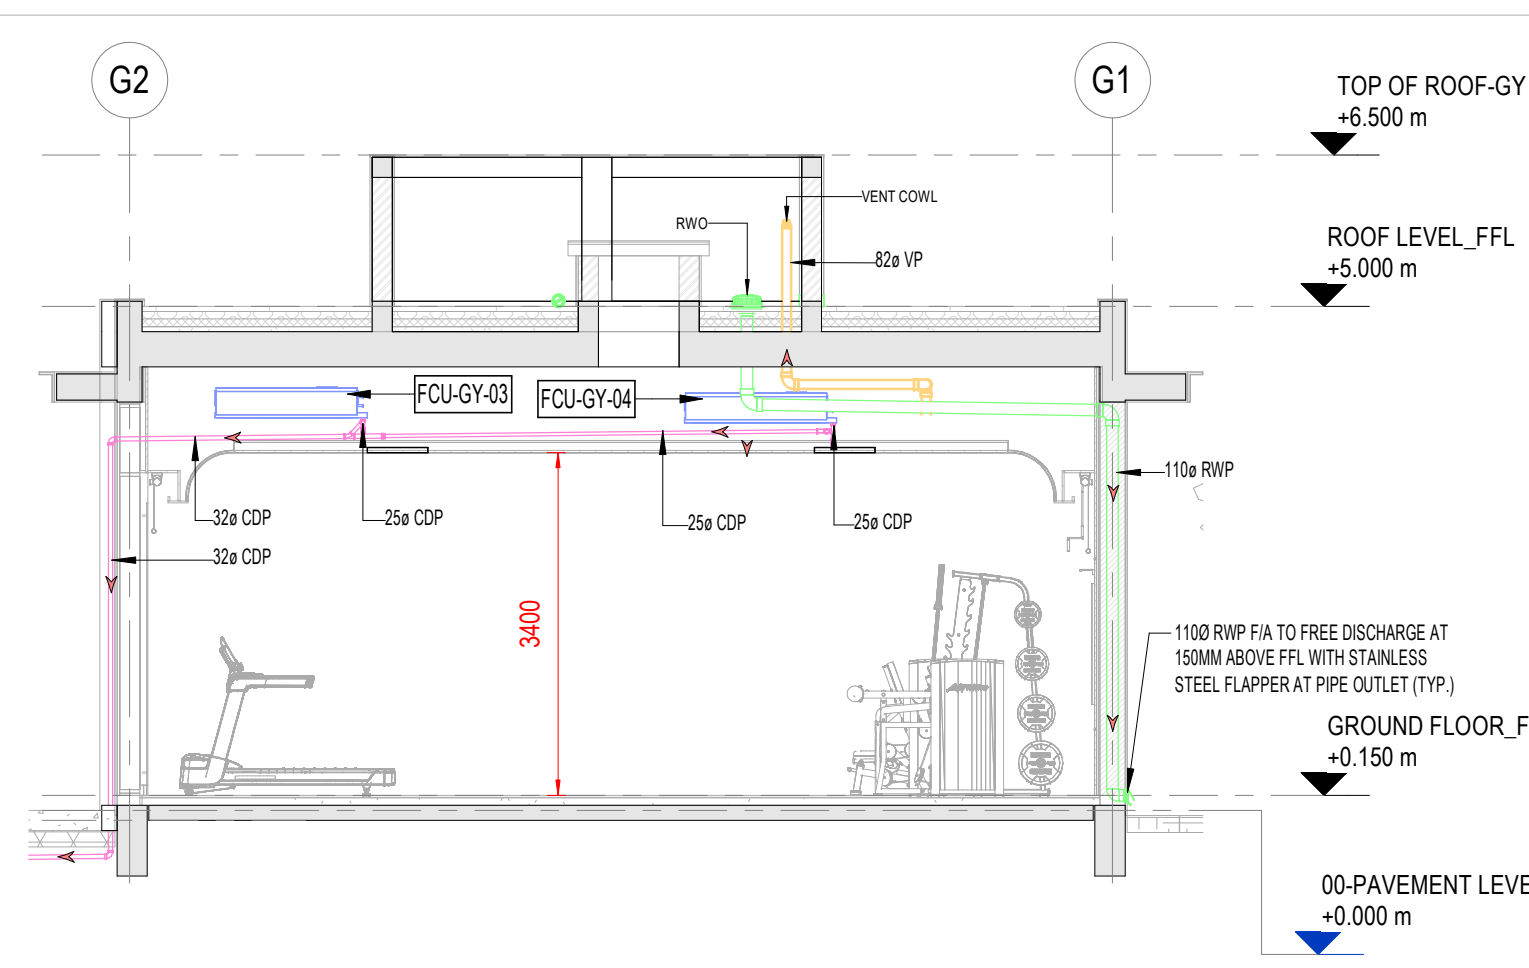

4 GYM&YOGA DRAINAGE SECTION 02
1 : 75

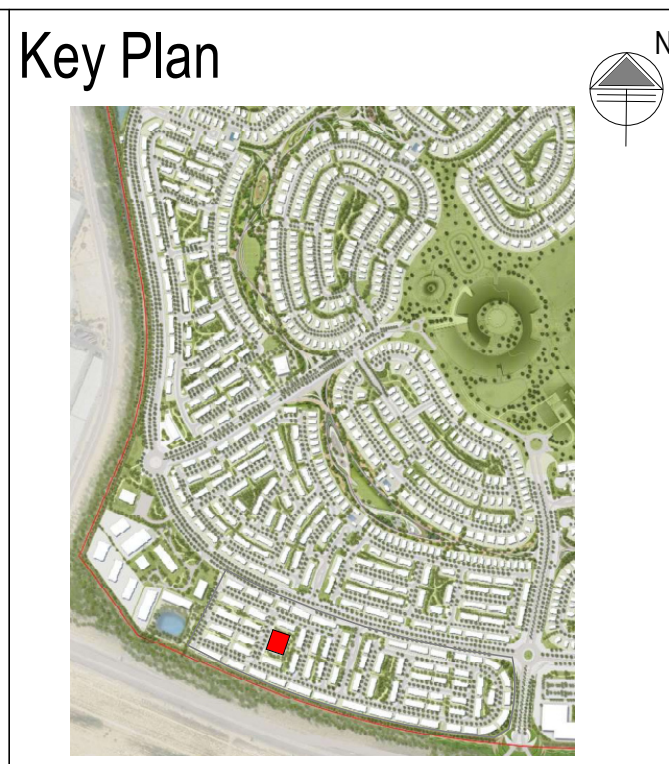

Key Plan

General Notes :

- Do not Scale The Drawings. Follow (The MM) Written Dimensions Unless Otherwise Mentioned.
- Each Drawing Shall be Read in Conjunction With all Other Drawings Specification & the General Standard Details. In Case of Any Discrepancies Bring it to the Knowledge of Engineer and Same to be Resolved Prior to Execution of Work.
- Dimensions Shown on These Drawings are Structural Dimensions. Unless Noted Otherwise.
- All Levels Indicated On These Drawings are Levels as per the Survey Datum, Same Should be Verified at Site Prior to Execution of Work.
- All Levels Indicated On These Drawings are Based On Design Level, Which is Equivalent to Datum Level and Same Should be Verified at Site Prior to Execution of Work.

TENDER DRAWINGS

00	10/03/2026	LSG	TENDER SUBMISSION
00	16/01/2026	LSG	DETAILED DESIGN SUBMISSION
00	31/10/2025	LSG	SCHEMATIC DESIGN SUBMISSION
00	15/10/2025	LSG	SCHEMATIC SUBMISSION-50%
00	01/09/2025	LSG	CONCEPT DESIGN SUBMISSION

REVISIONS / ISSUE

THIS DRAWING MUST NOT BE REPRODUCED IN WHOLE OR IN PART WITHOUT THE PRIOR APPROVAL OF ARIF & BINTOAK

Status

TENDER SUBMISSION

Client

EMAAR

Lead Consultant

Arif & BintOak
consulting architects & engineers

Project Title: Proposed Residential Townhouses and Standalone Villas TH-01, TH-02, and TH-03 at Grand Polo Club & Resort, Dubai, UAE

Discipline: MECHANICAL

Drawing title: GYM & YOGA GROUND & ROOF FLOOR DRAINAGE LAYOUT

Architectural Engineer	Electrical Engineer	Structural Engineer
MUSTAFA ABID	MARWAN MOHD.	RIHAM RAMADAN
Registration # 5847	Registration # 80102	Registration # 105892
Scale(s): As indicated	Date: 10/03/2026	Project no: 1857
Drawn by: LSG	Checked: MAV	Approved: MRM

Drawing Number: GPCR-TH01-AB-DRG-ZZZ-MEC-DR-3401-00