




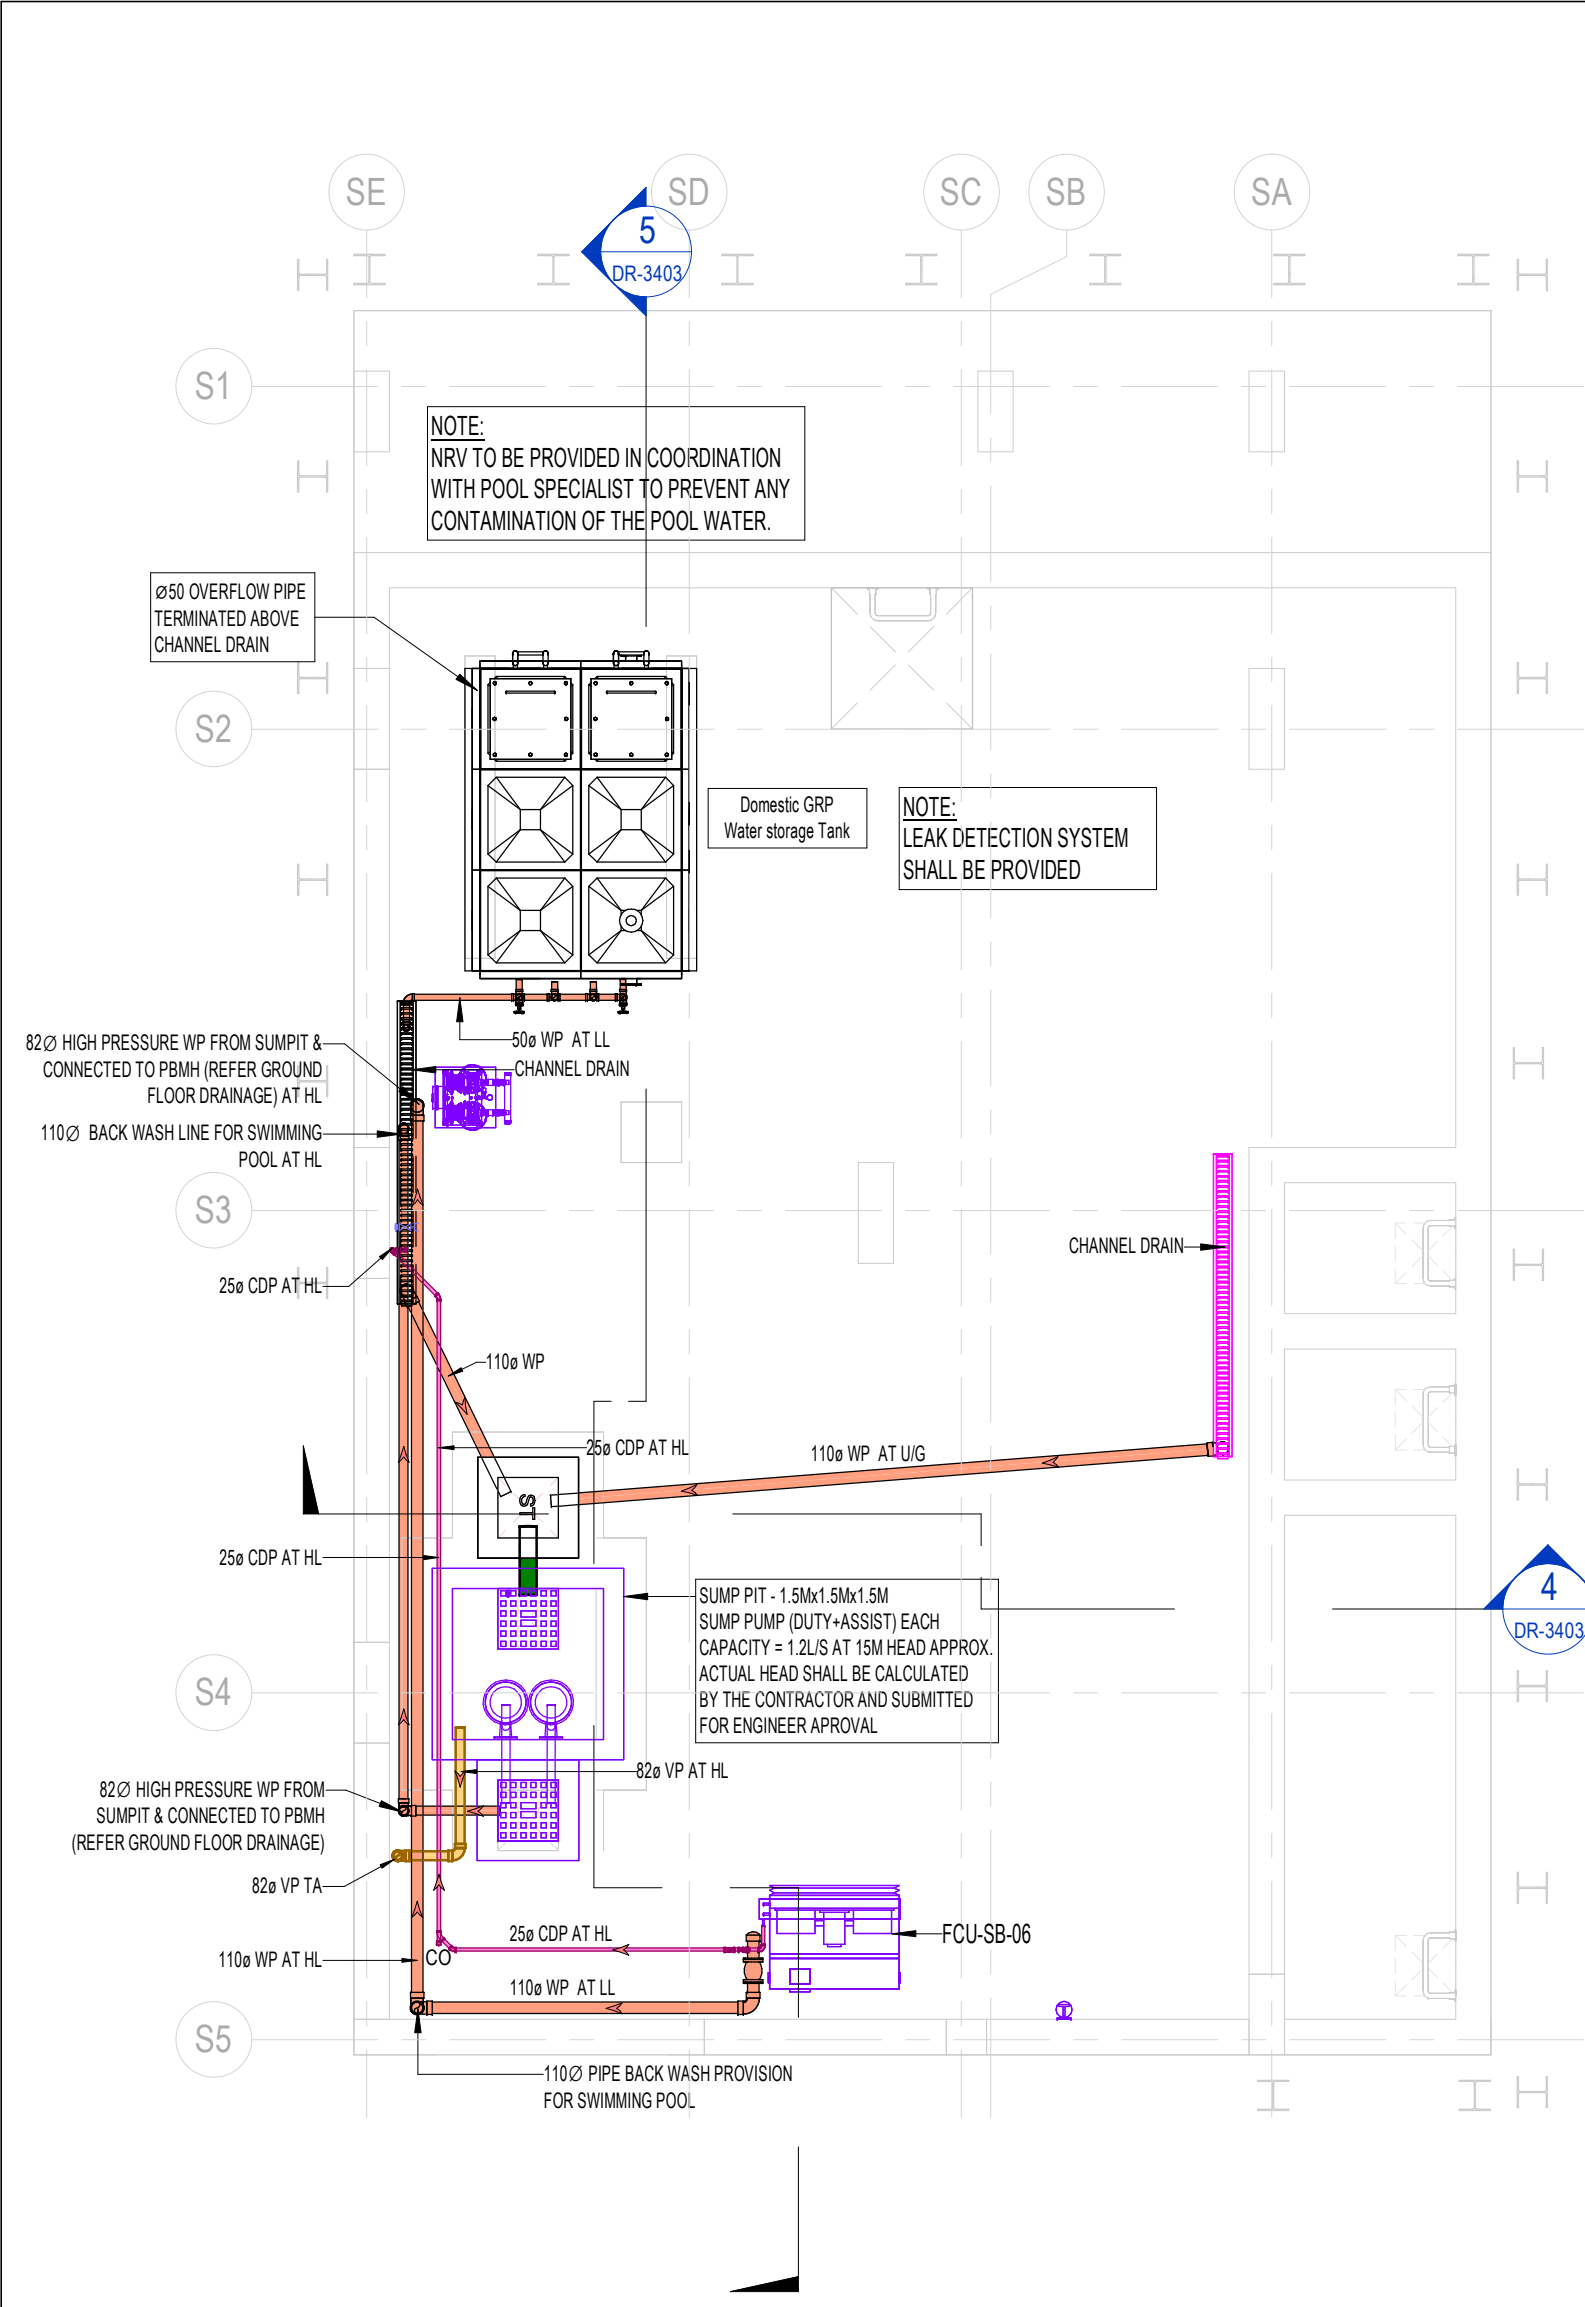


1 BASEMENT FLOOR DRAINAGE LAYOUT SERVICE BLOCK
1 : 75

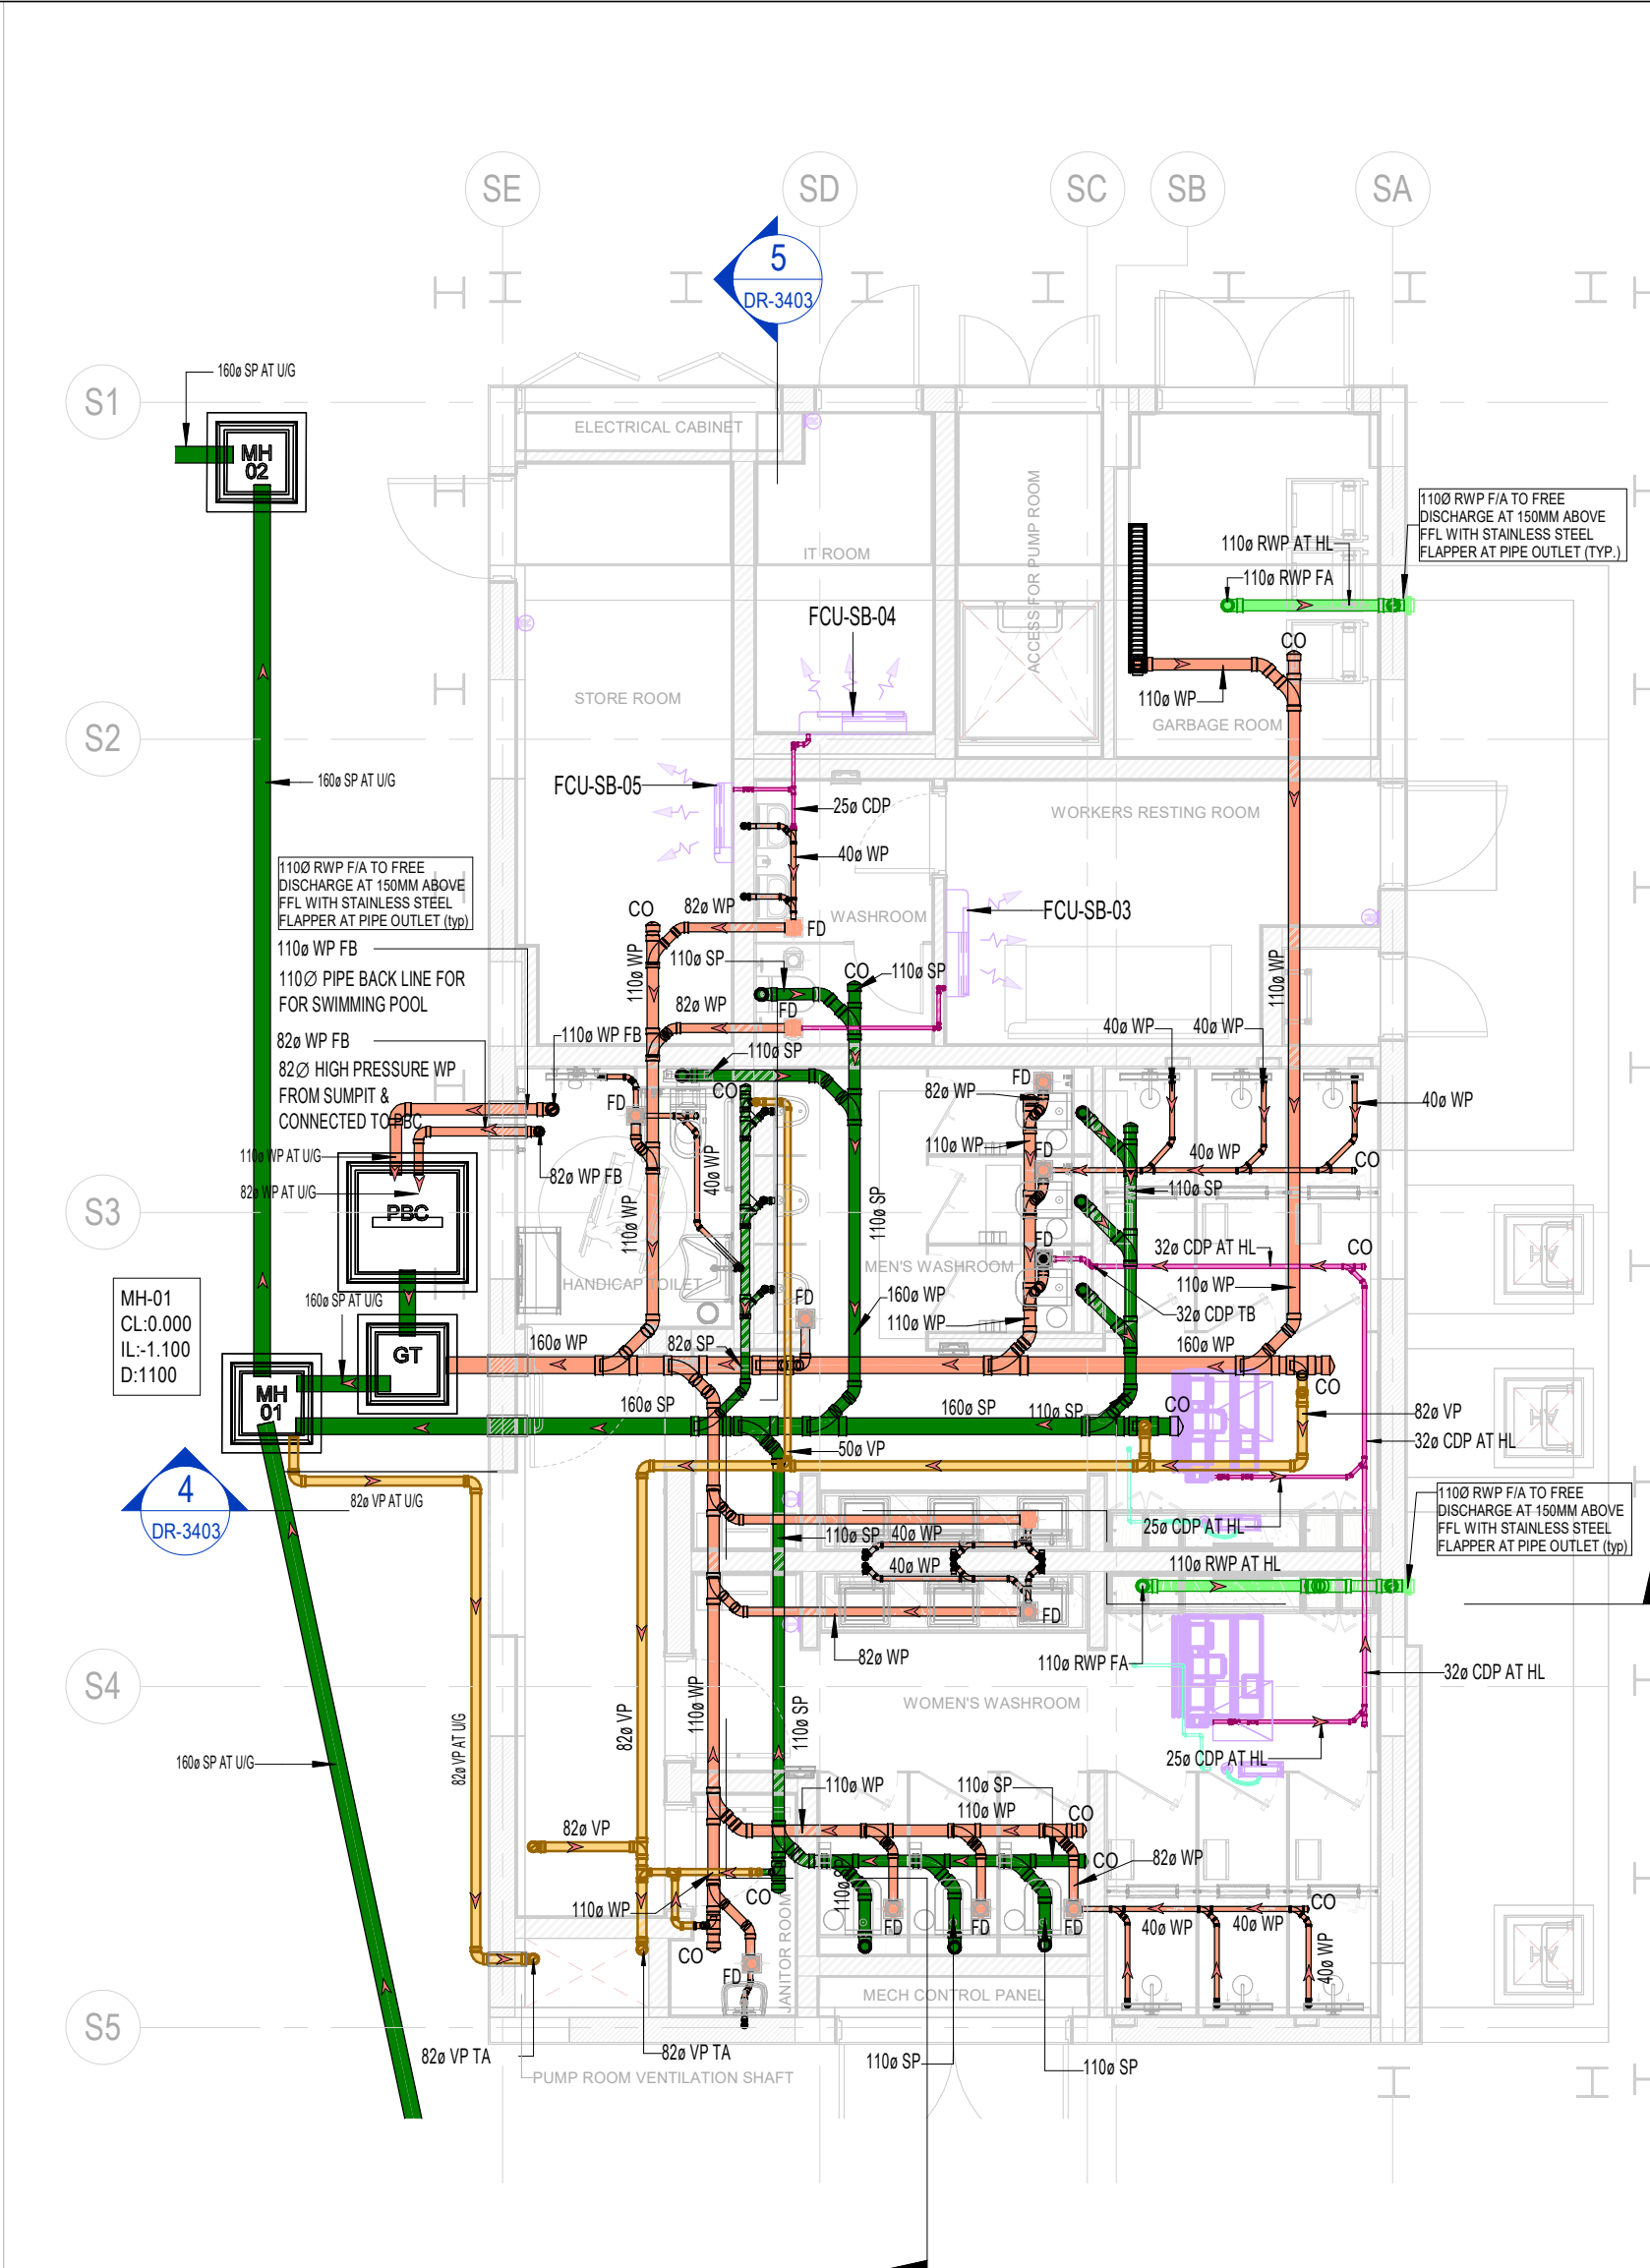

2 GROUND FLOOR DRAINAGE LAYOUT SERVICE BLOCK
1 : 75

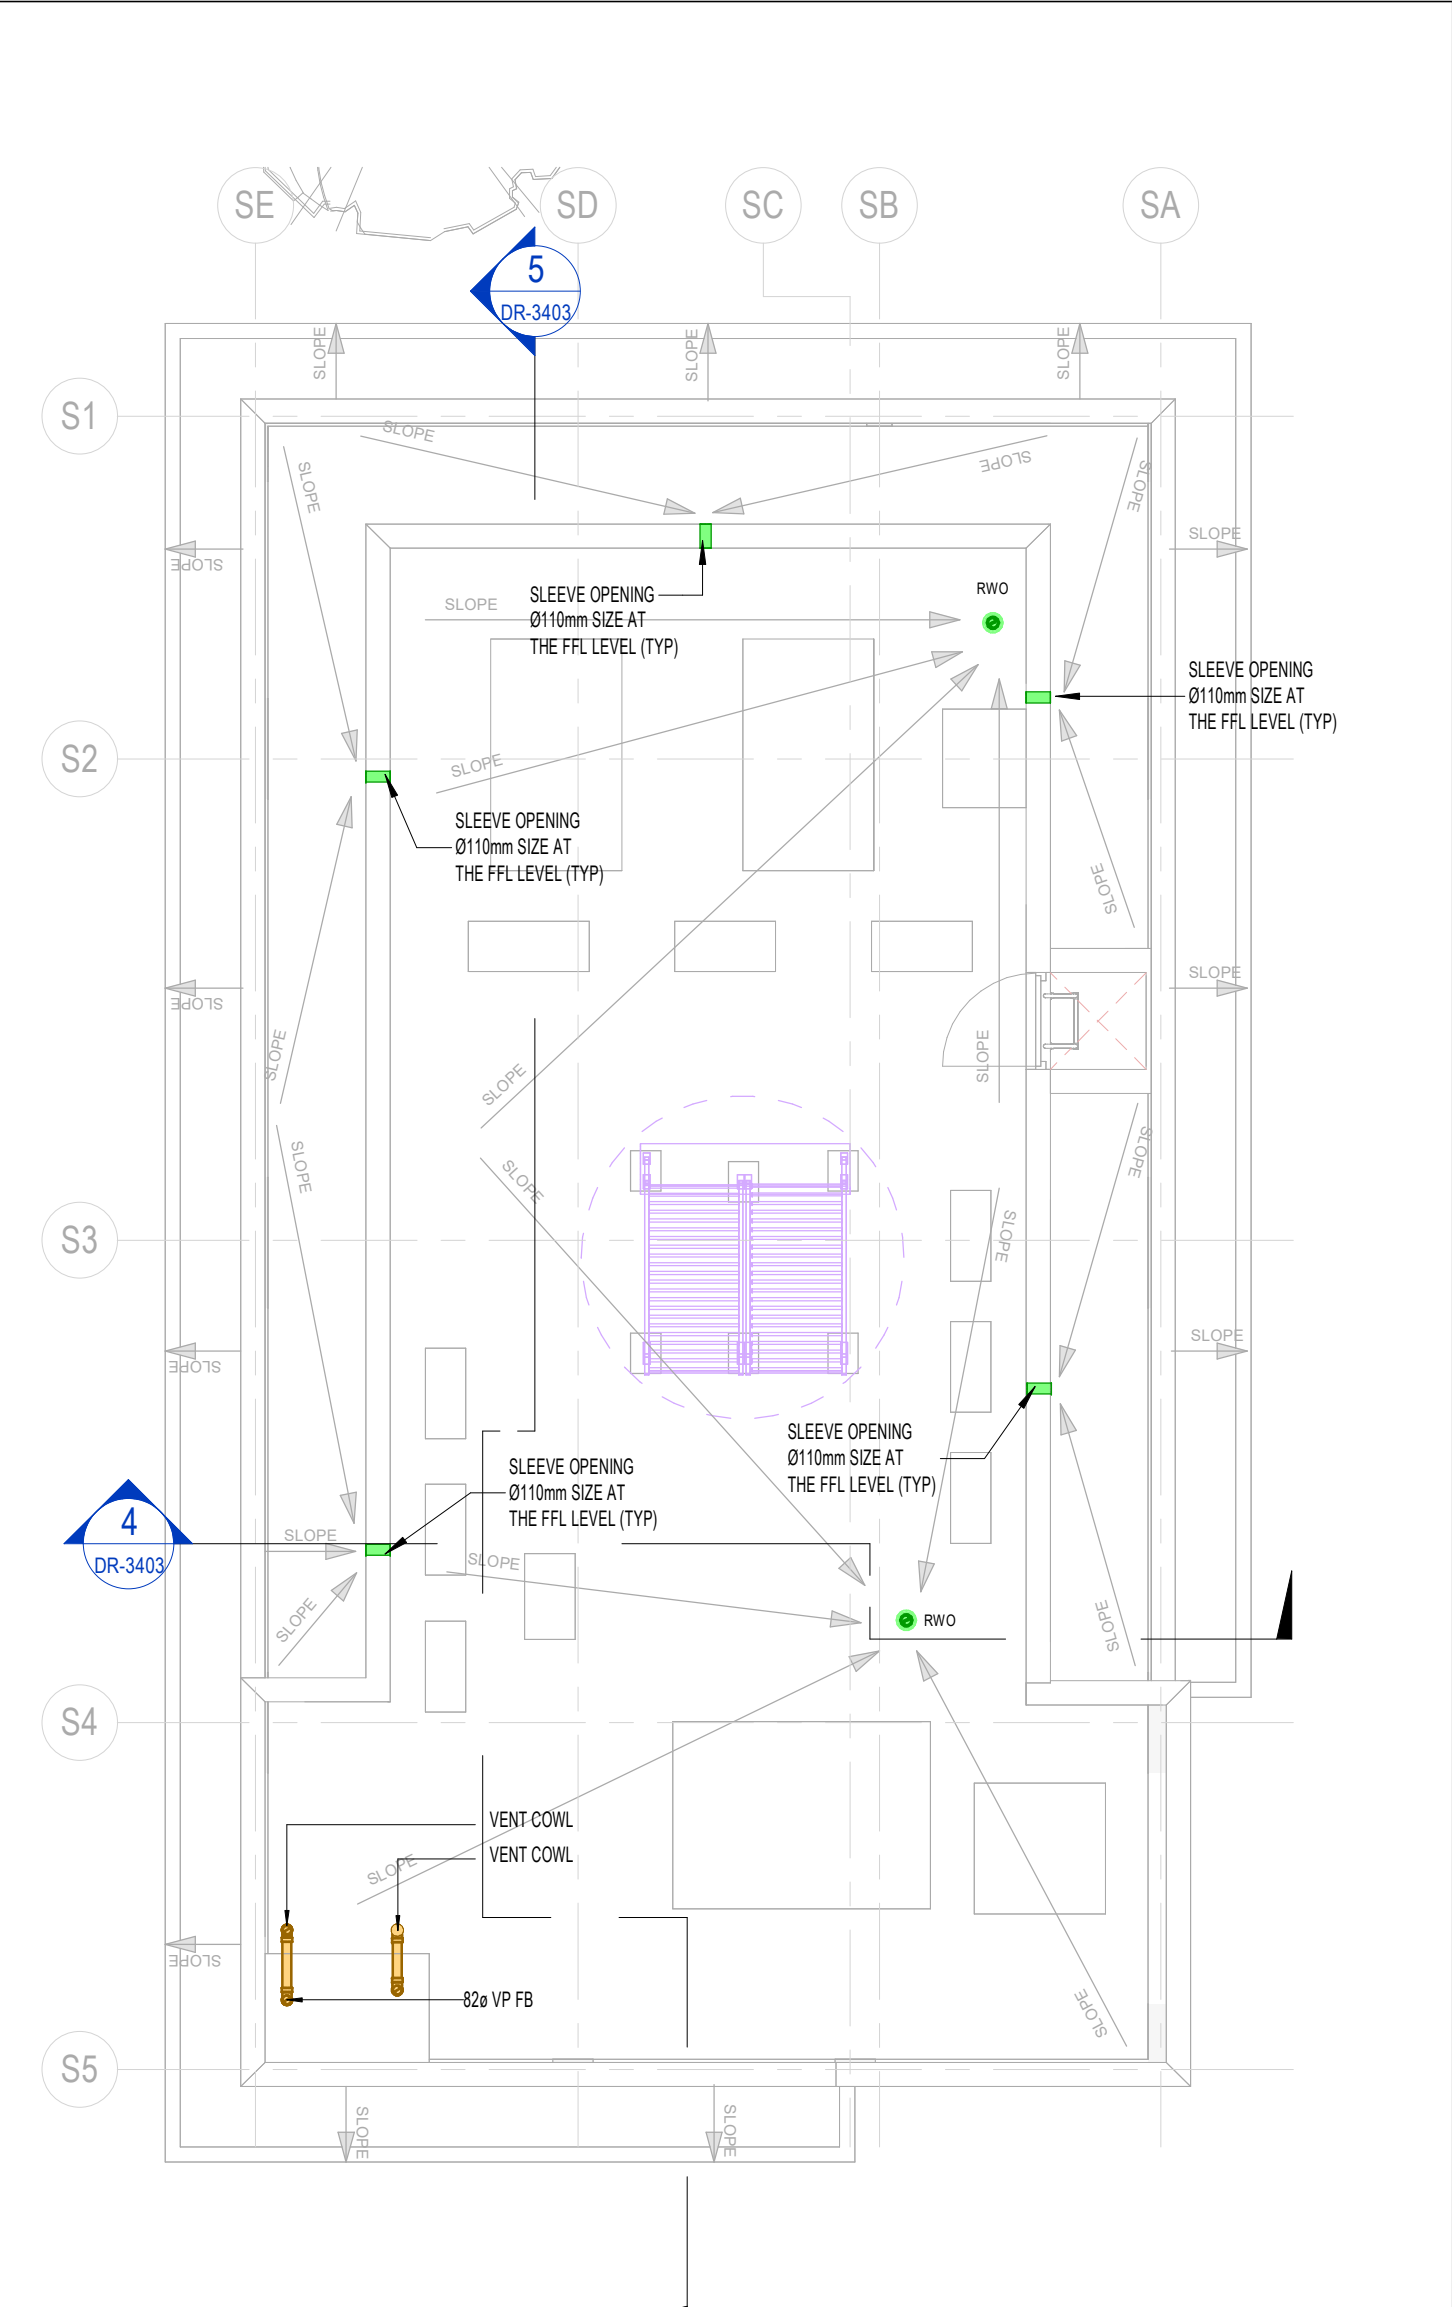


3 ROOF FLOOR DRAINAGE LAYOUT SERVICE BLOCK
1 : 75

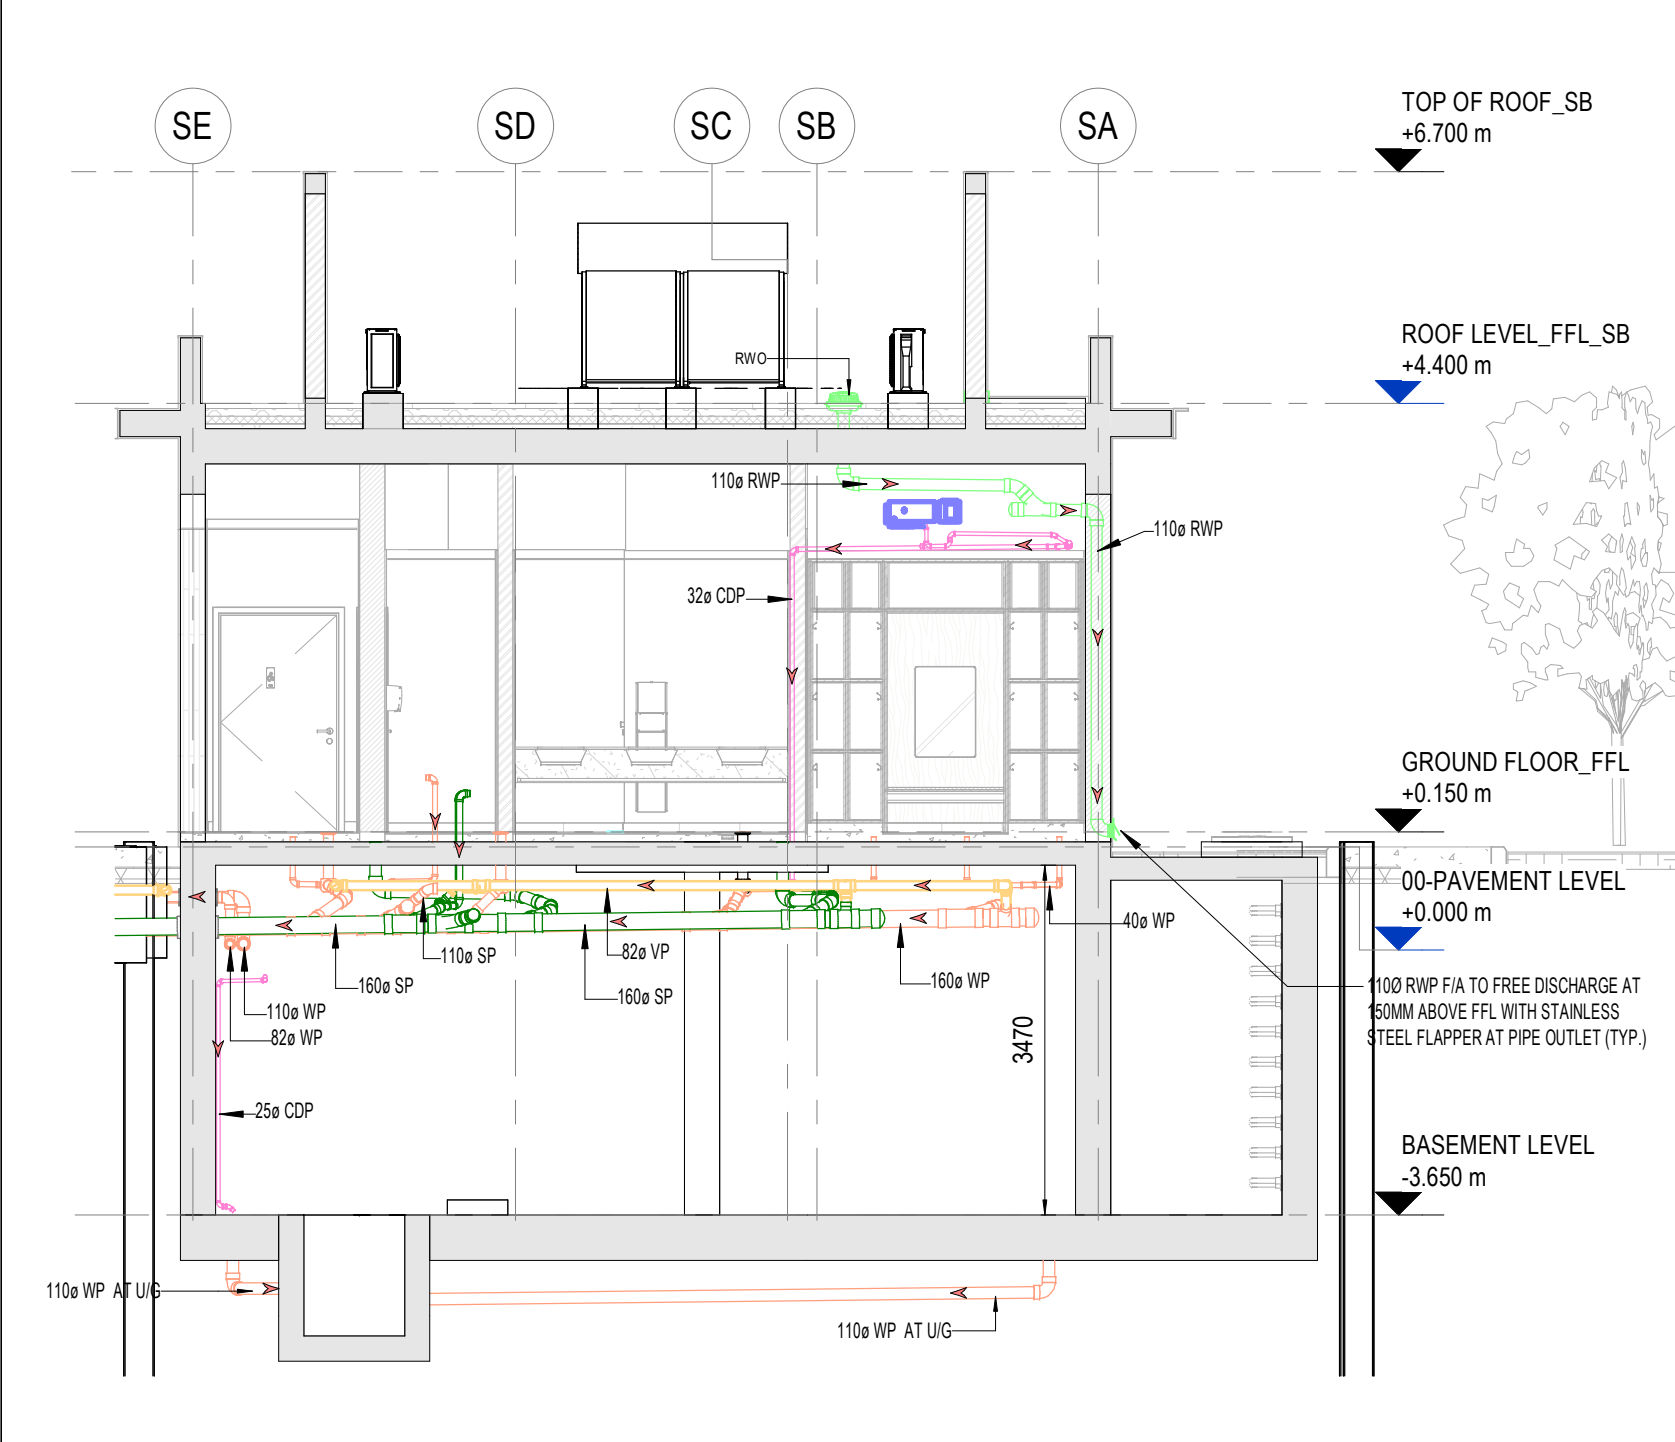

4 SERVICE BLOCK DRAINAGE SECTION 01
1 : 75




5 SERVICE BLOCK DRAINAGE SECTION 02
1 : 75

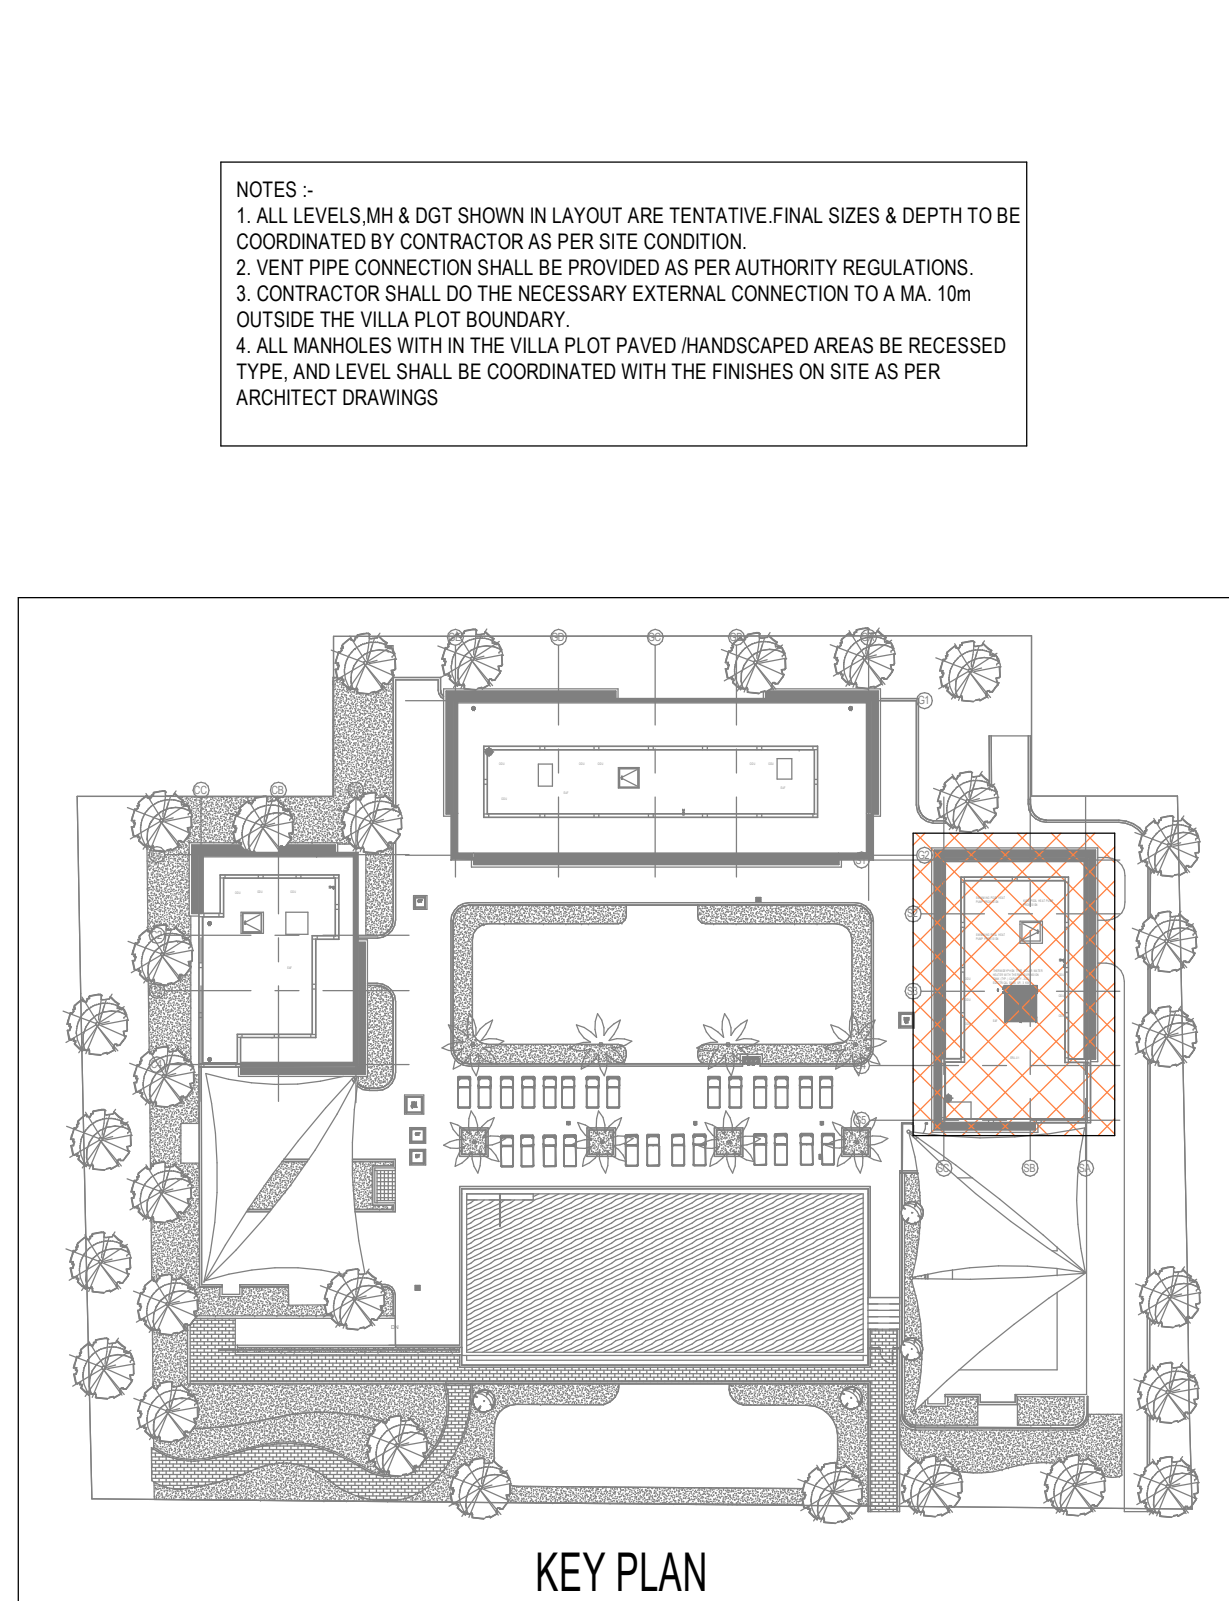

KEY PLAN

- NOTES:-
- ALL DIMENSIONS ARE IN MILLIMETERS UNLESS OTHERWISE SPECIFIED
 - ALL SERVICES OUTLETS ON THIS DRAWINGS ARE INDICATIVE ONLY. THE CONTRACTOR SHALL PREPARE DETAILED SHOP DRAWINGS AFTER COORDINATING PRIOR TO EXECUTION OF WORK.
- LEGEND
- | | |
|-----------------------------|-----------------------------|
| SOIL PIPE (SP) | SOIL PIPE (SP) |
| WASTE PIPE (WP) | WASTE PIPE (WP) |
| VENT PIPE (VP) | VENT PIPE (VP) |
| RAIN WATER PIPE (RWP) | RAIN WATER PIPE (RWP) |
| CONDENSATE DRAIN PIPE (CDP) | CONDENSATE DRAIN PIPE (CDP) |
| PALINTER DRAIN PIPE (PDP) | PALINTER DRAIN PIPE (PDP) |
| PRESSURE PIPE (HPP) | PRESSURE PIPE (HPP) |
| MH | MANHOLE |
| GT | GULLY TRAP |
| SD | SHOWER DRAIN |
| FD | FLOOR DRAIN |
| CB | CATCH BASIN |
| PBMH | PRESSURE BREAKING MANHOLE |
| ST | SAND TRAP |
| PDO | PLANTER DRAIN OUTLET |
| RWO | RAIN WATER OUTLET |
| FCO | FLOOR CLEAN OUT |
| CO | CLEAN OUT |
| F/A | FROM ABOVE |
| F/B | FROM BELOW |
| T/A | TO ABOVE |
| T/B | TO BELOW |
| HL | HIGH LEVEL |
| LL | LOW LEVEL |
| DTLL | DROP TO LOW LEVEL |

Key Plan

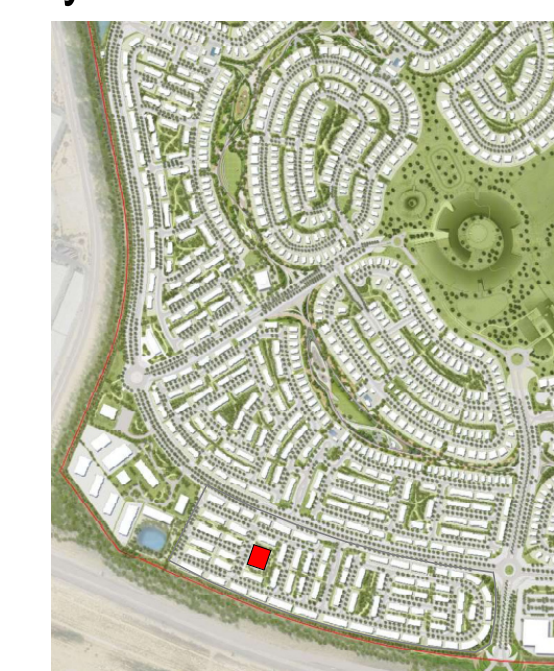

General Notes :

- Do not Scale The Drawings. Follow (The MM) Written Dimensions Unless Otherwise Mentioned.
- Each Drawing Shall be Read in Conjunction With All Other Drawings Specification & the General Standard Details. In Case of Any Discrepancies Bring it to the Knowledge of Engineer and Same to be Resolved Prior to Execution of Work.
- Dimensions Shown on These Drawings are Structural Dimensions. Unless Noted Otherwise.
- All Levels Indicated On These Drawings are Levels as per the the Survey Datum, Same Should be Verified at Site Prior to Execution of Work.
- All Levels Indicated On These Drawings are Based On Design Level, Which is Equivalent to Datum Level and Same Should be Verified at Site Prior to Execution of Work.



00	10/03/2026	LSG	TENDER SUBMISSION
00	16/01/2026	LSG	DETAILED DESIGN SUBMISSION
00	31/10/2025	LSG	SCHEMATIC DESIGN SUBMISSION
00	15/10/2025	LSG	SCHEMATIC SUBMISSION-50%
00	01/09/2025	LSG	CONCEPT DESIGN SUBMISSION

No.	Date	Initials	Description
-----	------	----------	-------------

REVISIONS / ISSUE

THIS DRAWING MUST NOT BE REPRODUCED IN WHOLE OR IN PART WITHOUT THE PRIOR APPROVAL OF ARIF & BINTOAK

Status

TENDER SUBMISSION

Client

EMAAR

Lead Consultant



Project Title: Proposed Residential Townhouses and Standalone Villas TH-01, TH-02, and TH-03 at Grand Polo Club & Resort, Dubai, UAE

Discipline: MECHANICAL

SERVICE BLOCK BASEMENT, GROUND & ROOF FLOOR DRAINAGE LAYOUT

Architectural Engineer	Electrical Engineer	Structural Engineer
MUSTAFA ABID	MARWAN MOHD.	RIHAM RAMADAN
Registration # 5847	Registration # 60102	Registration # 106092
Scale(s): As indicated	Date: 10/03/2026	Project no: 1857
Drawn by: LSG	Checked: MAV	Approved: MRM

Drawing Number: GPCR-TH01-AB-DRG-ZZZ-MEC-DR-3403-00