




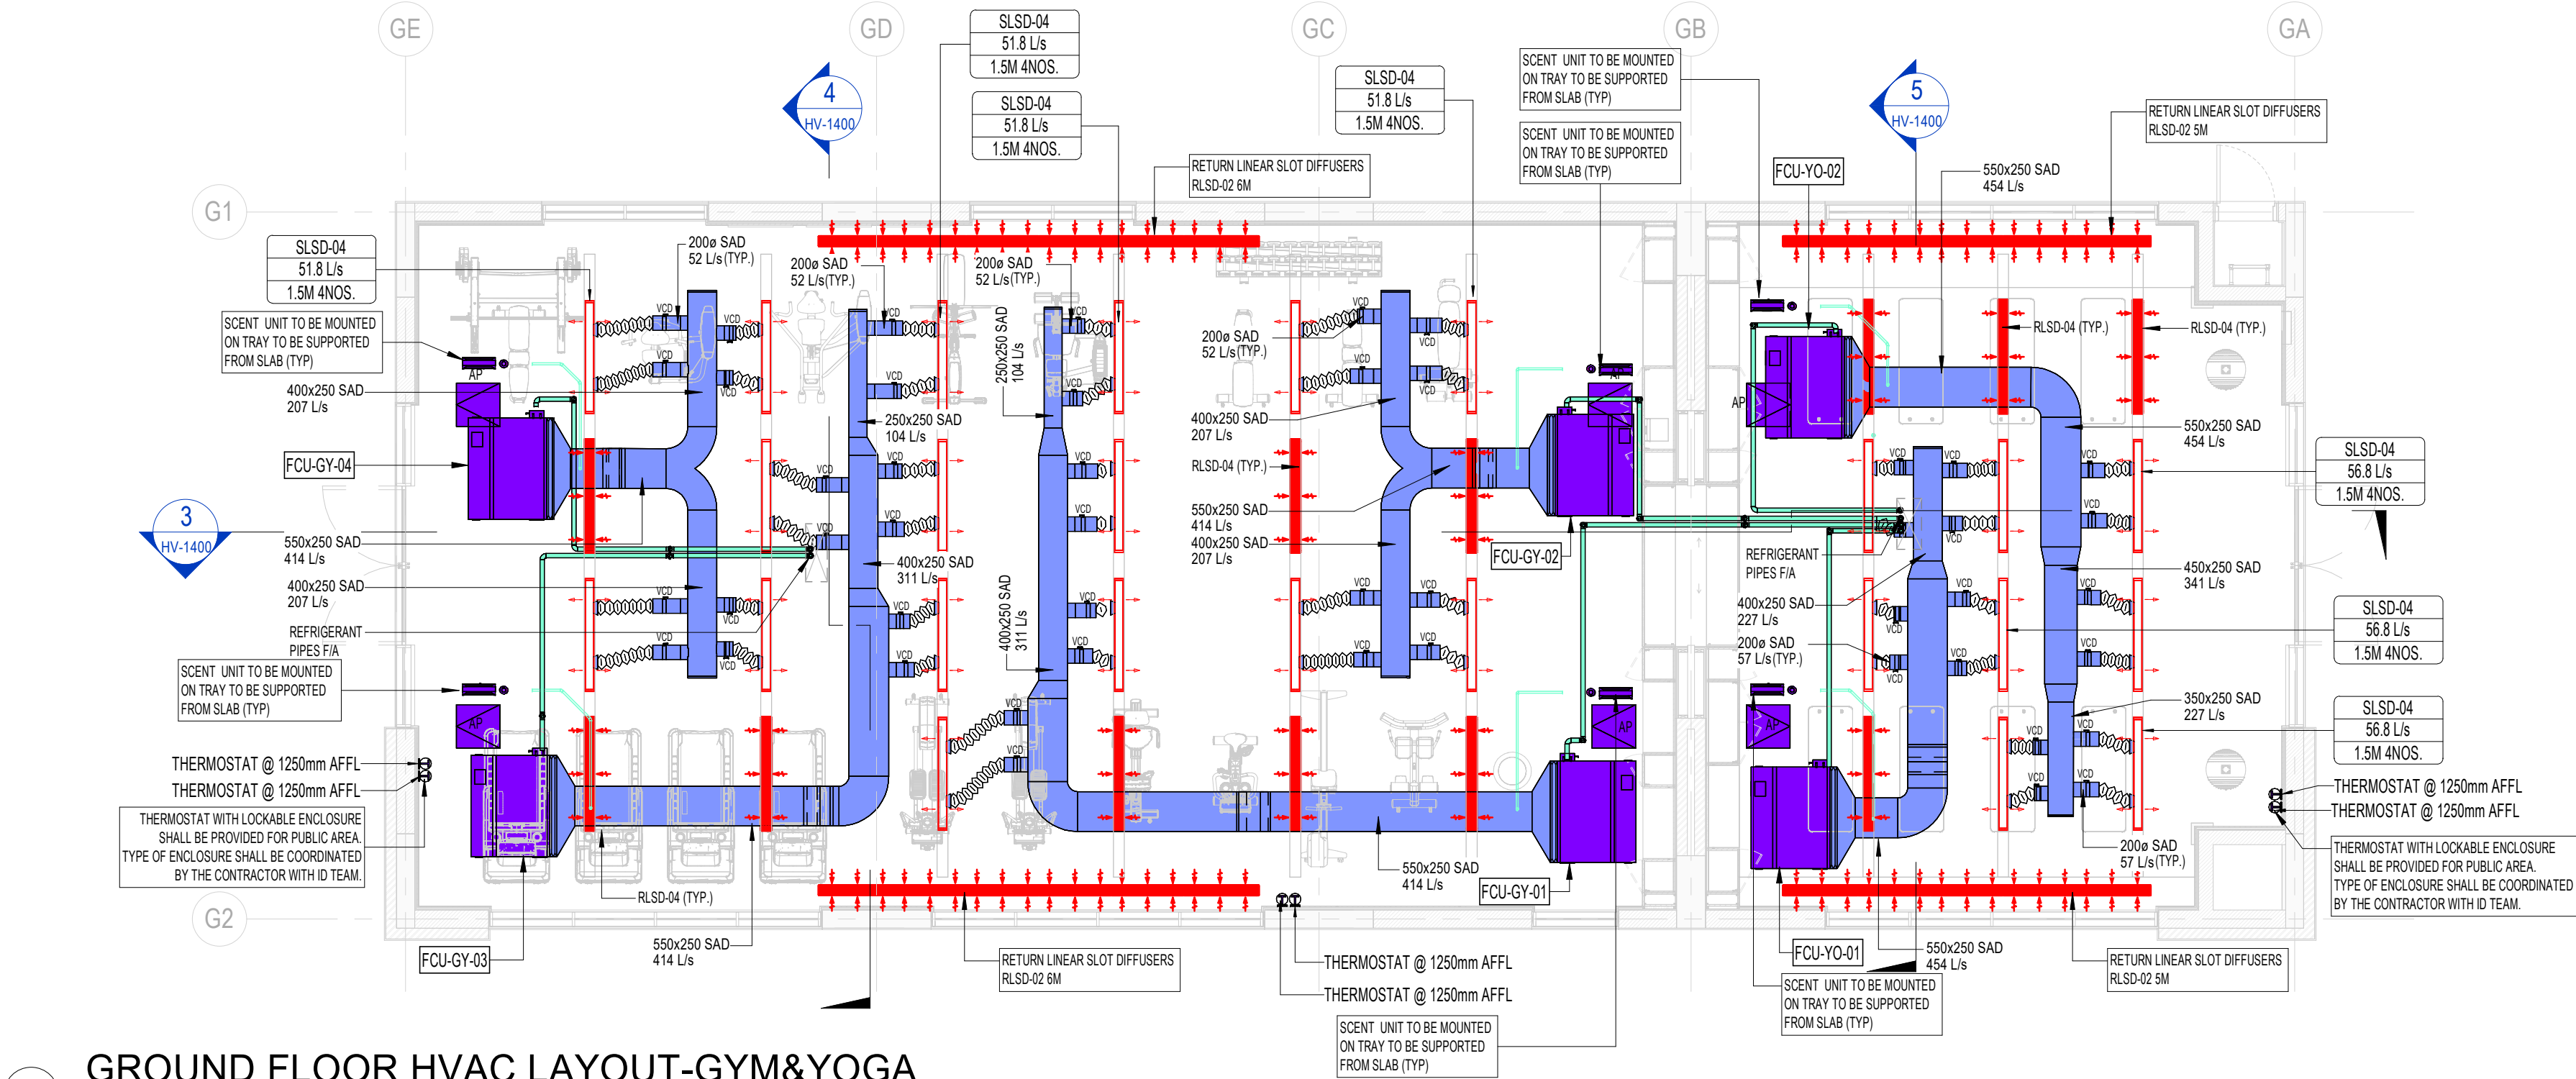


1 GROUND FLOOR HVAC LAYOUT-GYM&YOGA
1 : 75

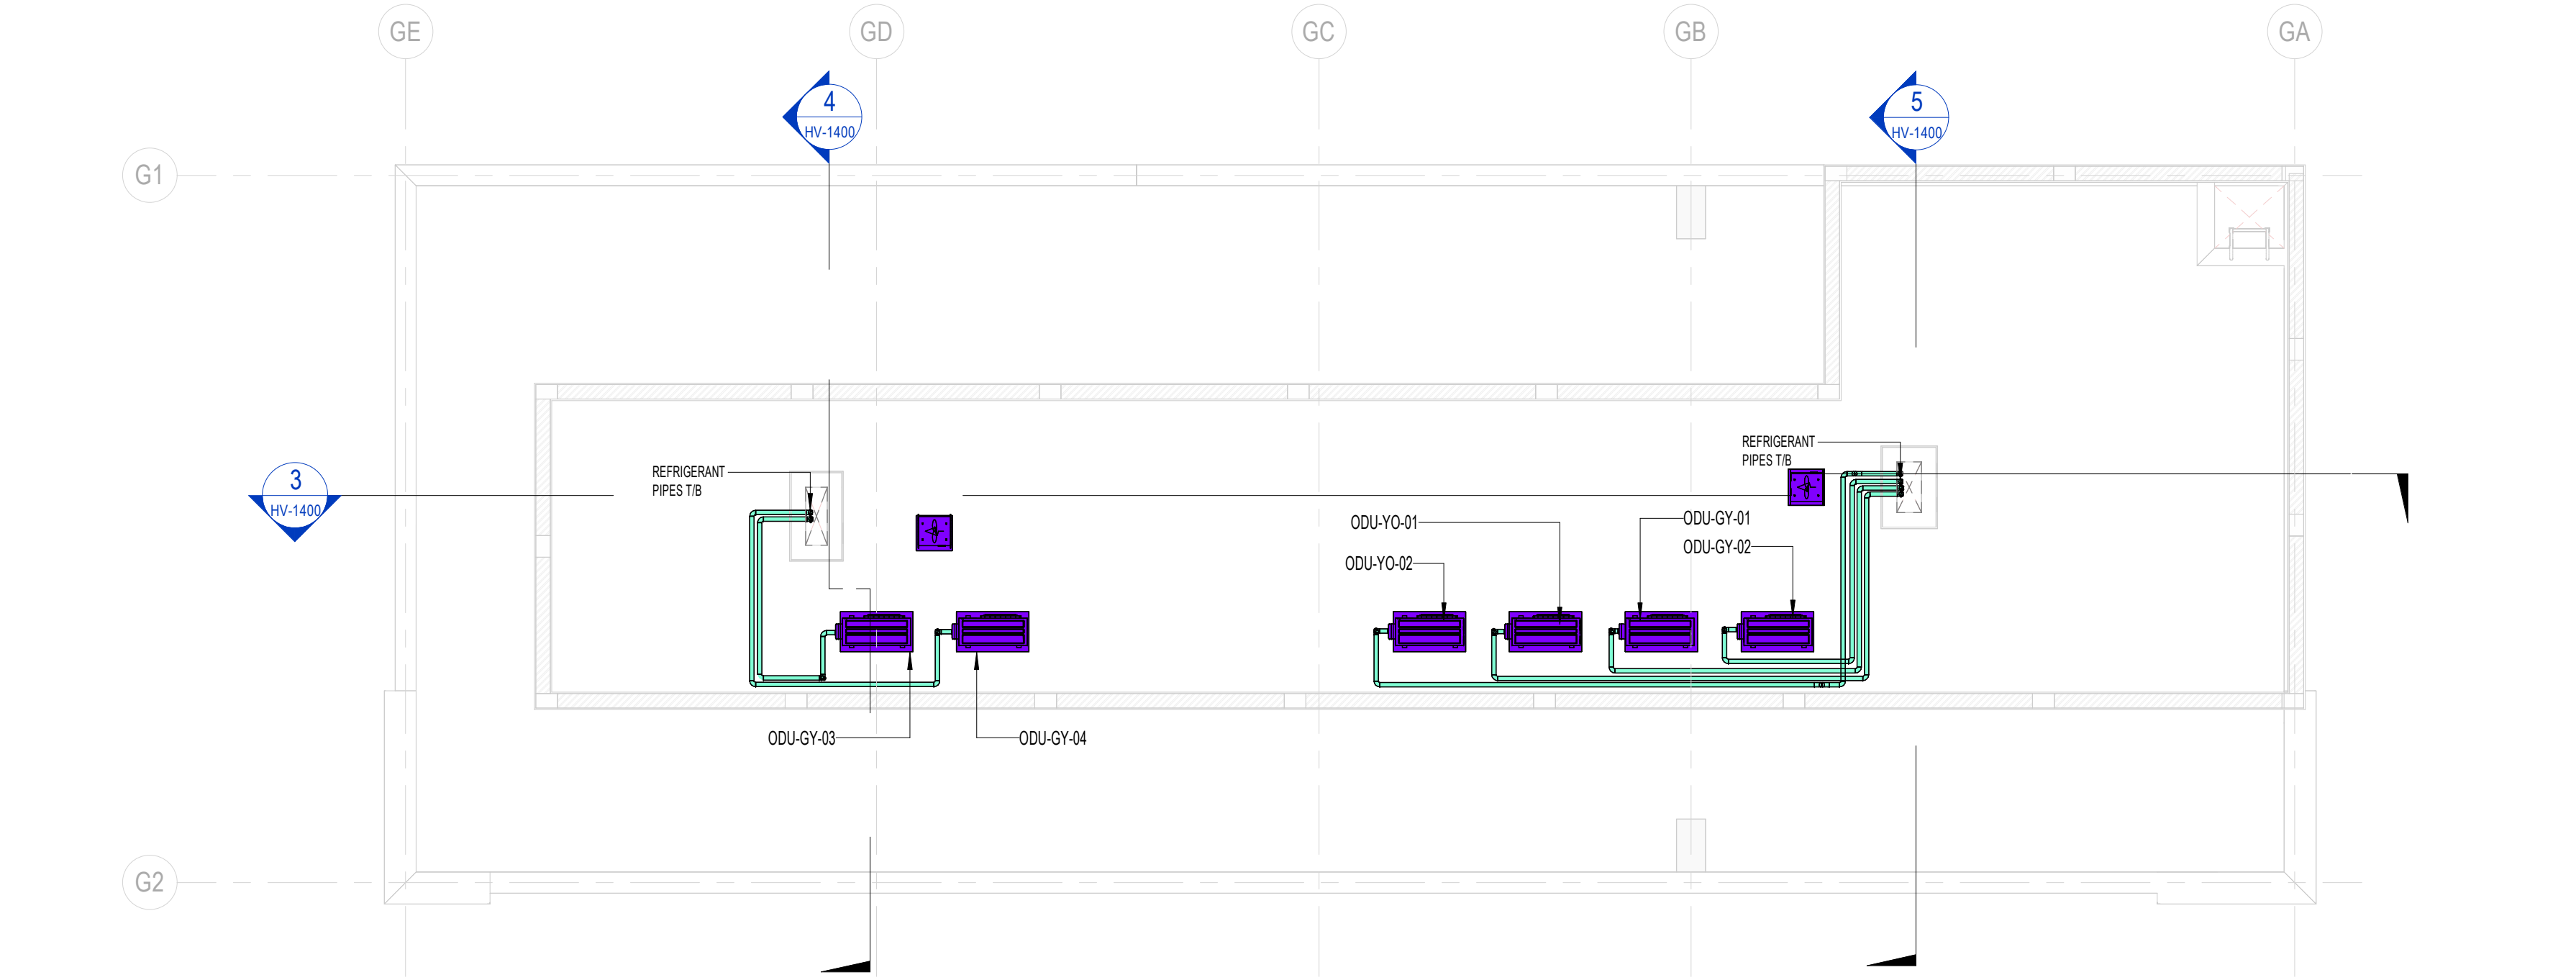


2 ROOF FLOOR HVAC LAYOUT-GYM&YOGA
1 : 75

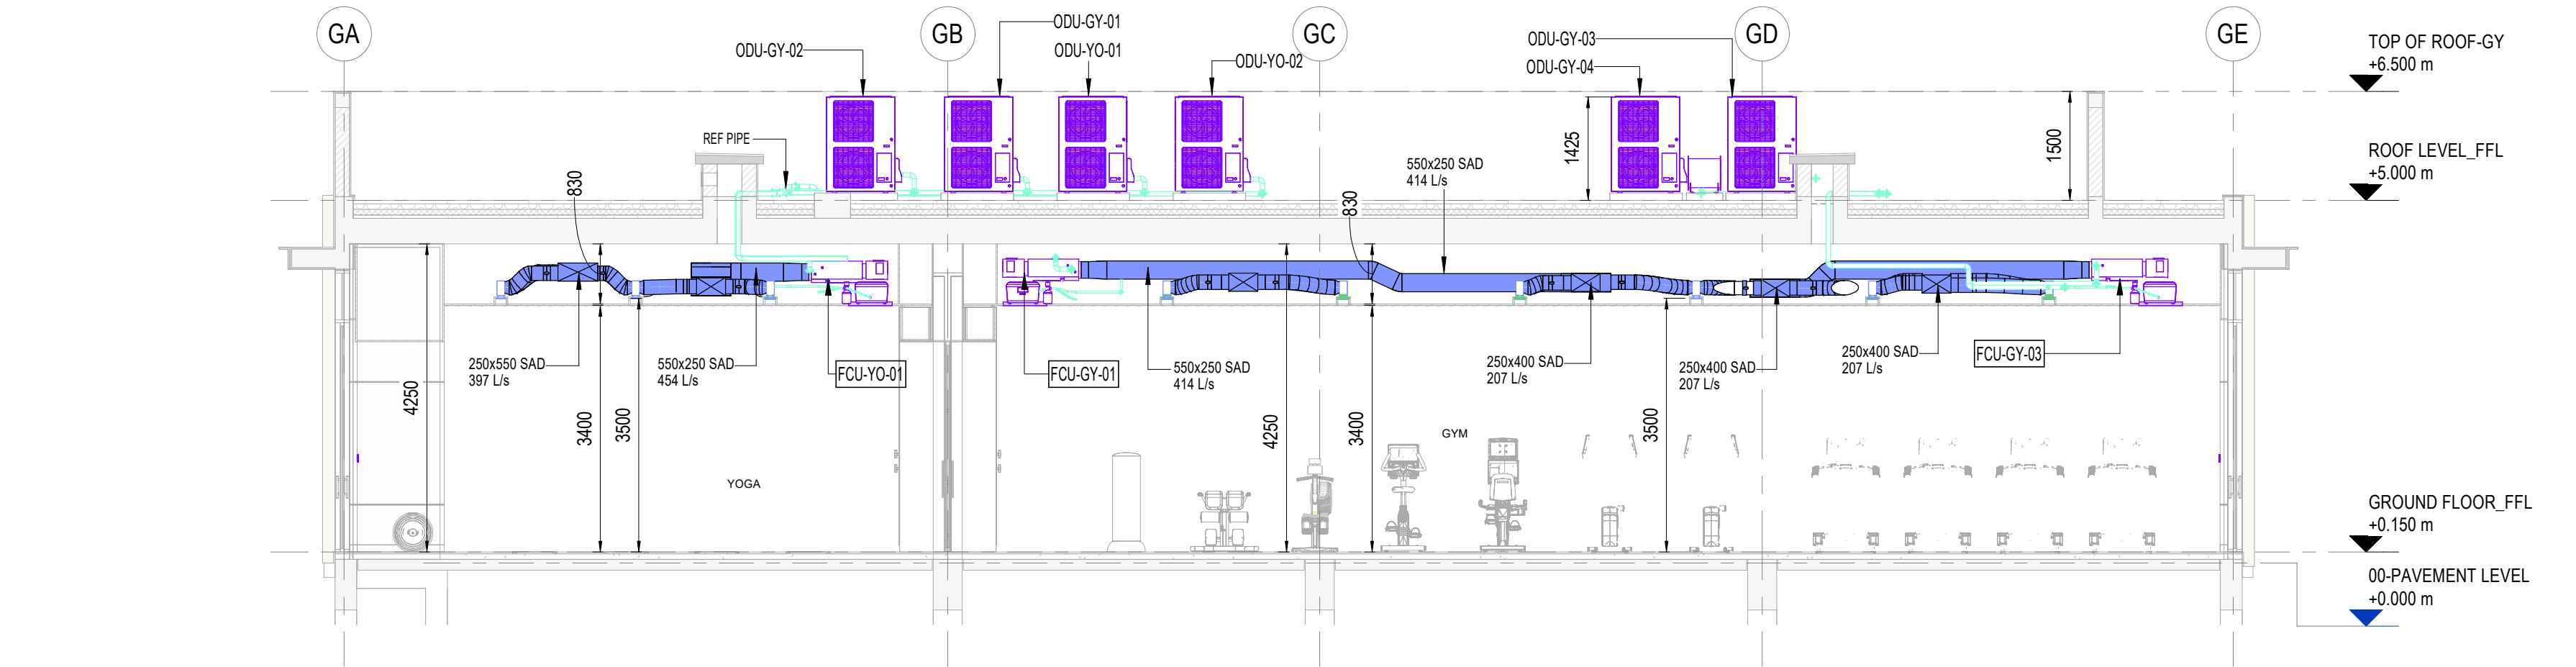


3 GYM&YOGA AC SECTION 01
1 : 75

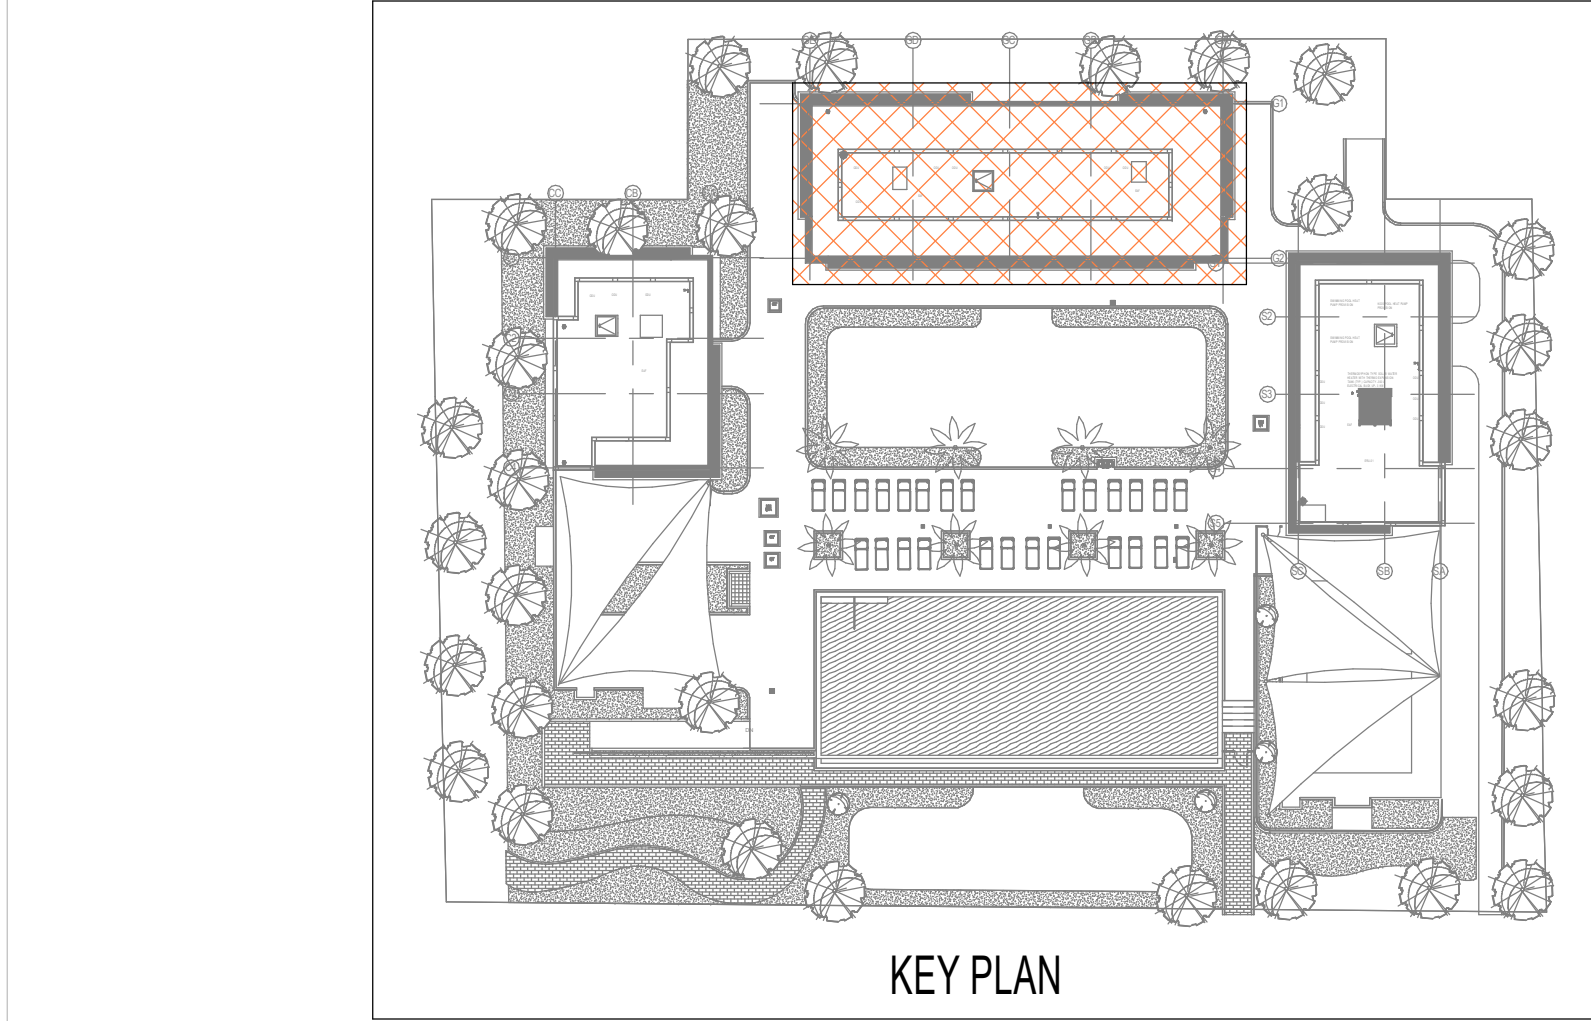

SUPPLY & RETURN LINEAR SLOT DIFFUSERS SCHEDULE					
UNIT NO.	DESCRIPTION	SLOTS		PLENUM BOX	
		NO.	WIDTH (mm)	LENGTH (mm)	CAPACITY RANGE (LPS)
SLSD-01 RLSD-01	SUPPLY & RETURN LINEAR SLOT DIFFUSER	1	20	1000	0 TO 47
SLSD-02 RLSD-02	SUPPLY & RETURN LINEAR SLOT DIFFUSER	2	20	1000	48 TO 70
SLSD-03 RLSD-03	SUPPLY & RETURN LINEAR SLOT DIFFUSER	2	20	500	up to 47
SLSD-04 RLSD-04	SUPPLY & RETURN LINEAR SLOT DIFFUSER	2	20	1500	50 TO 110

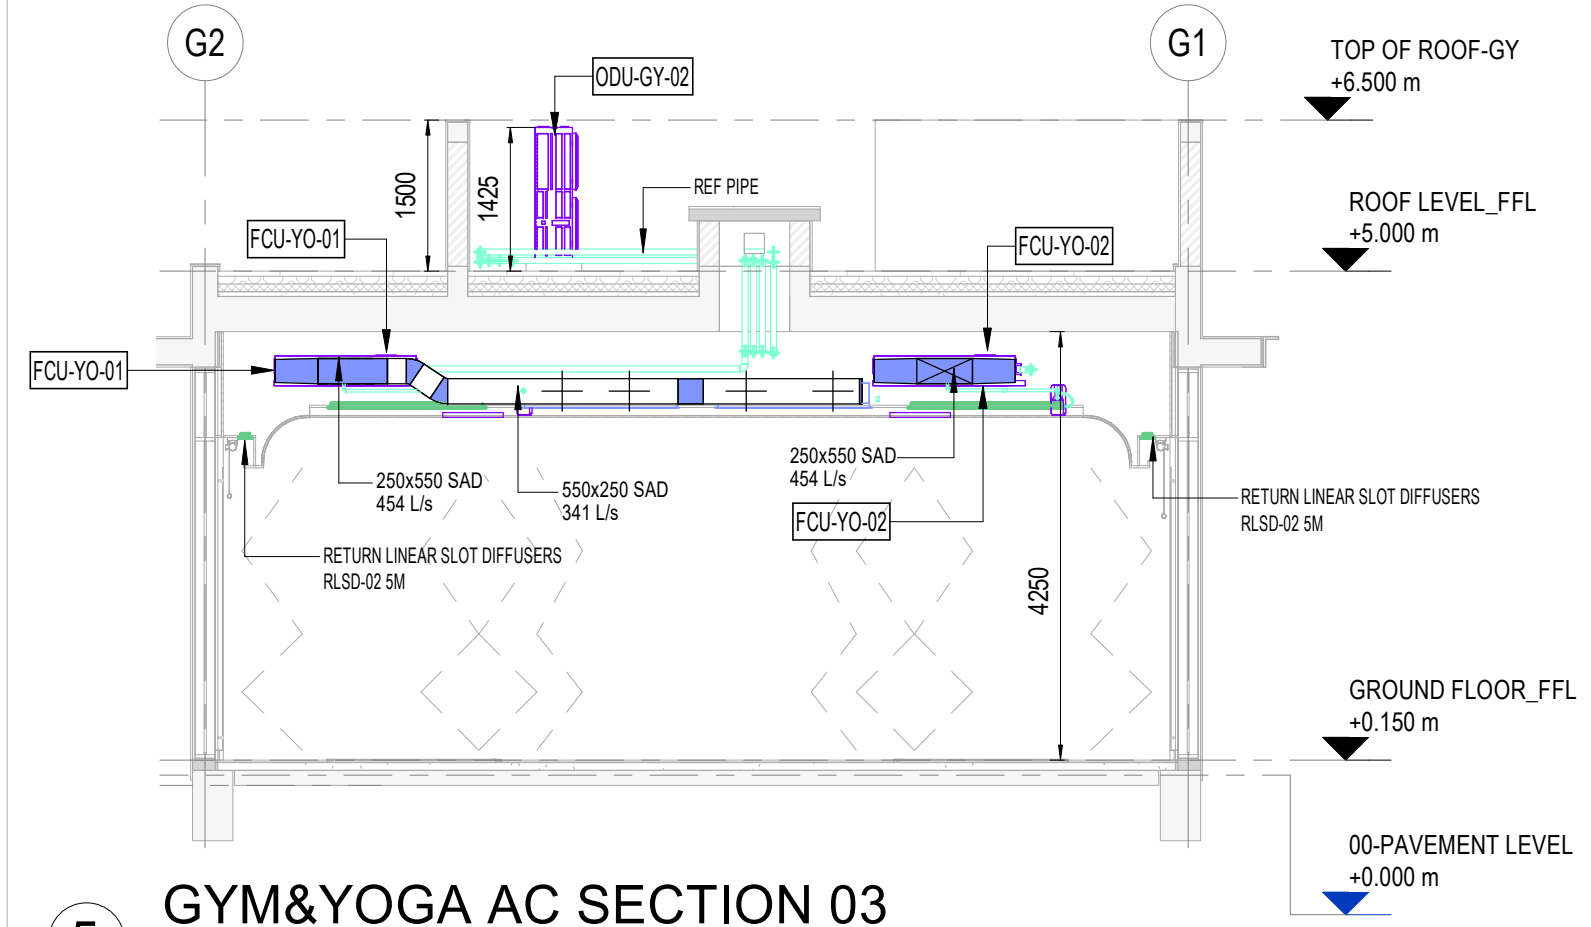


5 GYM&YOGA AC SECTION 03
1 : 75

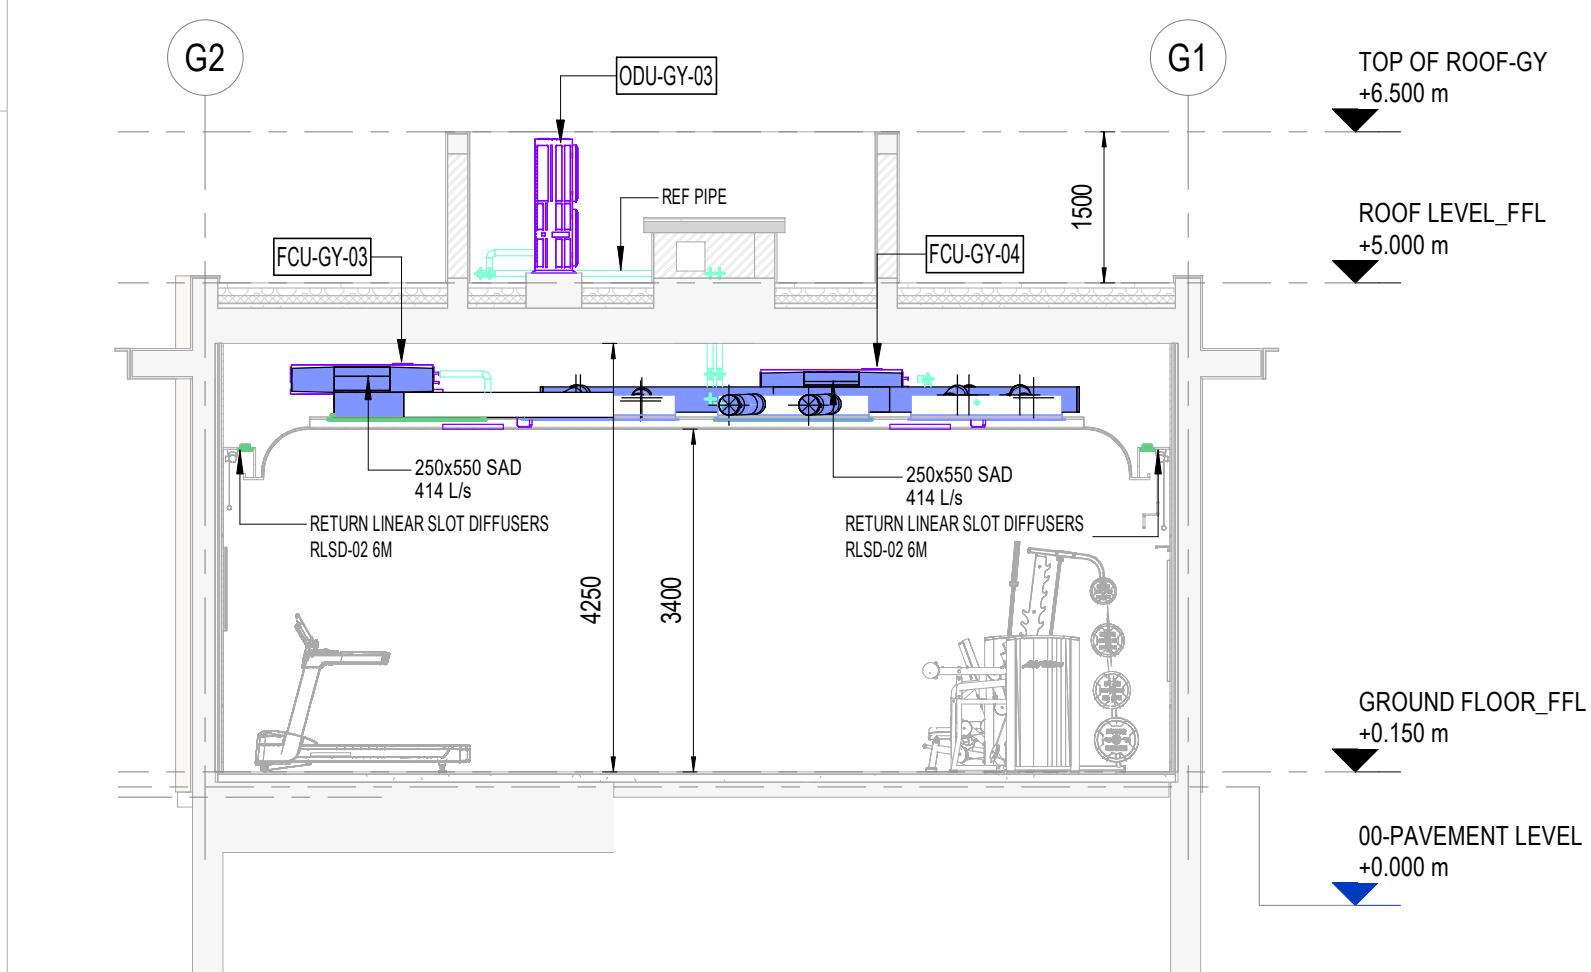

4 GYM&YOGA AC SECTION 02
1 : 75

Key Plan

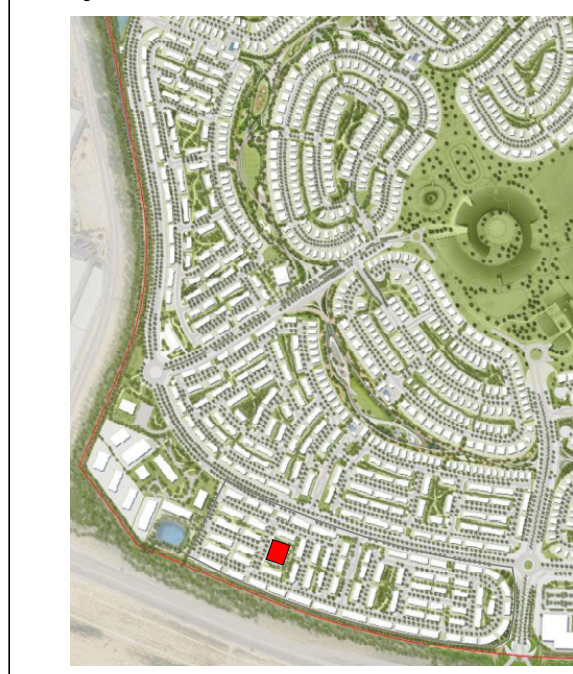

General Notes :

01. Do not Scale The Drawings. Follow (The MM) Written Dimensions Unless Otherwise Mentioned.
02. Each Drawing Shall be Read in Conjunction With all Other Drawings Specification & the General Standard Details. In Case of Any Discrepancies Bring it to the Knowledge of Engineer and Same to be Resolved Prior to Execution of Work.
03. Dimensions Shown on These Drawings are Structural Dimensions. Unless Noted Otherwise.
04. All Levels Indicated On These Drawings are Levels as per the Survey Datum, Same Should be Verified at Site Prior to Execution of Work.
05. All Levels Indicated On These Drawings are Based On Design Level, Which is Equivalent to Datum Level and Same Should be Verified at Site Prior to Execution of Work.



No.	Date	Initials	Description
00	10/03/2026	LSG	TENDER SUBMISSION
00	16/01/2026	LSG	DETAILED DESIGN SUBMISSION
00	31/10/2025	LSG	SCHEMATIC DESIGN SUBMISSION
00	15/10/2025	LSG	SCHEMATIC SUBMISSION-50%
00	01/09/2025	LSG	CONCEPT DESIGN SUBMISSION

REVISIONS / ISSUE

THIS DRAWING MUST NOT BE REPRODUCED IN WHOLE OR IN PART WITHOUT THE PRIOR APPROVAL OF ARIF & BINTOAK

Status

TENDER SUBMISSION

Client

EMAAR

Lead Consultant



Project Title:
Proposed Residential Townhouses and Standalone Villas
TH-01, TH-02, and TH-03 at Grand Polo Club & Resort, Dubai, UAE

Discipline: MECHANICAL

Drawing title:
**GYM & YOGA
GROUND & ROOF FLOOR
AC LAYOUT**

Architectural Engineer	Electrical Engineer	Structural Engineer
MUSTAFA ABID Registration # 5847	MARWAN MOHD. Registration # 80102	RIHAM RAMADAN Registration # 105892
Scale(s): 1 : 75	Date: 10/03/2026	Project no: 1857
Drawn by: LSG	Checked: MAV	Approved: MRM

Drawing Number: GPCR-TH01-AB-DRG-ZZZ-MEC-HV-1400-00