




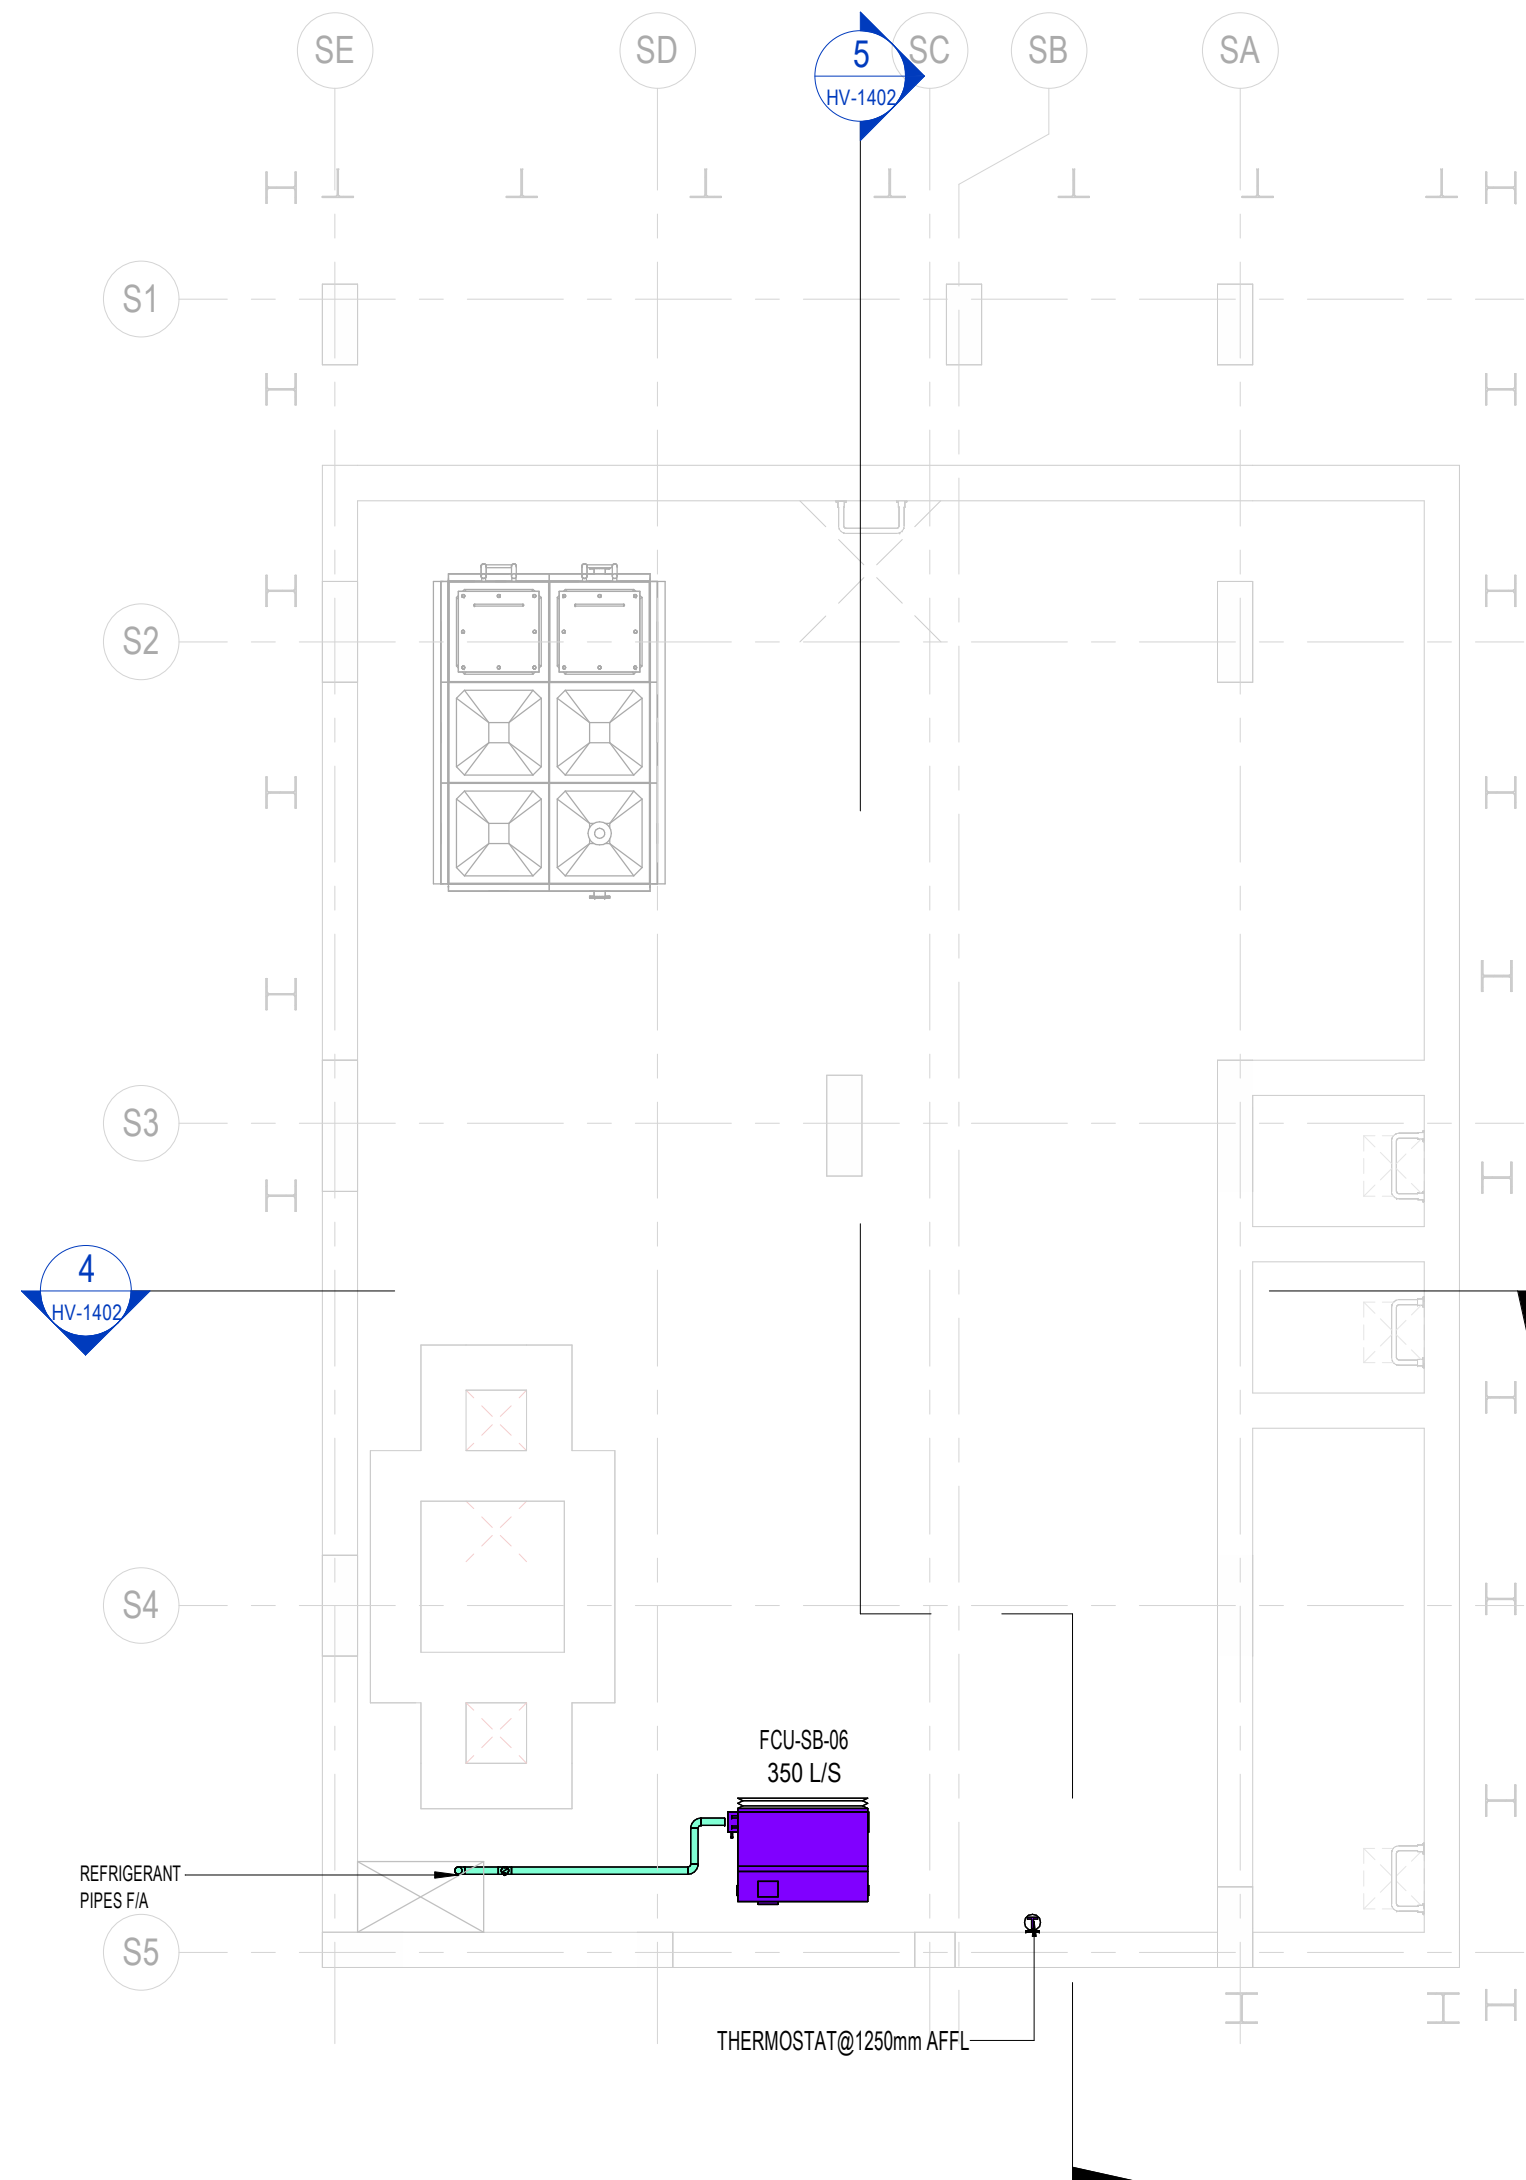


1 BASEMENT FLOOR HVAC LAYOUT
1 : 75

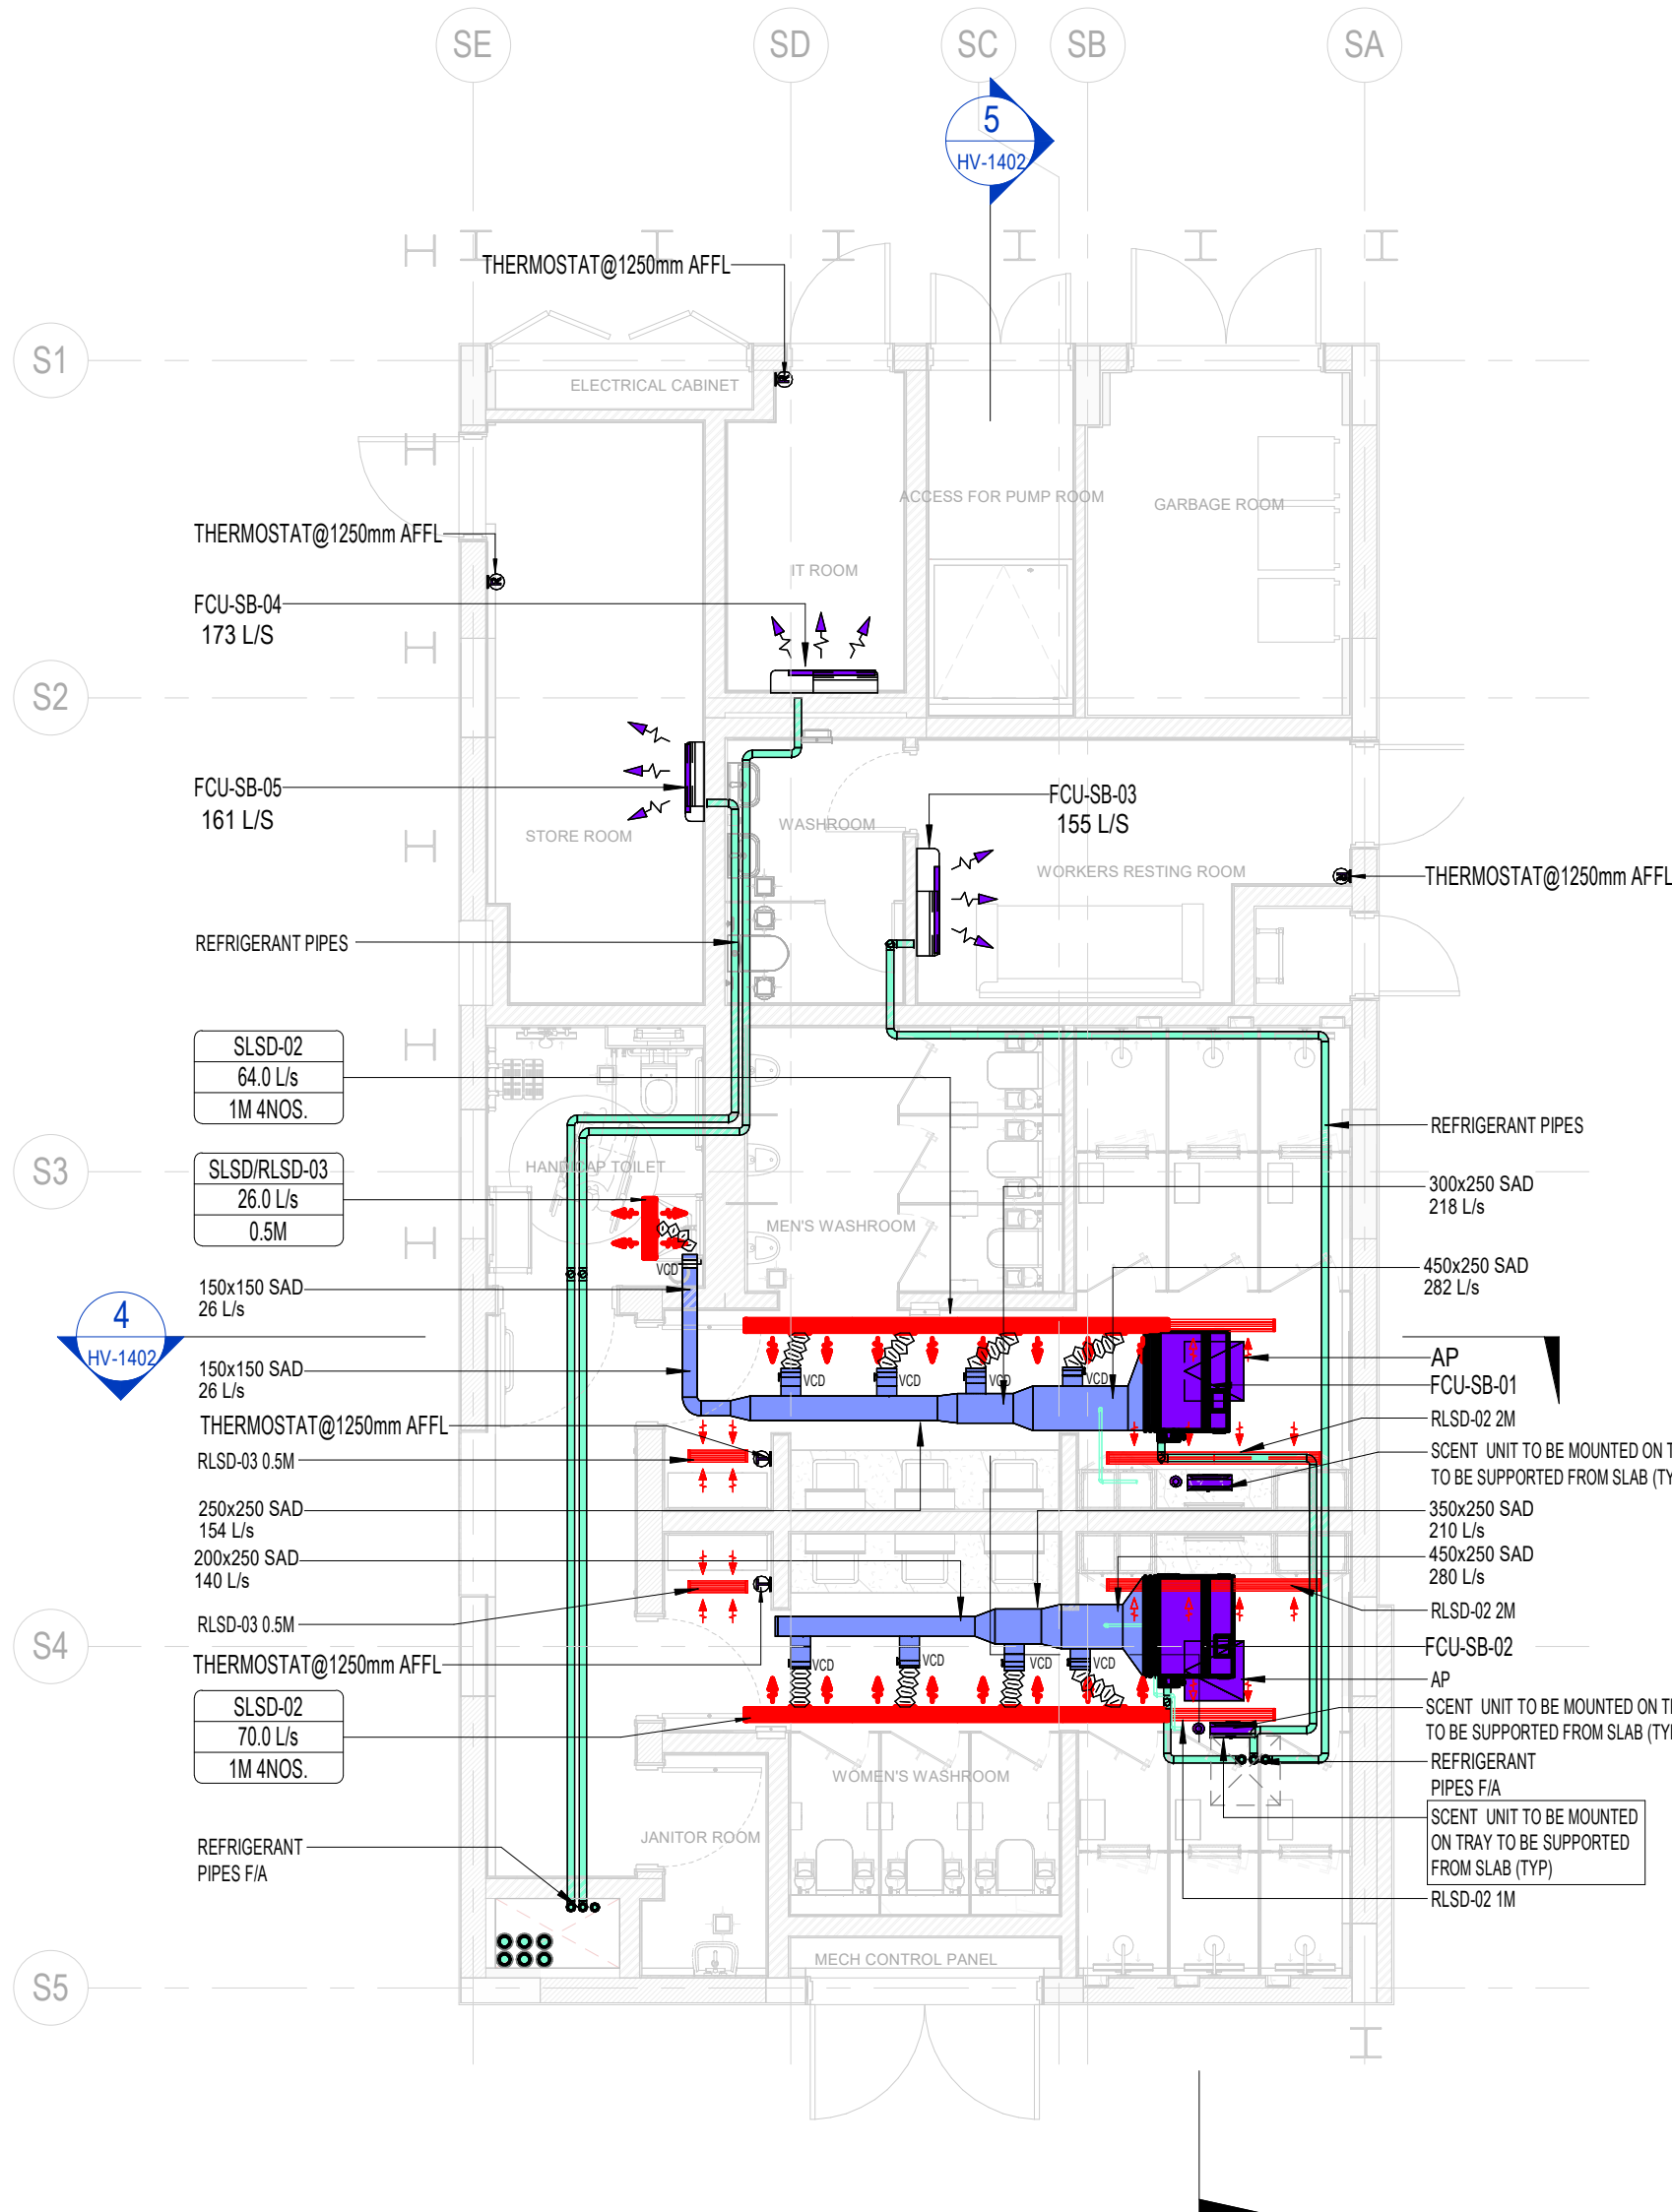


2 GROUND FLOOR HVAC LAYOUT-SERVICE BLOCK
1 : 75

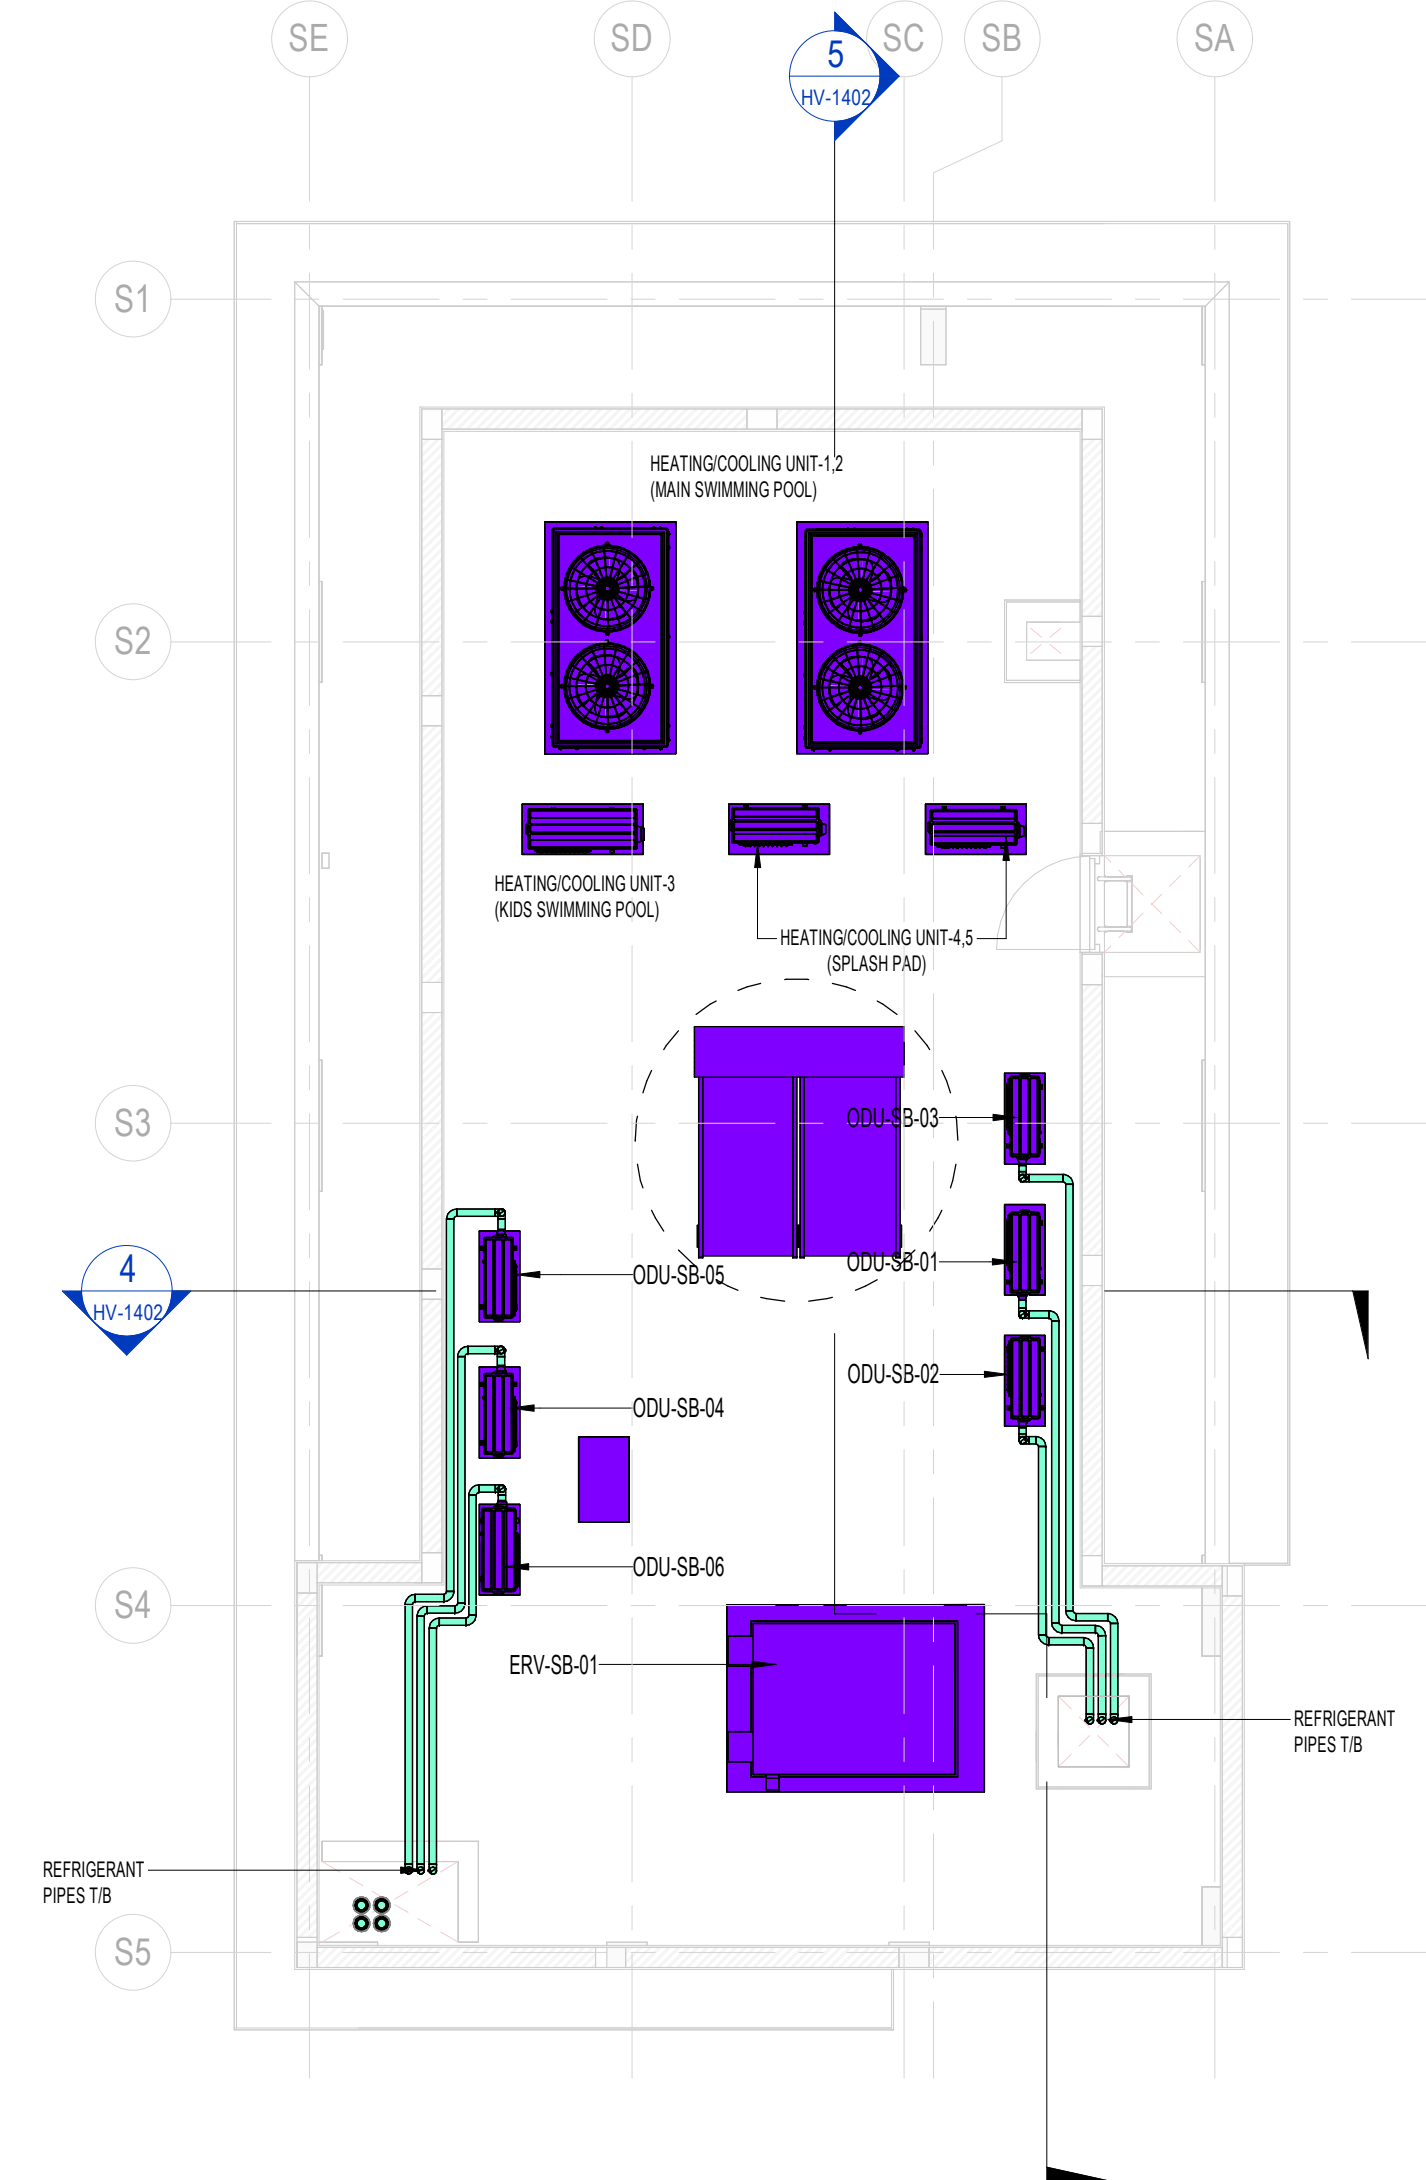

3 ROOF FLOOR HVAC LAYOUT-SERVICE BLOCK
1 : 75

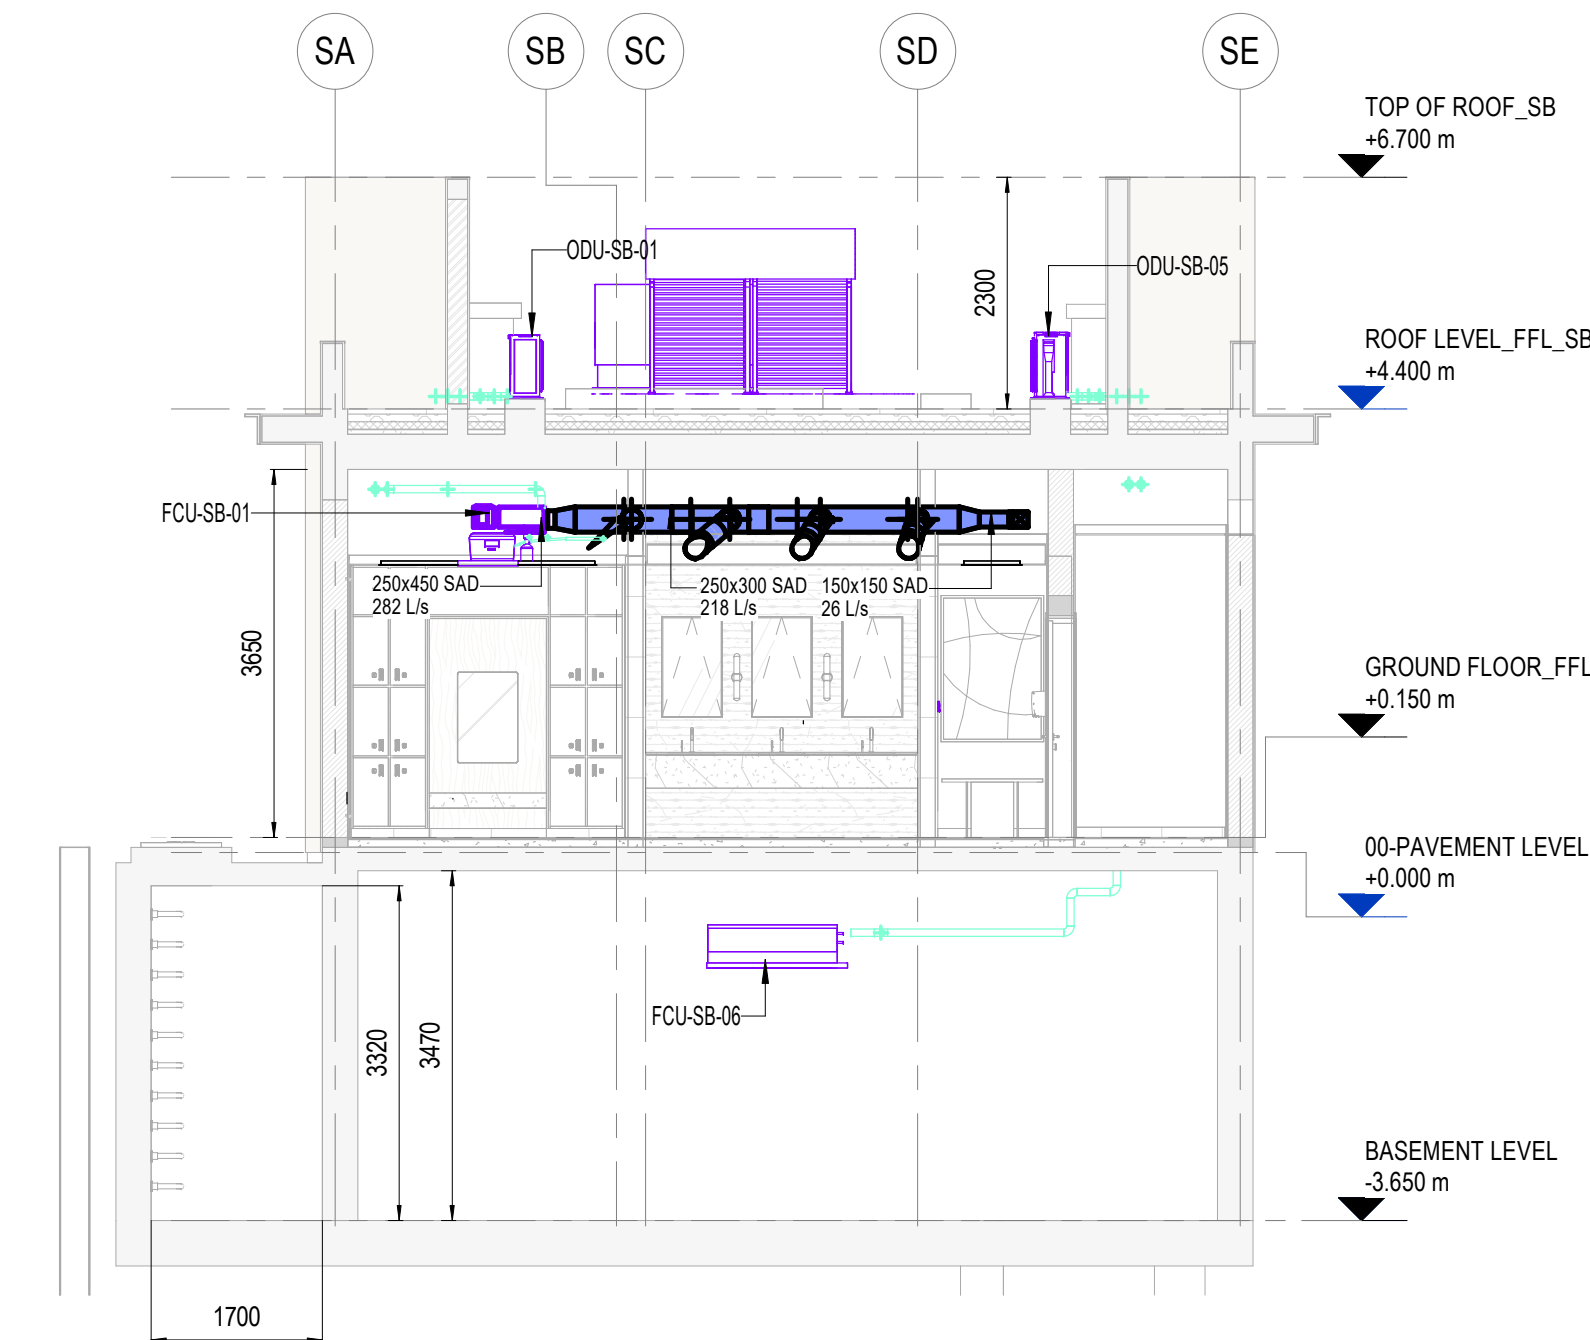


4 SERVICE BLOCK AC SECTION 01
1 : 75

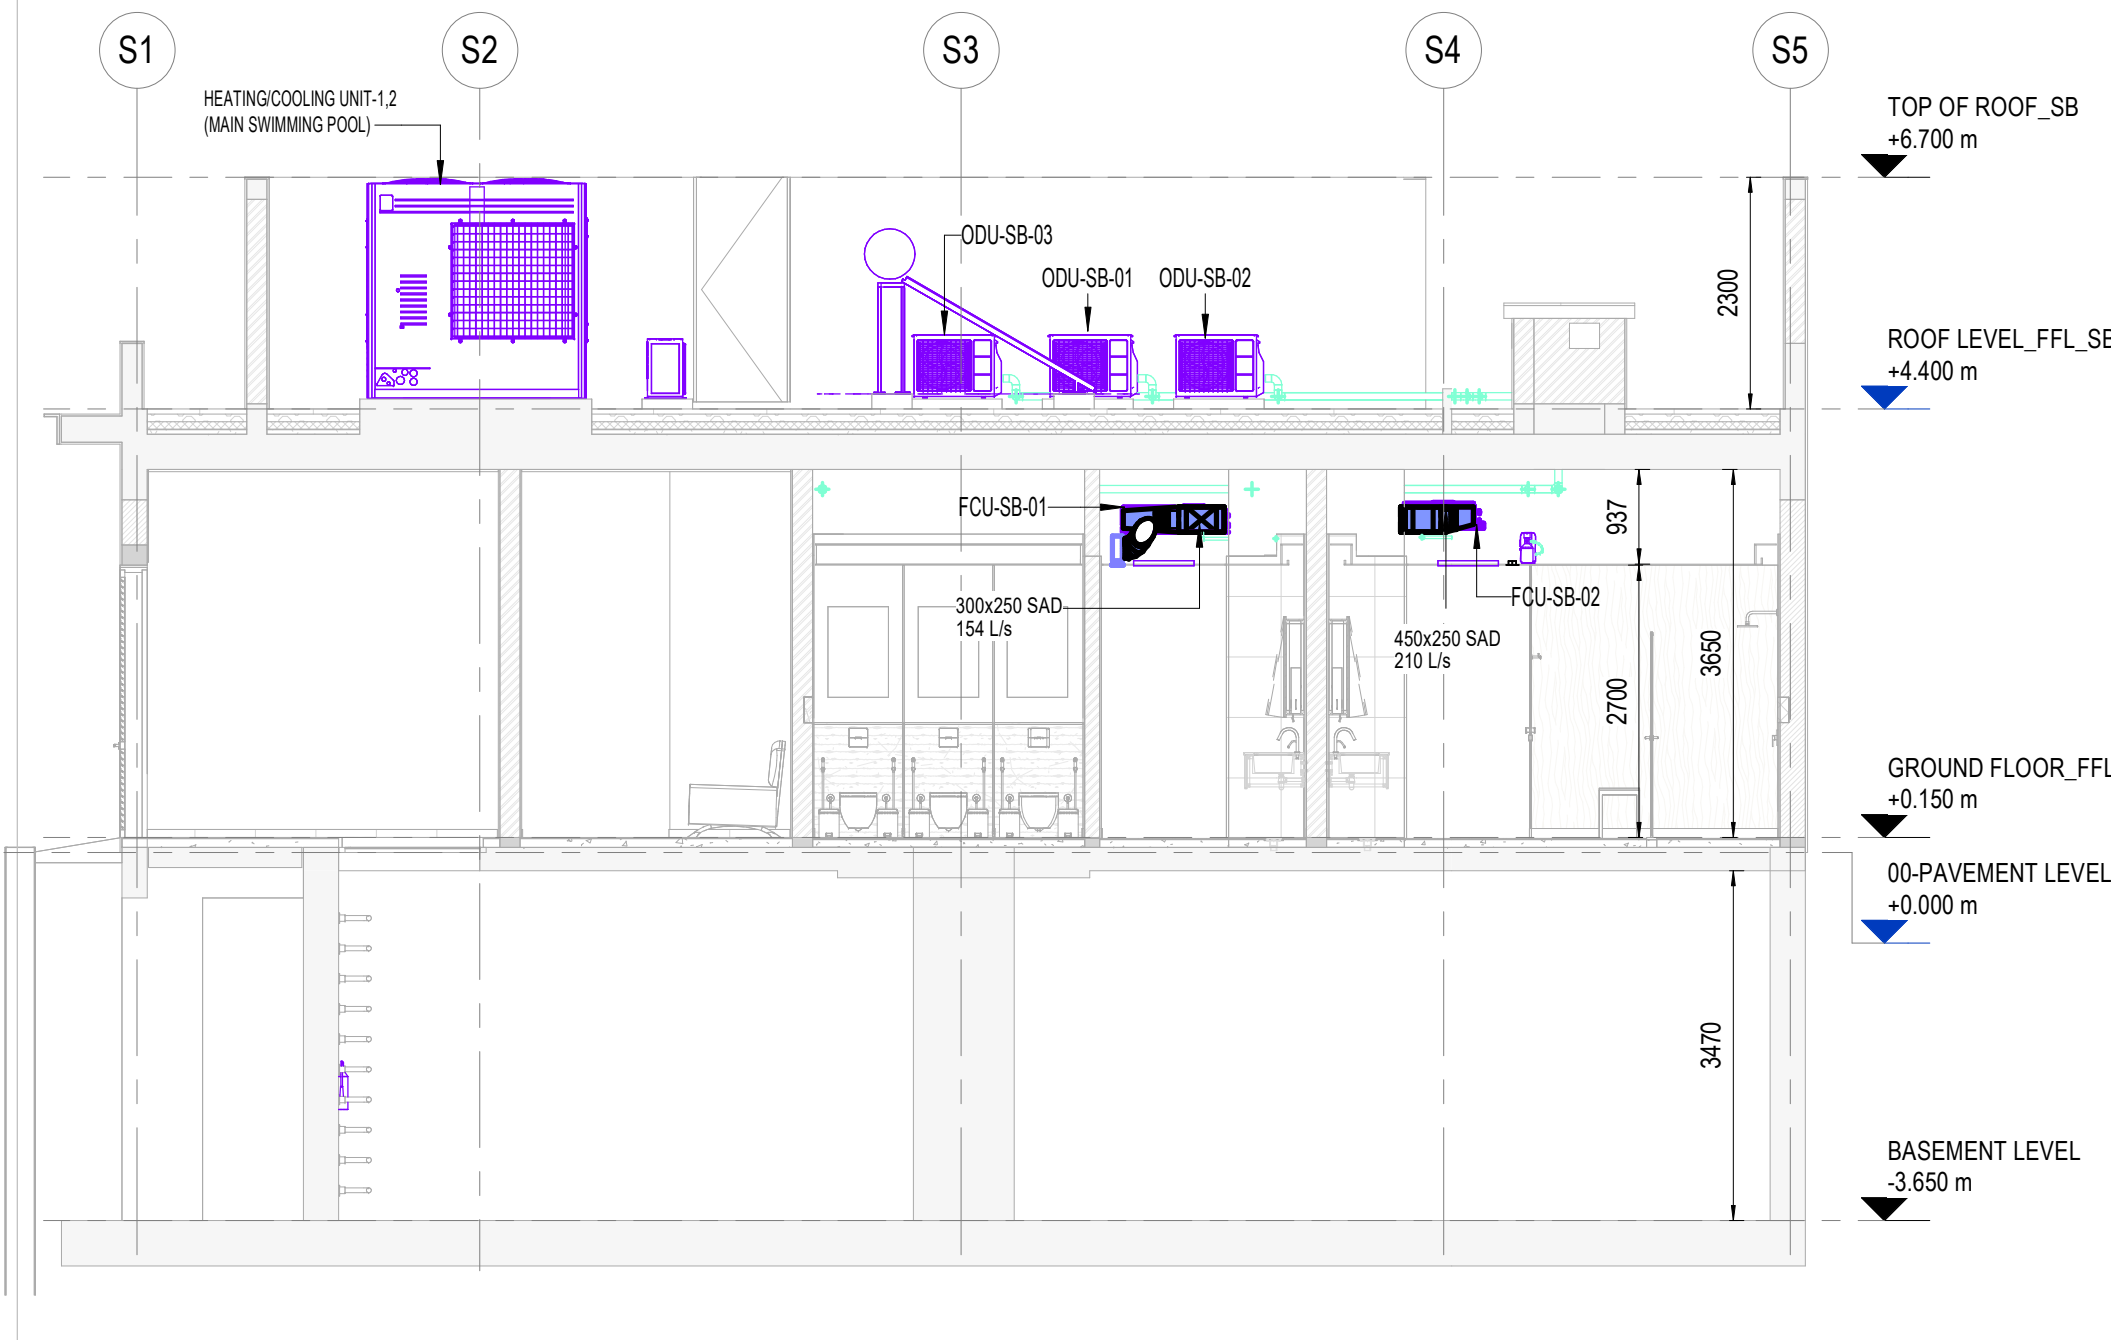


5 SERVICE BLOCK AC SECTION 02
1 : 75

SUPPLY & RETURN LINEAR SLOT DIFFUSERS SCHEDULE						
UNIT NO.	DESCRIPTION	SLOTS		PLENUM BOX		CAPACITY RANGE (LPS)
		NO.	WIDTH (mm)	LENGTH (mm)	INLET Ø (mm)	
SLSD_01 RLSD_01	SUPPLY & RETURN LINEAR SLOT DIFFUSER	1	20	1000	ø 150	0 TO 47
SLSD_02 RLSD_02	SUPPLY & RETURN LINEAR SLOT DIFFUSER	2	20	1000	ø 200	48 TO 70
SLSD_03 RLSD_03	SUPPLY & RETURN LINEAR SLOT DIFFUSER	2	20	500	ø 150	up TO 47
SLSD_04 RLSD_04	SUPPLY & RETURN LINEAR SLOT DIFFUSER	2	20	1500	ø 150	50 TO 110

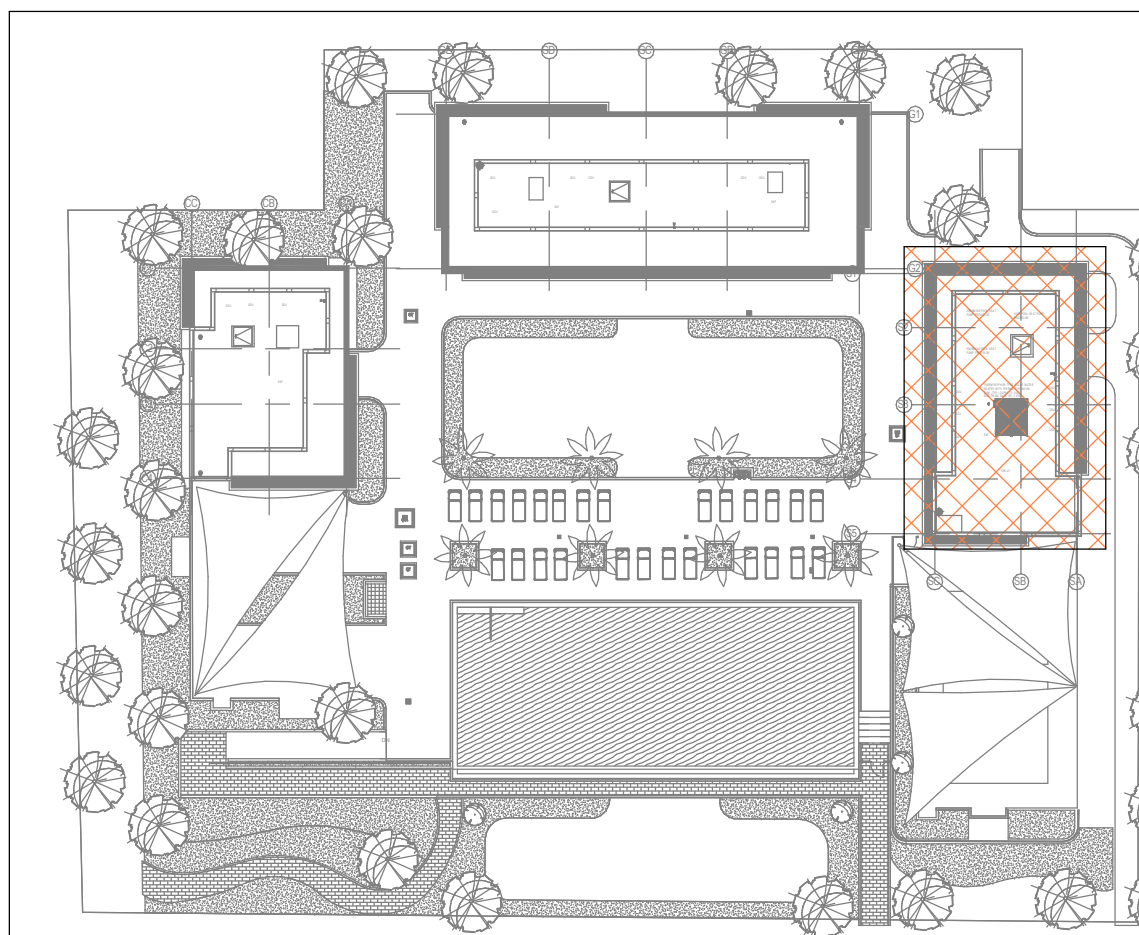

KEY PLAN

Key Plan

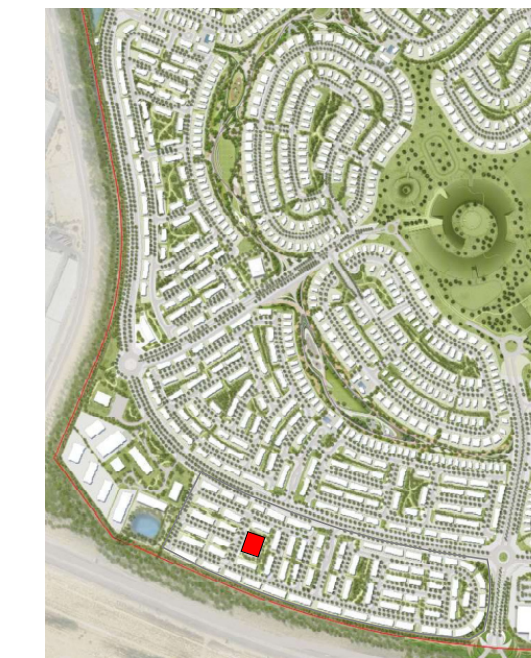

General Notes :

- Do not Scale The Drawings. Follow (The MM) Written Dimensions Unless Otherwise Mentioned.
- Each Drawing Shall be Read in Conjunction With all Other Drawings Specification & the General Standard Details. In Case of Any Discrepancies Bring it to the Knowledge of Engineer and Same to be Resolved Prior to Execution of Work.
- Dimensions Shown on These Drawings are Structural Dimensions Unless Noted Otherwise.
- All Levels Indicated On These Drawings are Levels as per the Survey Datum, Same Should be Verified at Site Prior to Execution of Work.
- All Levels Indicated On These Drawings are Based On Design Level, Which is Equivalent to Datum Level and Same Should be Verified at Site Prior to Execution of Work.



00	10/03/2026	LSG	TENDER SUBMISSION
00	16/01/2026	LSG	DETAILED DESIGN SUBMISSION
00	31/10/2025	LSG	SCHEMATIC DESIGN SUBMISSION
00	15/10/2025	LSG	SCHEMATIC SUBMISSION-50%
00	01/09/2025	LSG	CONCEPT DESIGN SUBMISSION

No.	Date	Initials	Description
REVISIONS / ISSUE			
THIS DRAWING MUST NOT BE REPRODUCED IN WHOLE OR IN PART WITHOUT THE PRIOR APPROVAL OF ARIF & BINTOAK			

Status: TENDER SUBMISSION

Client: EMAAR

Lead Consultant: Arif & BintOak

Project Title: Proposed Residential Townhouses and Standalone Villas TH-01, TH-02, and TH-03 at Grand Polo Club & Resort, Dubai, UAE

Discipline: MECHANICAL

Drawing title: SERVICE BLOCK BASEMENT, GROUND & ROOF FLOOR AC LAYOUT

Architectural Engineer: MUSTAFA ABID
Electrical Engineer: MARWAN MOHD.
Structural Engineer: RIHAM RAMADAN
Registration # 5847
Registration # 80102
Registration # 105892
Scale(s): 1 : 75
Date: 10/03/2026
Project no: 1857
Drawn by: LSG
Checked: MAV
Approved: MRM

Drawing Number: GPCR-TH01-AB-DRG-ZZZ-MEC-HV-1402-00