




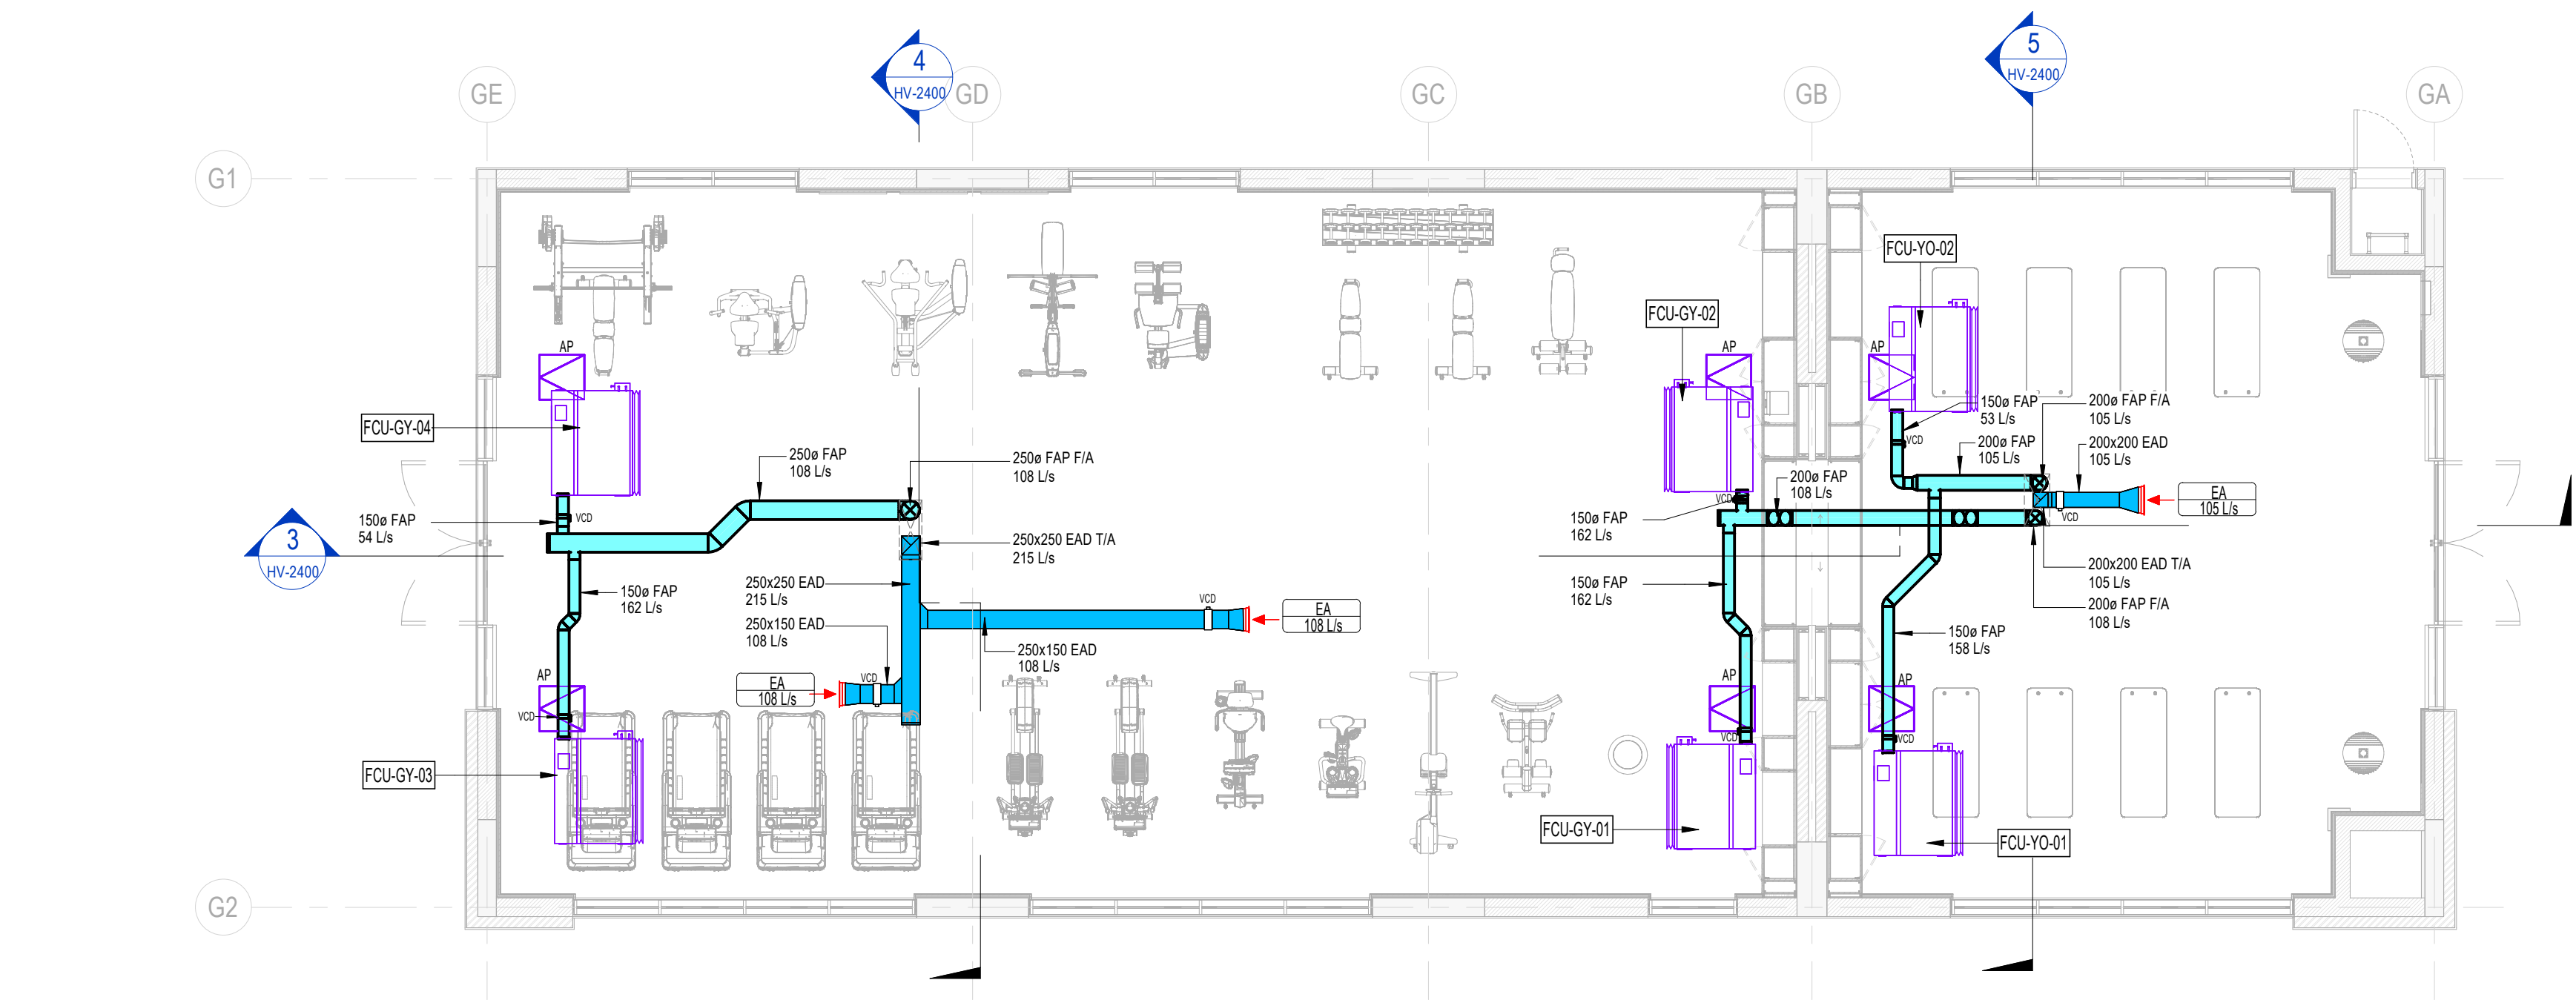


1 GROUND FLOOR VENTILATION LAYOUT-GYM&YOGA
1 : 75

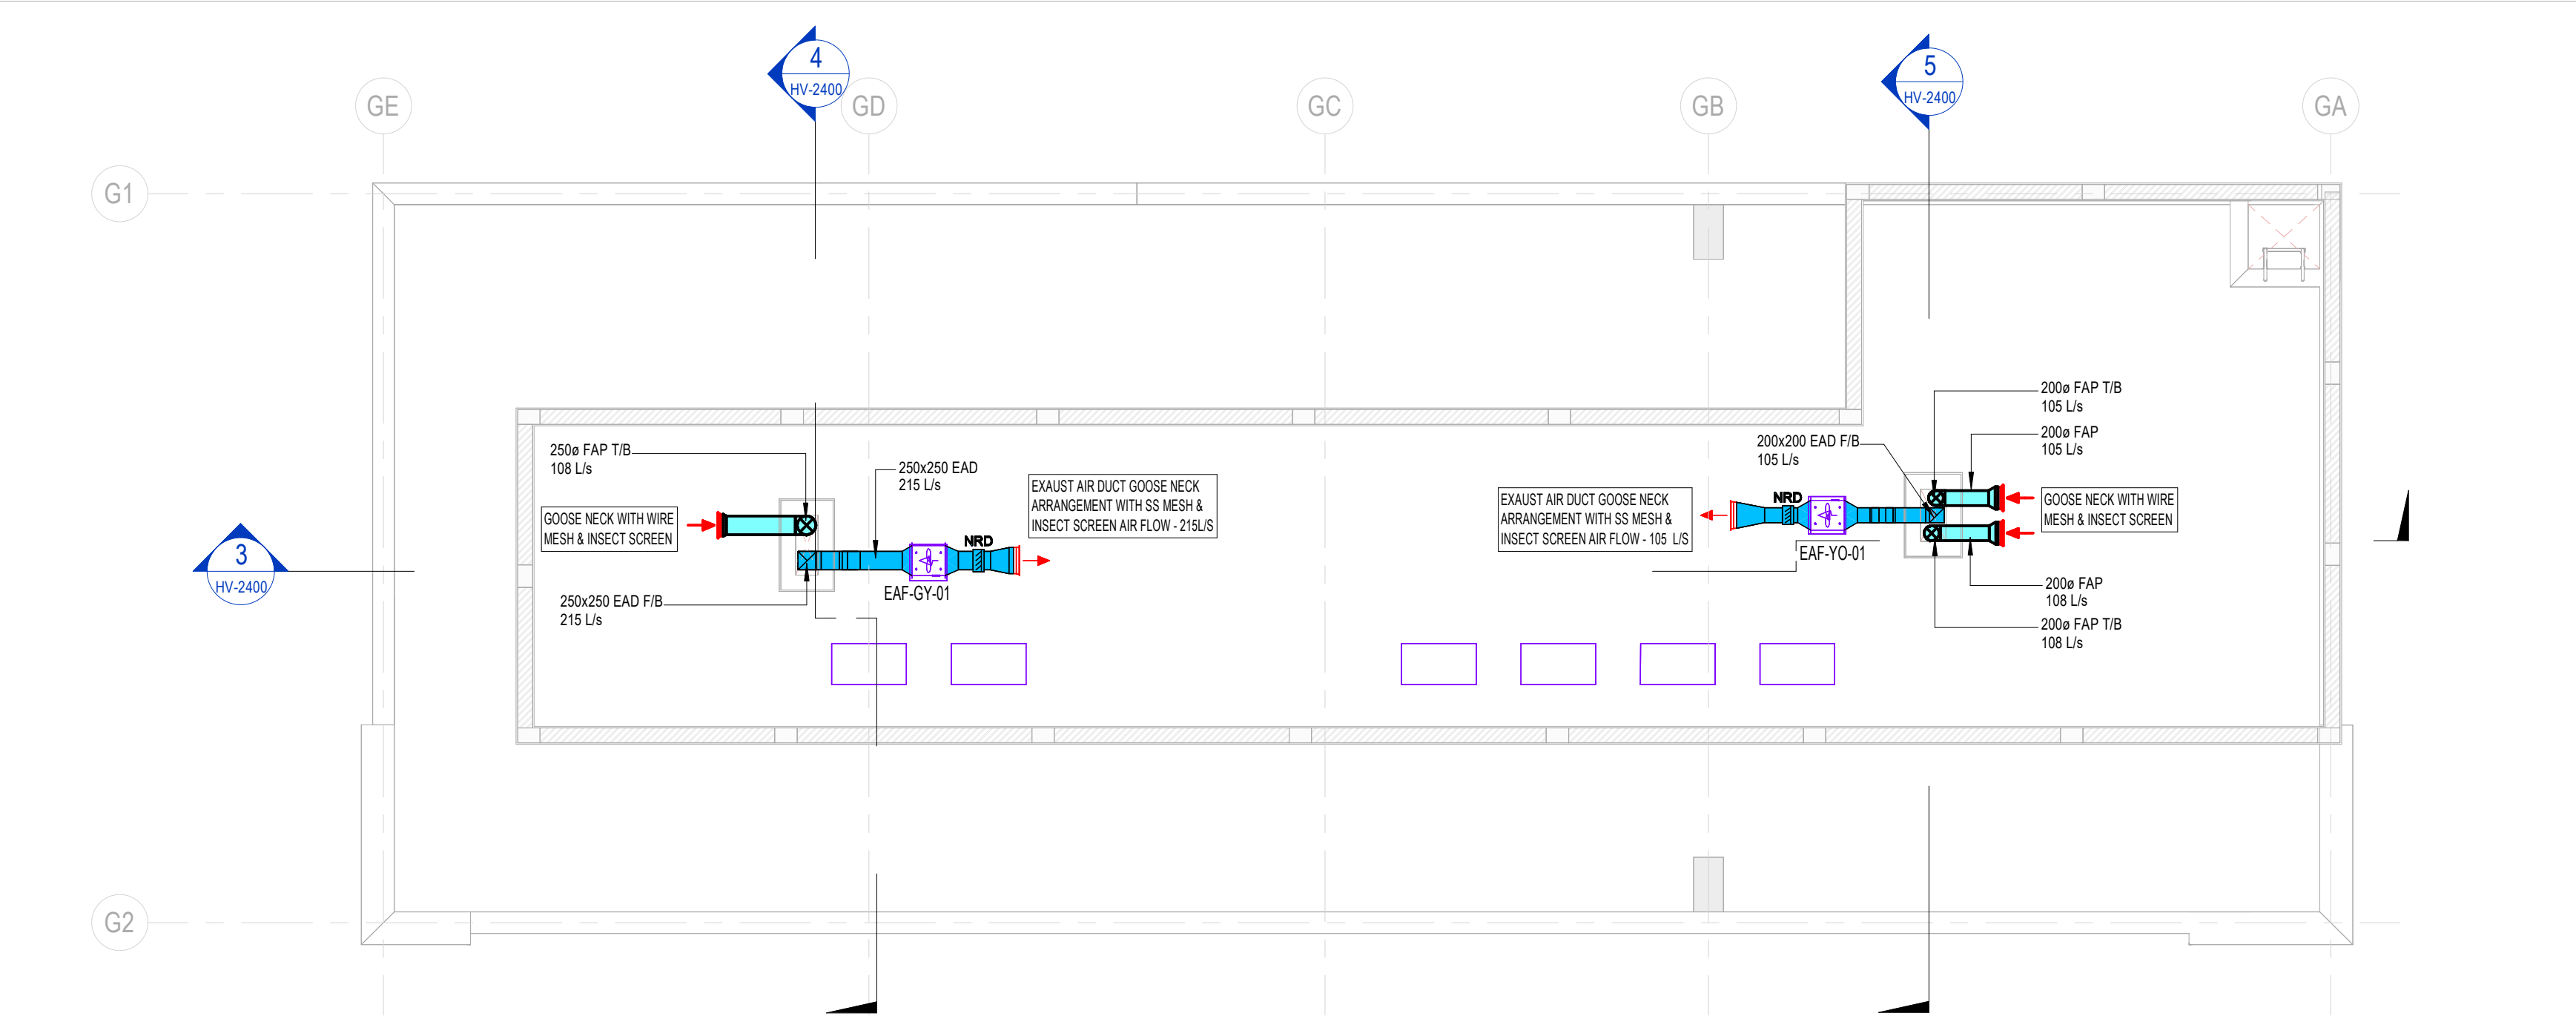

2 ROOF FLOOR VENTILATION LAYOUT-GYM&YOGA
1 : 75

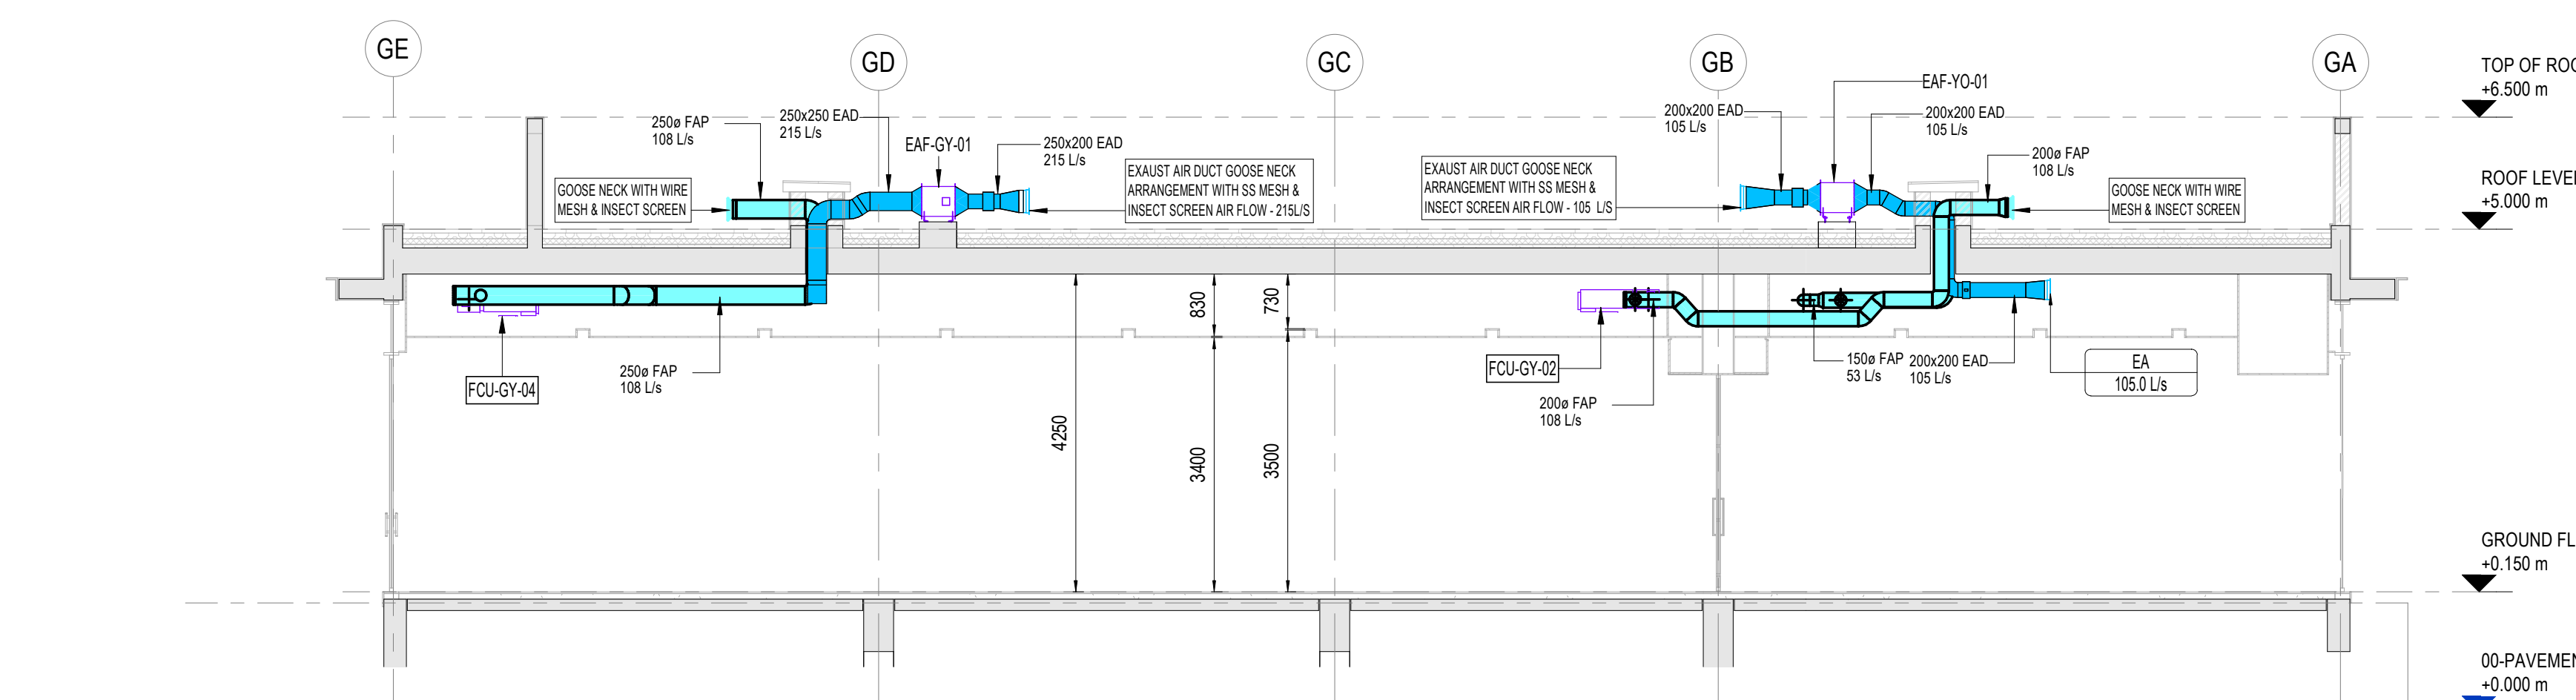


3 GYM&YOGA VENTILATION SECTION 01
1 : 75

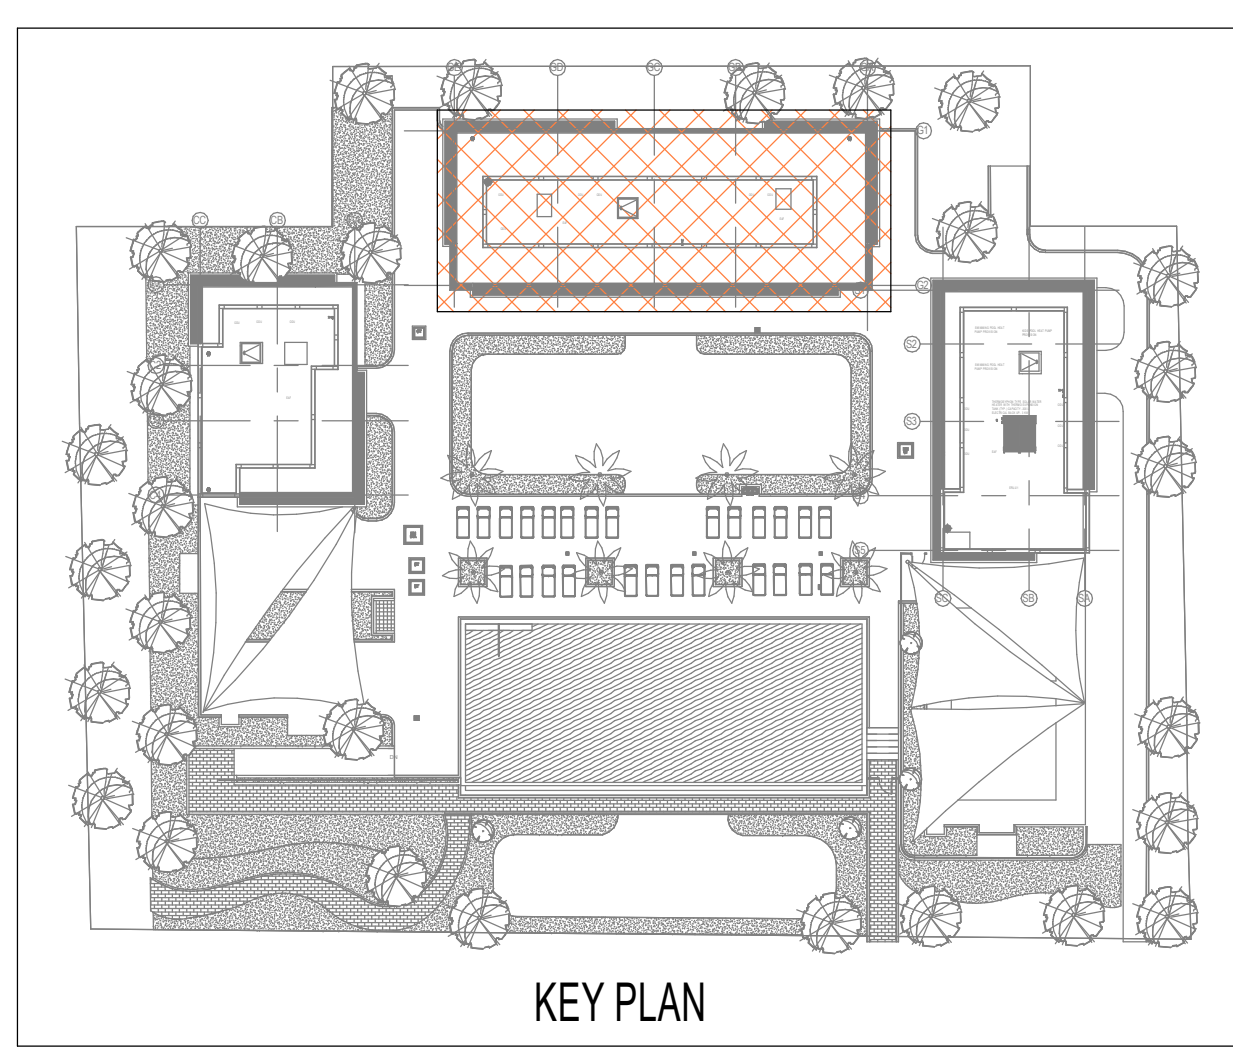


KEY PLAN

EXTRACT DISC. VALVE SCHEDULE			
UNIT NO.	DESCRIPTION	AIR OUTLET SIZE (mm)	CAPACITY RANGE (LPS)
EDV-01	EXTRACT DISC VALVE	Ø 100	0-12.5 L/s
EDV-02	EXTRACT DISC VALVE	Ø 200	12.5 -25 L/s

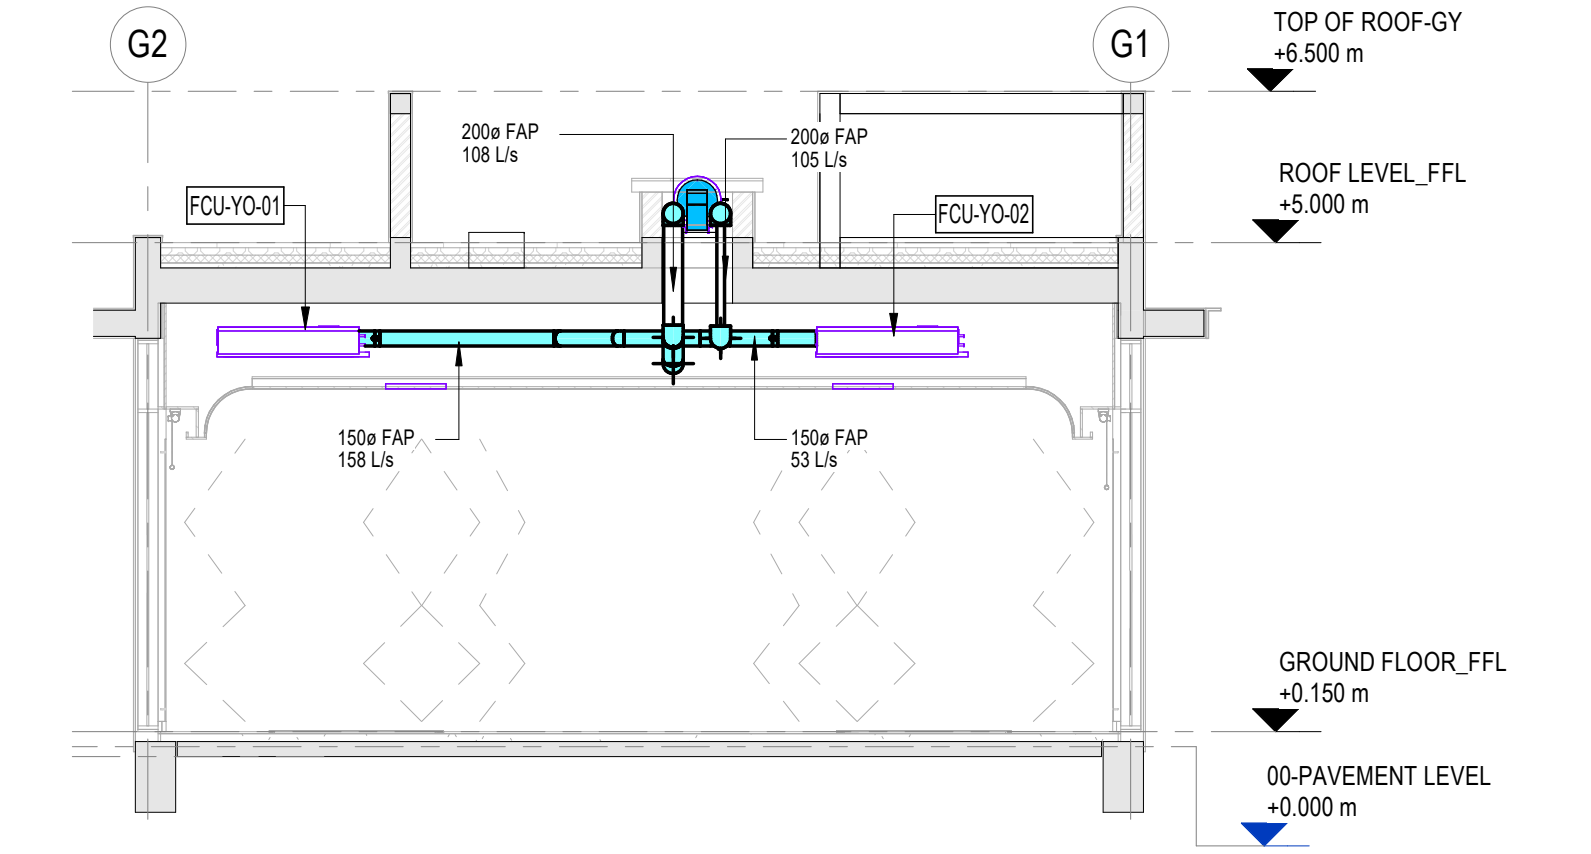

5 GYM&YOGA VENTILATION SECTION 03
1 : 75

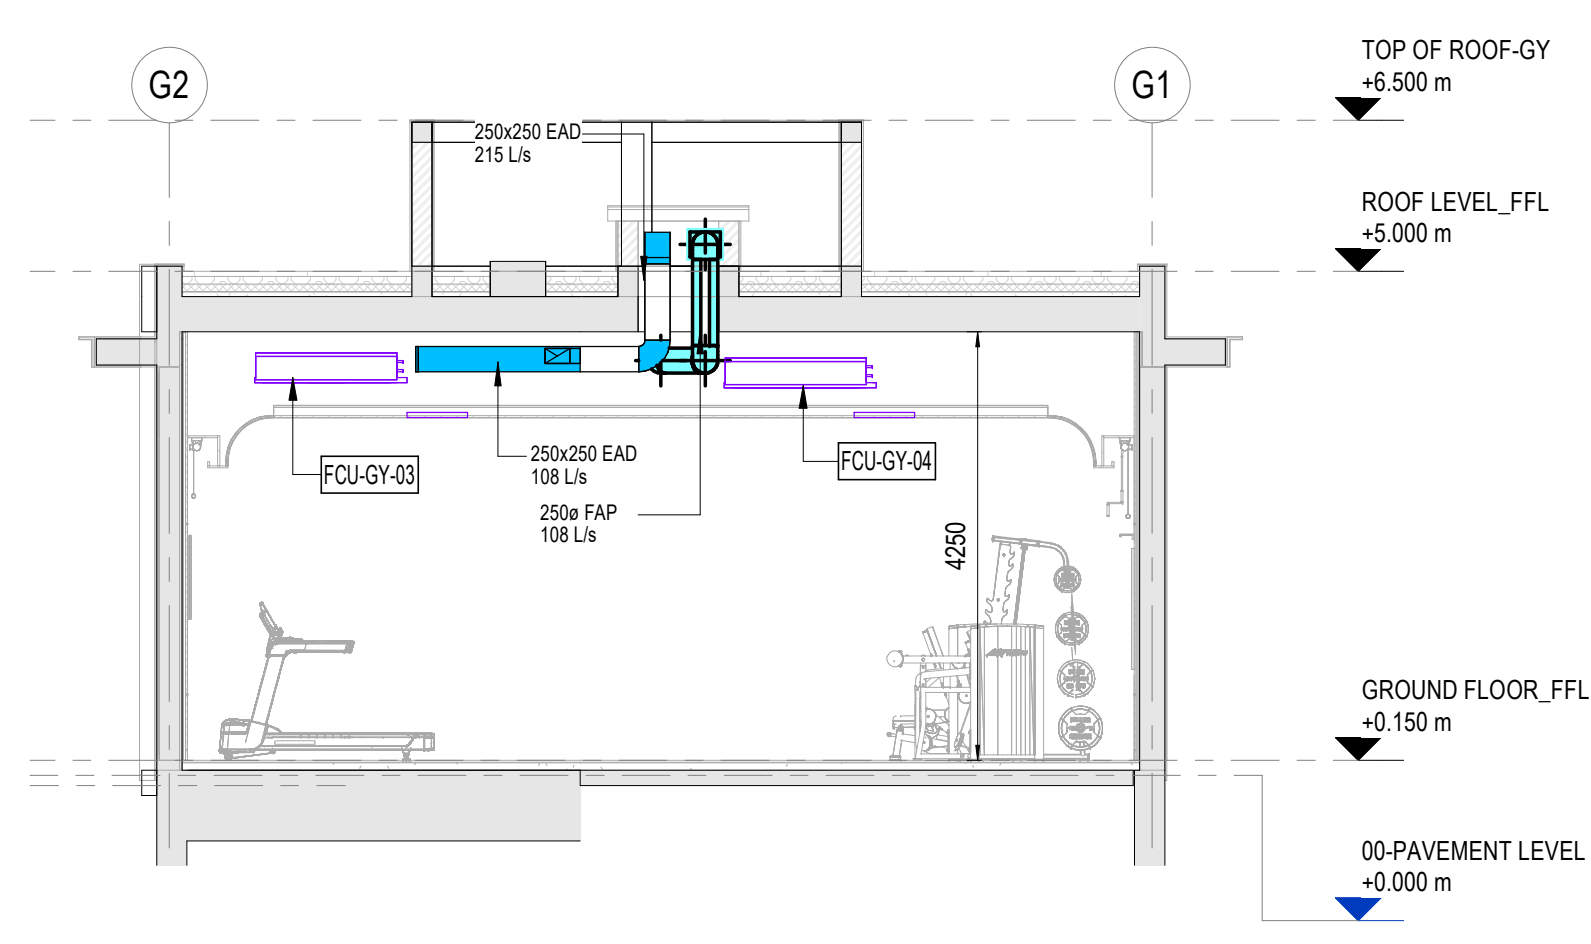

4 GYM&YOGA VENTILATION SECTION 02
1 : 75

Key Plan

General Notes :

- Do not Scale The Drawings. Follow (The MM) Written Dimensions Unless Otherwise Mentioned.
- Each Drawing Shall be Read in Conjunction With all Other Drawings Specification & the General Standard Details. In Case of Any Discrepancies Bring it to the Knowledge of Engineer and Same to be Resolved Prior to Execution of Work.
- Dimensions Shown on These Drawings are Structural Dimensions. Unless Noted Otherwise.
- All Levels Indicated On These Drawings are Levels as per the Survey Datum, Same Should be Verified at Site Prior to Execution of Work.
- All Levels Indicated On These Drawings are Based On Design Level, Which is Equivalent to Datum Level and Same Should be Verified at Site Prior to Execution of Work.

TENDER DRAWINGS

00 10/03/2026 LSG TENDER SUBMISSION

00 16/01/2026 LSG DETAILED DESIGN SUBMISSION

00 31/10/2025 LSG SCHEMATIC DESIGN SUBMISSION

00 15/10/2025 LSG SCHEMATIC SUBMISSION-50%

00 01/09/2025 LSG CONCEPT DESIGN SUBMISSION

No.	Date	Initials	Description
REVISIONS / ISSUE			
THIS DRAWING MUST NOT BE REPRODUCED IN WHOLE OR IN PART WITHOUT THE PRIOR APPROVAL OF ARIF & BINTOAK			
Status			
TENDER SUBMISSION			
Client			
EMAAR			
Lead Consultant			
Arif & Bint oak consulting architects & engineers POST BOX 5070 DUBAI, UAE TEL: 04-3372886 FAX: 04-3372832 POST BOX 5081 ABU DHABI, UAE TEL: 02-6566666 FAX: 02-6566666			
Project Title:			
Proposed Residential Townhouses and Standalone Villas TH-01, TH-02, and TH-03 at Grand Polo Club & Resort, Dubai, UAE			
Discipline:			
MECHANICAL			
Drawing title:			
GYM & YOGA GROUND & FIRST FLOOR VENTILATION LAYOUT			
Architectural Engineer			
Electrical Engineer			
Structural Engineer			
MUSTAFA ABID			
MARWAN MOHD.			
RIHAM RAMADAN			
Registration # 5847			
Registration # 60102			
Registration # 105892			
Scale(s):			
1 : 75			
Date:			
10/03/2026			
Project no:			
1857			
Drawn by:			
LSG			
Checked:			
MAV			
Approved:			
MRM			
Drawing Number:			
GPCR-TH01-AB-DRG-ZZZ-MEC-HV-2400-00			