




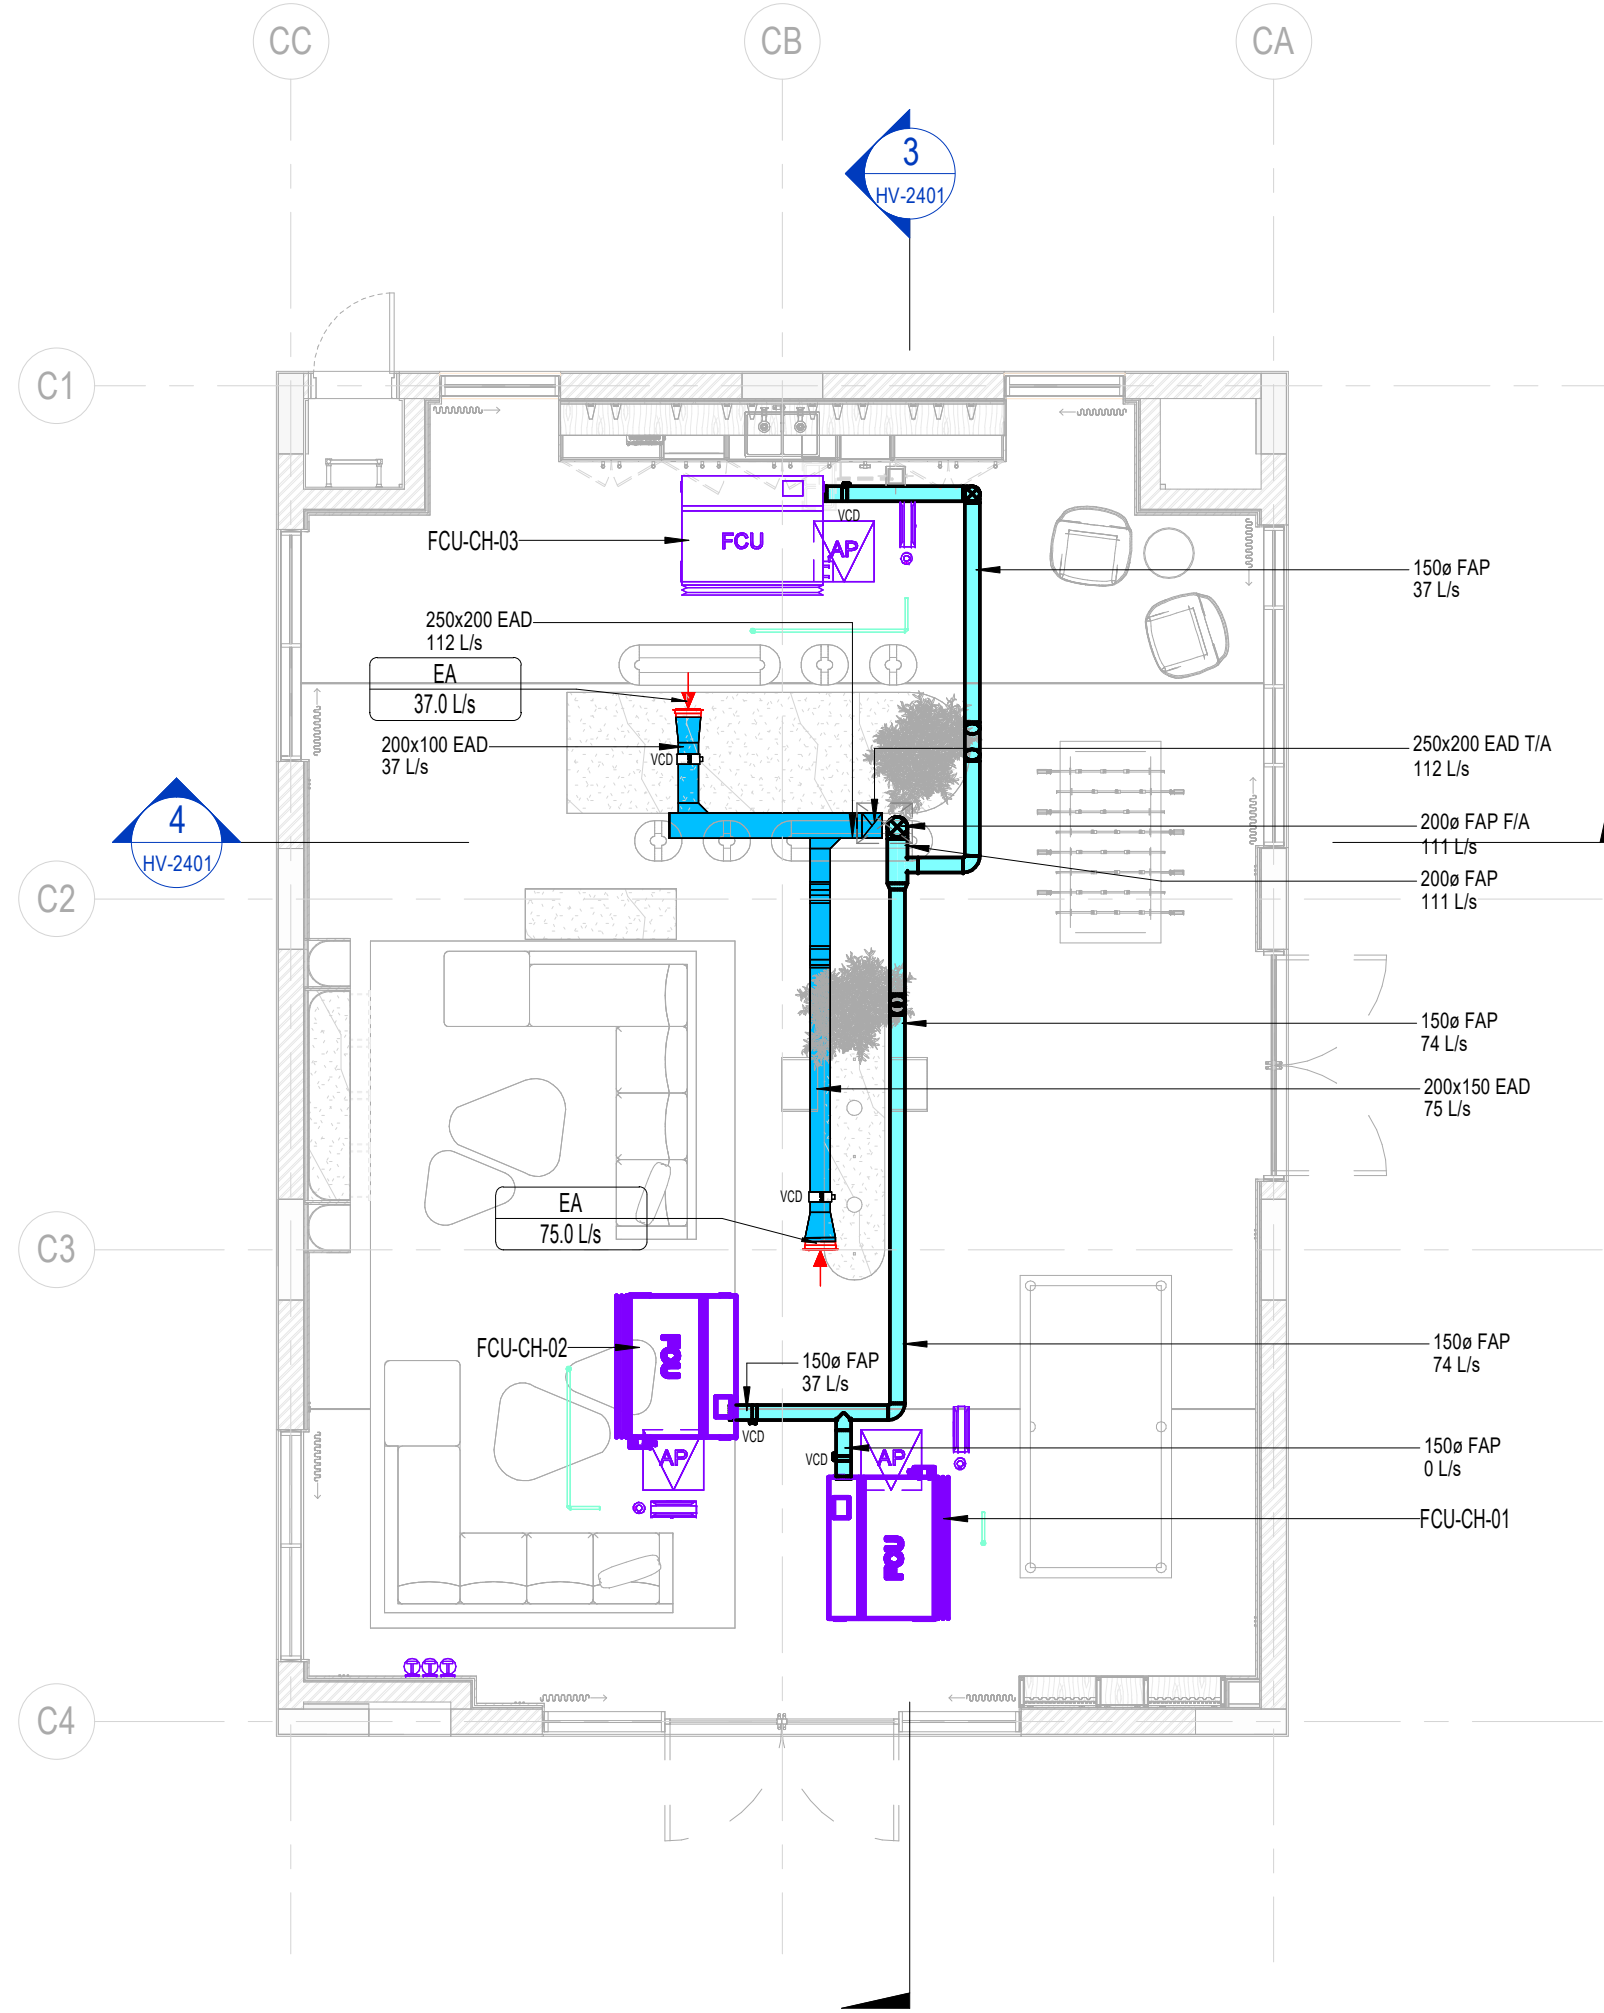


1 GROUND FLOOR VENTILATION LAYOUT-COMMUNITY HALL
1 : 75

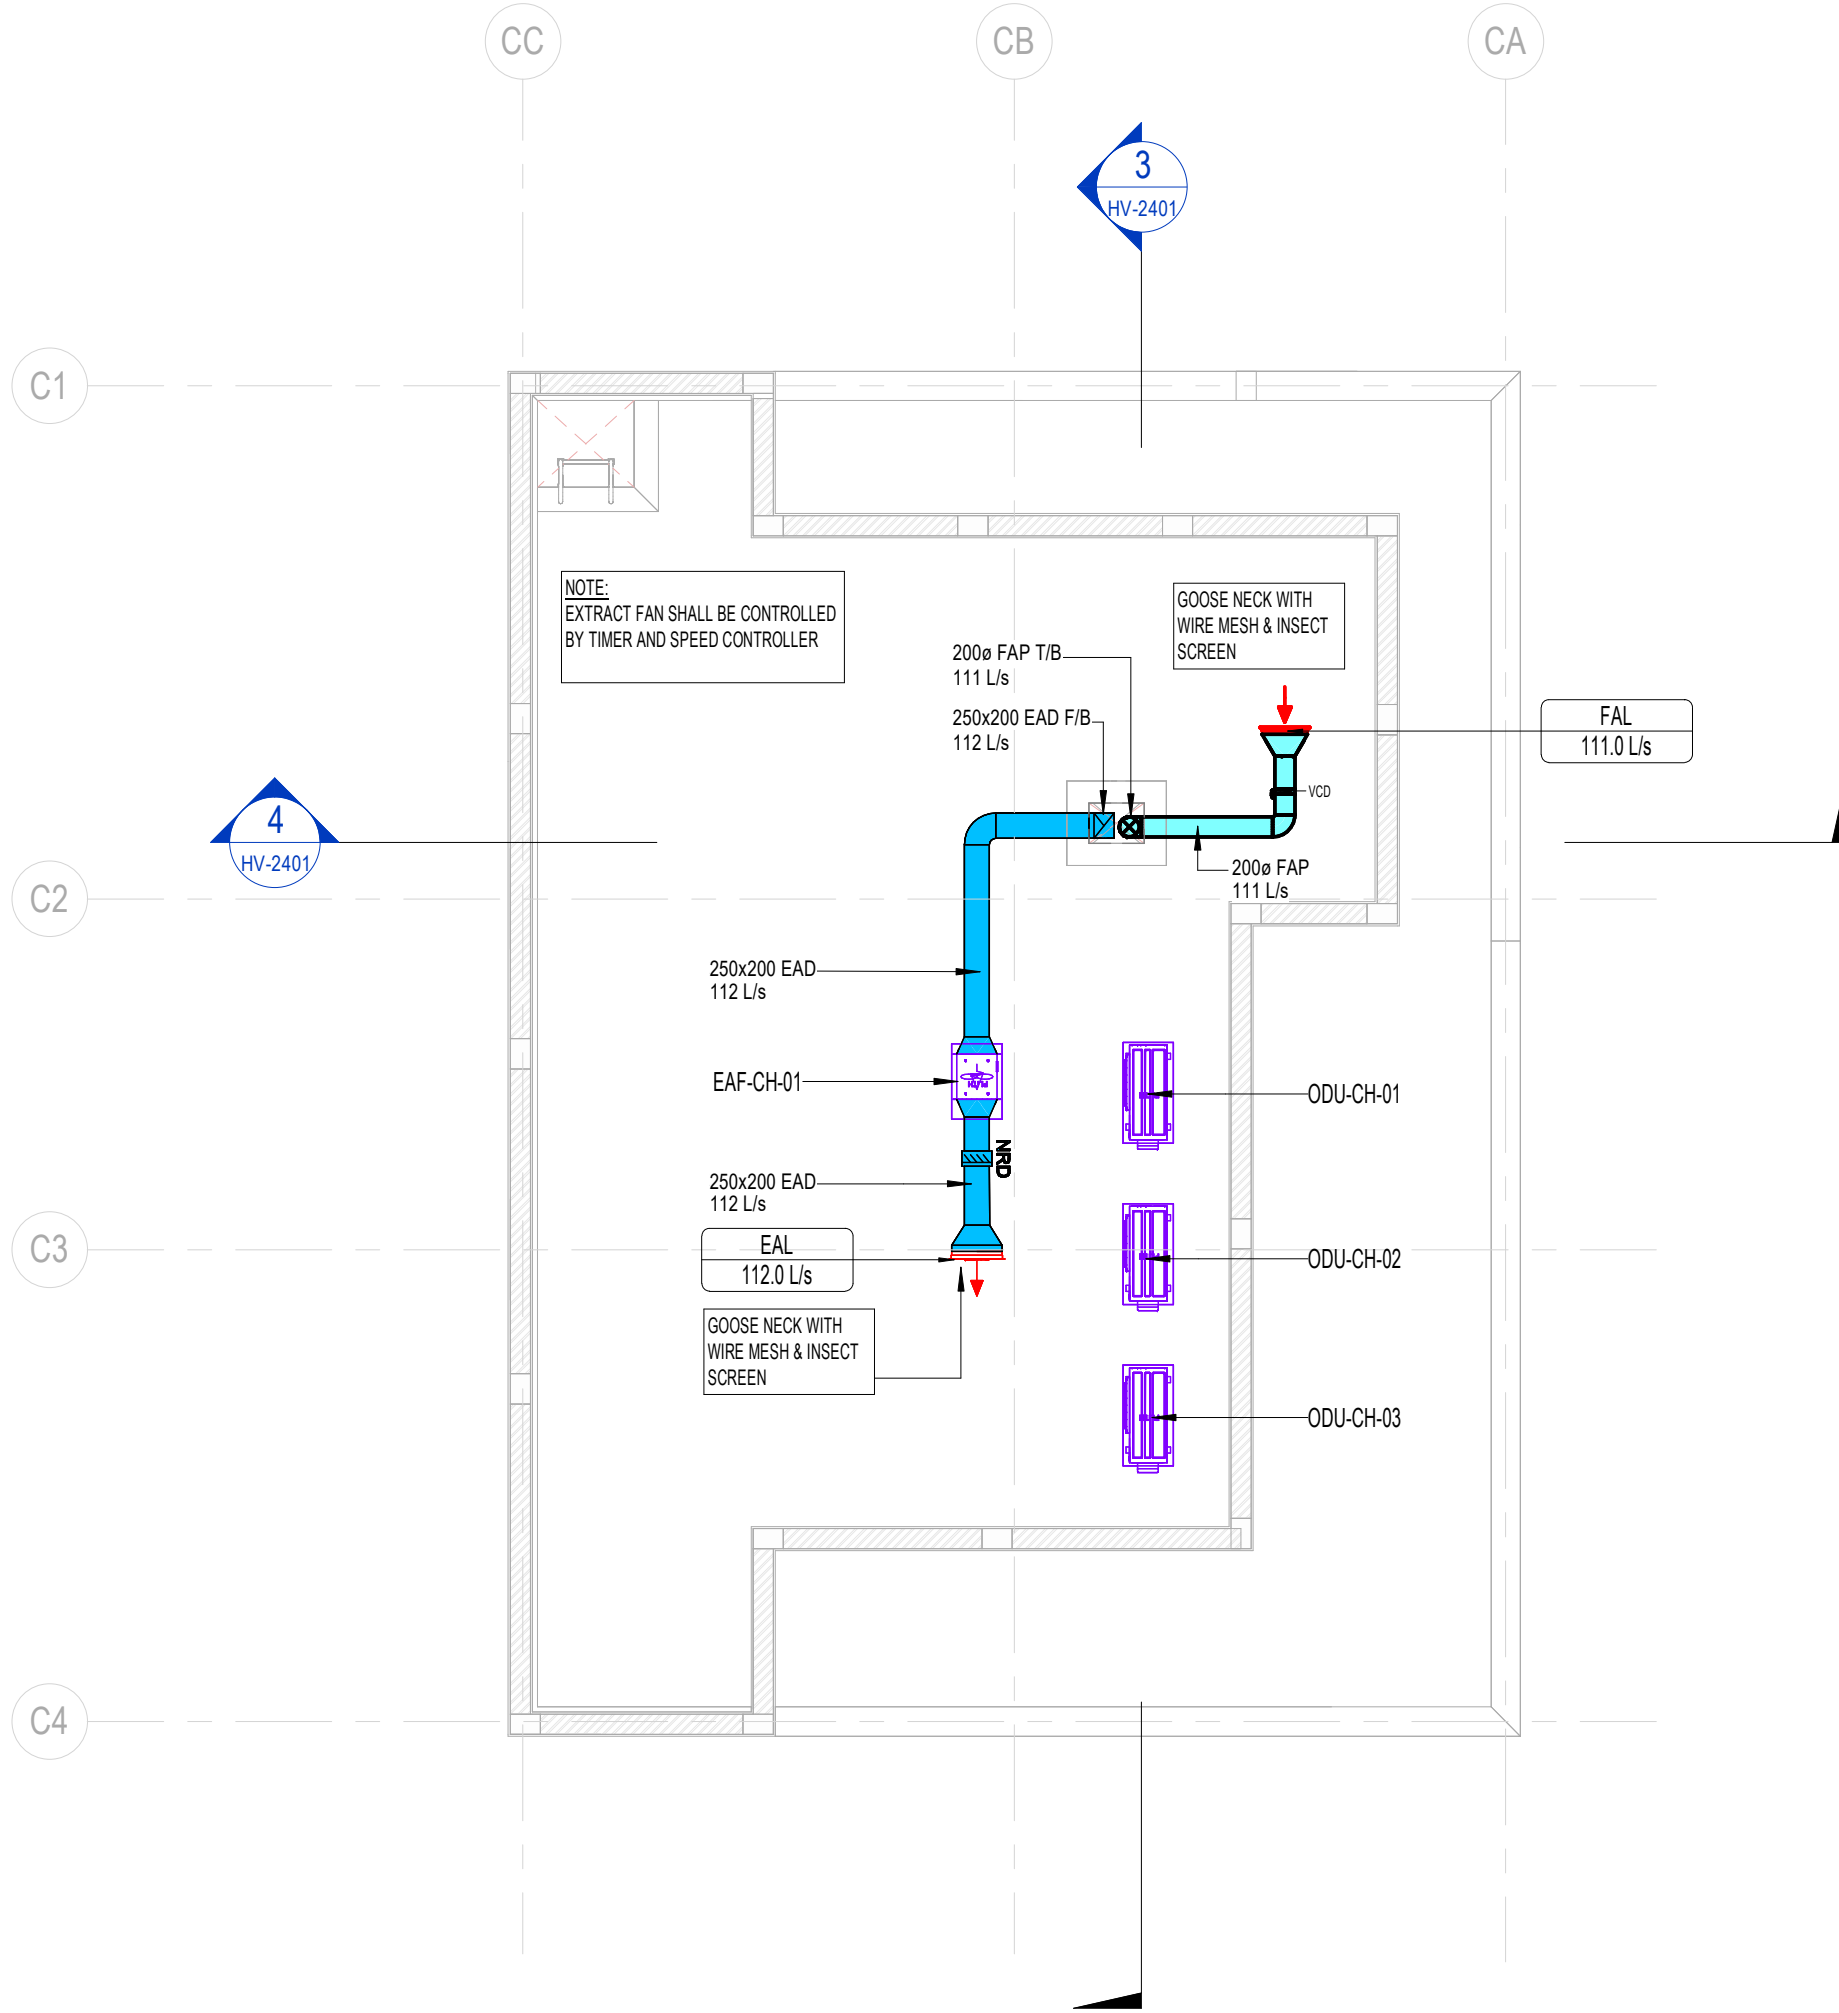


2 ROOF FLOOR VENTILATION LAYOUT-COMMUNITY HALL
1 : 75

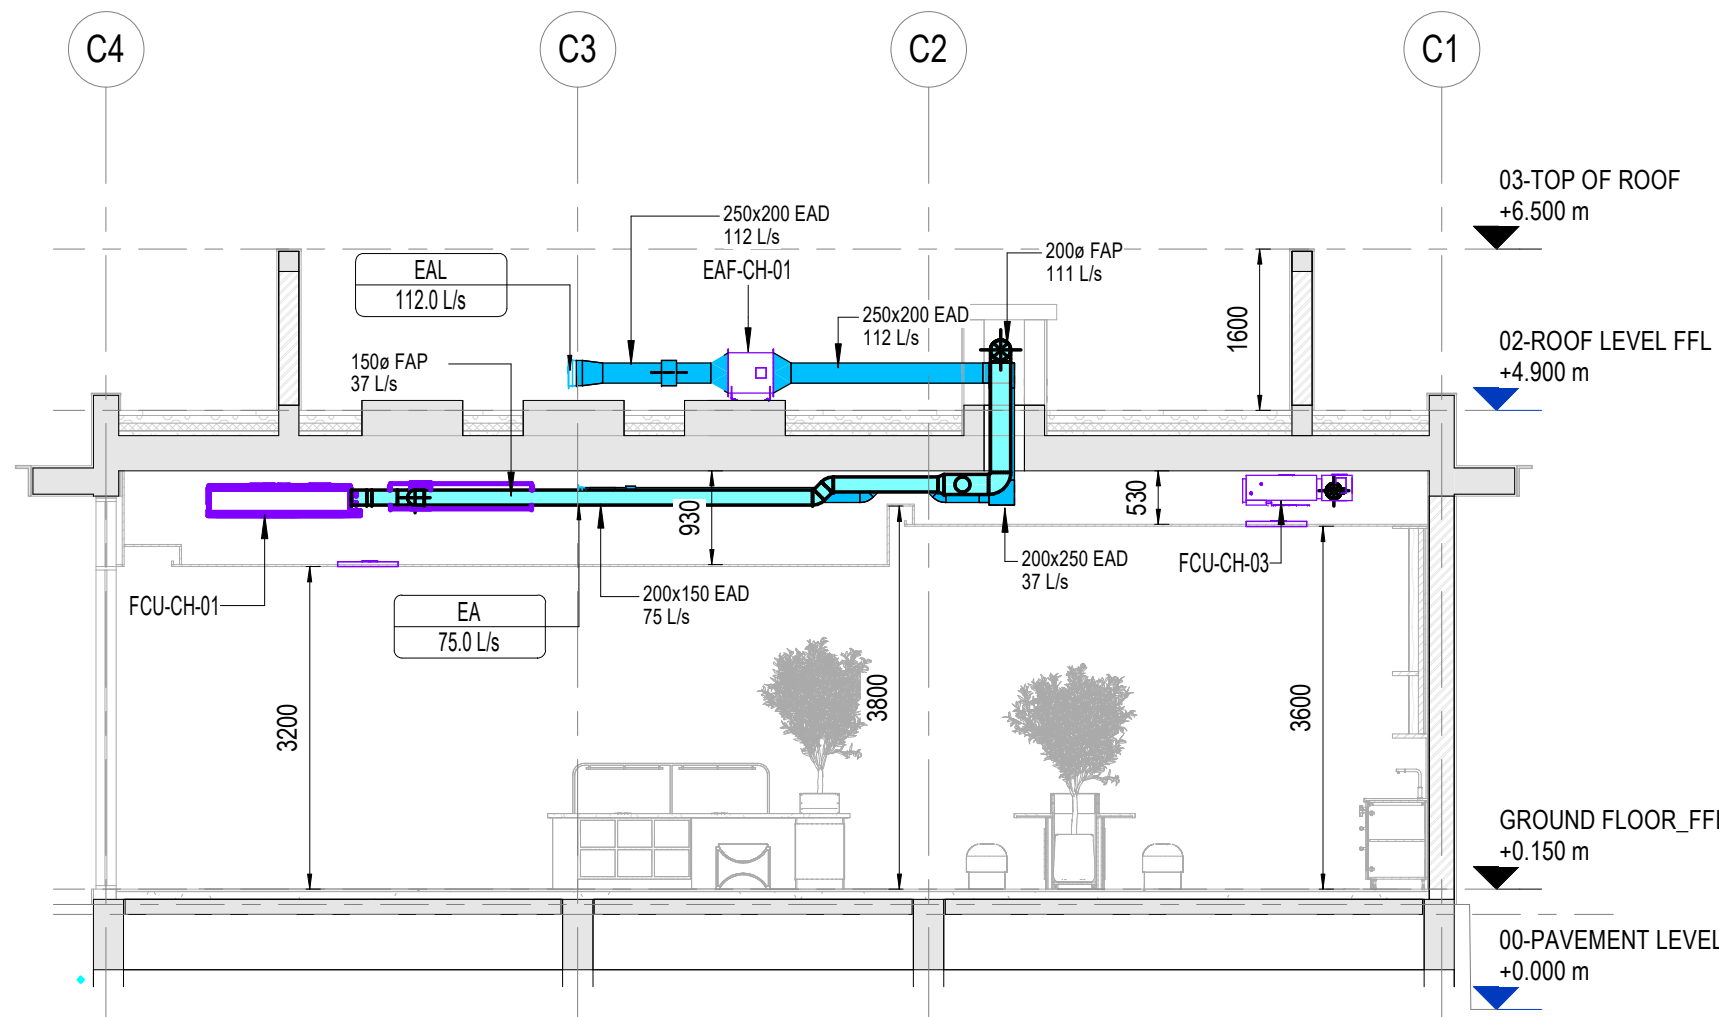

3 COMMUNITY HALL VENTILATION SECTION 01
1 : 75

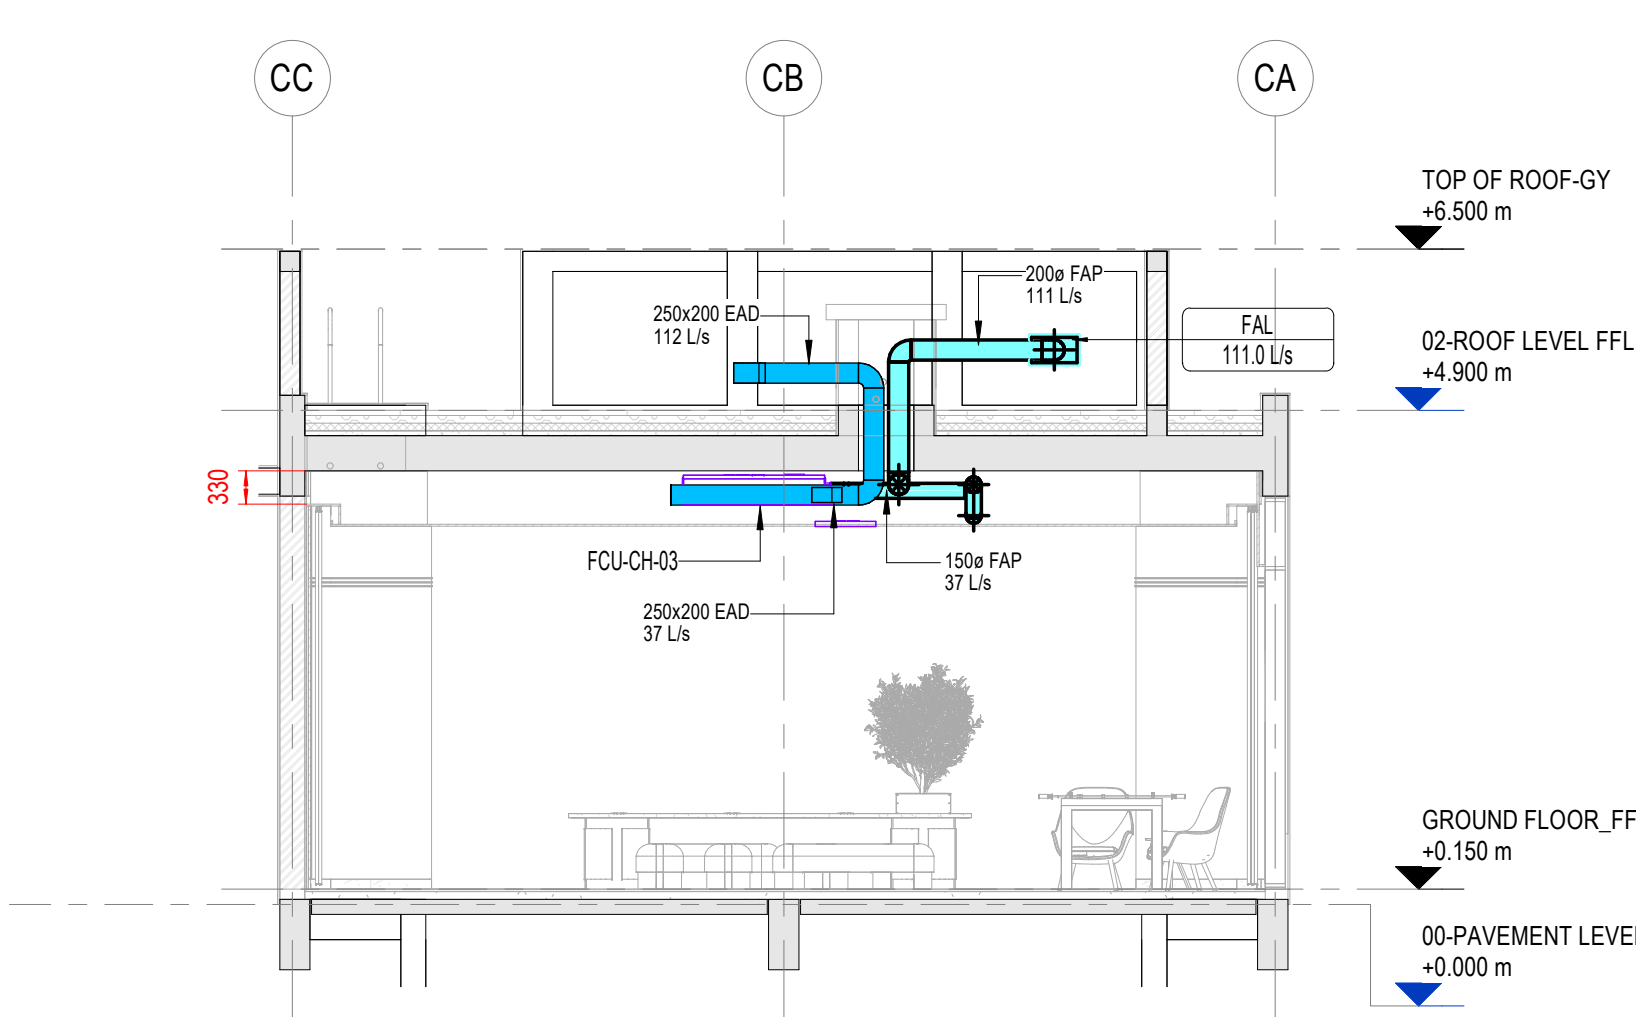


4 COMMUNITY HALL VENTILATION SECTION 02
1 : 75

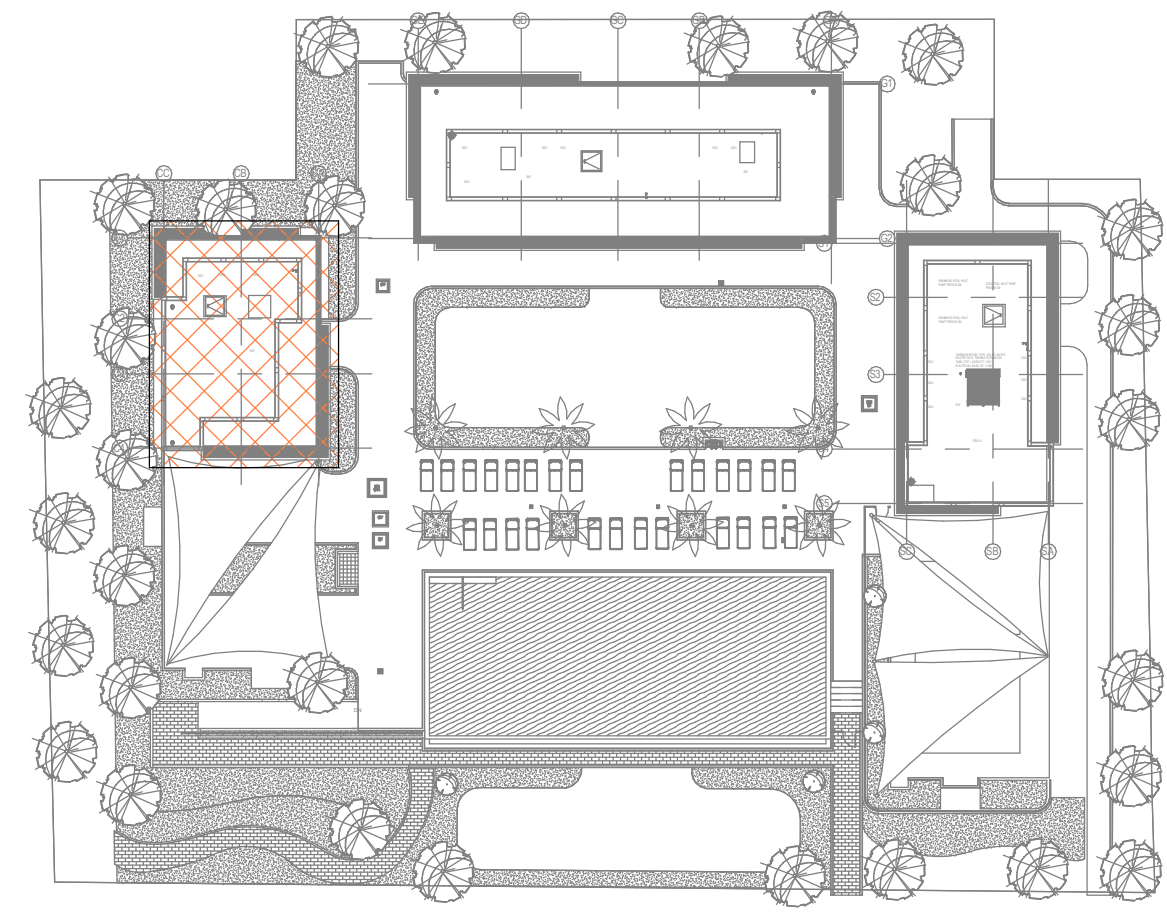

KEY PLAN

EXTRACT DISC VALVE SCHEDULE			
UNIT NO.	DESCRIPTION	AIR OUTLET SIZE (mm)	CAPACITY RANGE (LPS)
EDV-01	EXTRACT DISC VALVE	Ø 100	0 - 12.5 L/s
EDV-02	EXTRACT DISC VALVE	Ø 200	12.5 - 25 L/s

Key Plan

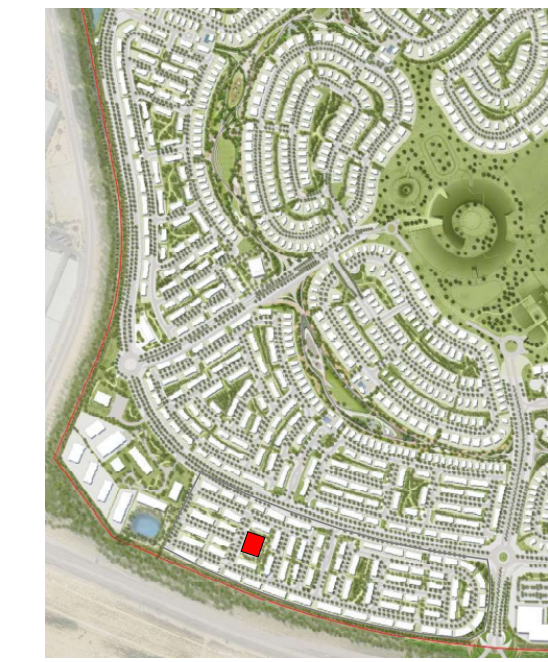

General Notes :

01. Do not Scale The Drawings. Follow (The MM) Written Dimensions Unless Otherwise Mentioned.
02. Each Drawing Shall be Read in Conjunction With all Other Drawings Specification & the General Standard Details. In Case of Any Discrepancies Bring it to the Knowledge of Engineer and Same to be Resolved Prior to Execution of Work.
03. Dimensions Shown on These Drawings are Structural Dimensions. Unless Noted Otherwise.
04. All Levels Indicated On These Drawings are Levels as per the Survey Datum, Same Should be Verified at Site Prior to Execution of Work.
05. All Levels Indicated On These Drawings are Based On Design Level, Which is Equivalent to Datum Level and Same Should be Verified at Site Prior to Execution of Work.



No.	Date	Initials	Description
00	10/03/2026	LSG	TENDER SUBMISSION
00	16/01/2026	LSG	DETAILED DESIGN SUBMISSION
00	31/10/2025	LSG	SCHEMATIC DESIGN SUBMISSION
00	15/10/2025	LSG	SCHEMATIC SUBMISSION-50%
00	01/09/2025	LSG	CONCEPT DESIGN SUBMISSION

REVISIONS / ISSUE

THIS DRAWING MUST NOT BE REPRODUCED IN WHOLE OR IN PART WITHOUT THE PRIOR APPROVAL OF ARIF & BINTOAK

TENDER SUBMISSION

Client

EMAAR

Lead Consultant



Project Title:

Proposed Residential Townhouses and Standalone Villas TH-01, TH-02, and TH-03 at Grand Polo Club & Resort, Dubai, UAE

Discipline:

MECHANICAL

Drawing title:

COMMUNITY HALL GROUND & FIRST FLOOR VENTILATION LAYOUT

Architectural Engineer

MUSTAFA ABID

Electrical Engineer

MARWAN MOHD.

Structural Engineer

RIHAM RAMADAN

Registration # 5847

Registration # 60102

Registration # 105892

Scale(s):

1 : 75

Date:

10/03/2026

Project no:

1857

Drawn by:

LSG

Checked:

MAV

Approved:

MRM

Drawing Number:

GPCR-TH01-AB-DRG-ZZZ-MEC-HV-2401-00