


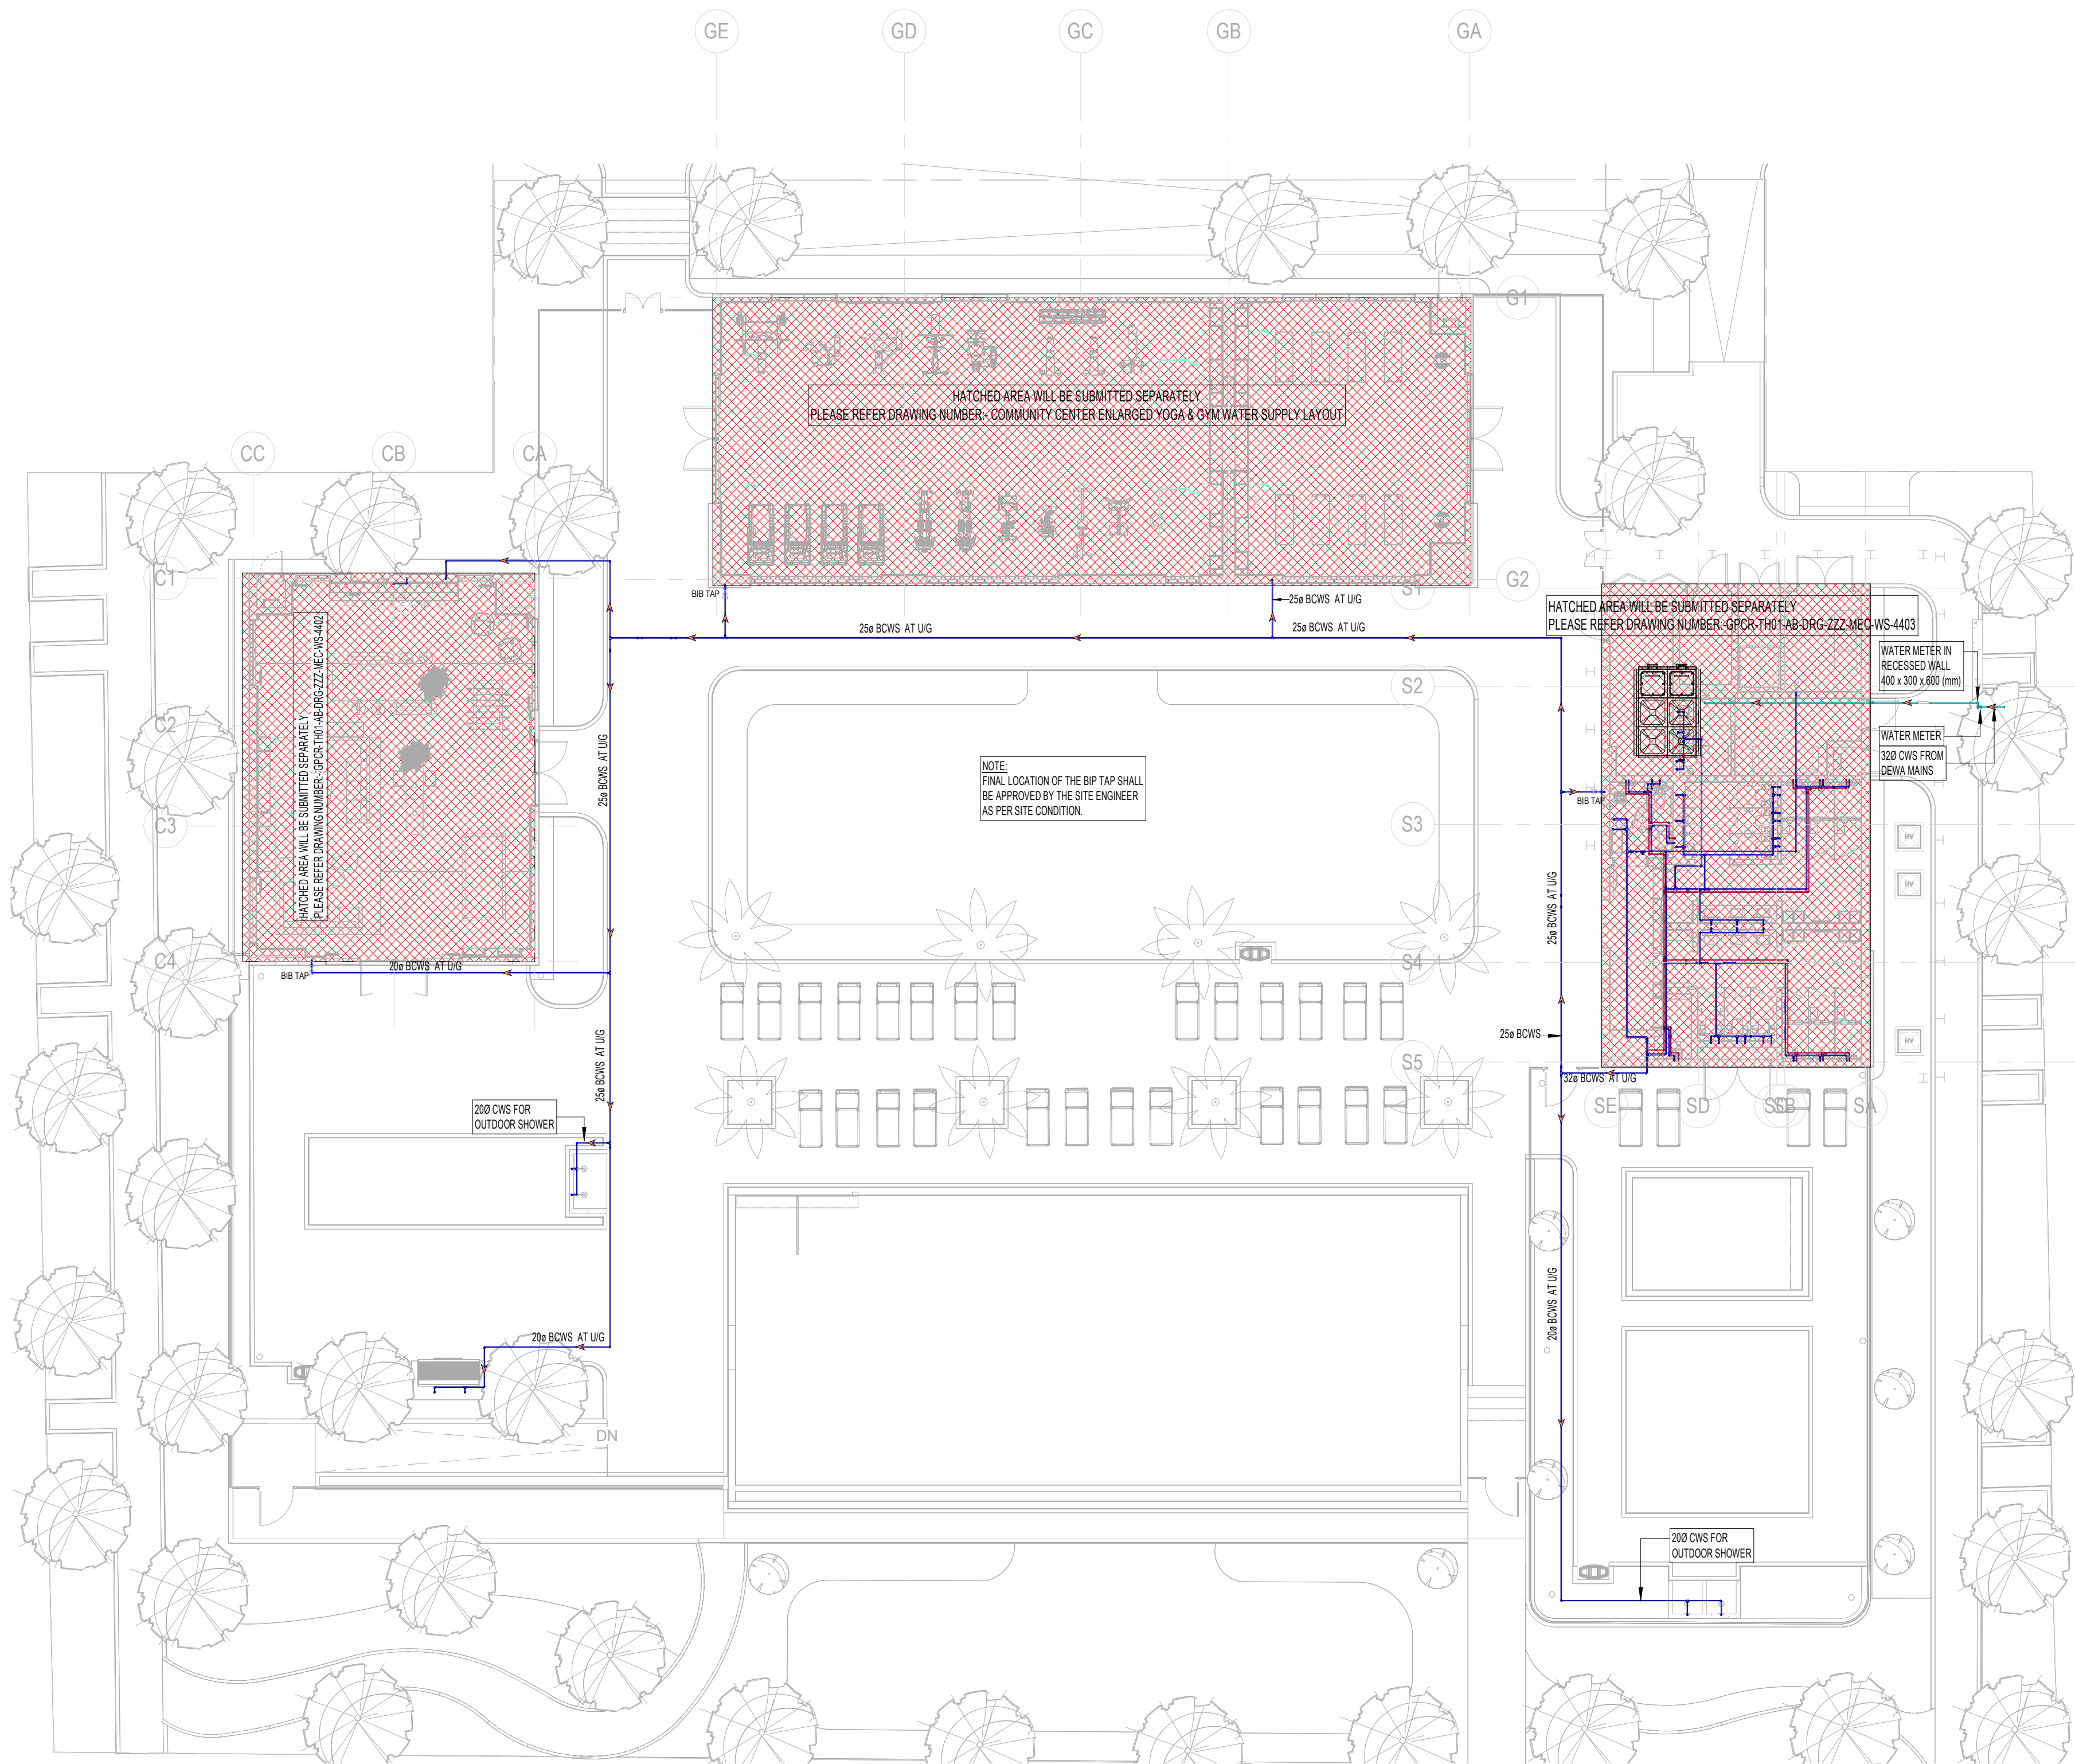


1 OVERALL GROUND FLOOR WATER SUPPLY LAYOUT
1 : 150

NOTE :
THE PIPE SIZES ON DRAWINGS ARE BASED ON
NOMINAL INTERNAL DIAMETER OF PPR PIPES
CONTRACTOR TO PROVIDE OUTSIDE PPR PIPES
DIAMETER ON SHOP DRAWINGS.
EXTERNAL BIP/TAP SHALL BE LOCKABLE TYPE.

LEGENDS	
CWS	COLD WATER SUPPLY
HWS	HOT WATER SUPPLY
GCWS	GRAVITY COLD WATER SUPPLY
BCWS	BOOSTER COLD WATER SUPPLY
CWTP	COLD WATER TRANSFER PIPE
WHA	WATER HAMMER ARRESTER
EWB	ELECTRIC WATER HEATER
IV	ISOLATING VALVE
DRV	DOUBLE REGULATING VALVE
NRV	NON RETURN VALVE
ST	STRAINER
NC	NORMALLY CLOSED VALVE
NO	NORMALLY OPENED VALVE
WM	WATER METER
BFP	BACK FLOW PREVENTER
TMV	THERMOSTAT MIXING VALVE
FA	FROM ABOVE
FB	FROM BELOW
TA	TO ABOVE
TB	TO BELOW
FB TA	FROM BELOW TO ABOVE
FA TB	FROM ABOVE TO BELOW
DTLL	DOWN TO LOW LEVEL
RTHL	RISE TO HIGH LEVEL
	BOOSTER PUMP SET (1DUTY+1STANDBY)

PLUMBING FIXTURES FLOW	
FIXTURE TYPE	MAXIMUM FLOW RATE
SHOWERHEADS	8 L/Min.
HAND WASHBASINS	6 L/Min.
KITCHEN SINKS	7 L/Min.
DUEL FLUSH TOILETS	6 L Full Flush 3 L Part Flush

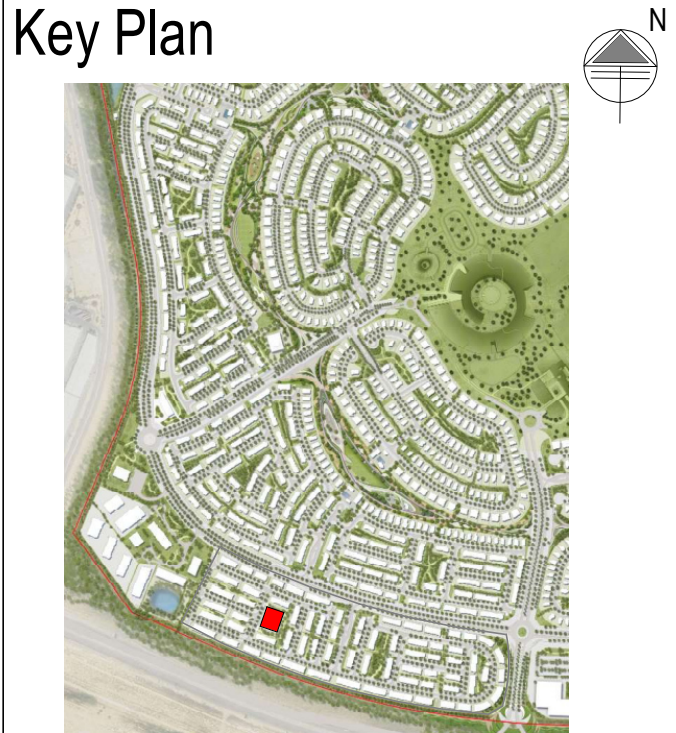

- General Notes :**
- Do not Scale The Drawings. Follow (The MM) Written Dimensions Unless Otherwise Mentioned.
 - Each Drawing Shall be Read in Conjunction With all Other Drawings Specification & the General Standard Details. In Case of Any Discrepancies Bring it to the Knowledge of Engineer and Same to be Resolved Prior to Execution of Work.
 - Dimensions Shown on These Drawings are Structural Dimensions. Unless Noted Otherwise.
 - All Levels Indicated On These Drawings are Levels as per the the Survey Datum, Same Should be Verified at Site Prior to Execution of Work.
 - All Levels Indicated On These Drawings are Based On Design Level, Which is Equivalent to Datum Level and Same Should be Verified at Site Prior to Execution of Work.



00	10/03/2026	LSG	TENDER SUBMISSION
00	16/01/2026	LSG	DETAILED DESIGN SUBMISSION
00	31/10/2025	LSG	SCHEMATIC DESIGN SUBMISSION
00	15/10/2025	LSG	SCHEMATIC SUBMISSION-50%
00	01/09/2025	LSG	CONCEPT DESIGN SUBMISSION

No.	Date	Initials	Description
REVISIONS / ISSUE			
THIS DRAWING MUST NOT BE REPRODUCED IN WHOLE OR IN PART WITHOUT THE PRIOR APPROVAL OF ARIF & BINTOAK			

Status: TENDER SUBMISSION

Client: EMAAR

Lead Consultant:

المستشارون:
عارف وبن طوق
Arif & Bint oak
consulting architects & engineers
POST BOX 5070 DUBAI, UAE TEL: 04-3372886 FAX: 04-3372832
POST BOX 42081 ABU DHABI, UAE TEL: 02-6246605 arif@arifbintoak.com.ae

Project Title: Proposed Residential Townhouses and Standalone Villas
TH-01, TH-02, and TH-03 at Grand Polo Club & Resort,
Dubai, UAE

Discipline: MECHANICAL

Drawing title:
**OVERALL GROUND FLOOR
COMMUNITY CENTER
WATER SUPPLY LAYOUT**

Architectural Engineer	Electrical Engineer	Structural Engineer
MUSTAFA ABID	MARWAN MOHD.	RIHAM RAMADAN
Registration # 5847	Registration # 80102	Registration # 105892
Scale(s): As indicated	Date: 10/03/2026	Project no: 1857
Drawn by: LSG	Checked: MAV	Approved: MRM

Drawing Number: GPCR-TH01-AB-DRG-ZZZ-MEC-WS-4400-00