



This 2D drawing is extracted from 3D BIM Model

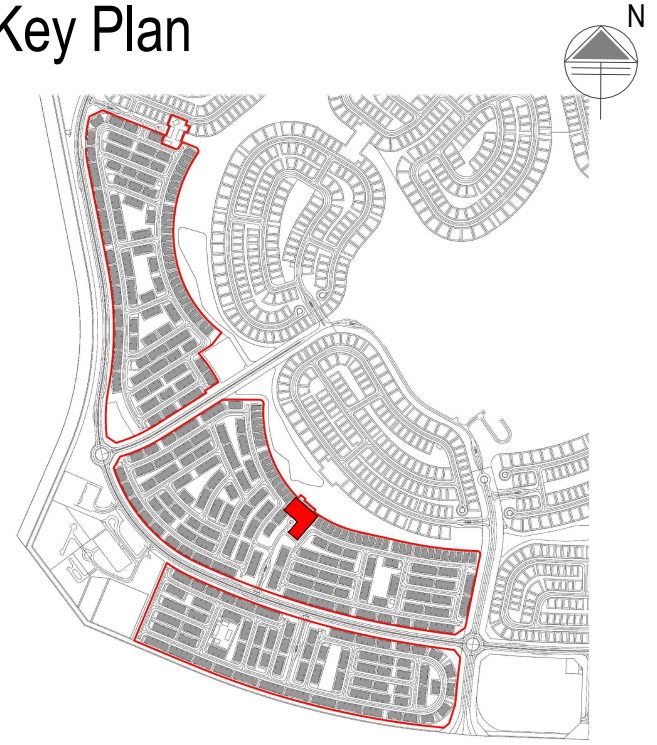

- General Notes :**
01. Do not Scale The Drawings. Follow (The MM) Written Dimensions Unless Otherwise Mentioned.
 02. Each Drawing Shall be Read in Conjunction With all Other Drawings, Specification & the General Standard Details. In Case of Any Discrepancies Bring it to the Knowledge of Engineer and Same to be Resolved Prior to Execution of Work.
 03. Dimensions Shown on These Drawings are Structural Dimensions Unless Noted Otherwise.
 04. All Levels Indicated On These Drawings are Levels as per the the Survey Datum, Same Should be Verified at Site Prior to Execution of Work.
 05. All Levels Indicated On These Drawings are Based On Design Level, Which is Equivalent to Datum Level and Same Should be Verified at Site Prior to Execution of Work.

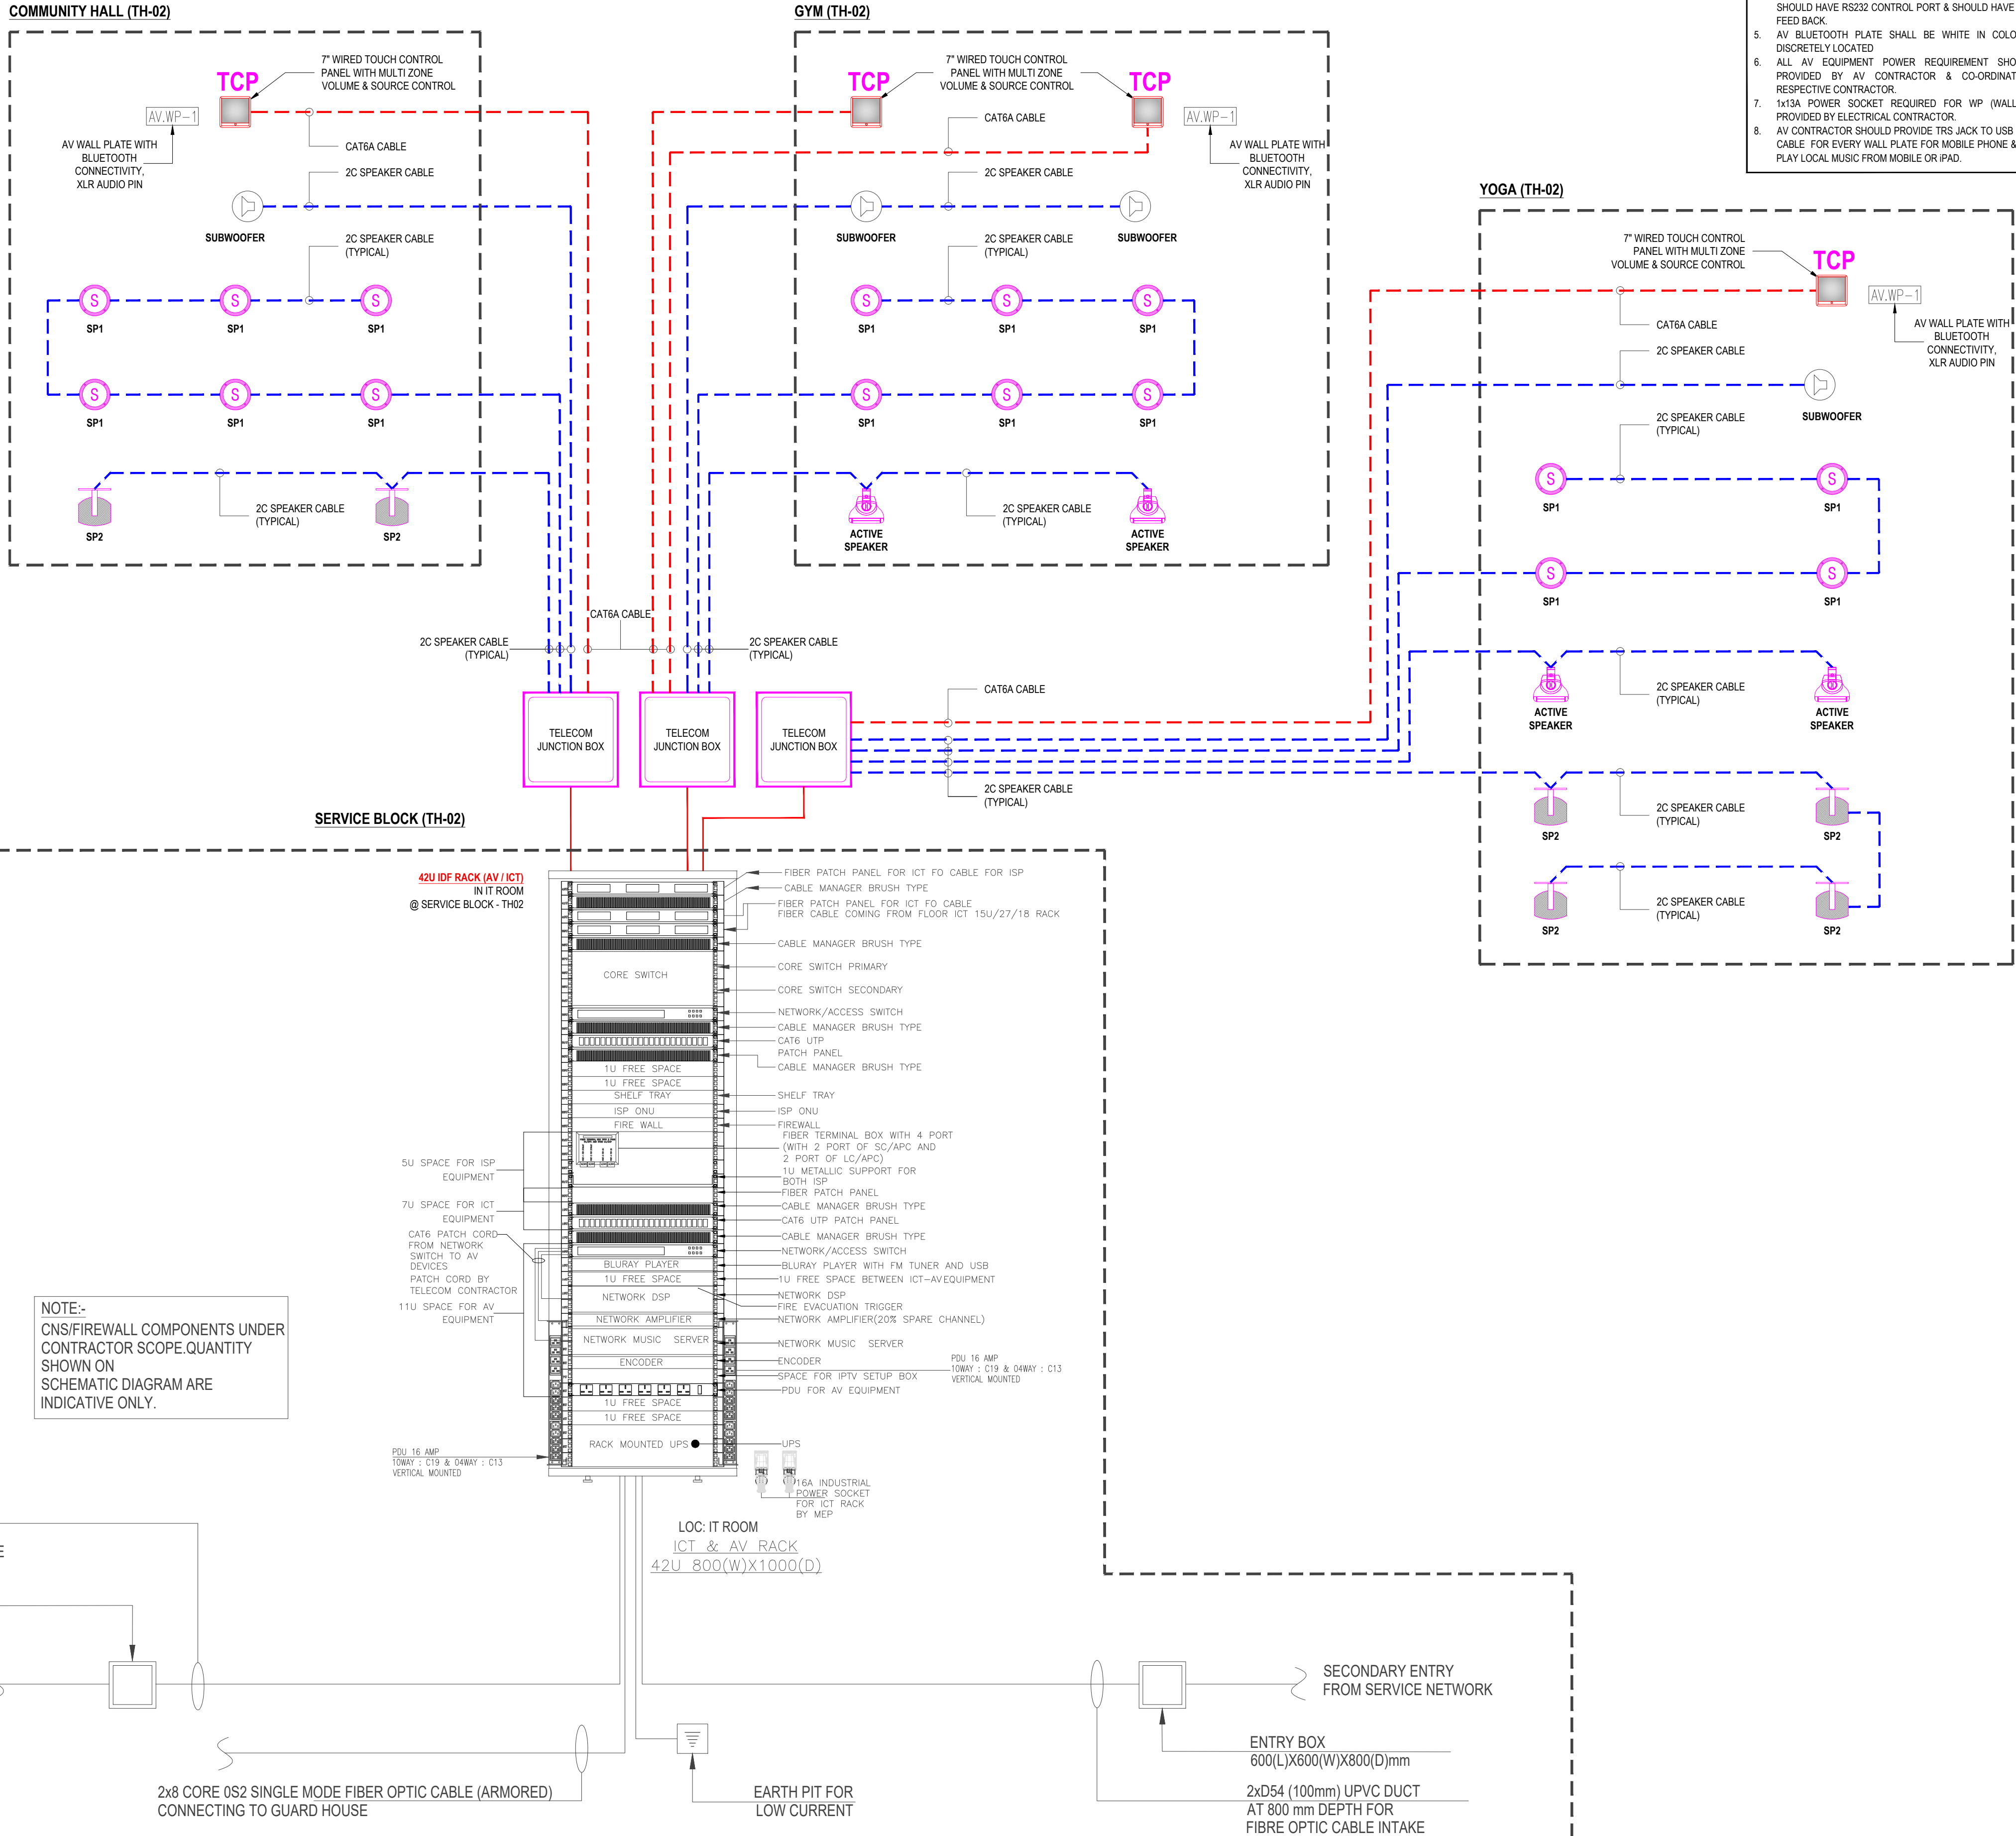

No.	09	Date	10/03/2026	Initials	JP	Description	TENDER SUBMISSION
REVISIONS / ISSUE							
THIS DRAWING MUST NOT BE REPRODUCED IN WHOLE OR IN PART WITHOUT THE PRIOR APPROVAL OF ARIF & BINTOAK							
Status	TENDER SUBMISSION						
Client	EMAAR						
Lead Consultant	عارف وبن طوق Arif & Bintok consulting architects & engineers POST BOX 3676 DUBAI UAE TEL: 84-3272888 FAX: 84-3273552 POST BOX 42981 ABU DHABI UAE TEL: 62-434669 -aribintok@emaar.ae						
Security Consultant	INTERNATIONAL ELECTRONIC SECURITY TEL: 04 397 0757, FAX: 04 397 0754 P.O. BOX 12734 DUBAI - U.A.E ENQUIRIES@IESCONSULTING.AE AUDIT@IESCONSULTING.AE WWW.IESCONSULTING.AE						

Project Title:

Proposed Residential Townhouses and Standalone Villas TH-1, TH-2, and TH-3 at Grand Polo Club & Resort, Dubai, UAE

Discipline :	AUDIO VISUAL (AV)		
Drawing title:	BGM SYSTEM SINGLE LINE DIAGRAM COMMUNITY CENTER - TH-02		
Architectural Engineer	Electrical Engineer	Structural Engineer	
MUSTAFA ABID	MARWAN MOHD.	RIHAM RAMADAN	
Registration # 5847	Registration # 80102	Registration # 105092	
Scale(s):	Date drawn: 10/03/2026	Project no: 1857	
Drawn by: JP	Checked: MM	Approved: JR	
Drawing Number :	GPCR-TH02-IES-CC2-SLD-AVC-AV-2000-00		