


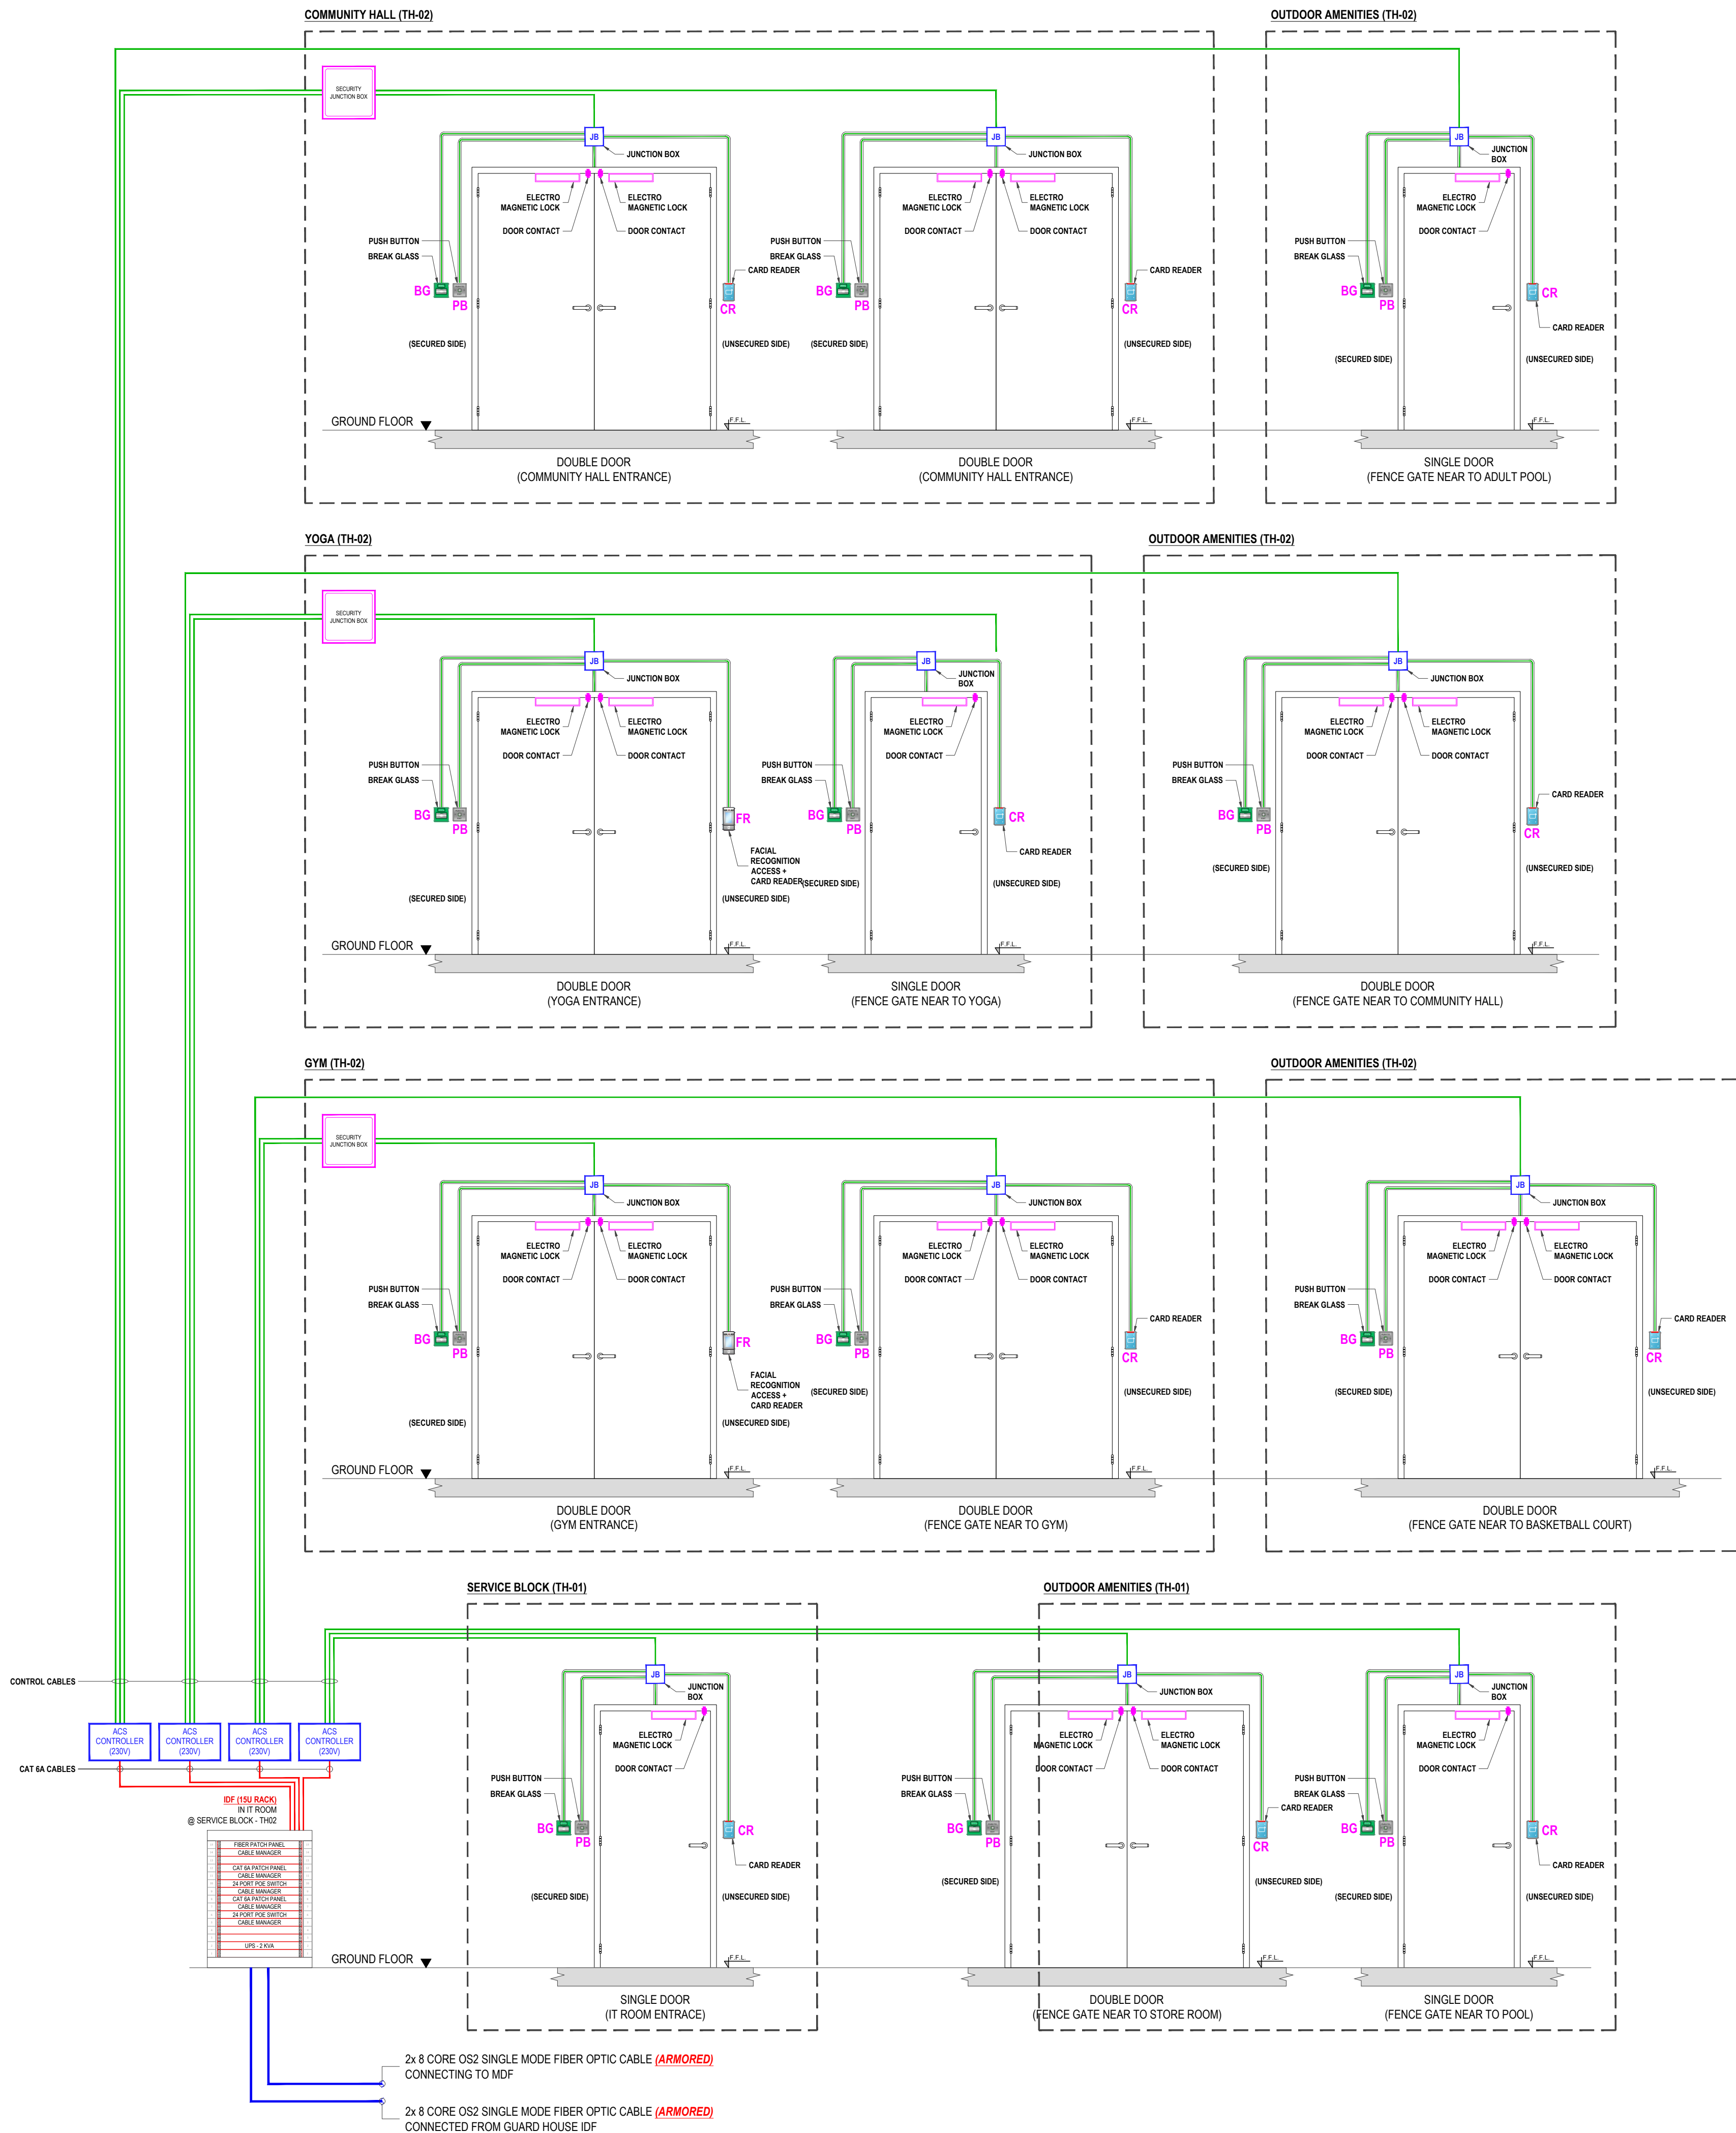


IES NOTE: CCTV + INTRUSION + ACCESS CONTROL

1. THE LOCATIONS OF CCTV, ALARM, AND ACS COMPONENTS ARE INDICATED APPROXIMATELY ON THE DRAWINGS AND ARE SUBJECT TO ON-SITE VERIFICATION.
2. EXACT LOCATIONS AND HEIGHTS OF COMPONENTS WILL BE FINALIZED IN COORDINATION WITH THE CONTRACTOR ON-SITE, CONSIDERING BUILDING LAYOUT, INTERIOR DESIGN, DECORATION, AND ANY OTHER RELEVANT SERVICES OR COMPONENTS.
3. ON-SITE, COORDINATION WITH THE CONTRACTOR IS ESSENTIAL TO ADDRESS ANY POTENTIAL OBSTRUCTIONS TO THE CAMERA'S FIELD OF VIEW, IN COMPLIANCE WITH DUBAI LAW 12/2016, AS WELL AS TO MITIGATE ELECTROMAGNETIC INTERFERENCE (EMI) IMPACTING ELECTRONIC SECURITY COMPONENTS.
4. THIS DESIGN WILL BECOME INVALID IF THERE ARE ANY MODIFICATIONS TO THE ARCHITECTURAL PLANS OR CHANGES IN LEGAL REQUIREMENTS.
5. LOW-LIGHT AREAS SHOULD BE EQUIPPED WITH INFRARED (IR) OR NIGHT VISION CAMERAS TO ENSURE PROPER COVERAGE AND VISIBILITY.

| ACCESS CONTROL SYSTEM SCHEDULE |                                       |          |              |                  |
|--------------------------------|---------------------------------------|----------|--------------|------------------|
| SYMBOL                         | DESCRIPTION                           | ACS QTY. | NO. OF FLOOR | TOTAL NO. OF ACS |
| CR                             | CARD READER                           | 10       | 1            | 10               |
| FR                             | FACE RECOGNITION ACCESS + CARD READER | 2        | 1            | 2                |
| BG                             | BREAK GLASS                           | 12       | 1            | 12               |
| PB                             | PUSH BUTTON                           | 12       | 1            | 12               |
| DC                             | DOOR CONTACT                          | 20       | 1            | 20               |
| EML                            | ELECTRO MAGNETIC LOCK                 | 20       | 1            | 20               |
| ACP                            | ACCESS CONTROL SYSTEM PANEL           | 4        | 1            | 4                |

| LEGEND |                                                   |           |
|--------|---------------------------------------------------|-----------|
| SYMBOL | DESCRIPTION                                       | TOTAL NO. |
|        | JUNCTION BOX FOR SECURITY (300mm x 150mm x 150mm) | 3         |
|        | 15U SECURITY RACK (WALL MOUNTED)                  | 1         |

Key Plan

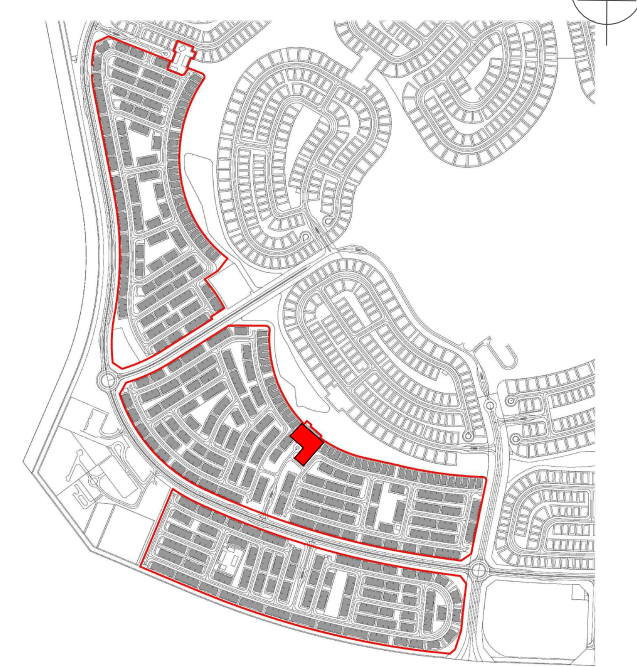

General Notes :

01. Do not Scale The Drawings. Follow (The MM) Written Dimensions Unless Otherwise Mentioned.
02. Each Drawing Shall be Read in Conjunction With all Other Drawings, Specification & the General Standard Details. In Case of Any Discrepancies Bring it to the Knowledge of Engineer and Same to be Resolved Prior to Execution of Work.
03. Dimensions Shown on These Drawings are Structural Dimensions. Unless Noted Otherwise.
04. All Levels Indicated On These Drawings are Levels as per the Survey Datum, Same Should be Verified at Site Prior to Execution of Work.
05. All Levels Indicated On These Drawings are Based On Design Level, Which is Equivalent to Datum Level and Same Should be Verified at Site Prior to Execution of Work.



|     |            |          |                   |
|-----|------------|----------|-------------------|
| 09  | 10/03/2026 | JP       | TENDER SUBMISSION |
| No. | Date       | Initials | Description       |

REVISIONS / ISSUE

THIS DRAWING MUST NOT BE REPRODUCED IN WHOLE OR IN PART WITHOUT THE PRIOR APPROVAL OF ARIF & BINTOAK

Status: TENDER SUBMISSION

Client: EMAAR

Lead Consultant: عارف وبن طوق Arif&Bintoak

CONSULTING architects & engineers  
POST BOX 3670 DUBAI UAE TEL: 84-3272888 FAX: 84-3270352  
POST BOX 42981 ABU DHABI UAE TEL: 02-434669 arif&bintoak@gmail.com

Security Consultant: INTERNATIONAL ELECTRONIC SECURITY  
TEL: 04 397 0757, FAX: 04 397 0754  
P.O. BOX 12734 DUBAI - U.A.E  
ENQUIRIES@IESCONSULTING.AE  
AUDIT@IESCONSULTING.AE  
WWW.IESCONSULTING.AE

Project Title: Proposed Residential Townhouses and Standalone Villas TH-1, TH-2, and TH-3 at Grand Polo Club & Resort, Dubai, UAE

Discipline: SECURITY

Drawing title: ACCESS CONTROL SYSTEM SINGLE LINE DIAGRAM COMMUNITY CENTER - TH-02

|                        |                        |                       |
|------------------------|------------------------|-----------------------|
| Architectural Engineer | Electrical Engineer    | Structural Engineer   |
| MUSTAFA ABID           | MARWAN MOHD.           | RIHAM RAMADAN         |
| Registration # 5847    | Registration # 80102   | Registration # 105092 |
| Scale(s): NTS          | Date drawn: 10/03/2026 | Project no: 1857      |

|                                                       |             |              |
|-------------------------------------------------------|-------------|--------------|
| Drawn by: JP                                          | Checked: MM | Approved: JR |
| Drawing Number: GPCR-TH02-IES-CC2-SLD-SEC-ACS-2000-00 |             |              |