



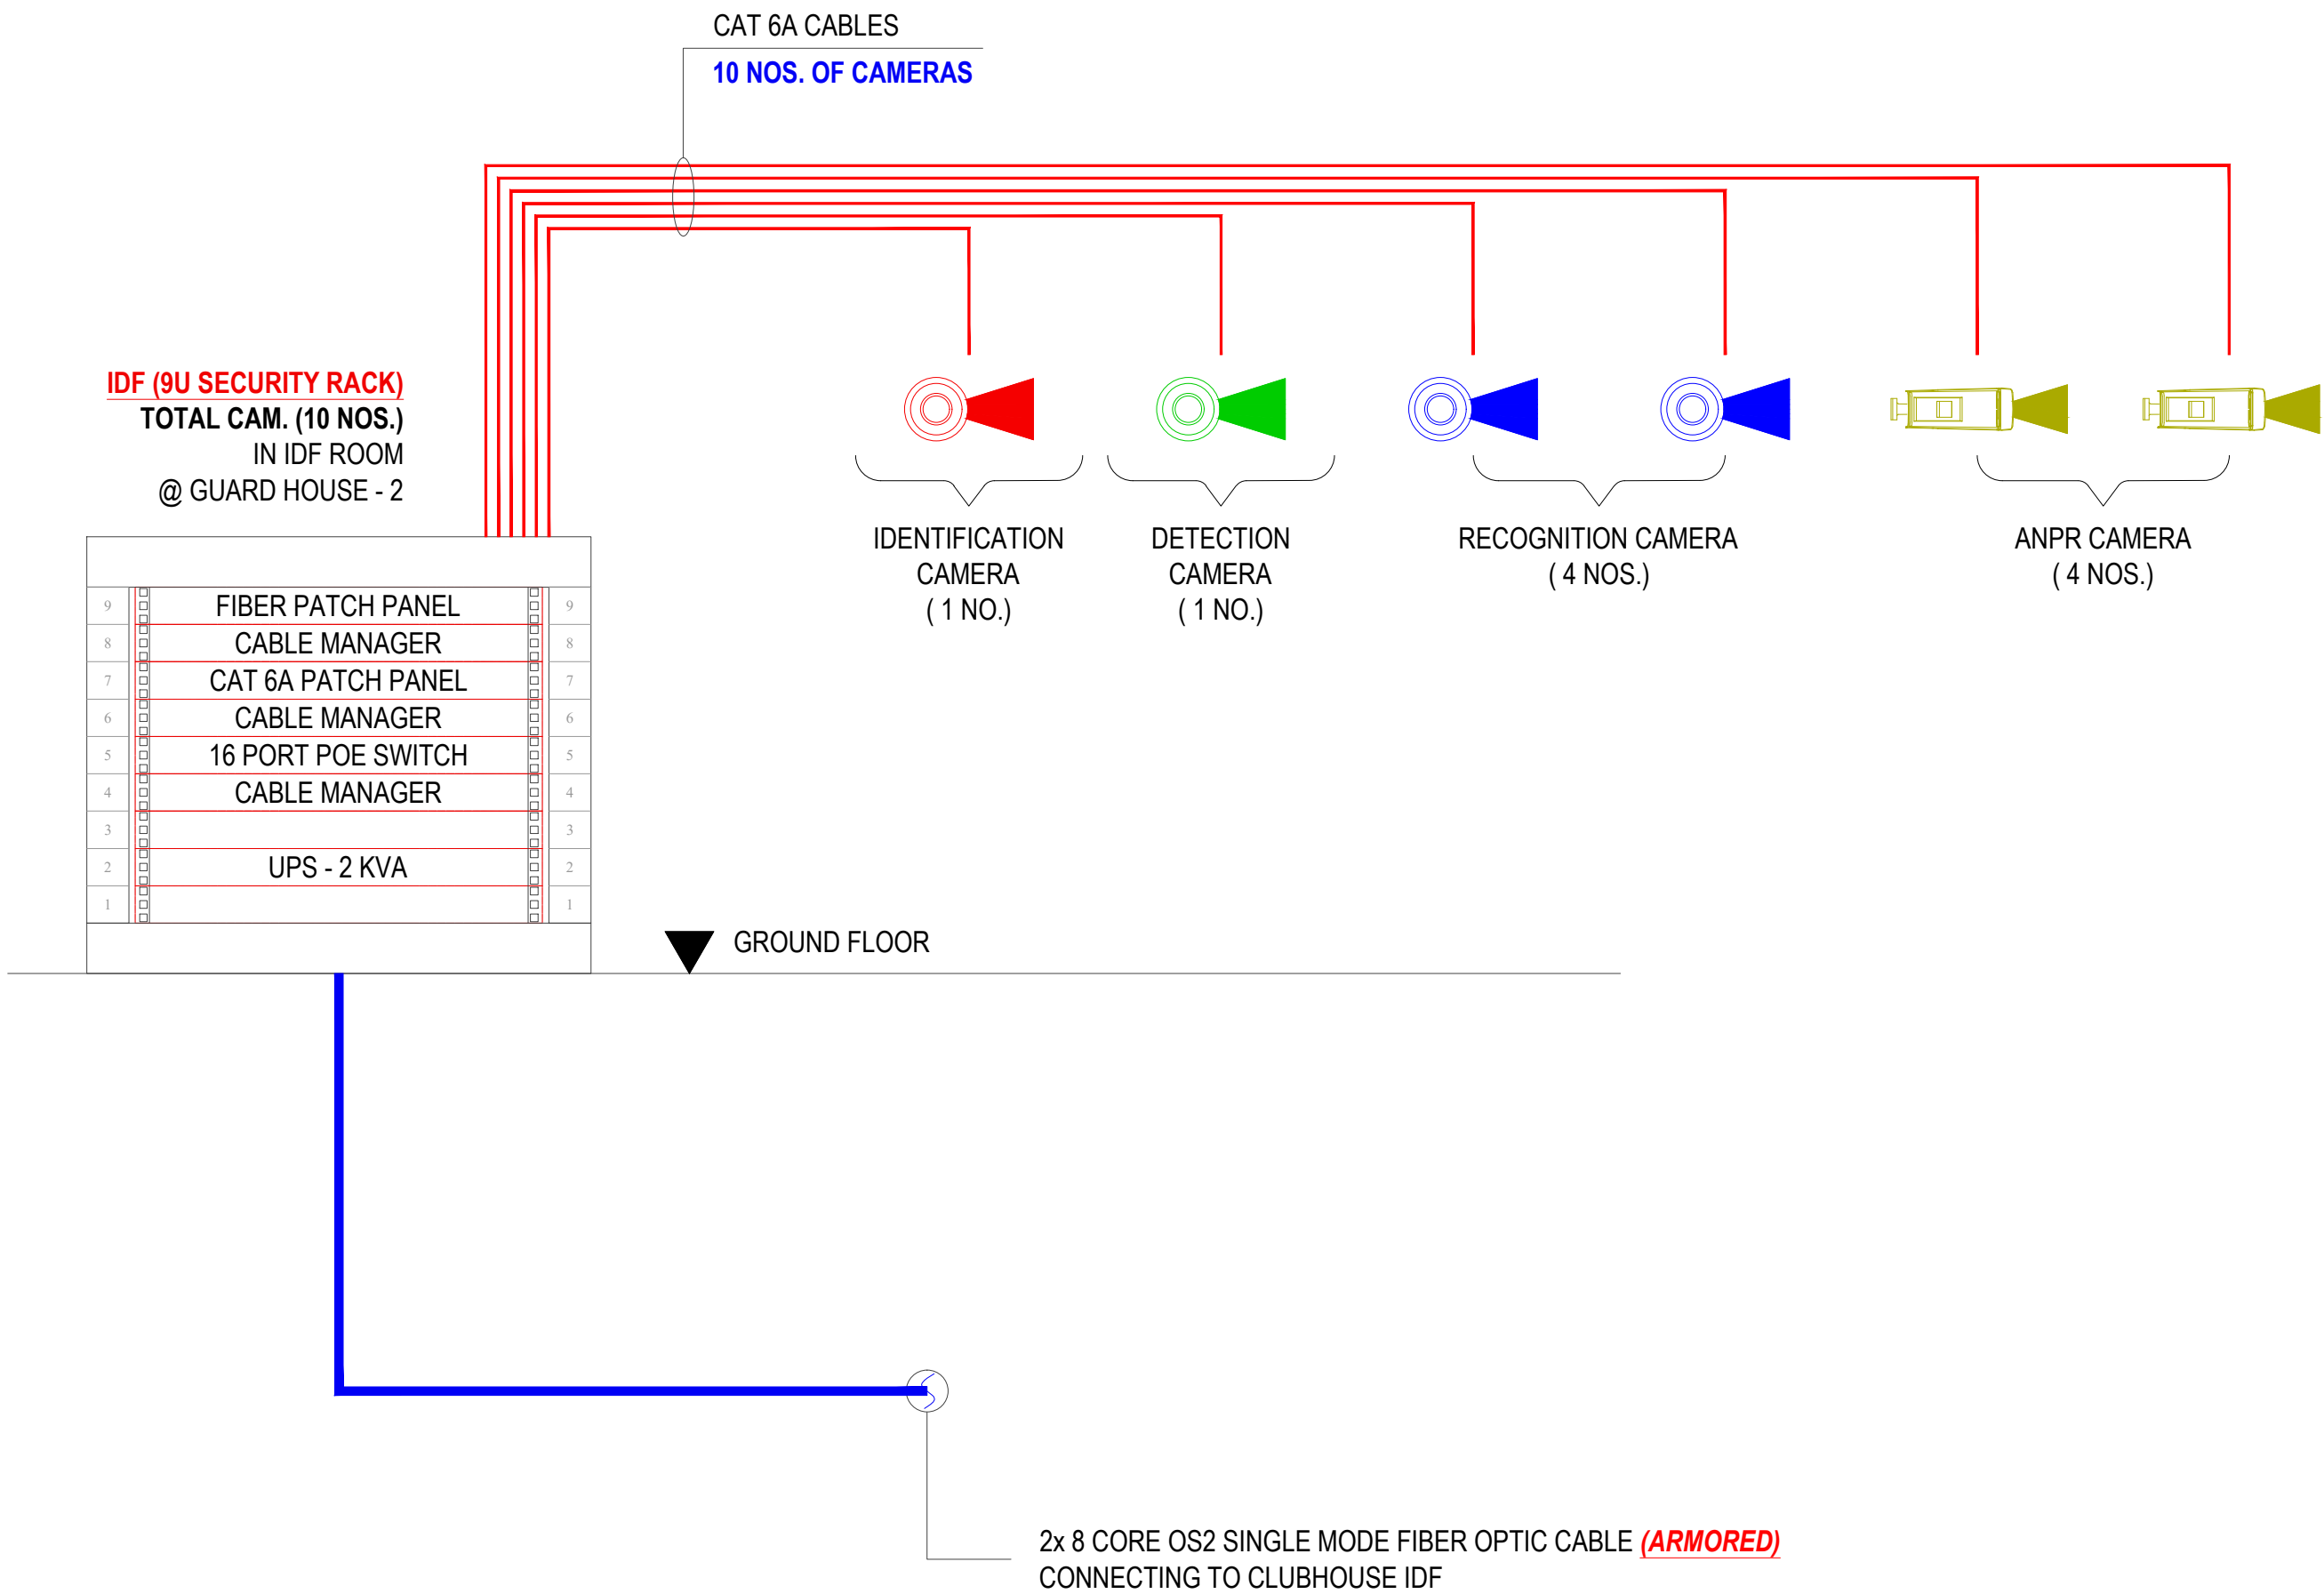


- IES NOTE: CCTV + INTRUSION + ACCESS CONTROL**
1. THE LOCATIONS OF CCTV, ALARM, AND ACS COMPONENTS ARE INDICATED APPROXIMATELY ON THE DRAWINGS AND ARE SUBJECT TO ON-SITE VERIFICATION.
 2. EXACT LOCATIONS AND HEIGHTS OF COMPONENTS WILL BE FINALIZED IN COORDINATION WITH THE CONTRACTOR ON-SITE, CONSIDERING BUILDING LAYOUT, INTERIOR DESIGN, DECORATION, AND ANY OTHER RELEVANT SERVICES OR COMPONENTS.
 3. ON-SITE, COORDINATION WITH THE CONTRACTOR IS ESSENTIAL TO ADDRESS ANY POTENTIAL OBSTRUCTIONS TO THE CAMERA'S FIELD OF VIEW, IN COMPLIANCE WITH DUBAI LAW 12/2016, AS WELL AS TO MITIGATE ELECTROMAGNETIC INTERFERENCE (EMI) IMPACTING ELECTRONIC SECURITY COMPONENTS.
 4. THIS DESIGN WILL BECOME INVALID IF THERE ARE ANY MODIFICATIONS TO THE ARCHITECTURAL PLANS OR CHANGES IN LEGAL REQUIREMENTS.
 5. LOW-LIGHT AREAS SHOULD BE EQUIPPED WITH INFRARED (IR) OR NIGHT VISION CAMERAS TO ENSURE PROPER COVERAGE AND VISIBILITY.

SECURITY CAMERA SCHEDULE			
SYMBOL	DESCRIPTION	CAM. QTY.	NO. OF FLOOR
	120% IDENTIFICATION CAMERA	1	1
	50% RECOGNITION CAMERA	4	1
	25% OBSERVATION CAMERA	0	1
	10% DETECTION CAMERA	1	1
	5% MONITORING CAMERA	0	1
	20% ANPR CAMERA	4	1
OVERALL TOTAL CAMERA			10

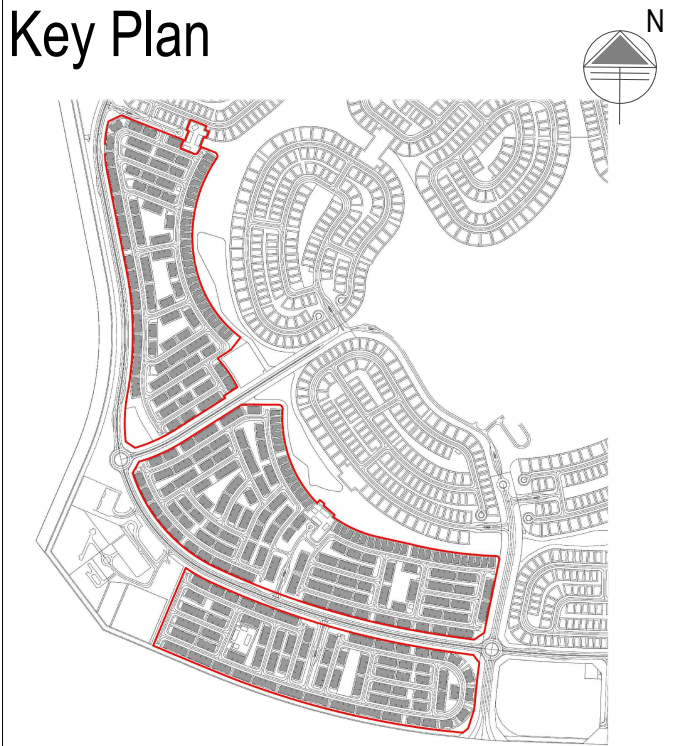

- General Notes :**
01. Do not Scale The Drawings. Follow (The MM) Written Dimensions Unless Otherwise Mentioned.
 02. Each Drawing Shall be Read in Conjunction With all Other Drawings, Specification & the General Standard Details. In Case of Any Discrepancies Bring it to the Knowledge of Engineer and Same to be Resolved Prior to Execution of Work.
 03. Dimensions Shown on These Drawings are Structural Dimensions, Unless Noted Otherwise.
 04. All Levels Indicated On These Drawings are Levels as per the Survey Datum, Same Should be Verified at Site Prior to Execution of Work.
 05. All Levels Indicated On These Drawings are Based On Design Level, Which is Equivalent to Datum Level and Same Should be Verified at Site Prior to Execution of Work.

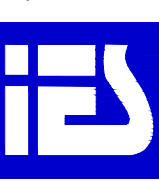

00	10/03/2026	JP	TENDER SUBMISSION
No.	Date	Initials	Description
REVISIONS / ISSUE			
THIS DRAWING MUST NOT BE REPRODUCED IN WHOLE OR IN PART WITHOUT THE PRIOR APPROVAL OF ARIF & BINTOAK			
Status			
TENDER SUBMISSION			
Client			
EMAAR			
Lead Consultant			
 consulting architects & engineers POST BOX 3670 DUBAI U.A.E. TEL: 84-3372888 FAX: 84-3379352 POST BOX 42961 ABU DHABI U.A.E. TEL: 62-434669 ariftoak@emirates.net.ae			
Security Consultant			
 INTERNATIONAL ELECTRONIC SECURITY TEL: 04 397 0757, FAX: 04 397 0754 P.O. BOX 12734 DUBAI - U.A.E ENQUIRIES@IESCONSULTING.AE AUDIT@IESCONSULTING.AE WWW.IESCONSULTING.AE			
Project Title:			
Proposed Residential Townhouses and Standalone Villas TH-1, TH-2, and TH-3 at Grand Polo Club & Resort, Dubai, UAE			
Discipline :			
SECURITY			
Drawing title:			
SINGLE LINE DIAGRAM CCTV SYSTEM LAYOUT GUARD HOUSE - TH-02			
Architectural Engineer	Electrical Engineer	Structural Engineer	
MUSTAFA ABID	MARWAN MOHD.	RIHAM RAMADAN	
Registration # 5847	Registration # 80102	Registration # 105082	
Scale(s):	Date drawn:	Project no:	
NTS	10/03/2026	1857	
Drawn by:	Checked:	Approved:	
JP	MM	JR	
Drawing Number :		GPCR-TH02-IES-GH2-SLD-SEC-VSS-2000-00	

© AB | A1 Title Block - BIM Standard Ver. 2.0

10/9/2026 3:20:21 PM