



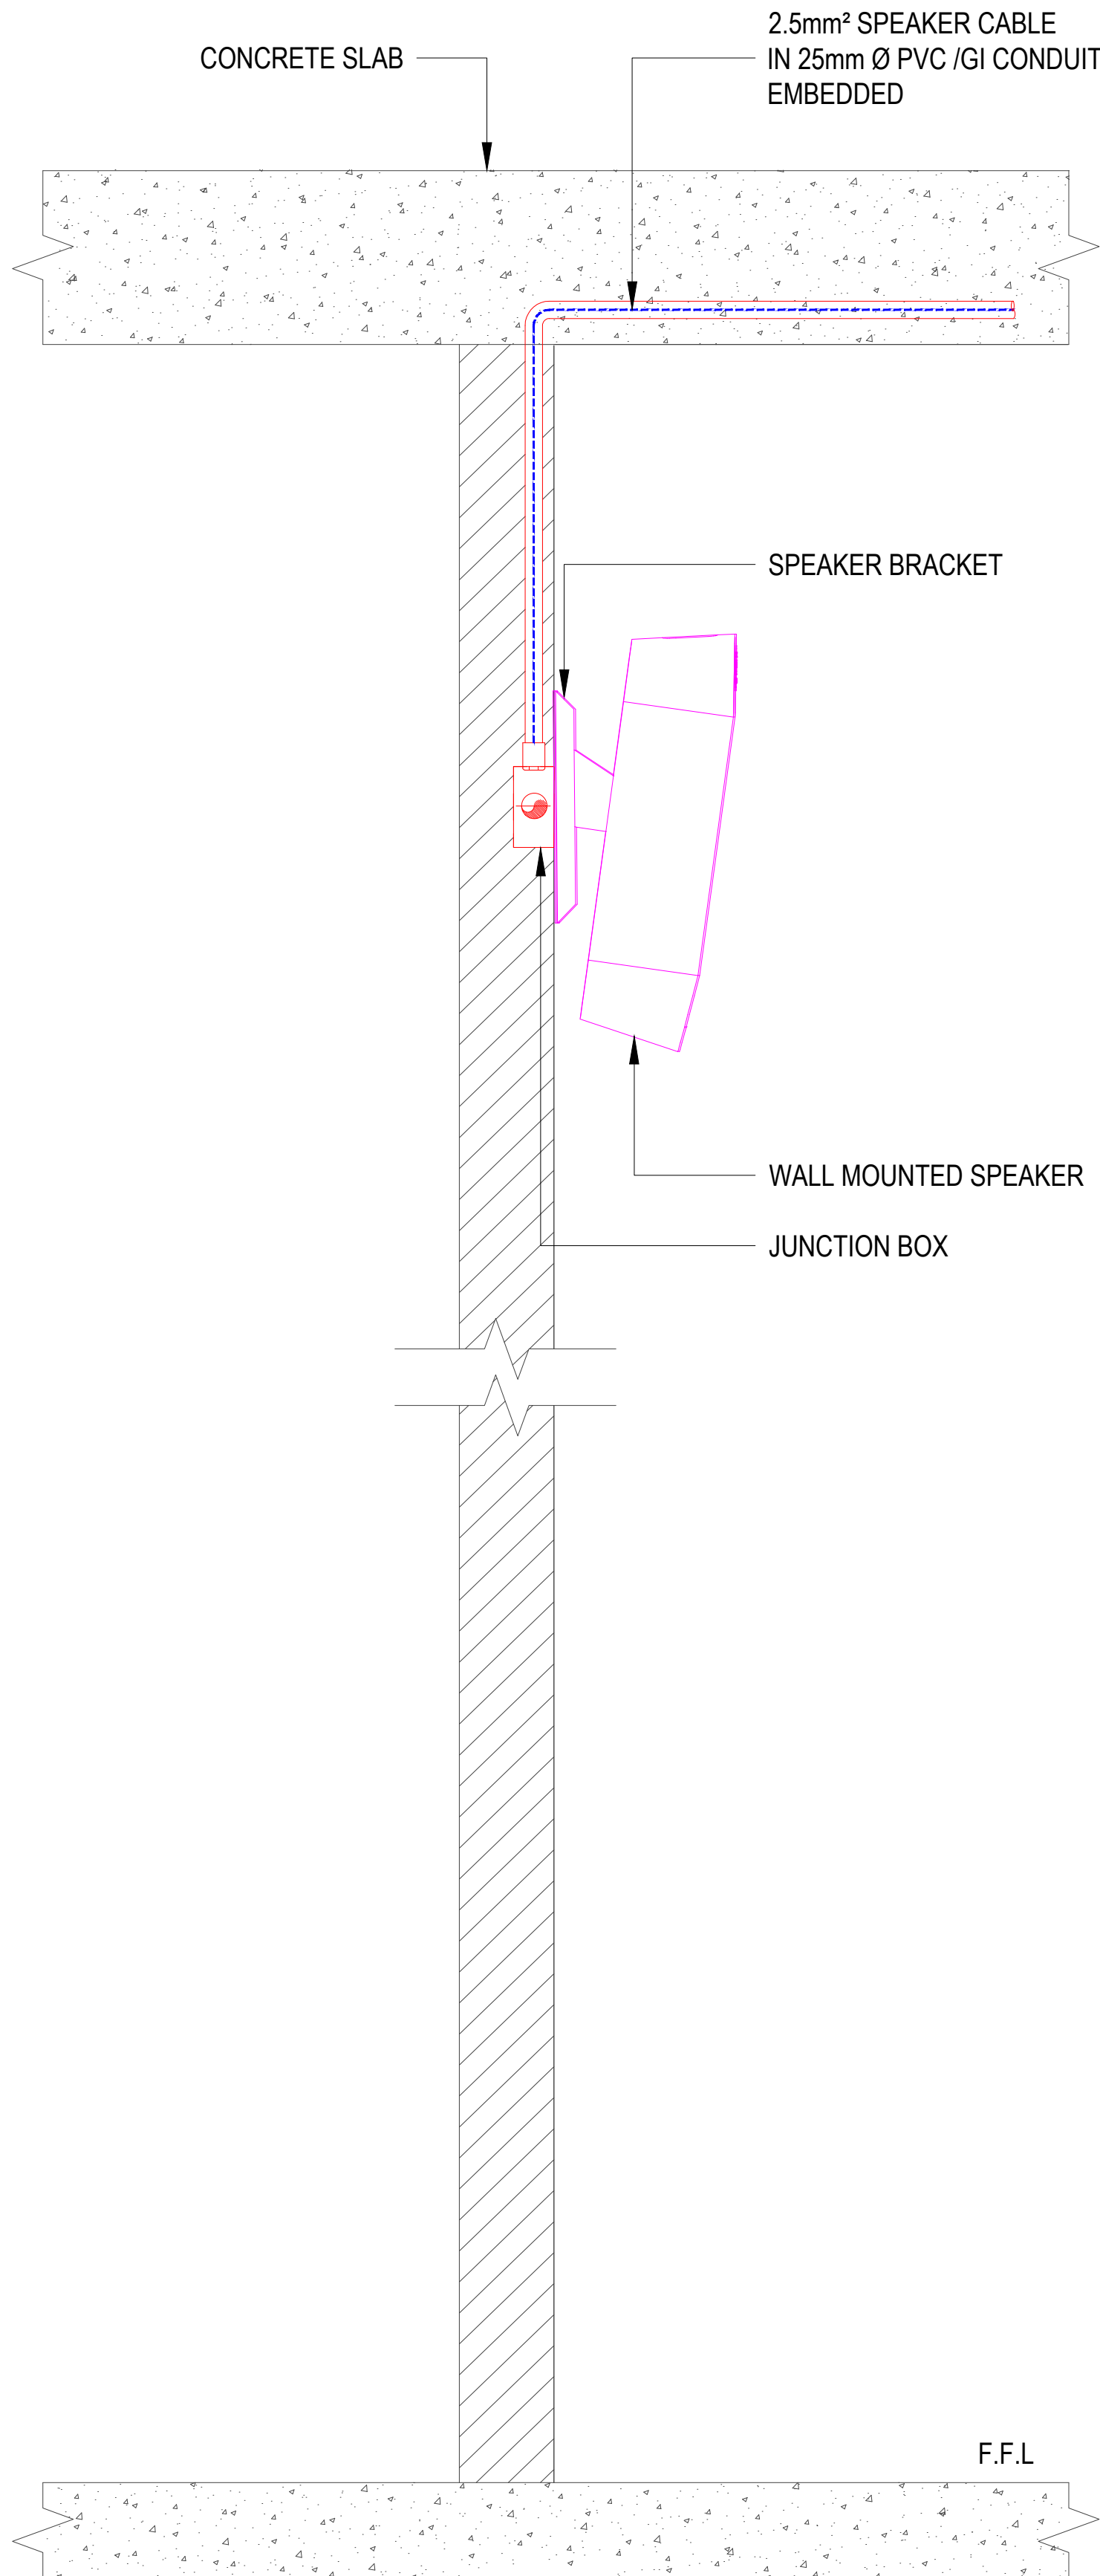

**WALL SPEAKER
TYPICAL MOUNTING DETAILS**

1

NOT TO SCALE

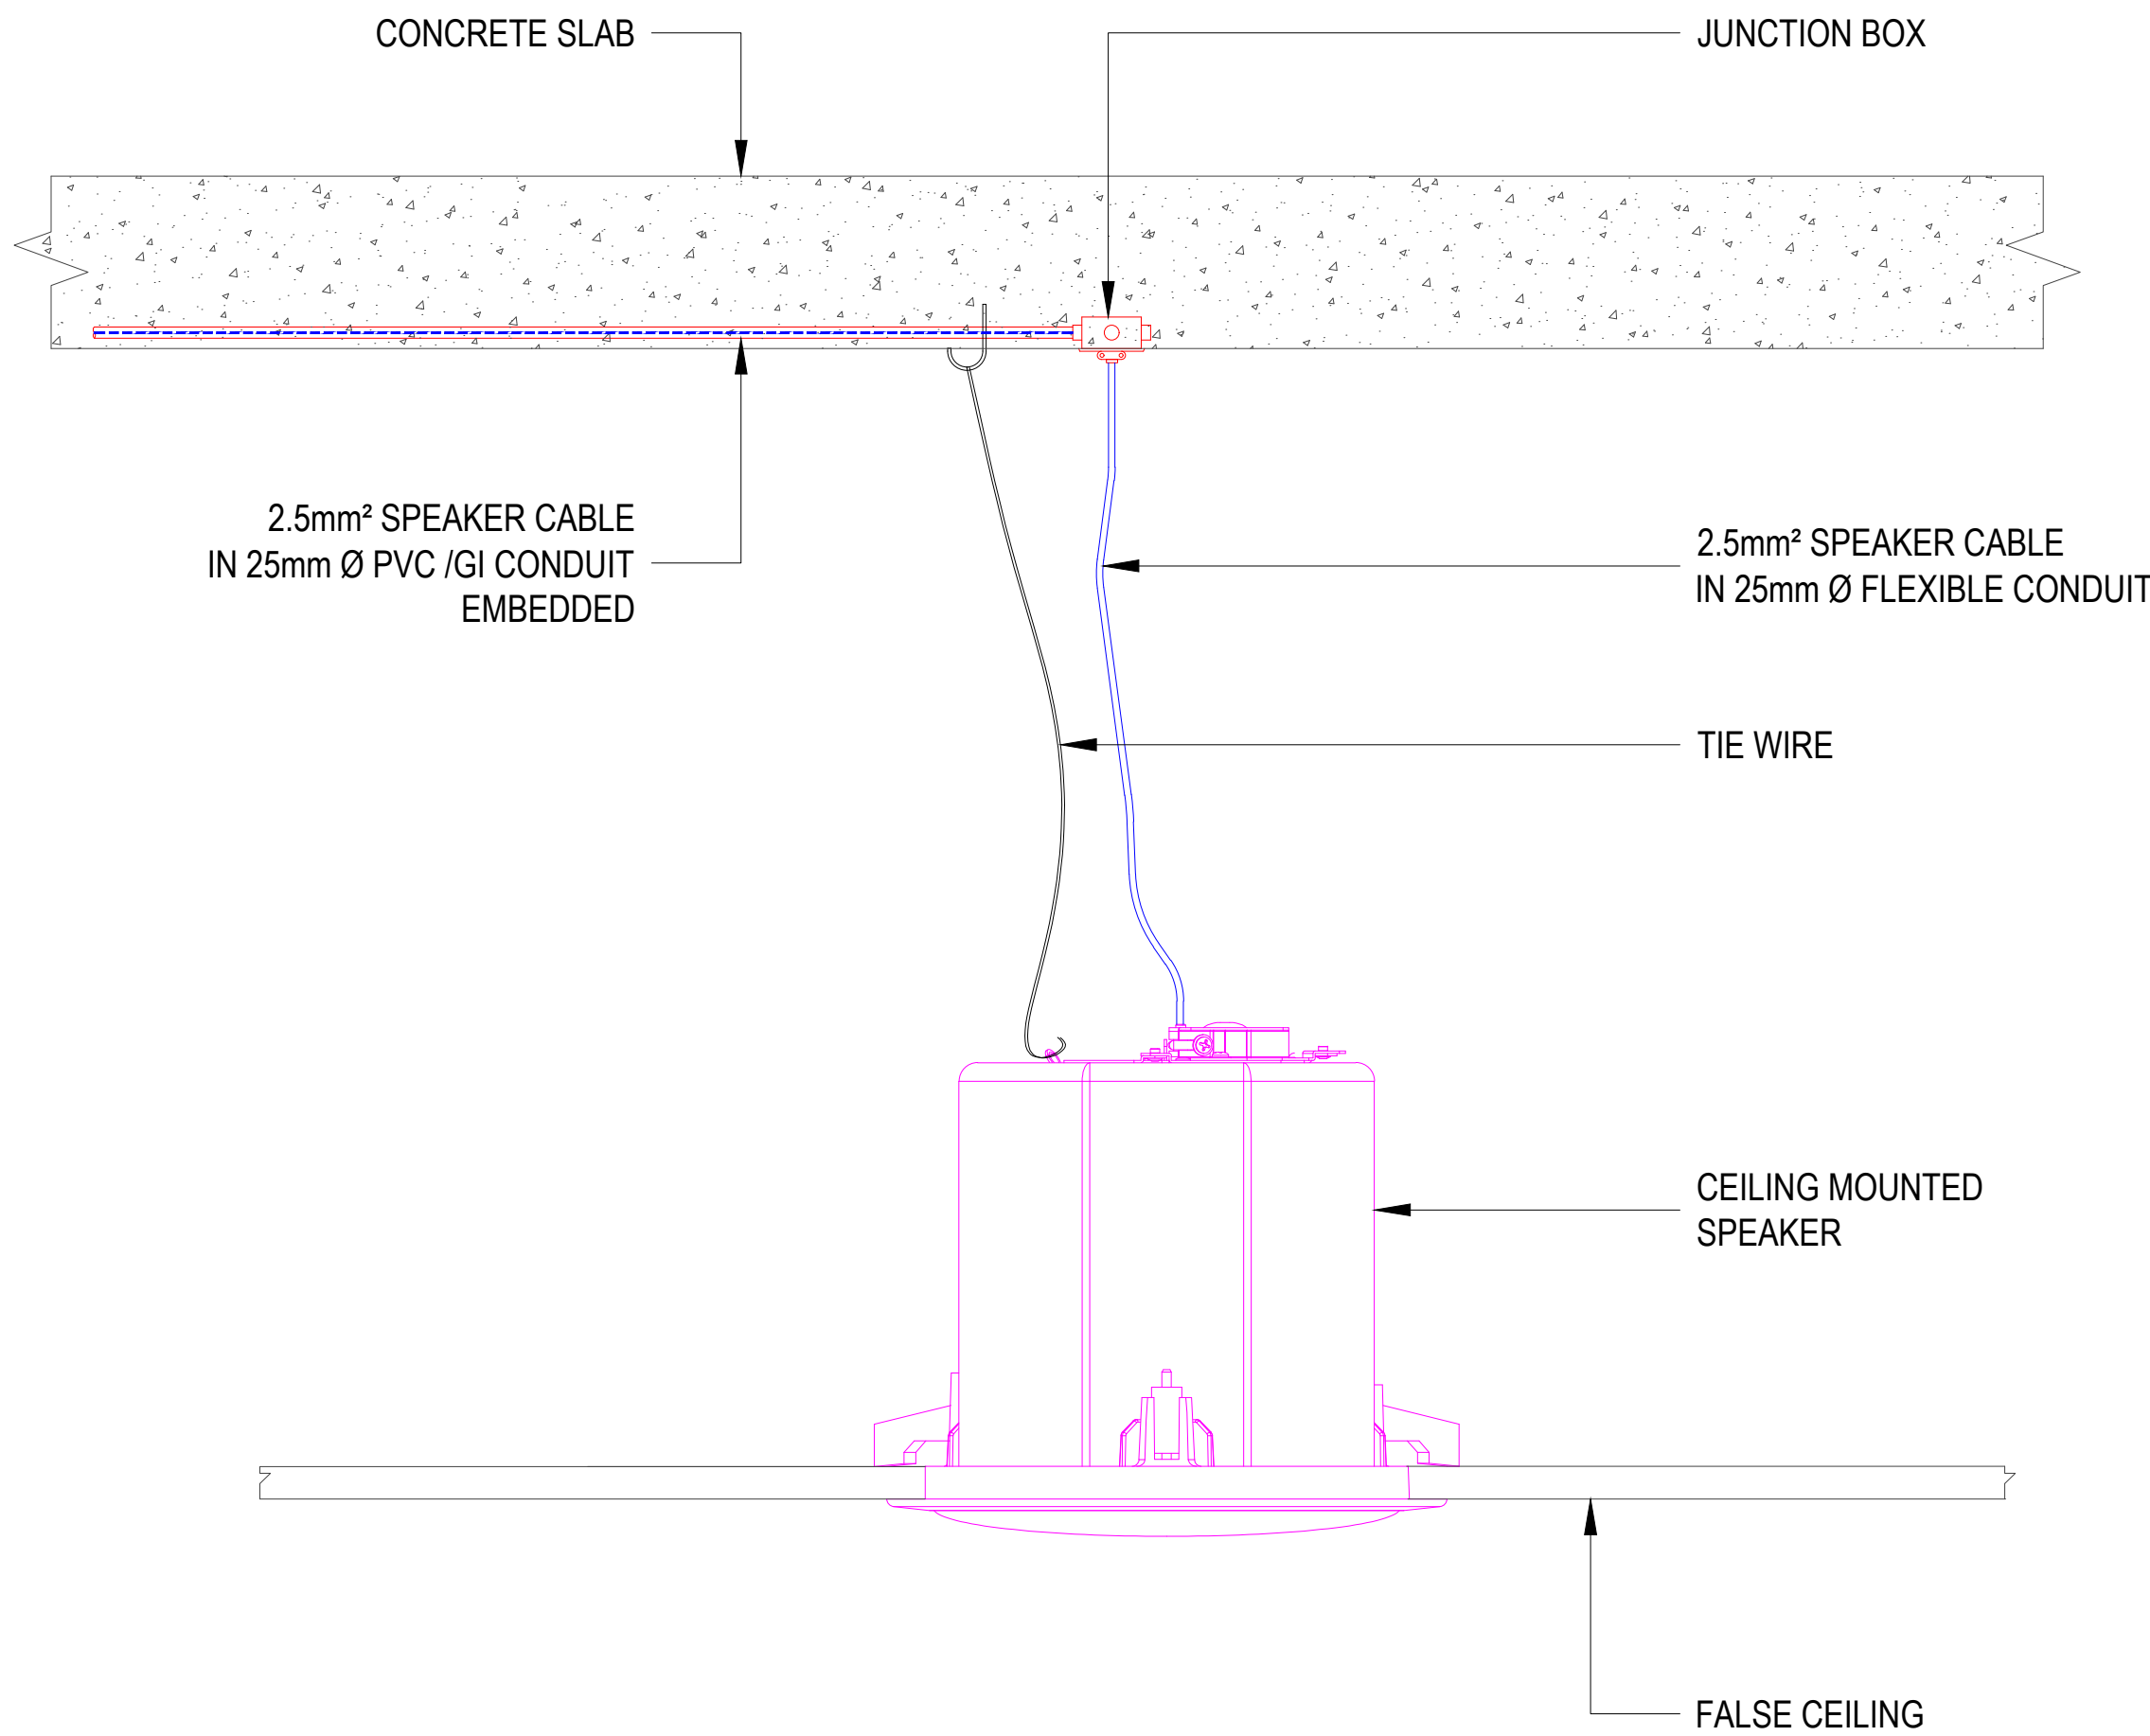


**CEILING SPEAKER
TYPICAL MOUNTING DETAILS**

2

NOT TO SCALE

- NOTE: AUDIO VISUAL (AV)**
1. SPEAKER LOCATION ARE INDICATIVE ONLY.KINDLY REFER ID DRAWINGS. AV CONTRACTOR SHOULD CO-ORDINATE WITH MEP, ARCHITECT ON SITE.
 2. ALL AV EQUIPMENT SHOULD HAVE RAL COLOR MATCHING WITH ID REQUIREMENTS
 3. INSTALLATION OF DISPLAY SCREENS, AV EQUIPMENT, RESPECTIVE CABLES & CONNECTORS SHOULD MATCH SITE REQUIREMENT.
 4. ALL AV EQUIPMENT SHOULD BE PRO-AUDIO. ALL EQUIPMENTS SHOULD HAVE RS232 CONTROL PORT & SHOULD HAVE PROPER FEED BACK.
 5. AV BLUETOOTH PLATE SHALL BE WHITE IN COLOUR AND DISCRETELY LOCATED
 6. ALL AV EQUIPMENT POWER REQUIREMENT SHOULD BE PROVIDED BY AV CONTRACTOR & CO-ORDINATE WITH RESPECTIVE CONTRACTOR.
 7. 1x13A POWER SOCKET REQUIRED FOR WP (WALL PLATE) PROVIDED BY ELECTRICAL CONTRACTOR.
 8. AV CONTRACTOR SHOULD PROVIDE TRS JACK TO USB C PATCH CABLE FOR EVERY WALL PLATE FOR MOBILE PHONE & IPAD TO PLAY LOCAL MUSIC FROM MOBILE OR IPAD.

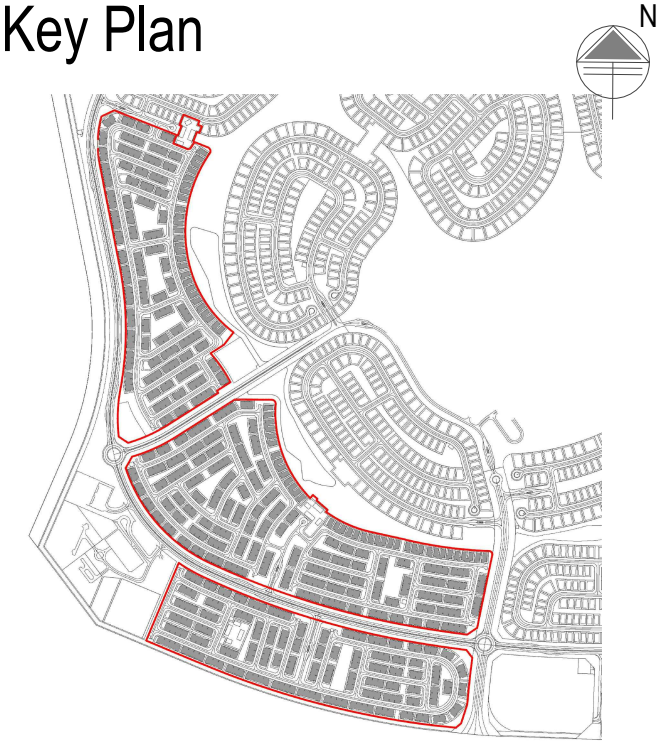

- General Notes :**
01. Do not Scale The Drawings. Follow (The MM) Written Dimensions Unless Otherwise Mentioned.
 02. Each Drawing Shall be Read in Conjunction With all Other Drawings, Specification & the General Standard Details. In Case of Any Discrepancies Bring it to the Knowledge of Engineer and Same to be Resolved Prior to Execution of Work.
 03. Dimensions Shown on These Drawings are Structural Dimensions. Unless Noted Otherwise.
 04. All Levels Indicated On These Drawings are Levels as per the Survey Datum, Same Should be Verified at Site Prior to Execution of Work.
 05. All Levels Indicated On These Drawings are Based On Design Level, Which is Equivalent to Datum Level and Same Should be Verified at Site Prior to Execution of Work.



No.	Date	Initials	Description
00	10/03/2026	JP	TENDER SUBMISSION

REVISIONS / ISSUE

THIS DRAWING MUST NOT BE REPRODUCED IN WHOLE OR IN PART WITHOUT THE PRIOR APPROVAL OF ARIF & BINTOAK

Status: **TENDER SUBMISSION**

Client:

EMAAR

Lead Consultant

عارف وبن طوق
Arif&Bintoak
consulting architects & engineers

POST BOX 3670 DUBAI U.A.E TEL: 04-3772888 FAX: 04-3770352
POST BOX 42981 ABU DHABI U.A.E TEL: 02-4546699 ariftoak@emirates.net.ae

Security Consultant

ies **INTERNATIONAL ELECTRONIC SECURITY**
TEL: 04 397 0757, FAX: 04 397 0754
P.O. BOX 12734 DUBAI - U.A.E
ENQUIRIES@IESCONSULTING.AE
AUDIT@IESCONSULTING.AE
WWW.IESCONSULTING.AE

Project Title:

Proposed Residential Townhouses and Standalone Villas TH-1, TH-2, and TH-3 at Grand Polo Club & Resort, Dubai, UAE

Discipline :	AUDIO VISUAL (AV)
Drawing title:	AUDIO VISUAL (AV) TYPICAL INSTALLATION DETAILS COMMUNITY CENTER - TH-02

Architectural Engineer	Electrical Engineer	Structural Engineer
MUSTAFA ABID	MARWAN MOHD.	RIHAM RAMADAN
Registration # 5847	Registration # 80102	Registration # 105082
Scale(s):	Date drawn: 10/03/2026	Project no: 1857
Drawn by: JP	Checked: MM	Approved: JR
Drawing Number :	GPCR-TH02-IES-INS-AVC-AV-1000-00	