




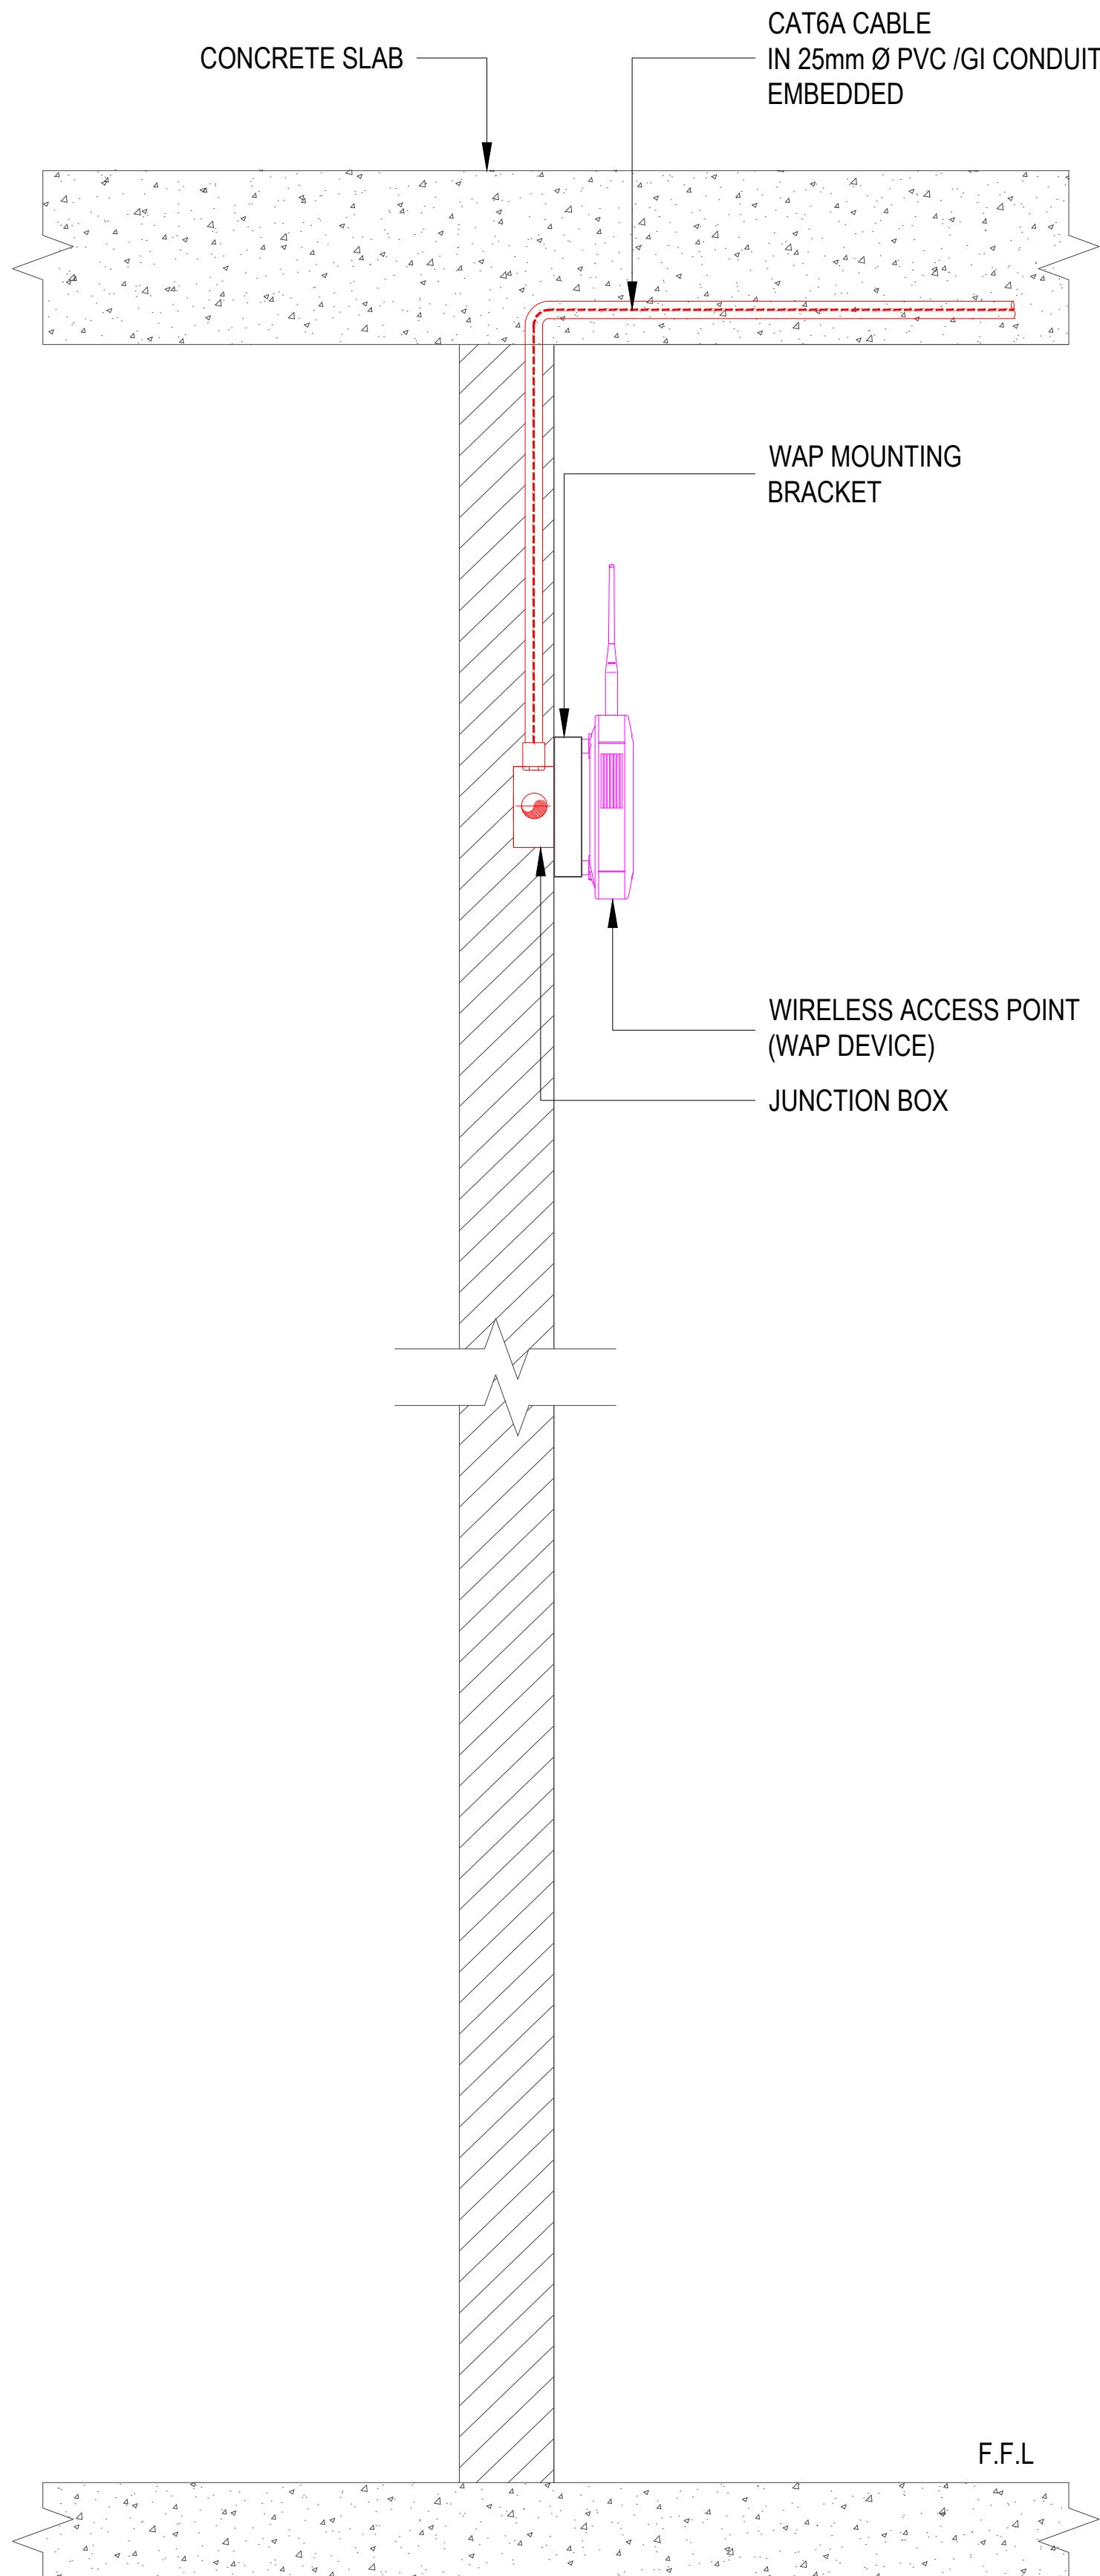

**WALL SPEAKER
TYPICAL MOUNTING DETAILS**
NOT TO SCALE

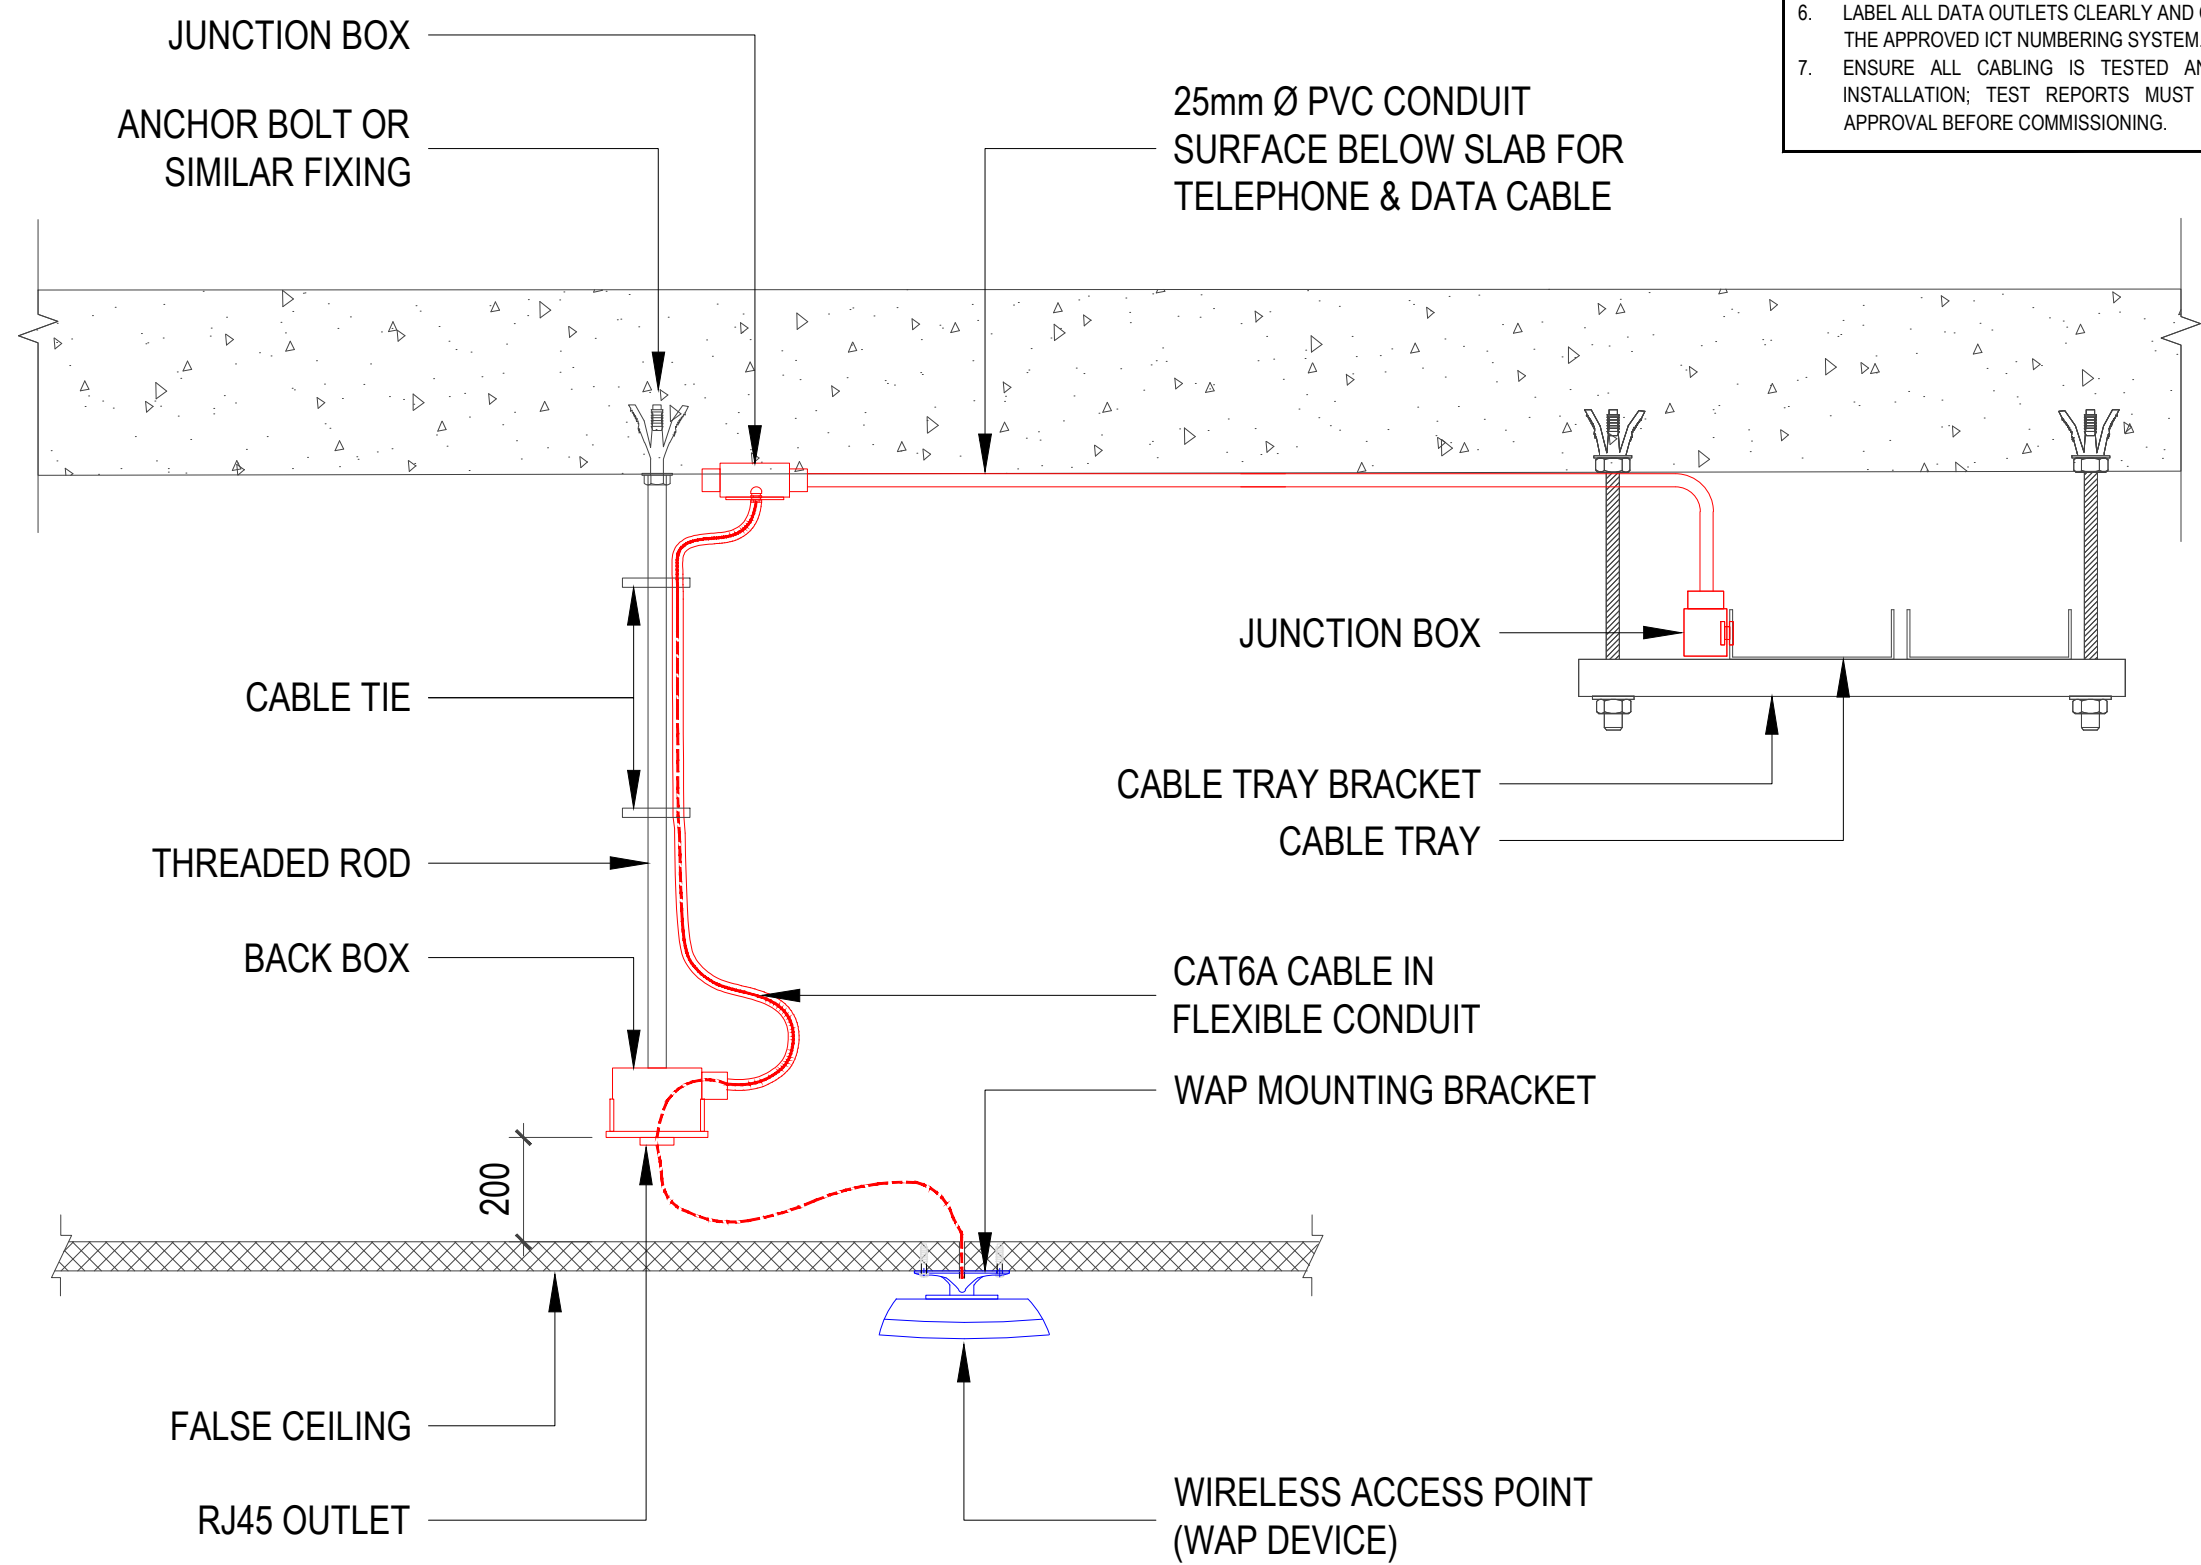


**CEILING SPEAKER
TYPICAL MOUNTING DETAILS**
NOT TO SCALE

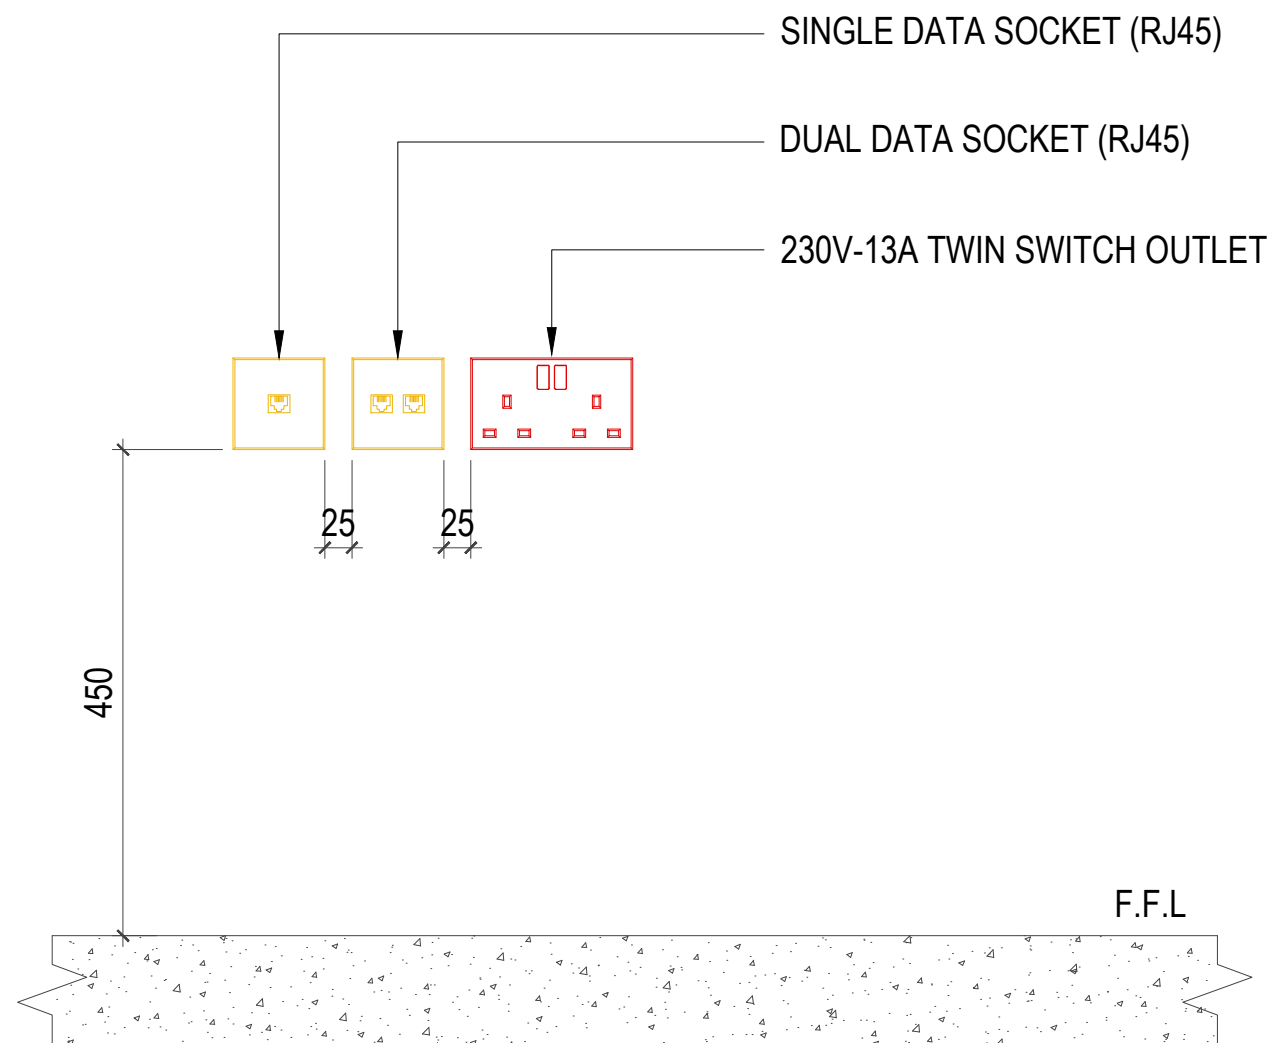

**DATA SOCKET (RJ45)
TYPICAL MOUNTING DETAILS**
NOT TO SCALE

- NOTE: ICT DATA POINTS AND WIRELESS ACCESS POINT (WAPs)**
1. ALL ICT DATA POINTS AND WAP LOCATIONS SHALL BE VERIFIED ON-SITE AND PRIOR TO INSTALLATION.
 2. ALL ICT DATA POINTS SHALL BE INSTALLED IN ACCORDANCE WITH THE LATEST STANDARDS FOR STRUCTURED CABLING (e.g., ANSI/TIA-568, ISO/IEC 11801).
 3. DATA OUTLETS SHALL BE RJ45 TYPE, CAT 6A, AND HOUSED IN STANDARD WALL-MOUNT OR FLOOR-BOX FACEPLATES AS PER PROJECT SPECIFICATIONS.
 3. ALL WIRELESS ACCESS POINTS (WAPs) SHALL BE INSTALLED AS PER MANUFACTURER SPECIFICATIONS TO ENSURE OPTIMAL WIRELESS COVERAGE AND PERFORMANCE.
 4. CONDUITS AND CABLE TRAYS USED FOR ICT CABLING SHALL BE SEPARATE FROM ELECTRICAL POWER CONDUITS TO AVOID INTERFERENCE.
 5. DATA OUTLET AND WAPs FINAL LOCATIONS SHALL BE COORDINATED WITH ARCHITECTURAL LAYOUTS TO ENSURE ACCESSIBILITY AND AVOID CONFLICTS WITH OTHER FIXTURES OR FINISHES.
 6. LABEL ALL DATA OUTLETS CLEARLY AND CONSISTENTLY AS PER THE APPROVED ICT NUMBERING SYSTEM.
 7. ENSURE ALL CABLING IS TESTED AND CERTIFIED AFTER INSTALLATION. TEST REPORTS MUST BE SUBMITTED FOR APPROVAL BEFORE COMMISSIONING.

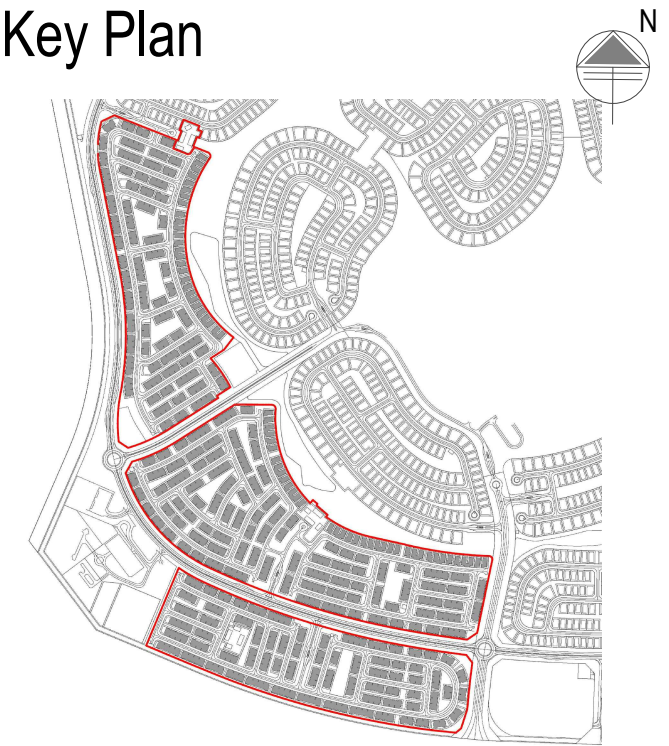

- General Notes :**
01. Do not Scale The Drawings. Follow (The MM) Written Dimensions Unless Otherwise Mentioned.
 02. Each Drawing Shall be Read in Conjunction With all Other Drawings, Specification & the General Standard Details. In Case of Any Discrepancies Bring it to the Knowledge of Engineer and Same to be Resolved Prior to Execution of Work.
 03. Dimensions Shown on These Drawings are Structural Dimensions, Unless Noted Otherwise.
 04. All Levels Indicated On These Drawings are Levels as per the Survey Datum, Same Should be Verified at Site Prior to Execution of Work.
 05. All Levels Indicated On These Drawings are Based On Design Level, Which is Equivalent to Datum Level and Same Should be Verified at Site Prior to Execution of Work.



09	10/03/2026	JP
No.	Date	Initials
TENDER SUBMISSION		
THIS DRAWING MUST NOT BE REPRODUCED IN WHOLE OR IN PART WITHOUT THE PRIOR APPROVAL OF ARIF & BINTOAK		
Status		
TENDER SUBMISSION		
Client		
EMAAR		
Lead Consultant		
عارف وبن طوق Arif&Bintoak consulting architects & engineers POST BOX 3670 DUBAI U.A.E TEL: 84-3372888 FAX: 84-3379352 POST BOX 42981 ABU DHABI U.A.E TEL: 02-454659 -arfoak@emirates.net.ae		
Security Consultant		
INTERNATIONAL ELECTRONIC SECURITY TEL: 04 397 0757, FAX: 04 397 0754 P.O. BOX 12734 DUBAI - U.A.E ENQUIRIES@IESCONSULTING.AE AUDIT@IESCONSULTING.AE WWW.IESCONSULTING.AE		
Project Title:		
Proposed Residential Townhouses and Standalone Villas TH-1, TH-2, and TH-3 at Grand Polo Club & Resort, Dubai, UAE		
Discipline :		
ICT		
Drawing title:		
WAP DEVICE AND DATA SOCKET TYPICAL INSTALLATION DETAILS COMMUNITY CENTER & GUARD HOUSE - TH-02		
Architectural Engineer	Electrical Engineer	Structural Engineer
MUSTAFA ABID	MARWAN MOHD.	RIHAM RAMADAN
Registration # 5847	Registration # 80102	Registration # 105082
Scale(s):	Date drawn:	Project no:
NTS	10/03/2026	1857
Drawn by:	Checked:	Approved:
JP	MM	JR
Drawing Number :		
GPCR-TH02-IES-INS-ICT-IT-1000-00		