




This 2D drawing is extracted from 3D BIM Model

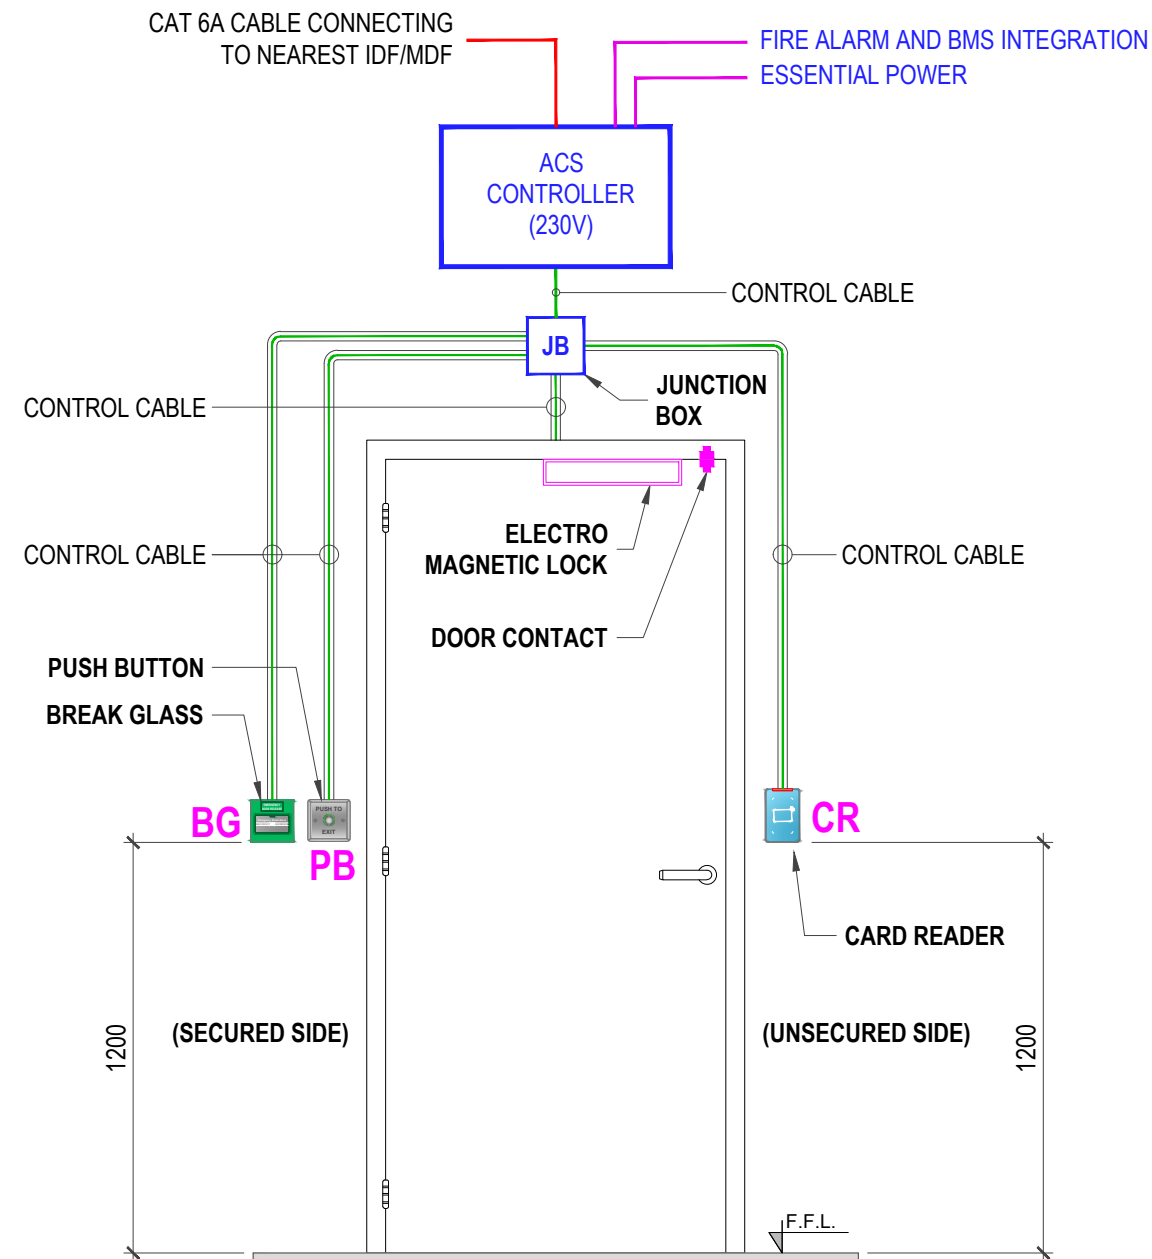


1 SINGLE DOOR
DC + EML + CR + BG + PB
NOT TO SCALE

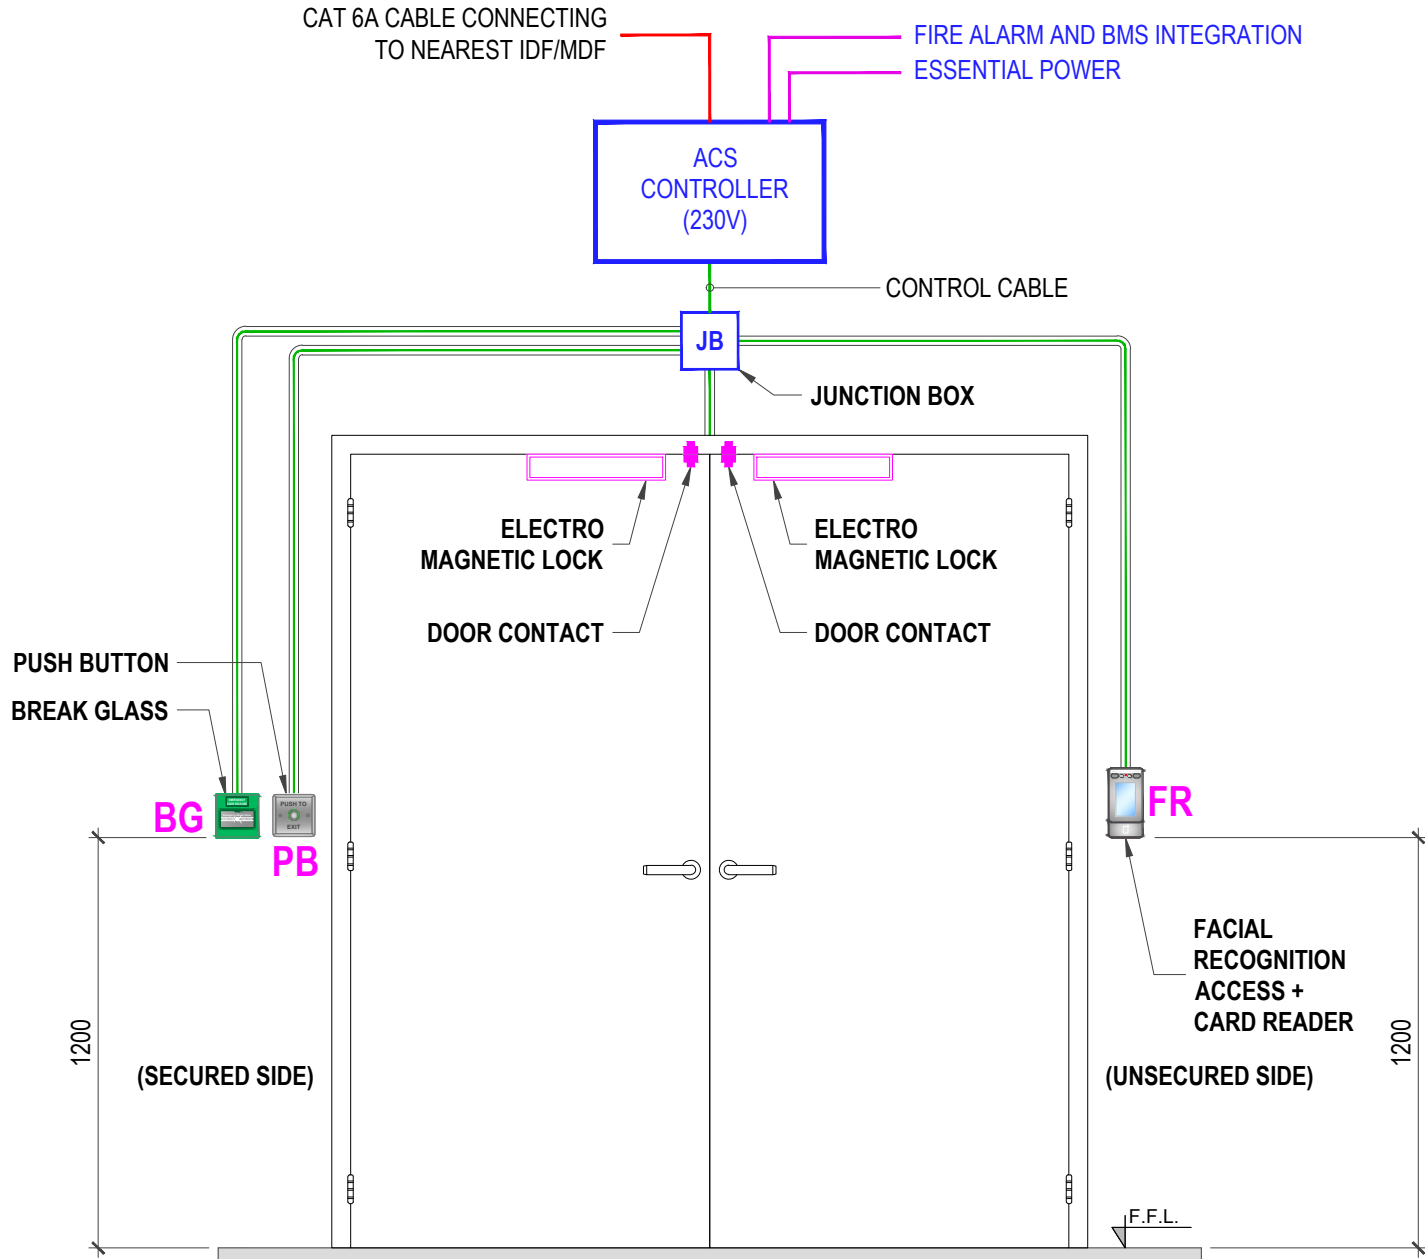


2 DOUBLE DOOR
2xDC + 2xEML + FR + BG + PB
NOT TO SCALE

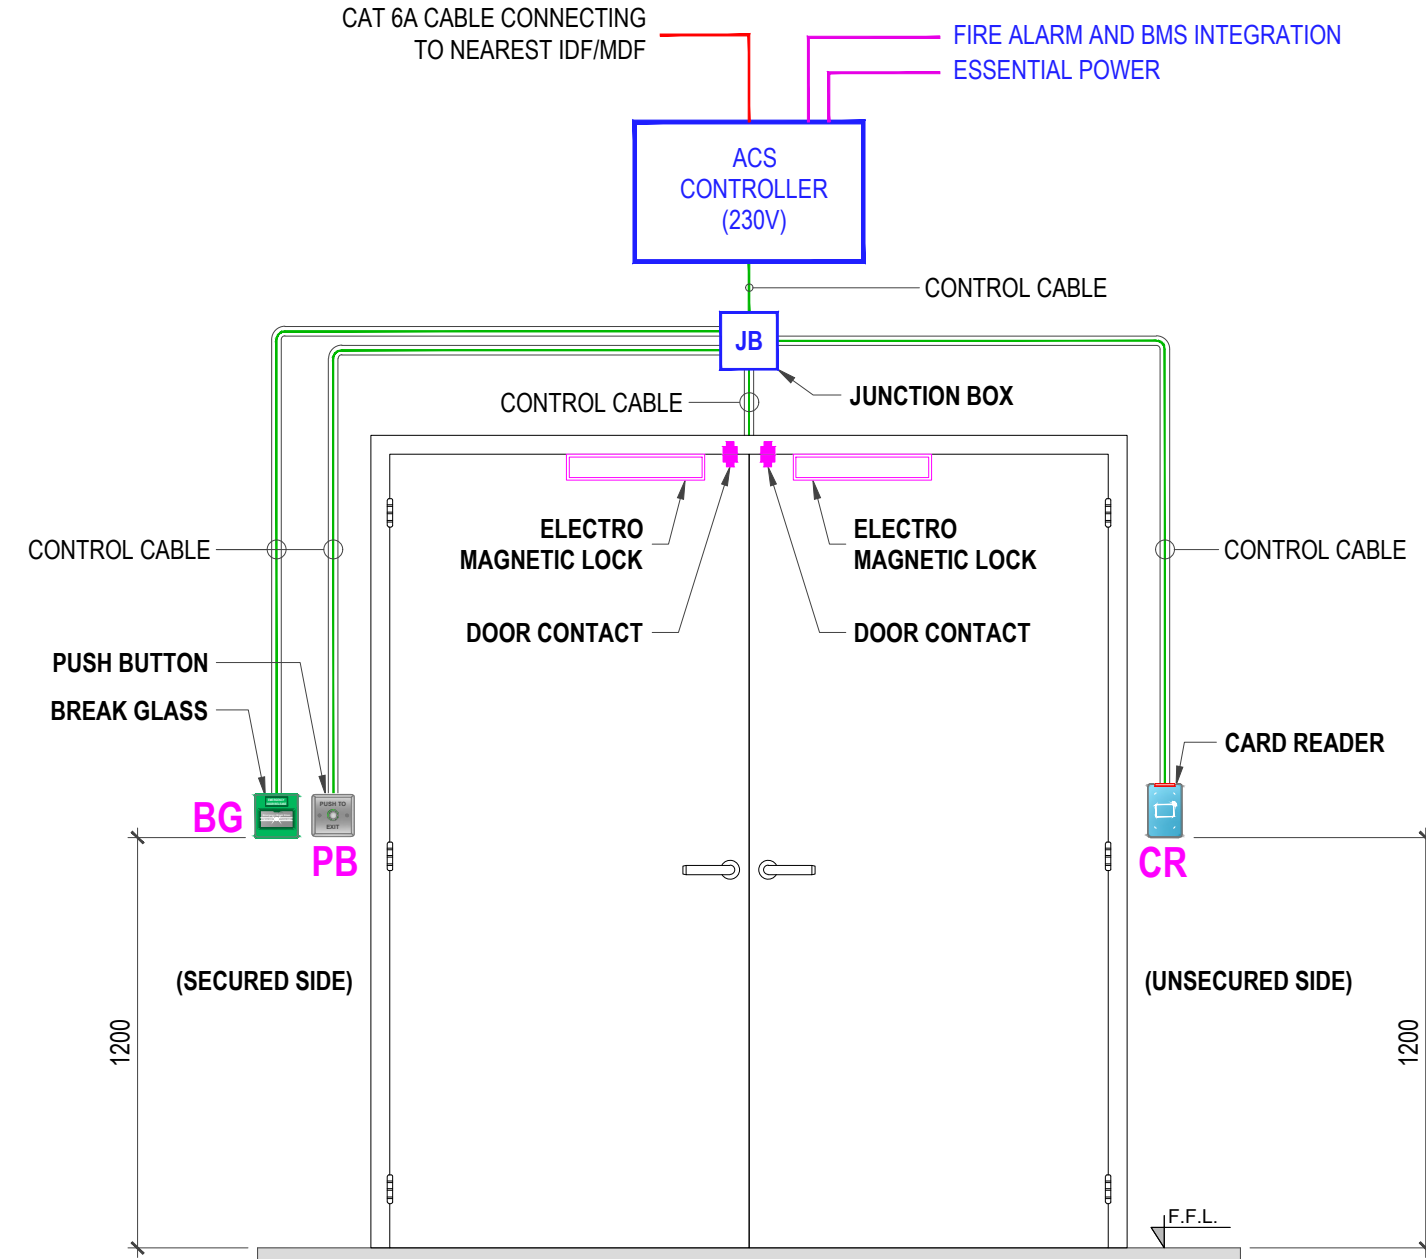



3 DOUBLE DOOR
2xDC + 2xEML + CR + BG + PB
NOT TO SCALE

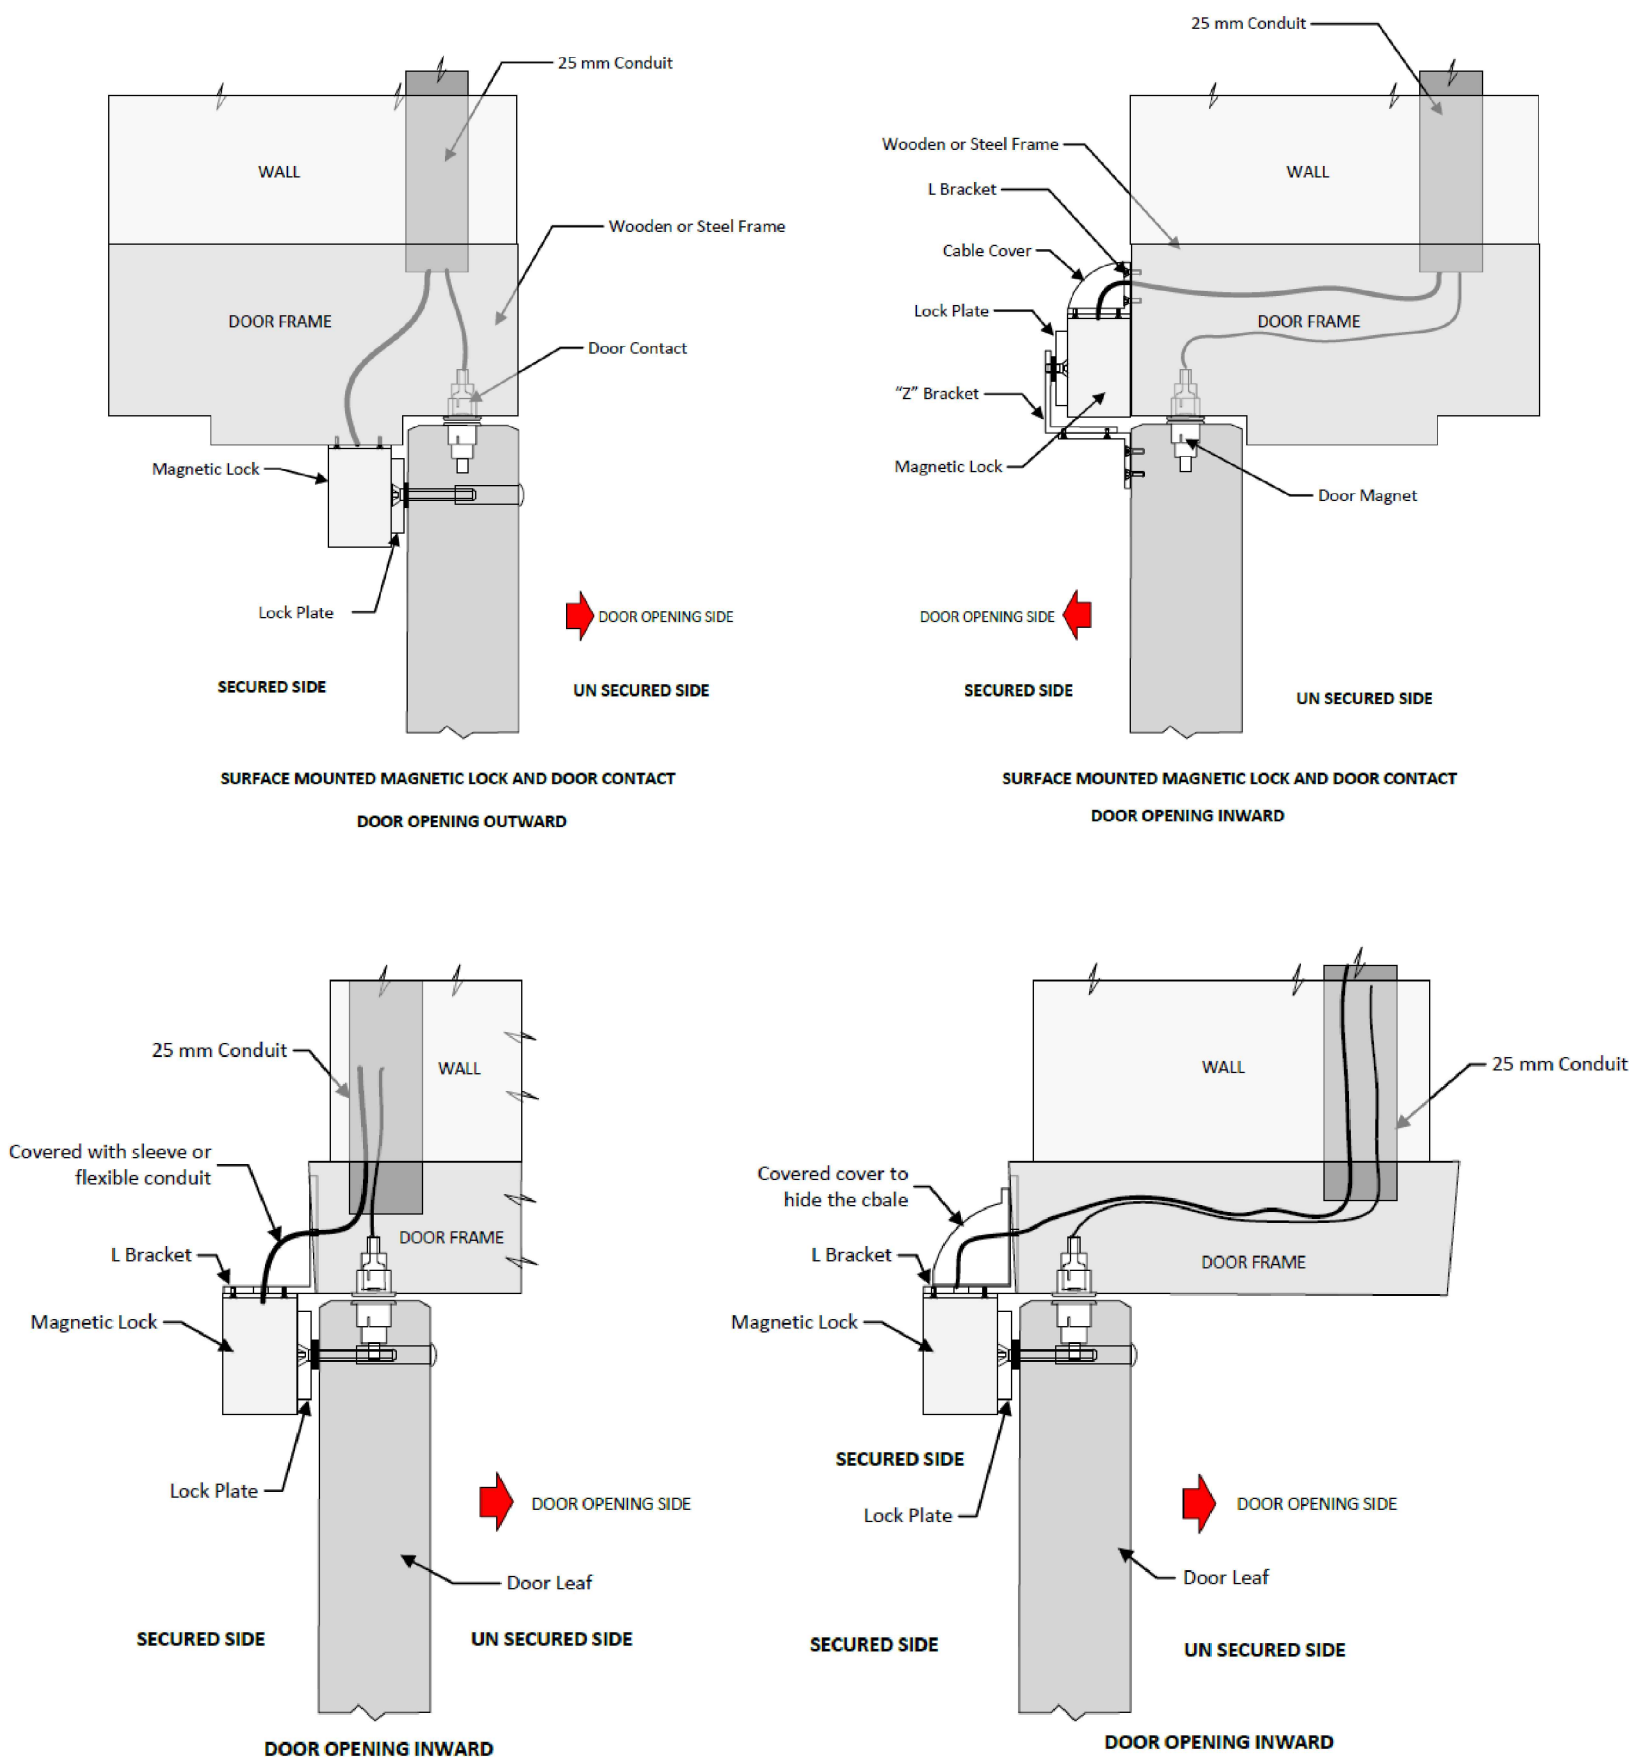

4 DOOR CONTACT & ELECTRO MAGNETIC LOCK
TYPICAL POSITIONING IN WOOD OR STEEL DOOR
NOT TO SCALE

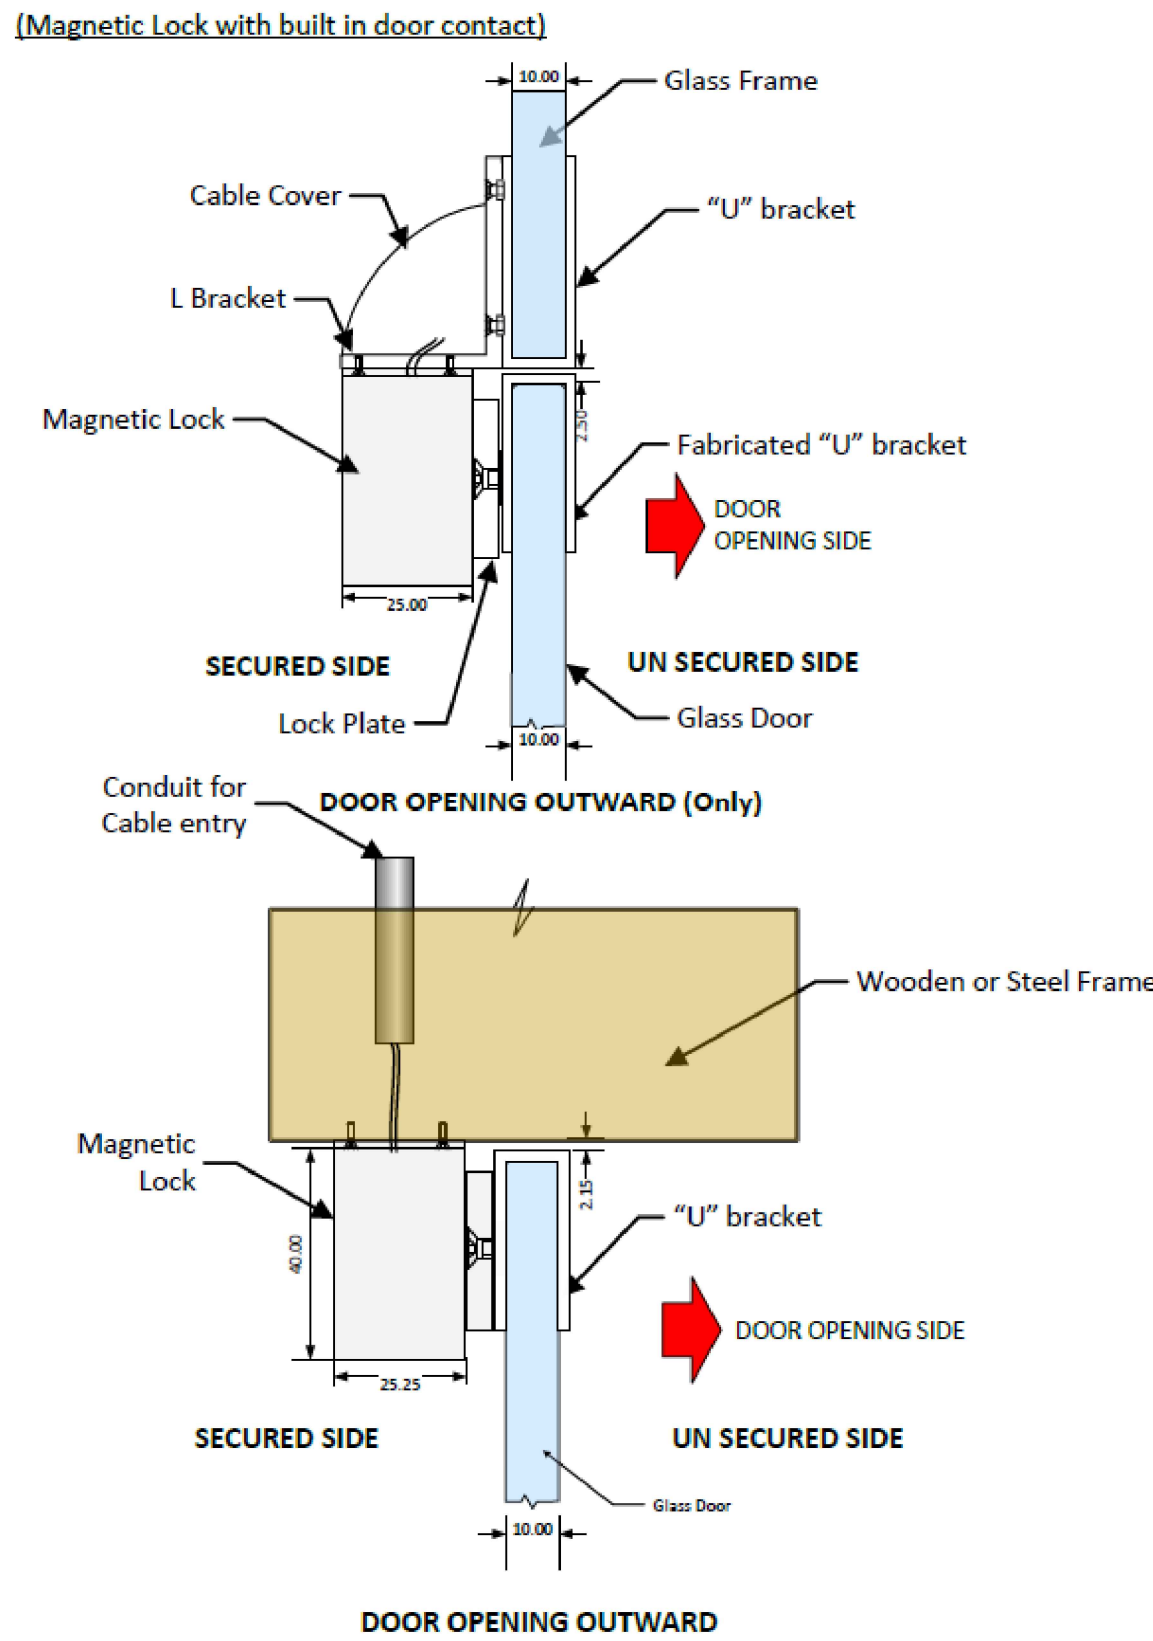

5 DOOR CONTACT & ELECTRO MAGNETIC LOCK
TYPICAL POSITIONING IN GLASS DOOR
NOT TO SCALE

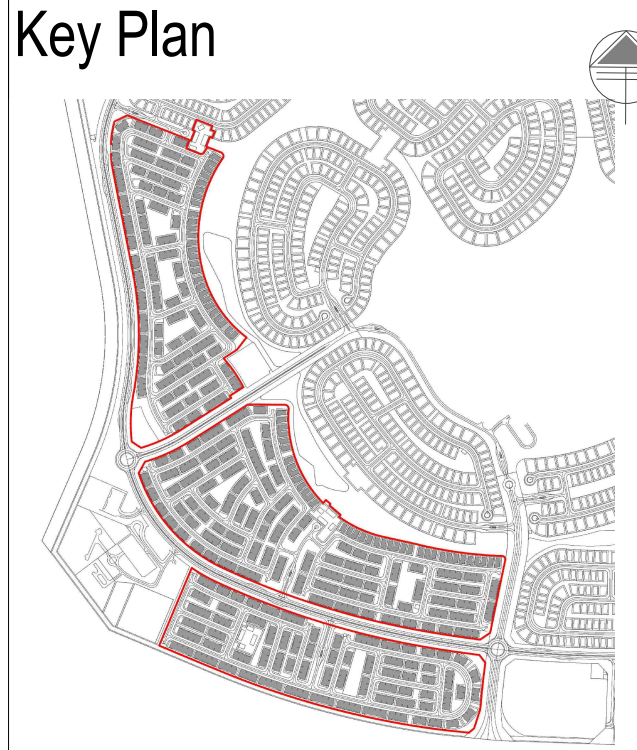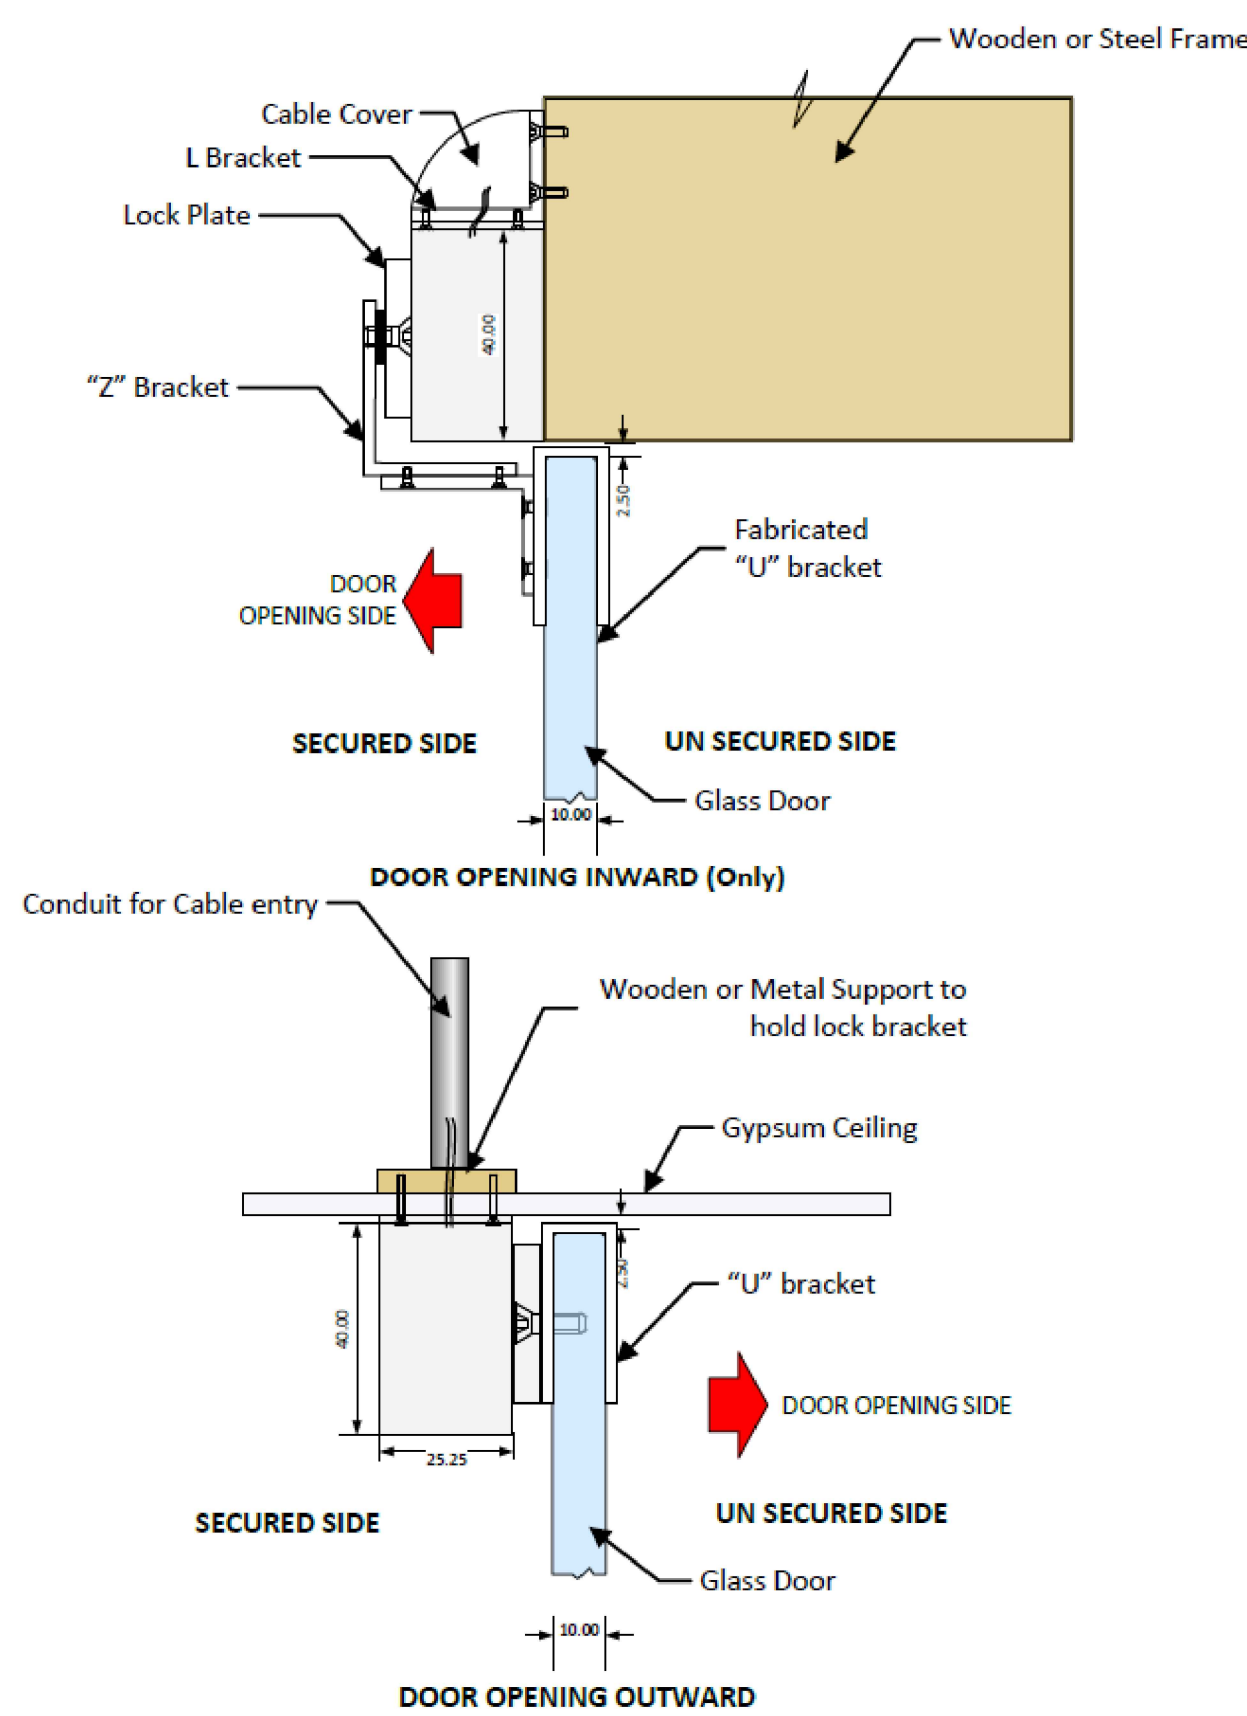

- General Notes :**
01. Do not Scale The Drawings. Follow (The MM) Written Dimensions Unless Otherwise Mentioned.
 02. Each Drawing Shall be Read in Conjunction With all Other Drawings, Specification & the General Standard Details. In Case of Any Discrepancies Bring it to the Knowledge of Engineer and Same to be Resolved Prior to Execution of Work.
 03. Dimensions Shown on These Drawings are Structural Dimensions Unless Noted Otherwise.
 04. All Levels Indicated On These Drawings are Levels as per the the Survey Datum, Same Should be Verified at Site Prior to Execution of Work.
 05. All Levels Indicated On These Drawings are Based On Design Level, Which is Equivalent to Datum Level and Same Should be Verified at Site Prior to Execution of Work.

- IES NOTE: CCTV + INTRUSION + ACCESS CONTROL**
1. THE LOCATIONS OF CCTV, ALARM, AND ACS COMPONENTS ARE INDICATED APPROXIMATELY ON THE DRAWINGS AND ARE SUBJECT TO ON-SITE VERIFICATION.
 2. EXACT LOCATIONS AND HEIGHTS OF COMPONENTS WILL BE FINALIZED IN COORDINATION WITH THE CONTRACTOR ON-SITE, CONSIDERING BUILDING LAYOUT, INTERIOR DESIGN, DECORATION, AND ANY OTHER RELEVANT SERVICES OR COMPONENTS.
 3. ON-SITE, COORDINATION WITH THE CONTRACTOR IS ESSENTIAL TO ADDRESS ANY POTENTIAL OBSTRUCTIONS TO THE CAMERA'S FIELD OF VIEW, IN COMPLIANCE WITH DUBAI LAW 12/2016, AS WELL AS TO MITIGATE ELECTROMAGNETIC INTERFERENCE (EMI) IMPACTING ELECTRONIC SECURITY COMPONENTS.
 4. THIS DESIGN WILL BECOME INVALID IF THERE ARE ANY MODIFICATIONS TO THE ARCHITECTURAL PLANS OR CHANGES IN LEGAL REQUIREMENTS.
 5. LOW-LIGHT AREAS SHOULD BE EQUIPPED WITH INFRARED (IR) OR NIGHT VISION CAMERAS TO ENSURE PROPER COVERAGE AND VISIBILITY.

TENDER DRAWINGS

09	10/03/2026	JP	TENDER SUBMISSION
No.	Date	Initials	Description

REVISIONS / ISSUE

THIS DRAWING MUST NOT BE REPRODUCED IN WHOLE OR IN PART WITHOUT THE PRIOR APPROVAL OF ARIF & BINTOAK

Status: **TENDER SUBMISSION**

Client: **EMAAR**

Lead Consultant: **عارف وبن طوق Arif&Bintoak**
consulting architects & engineers
POST BOX 3670 DUBAI U.A.E. TEL: 04-3972888 FAX: 04-3379352
POST BOX 42981 ABU DHABI U.A.E. TEL: 02-4346659 -ariftoak@emaar.ae

Security Consultant: **INTERNATIONAL ELECTRONIC SECURITY**
TEL: 04 397 0757, FAX: 04 397 0754
P.O. BOX 12734 DUBAI - U.A.E
ENQUIRIES@IESCONSULTING.AE
AUDIT@IESCONSULTING.AE
WWW.IESCONSULTING.AE

Project Title: **Proposed Residential Townhouses and Standalone Villas TH-1, TH-2, and TH-3 at Grand Polo Club & Resort, Dubai, UAE**

Discipline: **SECURITY**

Drawing Title: **ACCESS CONTROL SYSTEM
TYPICAL INSTALLATION DETAILS
COMMUNITY CENTER & GUARD HOUSE - TH-02**

Architectural Engineer	Electrical Engineer	Structural Engineer
MUSTAFA ABID	MARWAN MOHD.	RIHAM RAMADAN
Registration # 5847	Registration # 58102	Registration # 105092
Scale(s): NTS	Date drawn: 10/03/2026	Project no: 1857
Drawn by: JP	Checked: MM	Approved: JR
Drawing Number: GPCR-TH02-IES-INS-SEC-ACS-1000-00		