

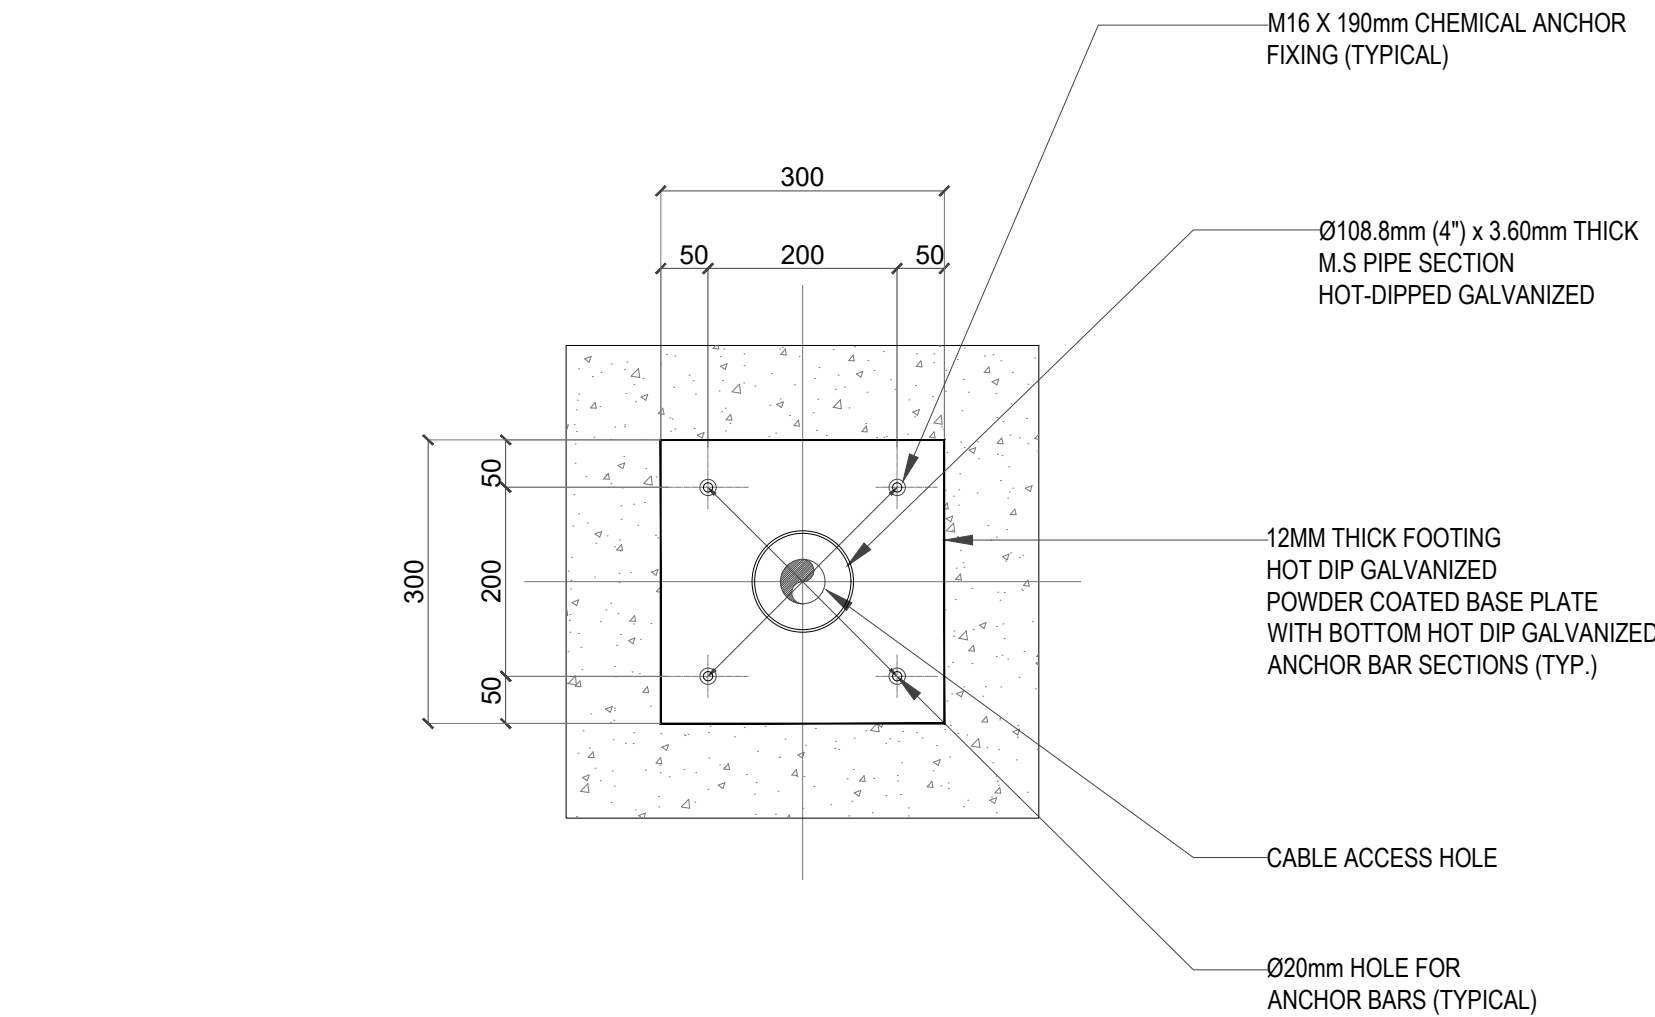


1
DOME CAMERA
TYPICAL POLE MOUNTED DETAILS
NOT TO SCALE

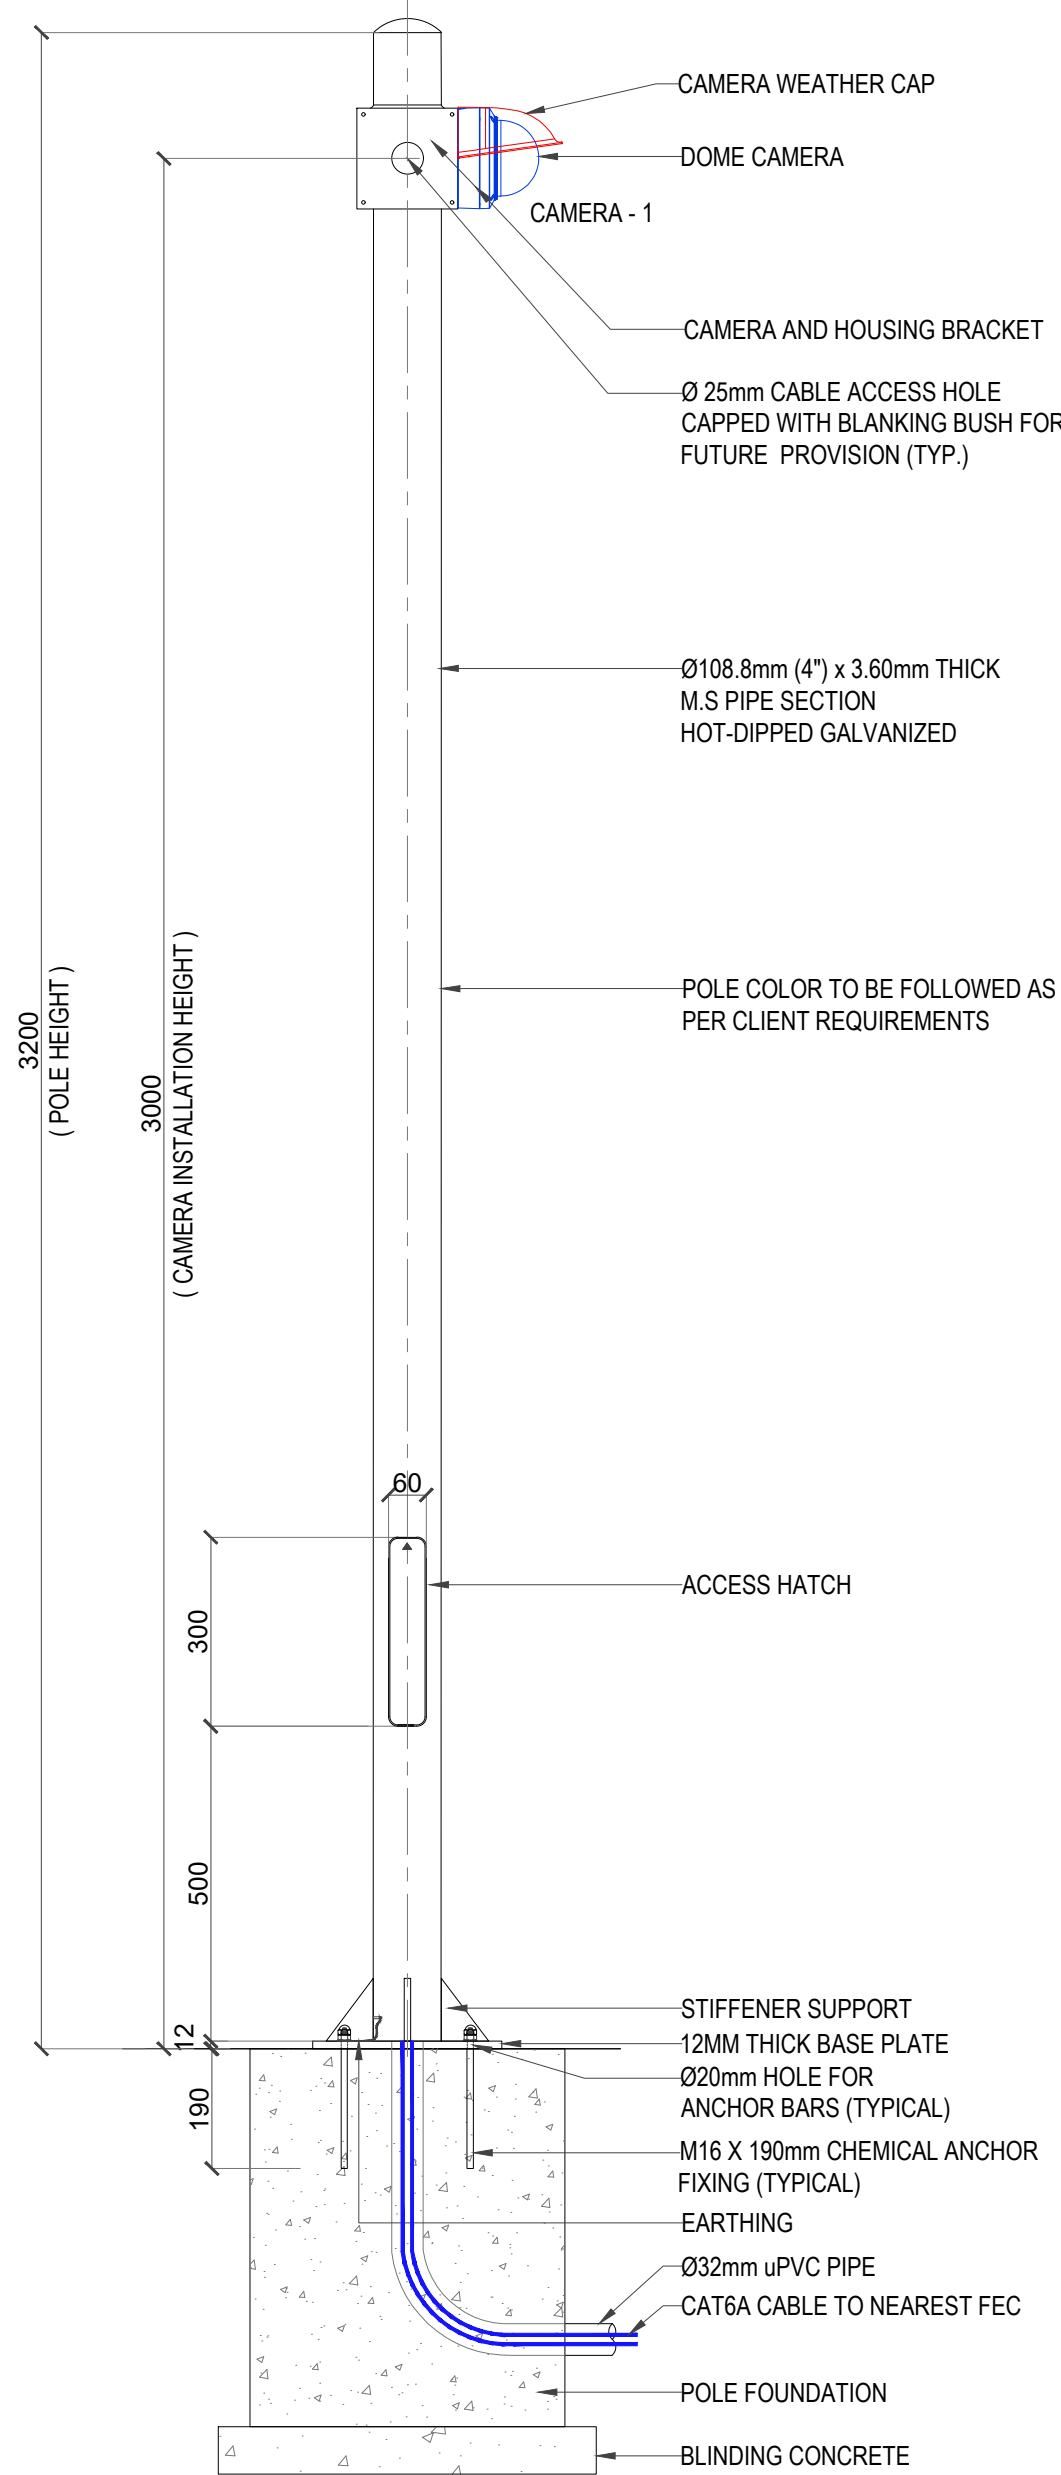


6
BASE PLATE DETAILS
NOT TO SCALE


2
OUTDOOR CAMERA W/ WEATHER CAP
TYPICAL WALL MOUNTED DETAILS
NOT TO SCALE

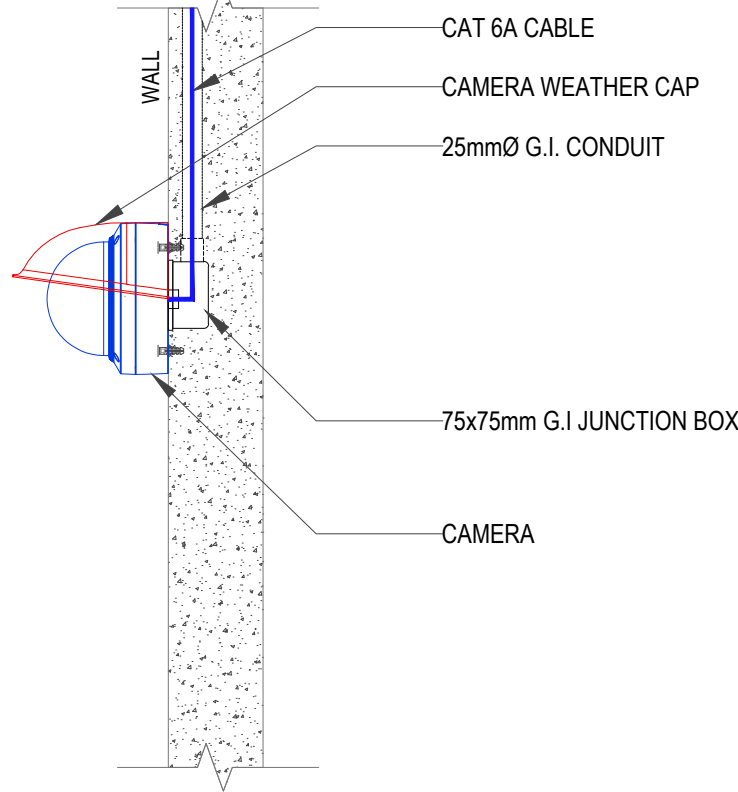


4
INDOOR CAMERA
TYPICAL WALL MOUNTED DETAILS
NOT TO SCALE

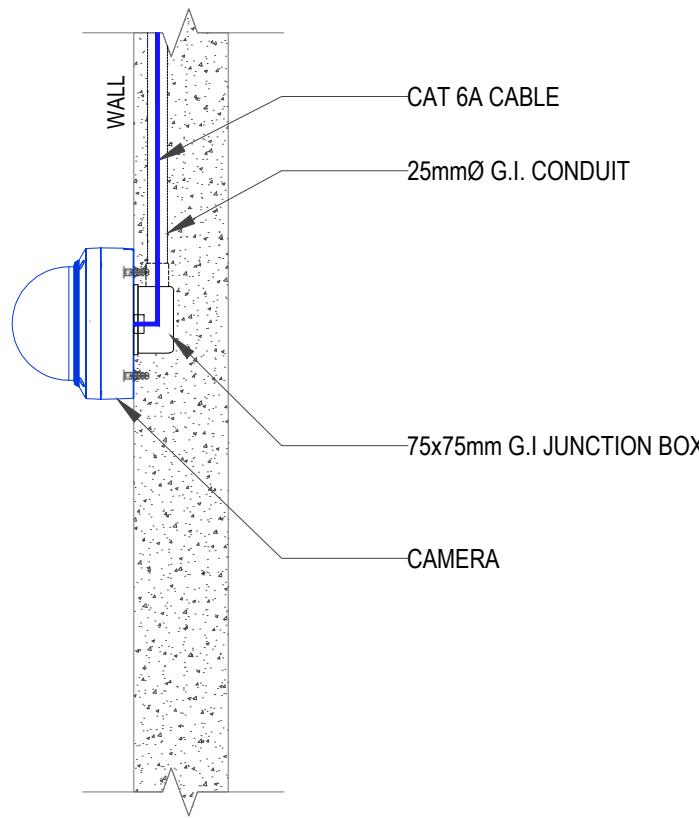


3
OUTDOOR CAMERA W/ BRACKET
TYPICAL WALL MOUNTED DETAILS
NOT TO SCALE

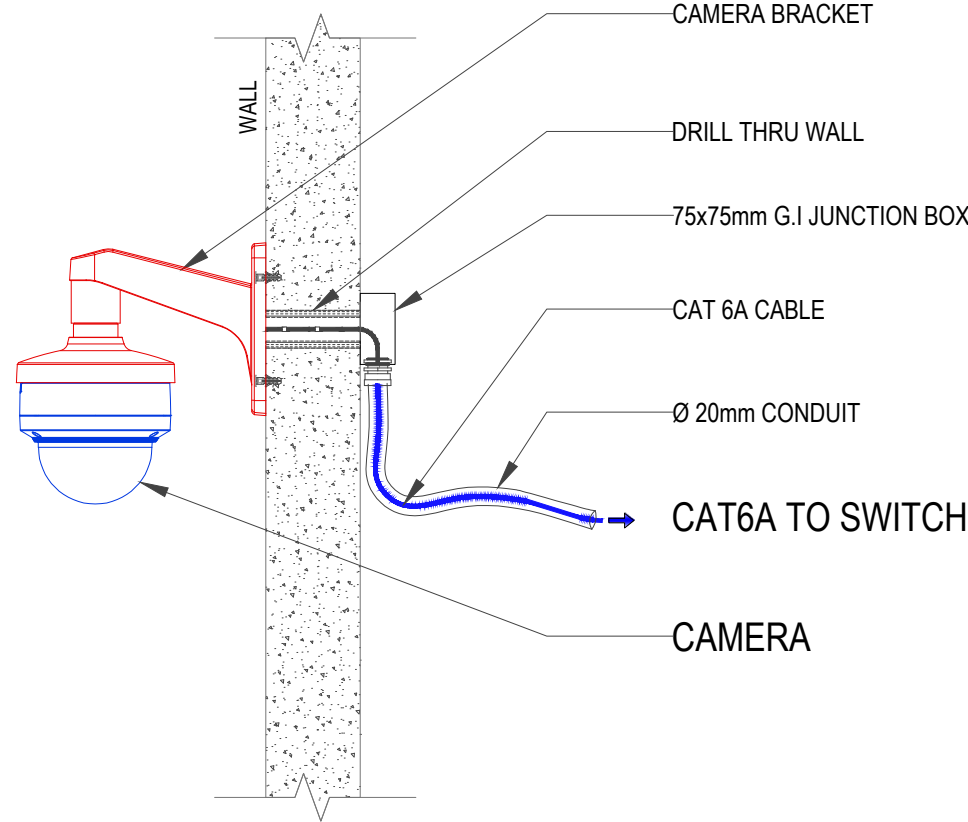


5
INDOOR / OUTDOOR CAMERA
TYP. FALSE CEILING MOUNTED DETAILS
NOT TO SCALE

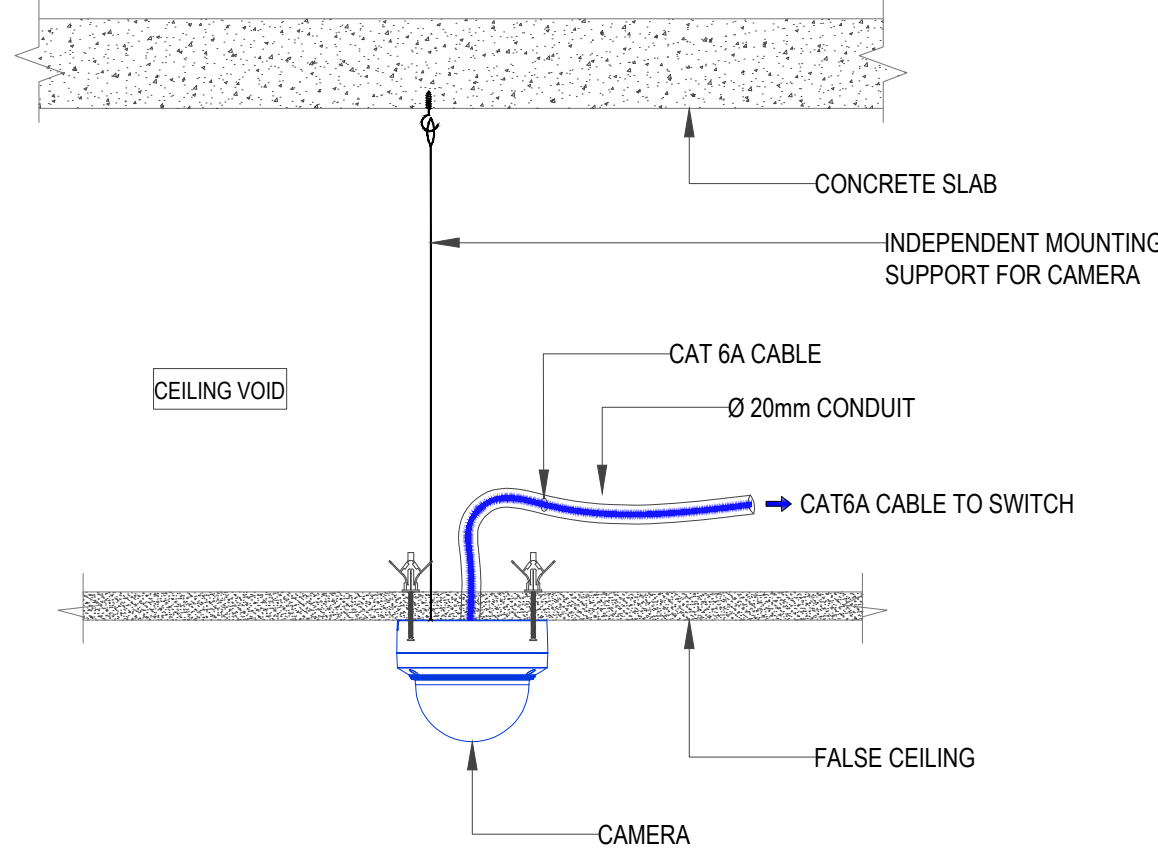


7
CAMERA POLE CASING
ISOMETRIC DETAILS
NOT TO SCALE

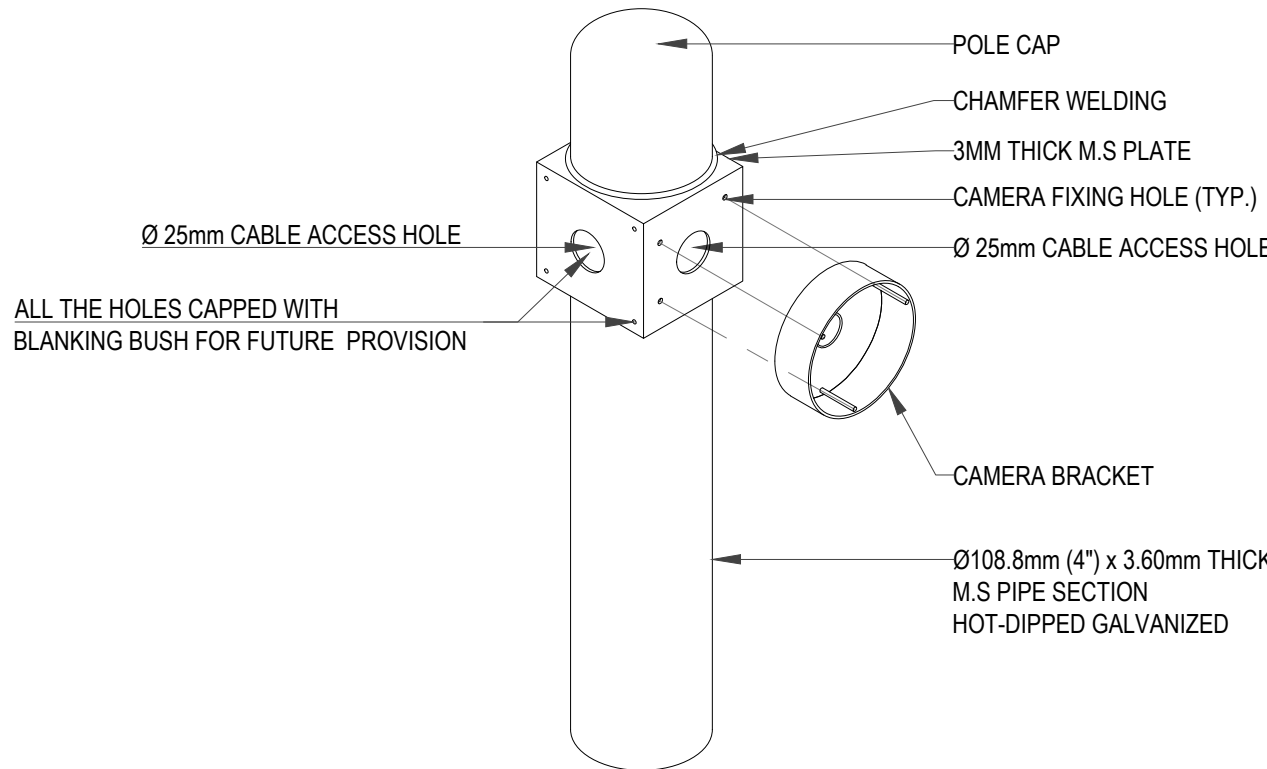


8
CAMERA WEATHER CAP
NOT TO SCALE

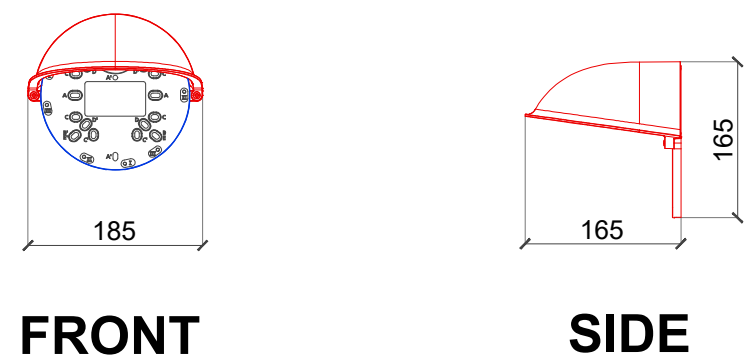

9
CAMERA MOUNTING PLATE
NOT TO SCALE

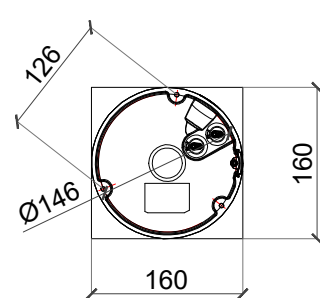

Key Plan

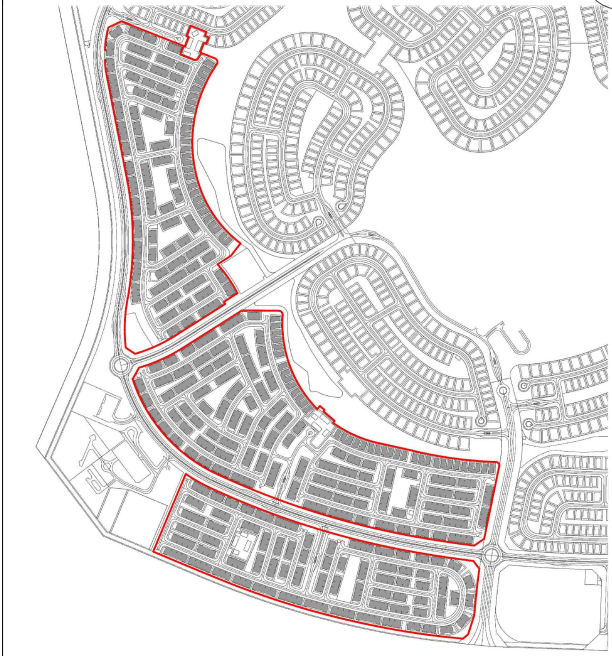

- General Notes :
- Do not Scale The Drawings. Follow (The MM) Written Dimensions Unless Otherwise Mentioned.
 - Each Drawing Shall be Read in Conjunction With all Other Drawings, Specification & the General Standard Details. In Case of Any Discrepancies Bring it to the Knowledge of Engineer and Same to be Resolved Prior to Execution of Work.
 - Dimensions Shown on These Drawings are Structural Dimensions. Unless Noted Otherwise.
 - All Levels Indicated On These Drawings are Levels as per the the Survey Datum, Same Should be Verified at Site Prior to Execution of Work.
 - All Levels Indicated On These Drawings are Based On Design Level, Which is Equivalent to Datum Level and Same Should be Verified at Site Prior to Execution of Work.

- IES NOTE: CCTV + INTRUSION + ACCESS CONTROL
- THE LOCATIONS OF CCTV, ALARM, AND ACS COMPONENTS ARE INDICATED APPROXIMATELY ON THE DRAWINGS AND ARE SUBJECT TO ON-SITE VERIFICATION.
 - EXACT LOCATIONS AND HEIGHTS OF COMPONENTS WILL BE FINALIZED IN COORDINATION WITH THE CONTRACTOR ON-SITE, CONSIDERING BUILDING LAYOUT, INTERIOR DESIGN, DECORATION, AND ANY OTHER RELEVANT SERVICES OR COMPONENTS.
 - ON-SITE, COORDINATION WITH THE CONTRACTOR IS ESSENTIAL TO ADDRESS ANY POTENTIAL OBSTRUCTIONS TO THE CAMERA'S FIELD OF VIEW, IN COMPLIANCE WITH DUBAI LAW 12/2016, AS WELL AS TO MITIGATE ELECTROMAGNETIC INTERFERENCE (EMI) IMPACTING ELECTRONIC SECURITY COMPONENTS.
 - THIS DESIGN WILL BECOME INVALID IF THERE ARE ANY MODIFICATIONS TO THE ARCHITECTURAL PLANS OR CHANGES IN LEGAL REQUIREMENTS.
 - LOW-LIGHT AREAS SHOULD BE EQUIPPED WITH INFRARED (IR) OR NIGHT VISION CAMERAS TO ENSURE PROPER COVERAGE AND VISIBILITY.



No.	Date	Initials	Description
01	10/03/2026	JP	TENDER SUBMISSION
REVISIONS / ISSUE			
THIS DRAWING MUST NOT BE REPRODUCED IN WHOLE OR IN PART WITHOUT THE PRIOR APPROVAL OF ARIF & BINTOAK			
Status			
TENDER SUBMISSION			
Client			

EMAAR

Lead Consultant
Arif & BintOak
consulting architects & engineers
POST BOX 3676 DUBAI UAE TEL: 04-3772888 FAX: 04-3770552
POST BOX 42981 ABU DHABI UAE TEL: 02-454659 arif@arifbintoak.net.ae

Security Consultant
INTERNATIONAL ELECTRONIC SECURITY
TEL: 04 397 0757, FAX: 04 397 0754
P.O. BOX 12734 DUBAI - U.A.E
ENQUIRIES@IESCONSULTING.AE
AUDIT@IESCONSULTING.AE
WWW.IESCONSULTING.AE

Project Title:
Proposed Residential Townhouses and Standalone Villas TH-1, TH-2, and TH-3 at Grand Polo Club & Resort, Dubai, UAE

Discipline : SECURITY
Drawing title:
TYPICAL SECURITY CAMERA INSTALLATION DETAILS
COMMUNITY CENTER & GUARD HOUSE - TH-02

Architectural Engineer	Electrical Engineer	Structural Engineer
MUSTAFA ABID	MARWAN MOHD.	RIHAM RAMADAN
Registration # 5847	Registration # 80102	Registration # 105092
Scale(s):	Date drawn: 10/03/2026	Project no: 1857
Drawn by: JP	Checked: MM	Approved: JR
Drawing Number: GPCR-TH02-IES-INS-SEC-VSS-1000-00		