



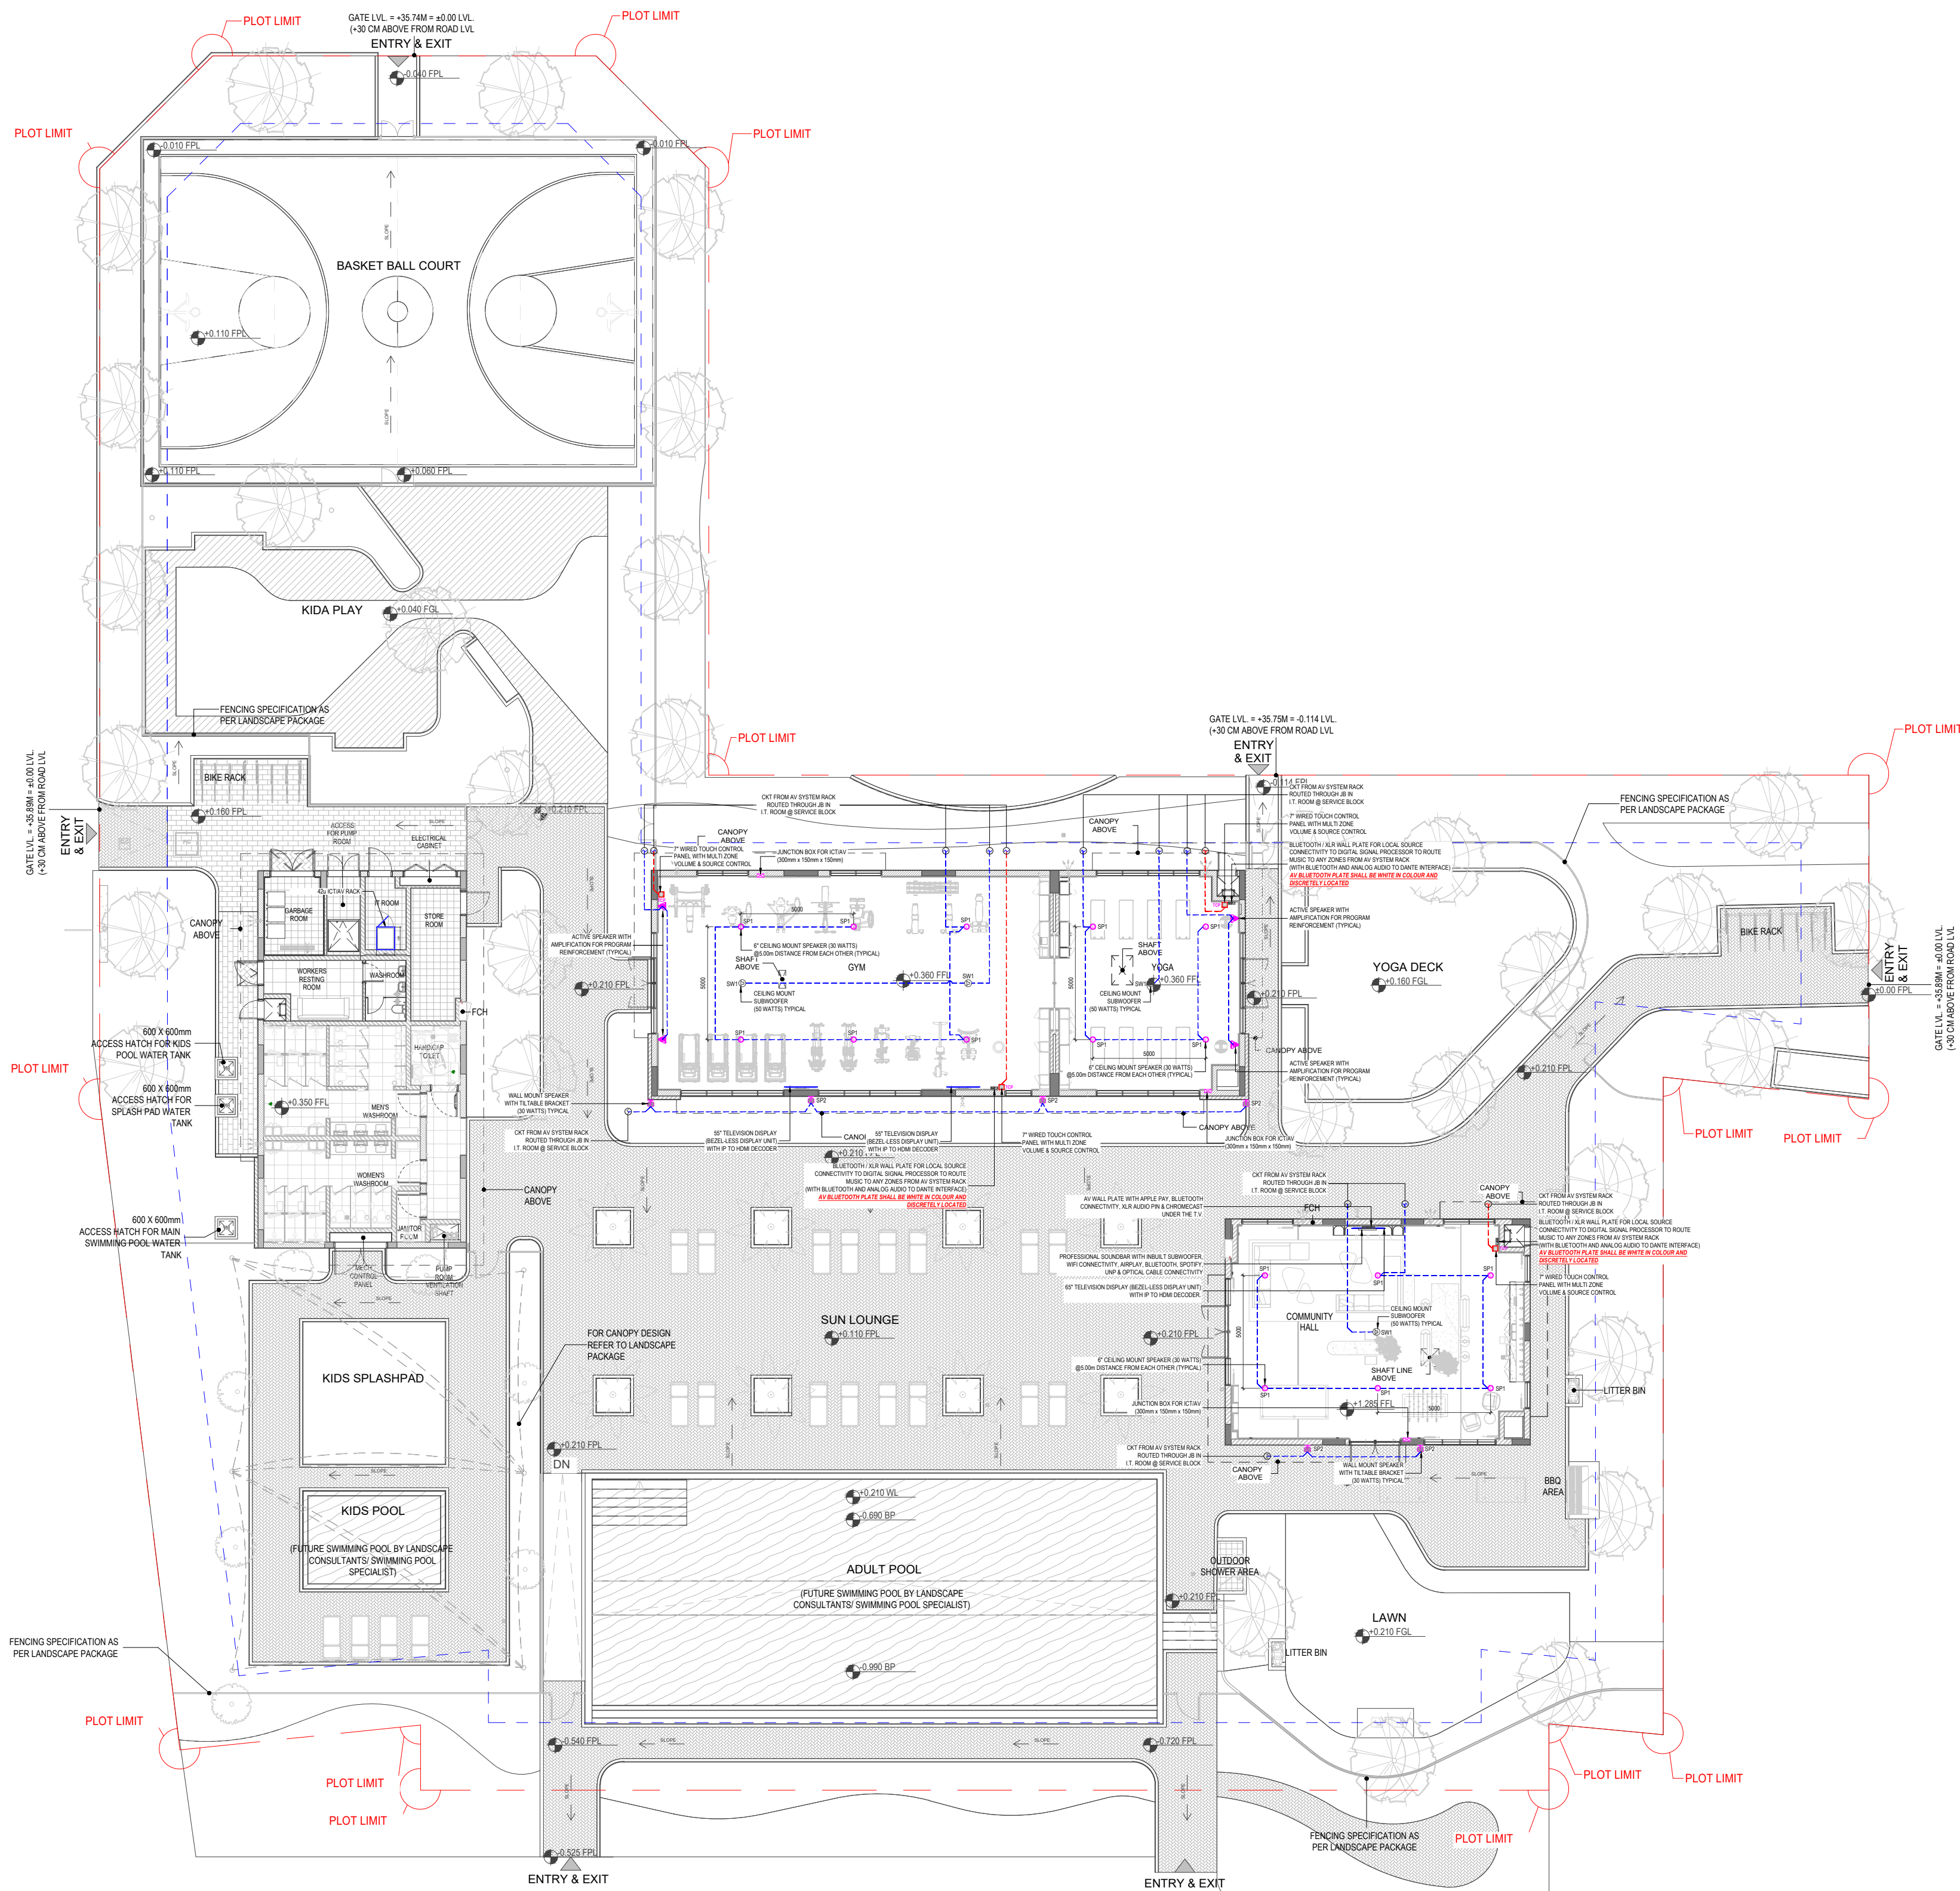

- NOTE: AUDIO VISUAL (AV)**
1. SPEAKER LOCATION ARE INDICATIVE ONLY.KINDLY REFER ID DRAWINGS. AV CONTRACTOR SHOULD CO-ORDINATE WITH MEP, ARCHITECT ON SITE.
 2. ALL AV EQUIPMENT SHOULD HAVE RAL COLOR MATCHING WITH ID REQUIREMENTS
 3. INSTALLATION OF DISPLAY SCREENS, AV EQUIPMENT, RESPECTIVE CABLES & CONNECTORS SHOULD MATCH SITE REQUIREMENT
 4. ALL AV EQUIPMENT SHOULD BE PRO-AUDIO. ALL EQUIPMENTS SHOULD HAVE RS232 CONTROL PORT & SHOULD HAVE PROPER FEED BACK.
 5. AV BLUETOOTH PLATE SHALL BE WHITE IN COLOUR AND DISCREETLY LOCATED
 6. ALL AV EQUIPMENT POWER REQUIREMENT SHOULD BE PROVIDED BY AV CONTRACTOR & CO-ORDINATE WITH RESPECTIVE CONTRACTOR.
 7. 1x13A POWER SOCKET REQUIRED FOR WP (WALL PLATE) PROVIDED BY ELECTRICAL CONTRACTOR.
 8. AV CONTRACTOR SHOULD PROVIDE TRS JACK TO USB C PATCH CABLE FOR EVERY WALL PLATE FOR MOBILE PHONE & IPAD TO PLAY LOCAL MUSIC FROM MOBILE OR IPAD.

AUDIO VISUAL SYSTEM SCHEDULE				
SYMBOL	DESCRIPTION	AV QTY.	NO. OF FLOOR	TOTAL NO OF AV
	6" CEILING MOUNT SPEAKER (30 WATTS)	16	1	16
	WALL MOUNT SPEAKER WITH TILTABLE WALL BRACKET (30 WATTS)	6	1	6
	ACTIVE SPEAKER WITH AMPLIFICATION	4	1	4
	8" CEILING MOUNT SUBWOOFER (50 WATTS)	4	1	4
	7" WIRED TOUCH CONTROL PANEL WITH MULTI ZONE VOLUME & SOURCE CONTROL	4	1	4
	AV WALL PLATE WITH BLUETOOTH CONNECTIVITY, XLR AUDIO PIN	3	1	3
	AV WALL PLATE WITH BLUETOOTH CONNECTIVITY, XLR AUDIO PIN & CHROMECAST UNDER THE T.V.	1	1	1
	55" T.V. LED BEZEL LESS DISPLAY ULTRA HD, 4K RESOLUTION	2	1	2
	65" T.V. LED BEZEL LESS DISPLAY ULTRA HD, 4K RESOLUTION	1	1	1
	IP TO HDMI DECODER	1	1	1
	PROFESSIONAL SOUNDBAR WITH INBUILT SUBWOOFER, WIFI CONNECTIVITY, AIRPLAY, BLUETOOTH, SPOTIFY, UNP & OPTICAL CABLE CONNECTIVITY	1	1	1

LEGEND		
SYMBOL	DESCRIPTION	TOTAL NO.
	JUNCTION BOX FOR ICT/AV (300mm x 150mm x 150mm)	3
	42U ICT / AV RACK (FREE STANDING)	1

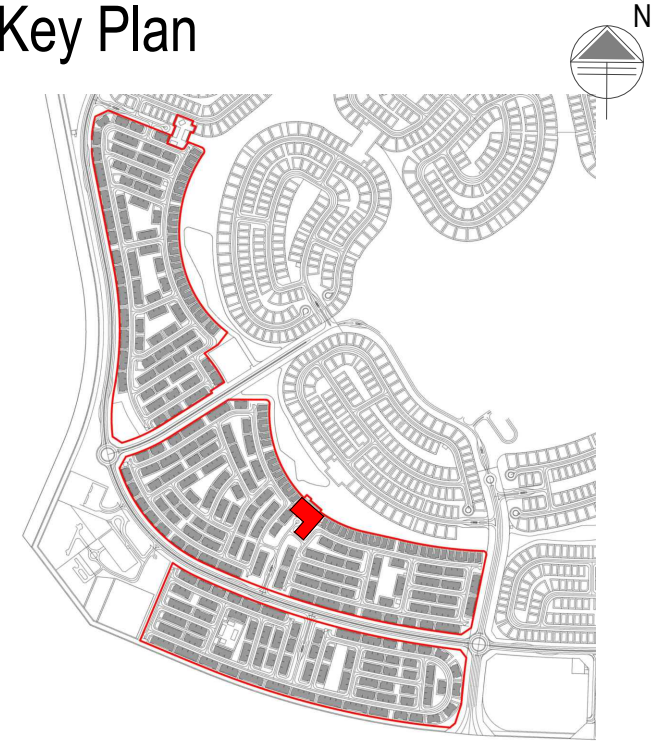

- General Notes :**
01. Do not Scale The Drawings. Follow (The MM) Written Dimensions Unless Otherwise Mentioned.
 02. Each Drawing Shall be Read in Conjunction With all Other Drawings, Specification & the General Standard Details. In Case of Any Discrepancies Bring it to the Knowledge of Engineer and Same to be Resolved Prior to Execution of Work.
 03. Dimensions Shown on These Drawings are Structural Dimensions. Unless Noted Otherwise.
 04. All Levels Indicated On These Drawings are Levels as per the the Survey Datum, Same Should be Verified at Site Prior to Execution of Work.
 05. All Levels Indicated On These Drawings are Based On Design Level, Which is Equivalent to Datum Level and Same Should be Verified at Site Prior to Execution of Work.



09	10/03/2026	JP	TENDER SUBMISSION
No.	Date	Initials	Description
REVISIONS / ISSUE			
THIS DRAWING MUST NOT BE REPRODUCED IN WHOLE OR IN PART WITHOUT THE PRIOR APPROVAL OF ARIF & BINTOAK			
Status	TENDER SUBMISSION		
Client	EMAAR		
Lead Consultant	عارف وبن طوق Arif&Bintoak consulting architects & engineers POST BOX 3676 DUBAI UAE TEL: 84-3272868 FAX: 84-3270352 POST BOX 42581 ABU DHABI UAE TEL: 62-434669 -arfoak@emirates.net.ae		
Security Consultant	INTERNATIONAL ELECTRONIC SECURITY TEL: 04 397 0757, FAX: 04 397 0754 P.O. BOX 12734 DUBAI - U.A.E ENQUIRIES@IESCONSULTING.AE AUDIT@IESCONSULTING.AE WWW.IESCONSULTING.AE		

Project Title:
Proposed Residential Townhouses and Standalone Villas TH-1, TH-2, and TH-3 at Grand Polo Club & Resort, Dubai, UAE

Discipline :	AUDIO VISUAL (AV)	
Drawing title:	OVERALL GROUND FLOOR PLAN AV SYSTEM LAYOUT COMMUNITY CENTER - TH-02	
Architectural Engineer	Electrical Engineer	Structural Engineer
MUSTAFA ABID	MARWAN MOHD.	RIHAM RAMADAN
Registration # 5847	Registration # 80102	Registration # 105092
Scale(s):	Date drawn: 10/03/2026	Project no: 1857
1 : 200		
Drawn by: JP	Checked: MM	Approved: JR
Drawing Number :	GPCR-TH02-IES-PL-CC2-AVC-AV-0001-00	