


Key Plan

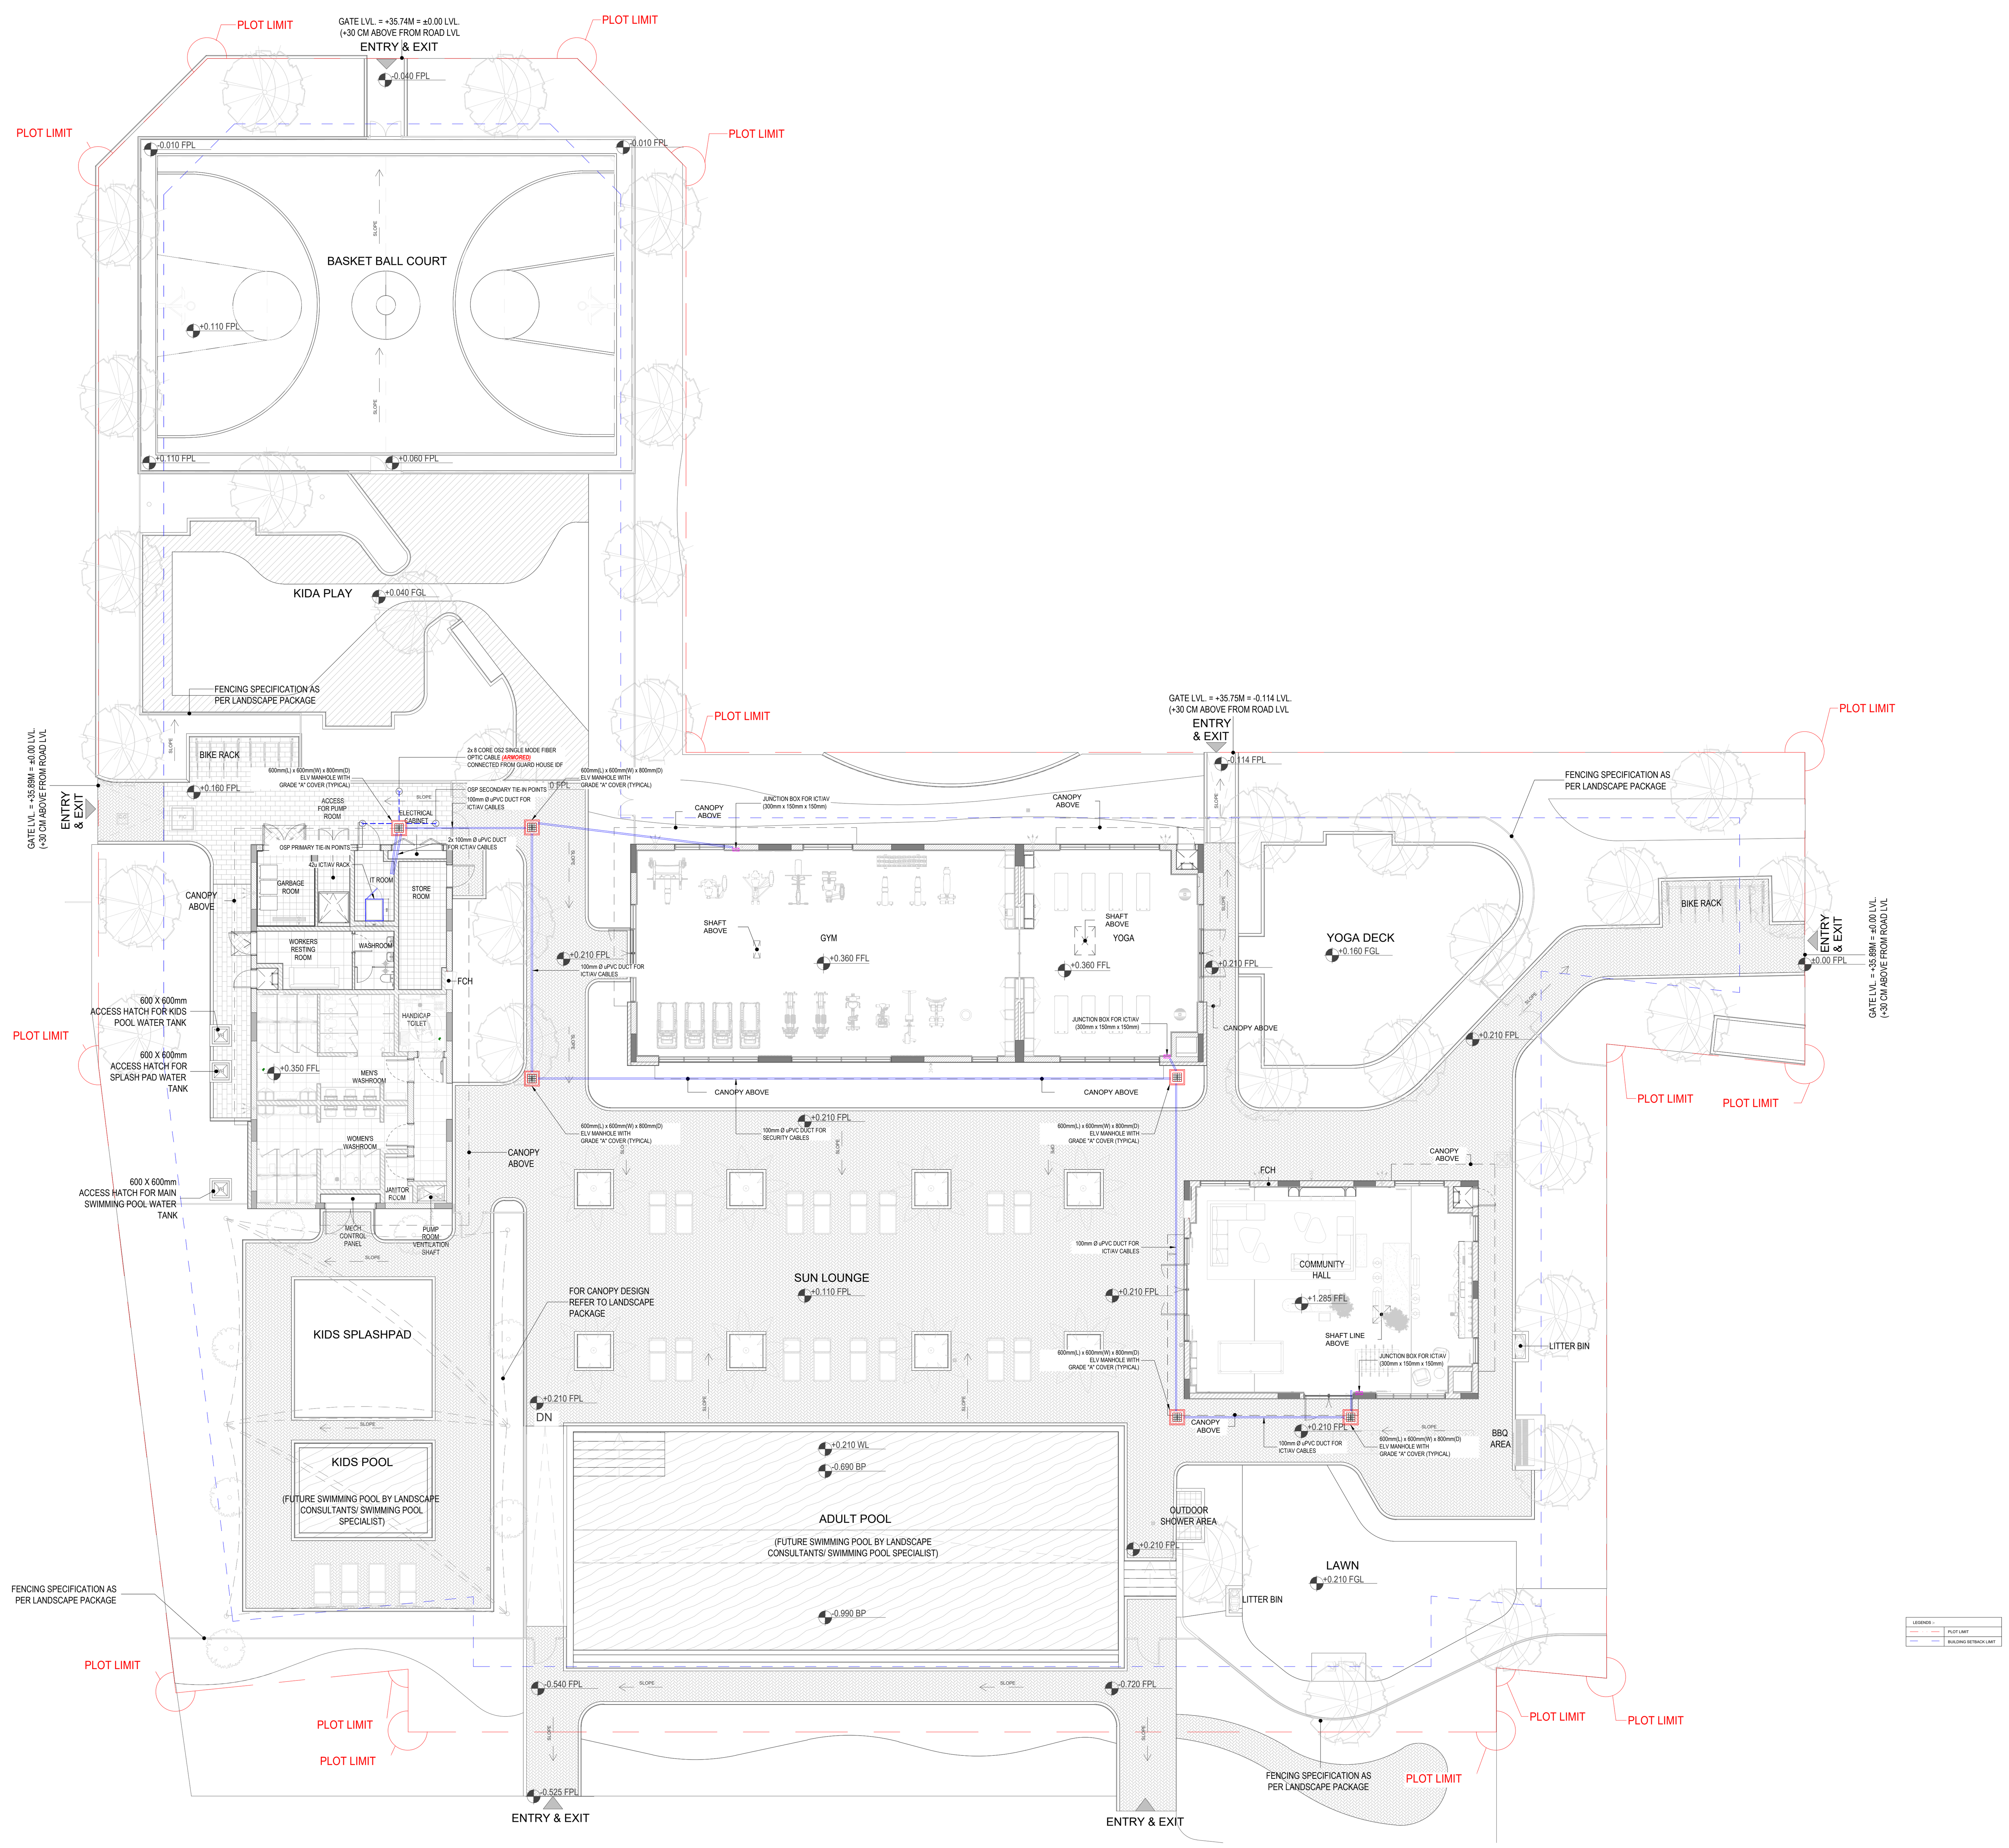

General Notes :

01. Do not Scale The Drawings. Follow (The MM) Written Dimensions Unless Otherwise Mentioned.
02. Each Drawing Shall be Read in Conjunction With all Other Drawings,Specification & the General Standard Details. In Case of Any Discrepancies Bring it to the Knowledge of Engineer and Same to be Resolved Prior to Execution of Work.
03. Dimensions Shown on These Drawings are Structural Dimensions. Unless Noted Otherwise.
04. All Levels Indicated On These Drawings are Levels as per the the Survey Datum, Same Should be Verified at Site Prior to Execution of Work.
05. All Levels Indicated On These Drawings are Based On Design Level, Which is Equivalent to Datum Level and Same Should be Verified at Site Prior to Execution of Work.

AB TENDER DRAWINGS

No.	Date	Initials	Description
00	10/03/2026	JP	TENDER SUBMISSION

REVISIONS / ISSUE

THIS DRAWING MUST NOT BE REPRODUCED IN WHOLE OR IN PART WITHOUT THE PRIOR APPROVAL OF ARIF & BINTOAK

Status
TENDER SUBMISSION

Client
EMAAR

Lead Consultant
عارف وبن طوق
Arif&Bintoak
consulting architects & engineers
POST BOX 3670 DUBAI.UAE TEL 04-3372888 FAX 04-3370352
POST BOX 42981 ABU DHABI.UAE TEL 02-634669 -artoak@emirates.net.ae

Security Consultant
INTERNATIONAL ELECTRONIC SECURITY
TEL 04 397 0757, FAX 04 397 0754
P.O.BOX 12734 DUBAI - U.A.E
ENQUIRIES@IESCONSULTING.AE
AUDIT@IESCONSULTING.AE
WWW.IESCONSULTING.AE

Project Title:
Proposed Residential Townhouses and Standalone Villas TH-1, TH-2, and TH-3 at Grand Polo Club & Resort, Dubai, UAE

Discipline : ICT / AV

Drawing title:
SETTING-OUT PLAN
ICT/AV SYSTEM LAYOUT
COMMUNITY CENTER - TH-02

Architectural Engineer	Electrical Engineer	Structural Engineer
MUSTAFA ABID	MARWAN MOHD.	RIHAM RAMADAN
Registration # 5847	Registration # 80102	Registration # 105092
Scale(s): 1 : 200	Date drawn: 10/03/2026	Project no: 1857
Drawn by: JP	Checked : MM	Approved : JR

Drawing Number : GPCR-TH02-IES-PL-CC2-ICT-IT-0000-00

This 2D drawing is extracted from 3D BIM Model

10/9/2025 3:20:21 PM

© AB I A1 Title Block . BIM Standard Ver. 2.0