
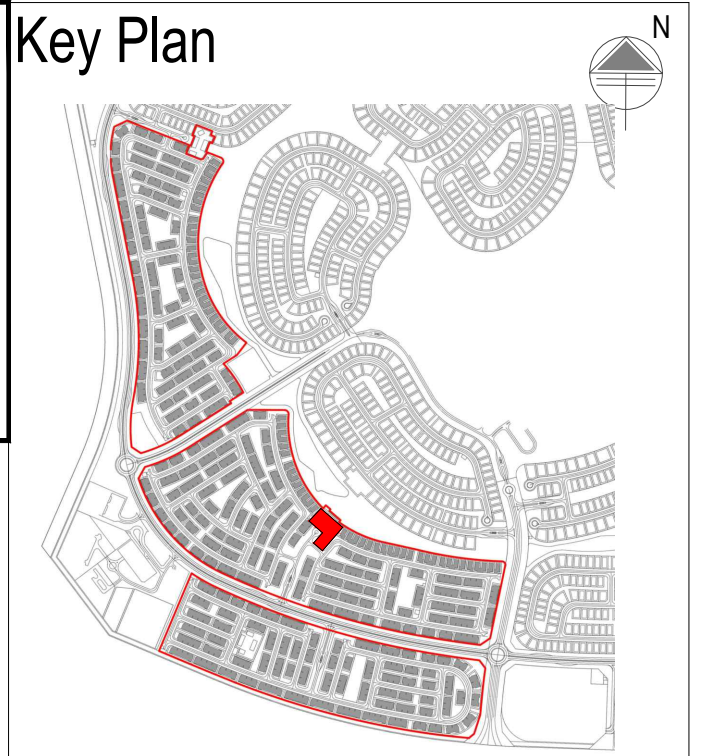


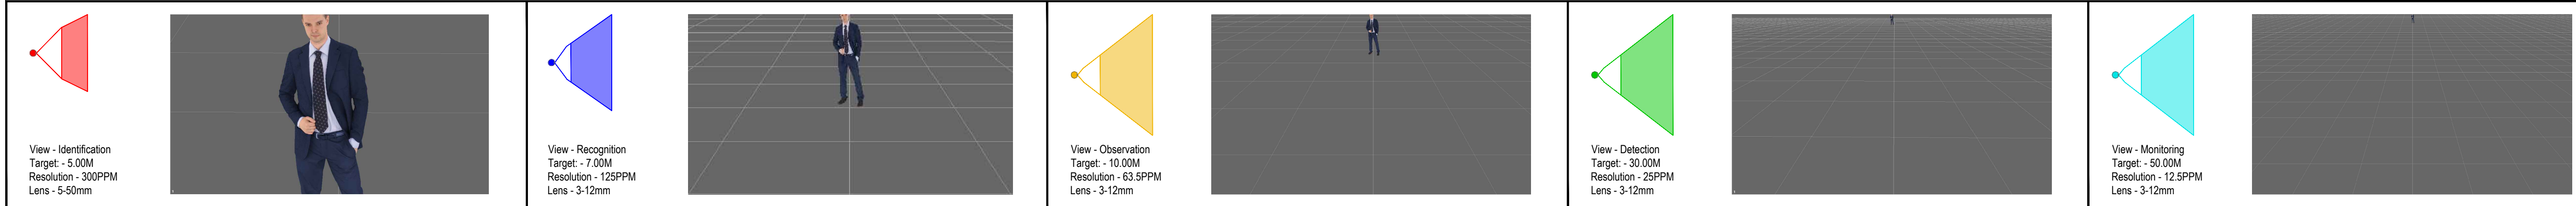

- General Notes :**
- Do not Scale The Drawings. Follow (The MM) Written Dimensions Unless Otherwise Mentioned.
 - Each Drawing Shall be Read in Conjunction With all Other Drawings, Specification & the General Standard Details. In Case of Any Discrepancies Bring it to the Knowledge of Engineer and Same to be Resolved Prior to Execution of Work.
 - Dimensions Shown on These Drawings are Structural Dimensions Unless Noted Otherwise.
 - All Levels Indicated On These Drawings are Levels as per the the Survey Datum, Same Should be Verified at Site Prior to Execution of Work.
 - All Levels Indicated On These Drawings are Based On Design Level, Which is Equivalent to Datum Level and Same Should be Verified at Site Prior to Execution of Work.

- IES NOTE: CCTV + INTRUSION + ACCESS CONTROL**
- THE LOCATIONS OF CCTV, ALARM, AND ACS COMPONENTS ARE INDICATED APPROXIMATELY ON THE DRAWINGS AND ARE SUBJECT TO ON-SITE VERIFICATION.
 - EXACT LOCATIONS AND HEIGHTS OF COMPONENTS WILL BE FINALIZED IN COORDINATION WITH THE CONTRACTOR ON-SITE, CONSIDERING BUILDING LAYOUT, INTERIOR DESIGN, DECORATION, AND ANY OTHER RELEVANT SERVICES OR COMPONENTS.
 - ON-SITE, COORDINATION WITH THE CONTRACTOR IS ESSENTIAL TO ADDRESS ANY POTENTIAL OBSTRUCTIONS TO THE CAMERA'S FIELD OF VIEW, IN COMPLIANCE WITH DUBAI LAW 12/2016, AS WELL AS TO MITIGATE ELECTROMAGNETIC INTERFERENCE (EMI) IMPACTING ELECTRONIC SECURITY COMPONENTS.
 - THIS DESIGN WILL BECOME INVALID IF THERE ARE ANY MODIFICATIONS TO THE ARCHITECTURAL PLANS OR CHANGES IN LEGAL REQUIREMENTS.
 - LOW/LIGHT AREAS SHOULD BE EQUIPPED WITH INFRARED (IR) OR NIGHT VISION CAMERAS TO ENSURE PROPER COVERAGE AND VISIBILITY.


SECURITY CAMERA SCHEDULE				
SYMBOL	DESCRIPTION	CAM. QTY.	NO. OF FLOOR	TOTAL NO. OF CAM.
	120% IDENTIFICATION CAMERA	7	1	7
	50% RECOGNITION CAMERA	4	1	4
	25% OBSERVATION CAMERA	0	1	0
	10% DETECTION CAMERA	21	1	21
	5% MONITORING CAMERA	2	1	2
	20% ANPR CAMERA	0	1	0
OVERALL TOTAL CAMERA				34

FIELD OF VIEW (FOV) LEGEND			
	120% IDENTIFICATION VIEW		20% ANPR / NPR VIEW
	50% RECOGNITION VIEW		10% DETECTION VIEW
	25% OBSERVATION VIEW		5% MONITORING VIEW

LEGEND		
SYMBOL	DESCRIPTION	TOTAL NO.
	SECURITY POLE	7
	FULL-FLAGGED EDGE-BUILT AI AND ANALYTICS ENABLED JUNCTION BOX FOR SECURITY (300mm x 150mm x 150mm)	6
	15U SECURITY RACK (WALL MOUNTED)	1

GENERAL NOTE:

For SPC approval, Security Integrator/ Contractor must adhere to the SIRA standard camera tagging, (e.g., **R0_CH_FLOOR LOCATION**)

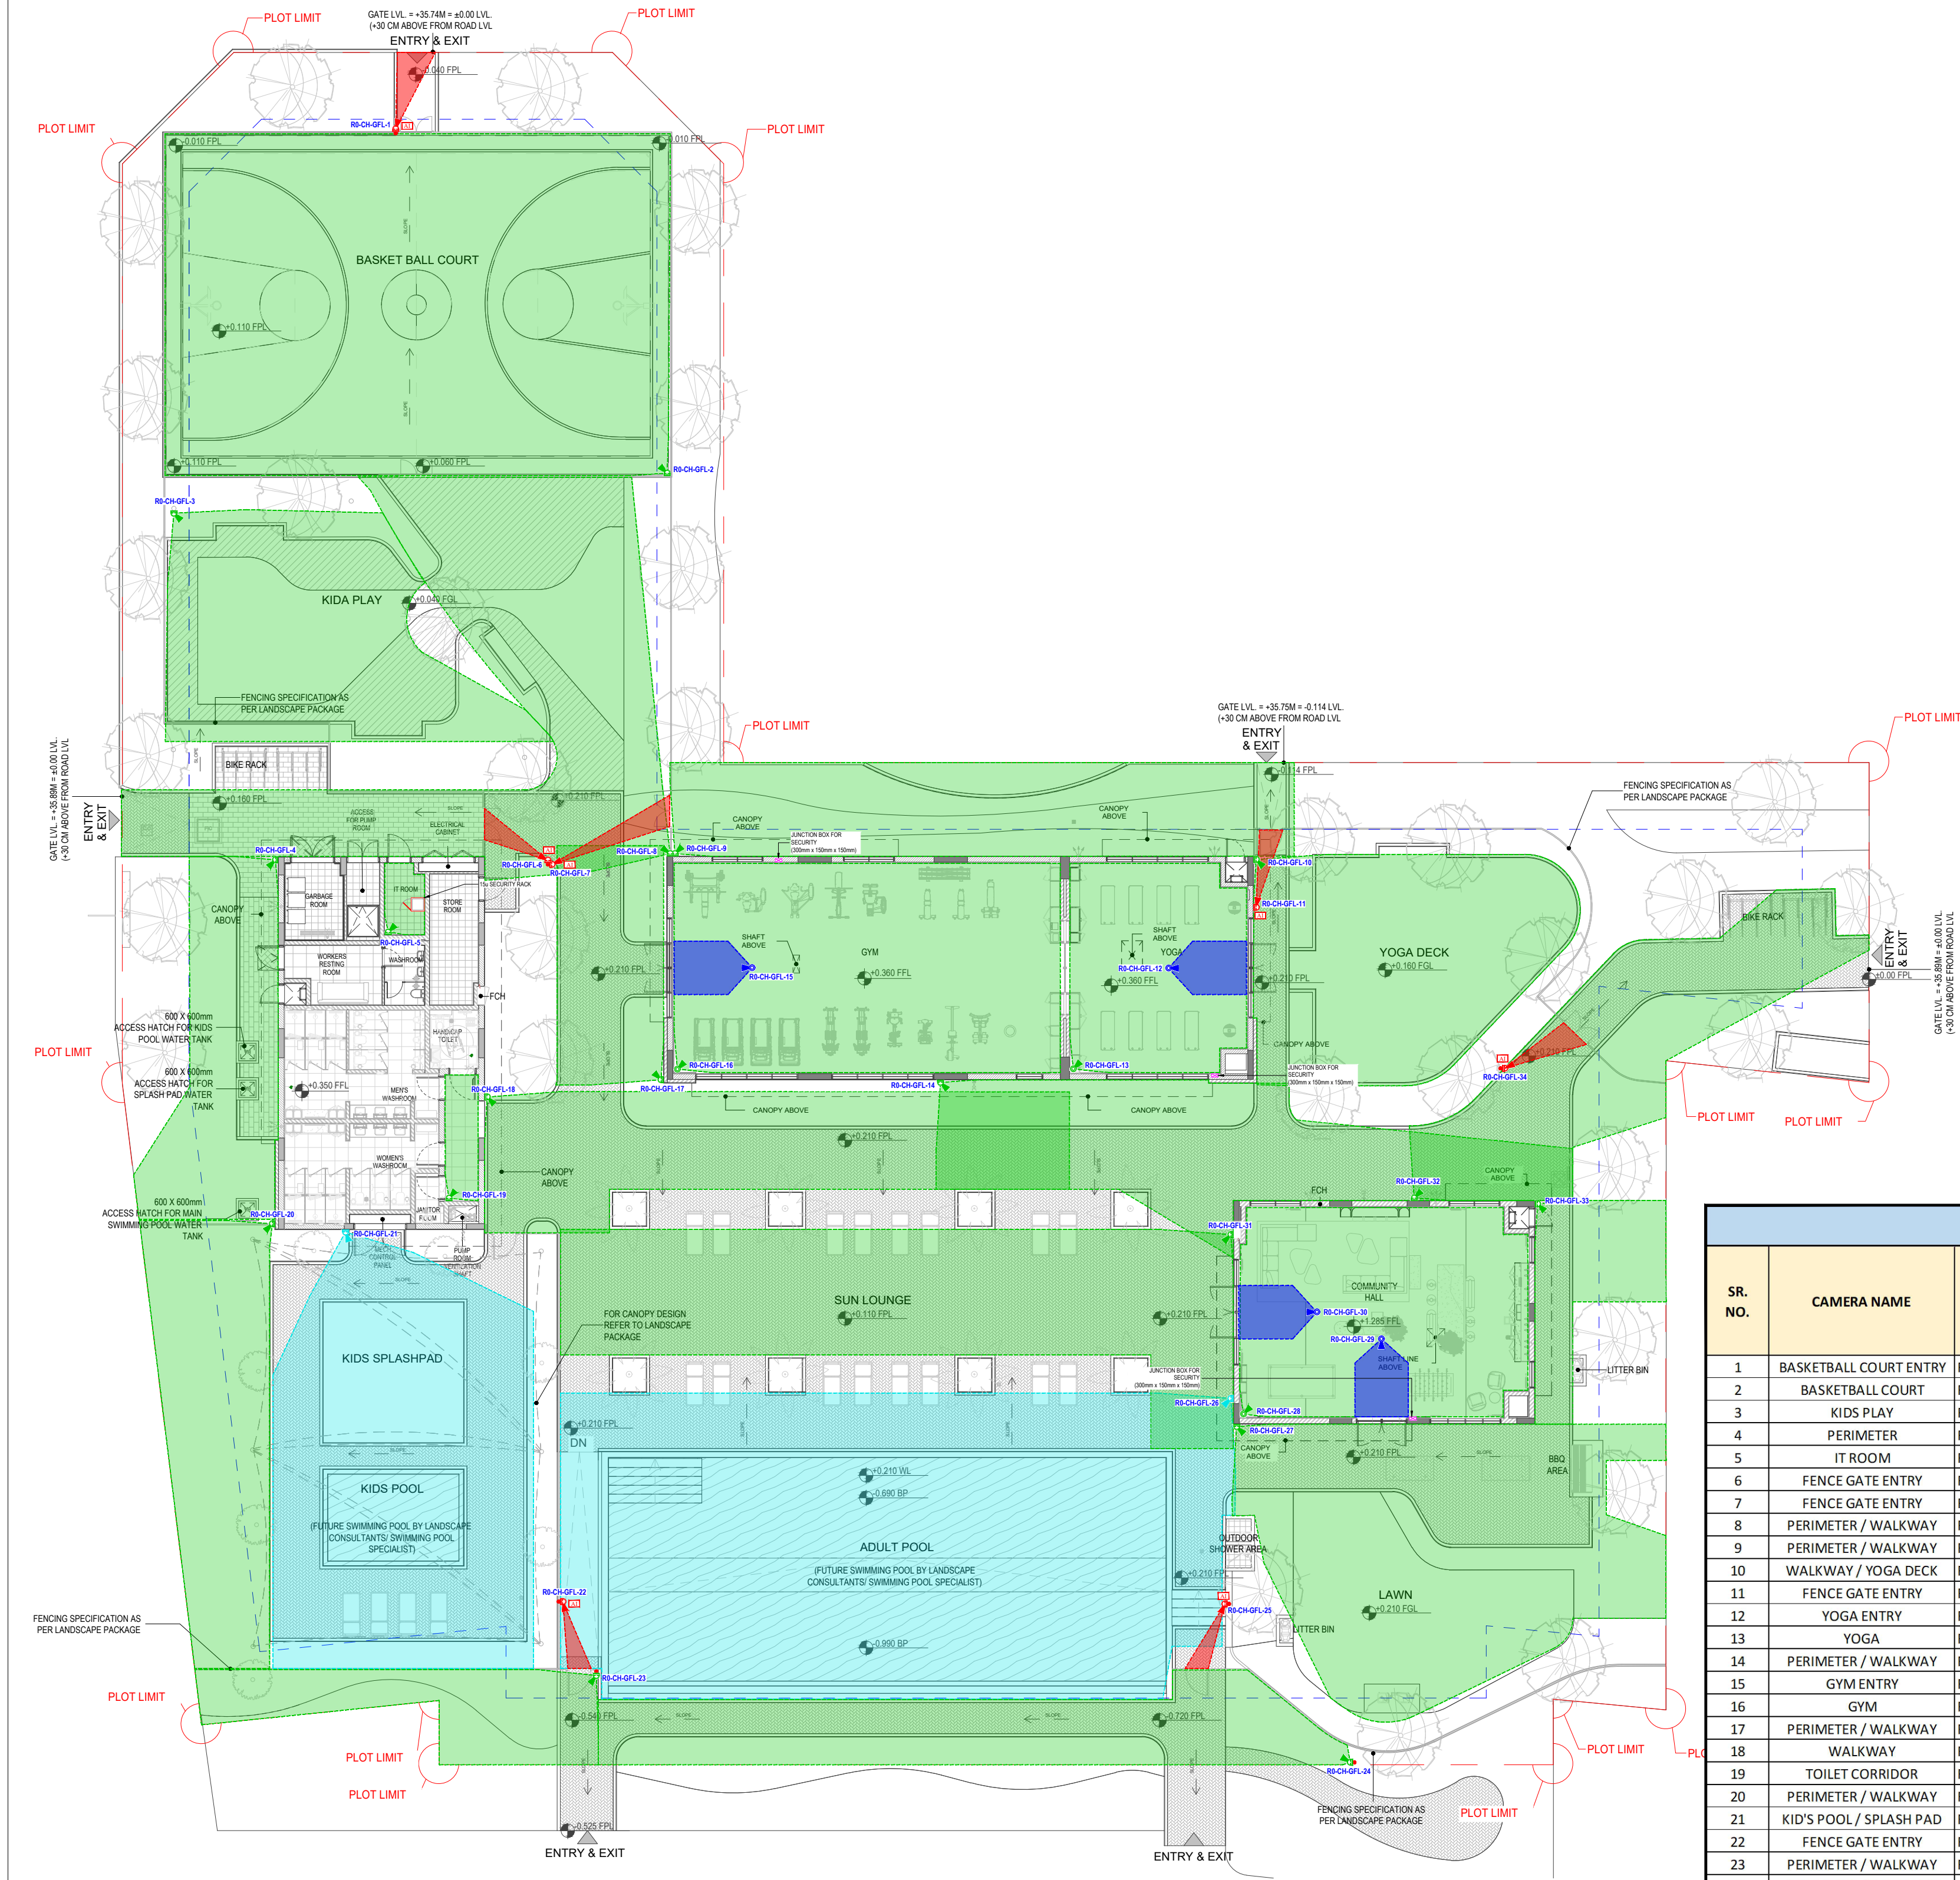

DETAILED SECURITY CAMERA SCHEDULE - COMMUNITY CENTER (TH-02)											
SR. NO.	CAMERA NAME	CAMERA TAG	CAMERA TYPE	CAMERA HEIGHT	CAMERA LENS	TILT ANGLE	FOV	VSS (CAMERA) CERTIFICATE NUMBER	ANPR CONNECTIVITY CERTIFICATE NUMBER (IF REQUIRED)	GLASS FILM CERTIFICATE NUMBER (IF REQUIRED)	PAD LOCK CERTIFICATE (IF REQUIRED)
1	BASKETBALL COURT ENTRY	R0-CH-GFL-1	WDR CAMERA	2600mm	5-50 MM	20°	120% IDENTIFICATION VIEW	XXX	XXX	XXX	XXX
2	BASKETBALL COURT	R0-CH-GFL-2	OUTDOOR CAMERA	3000mm	3-12 MM	75°	10% DETECTION VIEW	XXX	XXX	XXX	XXX
3	KIDS PLAY	R0-CH-GFL-3	OUTDOOR CAMERA	3000mm	3-12 MM	75°	10% DETECTION VIEW	XXX	XXX	XXX	XXX
4	PERIMETER	R0-CH-GFL-4	OUTDOOR CAMERA	3000mm	3-12 MM	75°	10% DETECTION VIEW	XXX	XXX	XXX	XXX
5	IT ROOM	R0-CH-GFL-5	INDOOR CAMERA	2600mm	3-12 MM	75°	10% DETECTION VIEW	XXX	XXX	XXX	XXX
6	FENCE GATE ENTRY	R0-CH-GFL-6	WDR CAMERA	3000mm	5-50 MM	20°	120% IDENTIFICATION VIEW	XXX	XXX	XXX	XXX
7	FENCE GATE ENTRY	R0-CH-GFL-7	WDR CAMERA	3000mm	5-50 MM	20°	120% IDENTIFICATION VIEW	XXX	XXX	XXX	XXX
8	PERIMETER / WALKWAY	R0-CH-GFL-8	OUTDOOR CAMERA	3000mm	3-12 MM	75°	10% DETECTION VIEW	XXX	XXX	XXX	XXX
9	PERIMETER / WALKWAY	R0-CH-GFL-9	OUTDOOR CAMERA	3000mm	3-12 MM	75°	10% DETECTION VIEW	XXX	XXX	XXX	XXX
10	WALKWAY / YOGA DECK	R0-CH-GFL-10	OUTDOOR CAMERA	3000mm	3-12 MM	75°	10% DETECTION VIEW	XXX	XXX	XXX	XXX
11	FENCE GATE ENTRY	R0-CH-GFL-11	WDR CAMERA	3000mm	5-50 MM	20°	120% IDENTIFICATION VIEW	XXX	XXX	XXX	XXX
12	YOGA ENTRY	R0-CH-GFL-12	INDOOR CAMERA	2600mm	3-12 MM	45°	50% RECOGNITION VIEW VIEW	XXX	XXX	XXX	XXX
13	YOGA	R0-CH-GFL-13	INDOOR CAMERA	2600mm	3-12 MM	75°	10% DETECTION VIEW	XXX	XXX	XXX	XXX
14	PERIMETER / WALKWAY	R0-CH-GFL-14	OUTDOOR CAMERA	3000mm	3-12 MM	75°	10% DETECTION VIEW	XXX	XXX	XXX	XXX
15	GYM ENTRY	R0-CH-GFL-15	INDOOR CAMERA	2600mm	3-12 MM	45°	50% RECOGNITION VIEW VIEW	XXX	XXX	XXX	XXX
16	GYM	R0-CH-GFL-16	INDOOR CAMERA	2600mm	3-12 MM	75°	10% DETECTION VIEW	XXX	XXX	XXX	XXX
17	PERIMETER / WALKWAY	R0-CH-GFL-17	OUTDOOR CAMERA	3000mm	3-12 MM	75°	10% DETECTION VIEW	XXX	XXX	XXX	XXX
18	WALKWAY	R0-CH-GFL-18	OUTDOOR CAMERA	3000mm	3-12 MM	75°	10% DETECTION VIEW	XXX	XXX	XXX	XXX
19	TOILET CORRIDOR	R0-CH-GFL-19	OUTDOOR CAMERA	2600mm	3-12 MM	75°	10% DETECTION VIEW	XXX	XXX	XXX	XXX
20	PERIMETER / WALKWAY	R0-CH-GFL-20	OUTDOOR CAMERA	3000mm	3-12 MM	75°	10% DETECTION VIEW	XXX	XXX	XXX	XXX
21	KID'S POOL / SPLASH PAD	R0-CH-GFL-21	OUTDOOR CAMERA	3000mm	3-12 MM	75°	5% MONITORING VIEW	XXX	XXX	XXX	XXX
22	FENCE GATE ENTRY	R0-CH-GFL-22	WDR CAMERA	3000mm	5-50 MM	20°	120% IDENTIFICATION VIEW	XXX	XXX	XXX	XXX
23	PERIMETER / WALKWAY	R0-CH-GFL-23	OUTDOOR CAMERA	3000mm	3-12 MM	75°	10% DETECTION VIEW	XXX	XXX	XXX	XXX
24	PERIMETER / WALKWAY	R0-CH-GFL-24	OUTDOOR CAMERA	3000mm	3-12 MM	75°	10% DETECTION VIEW	XXX	XXX	XXX	XXX
25	FENCE GATE ENTRY	R0-CH-GFL-25	WDR CAMERA	3000mm	5-50 MM	20°	120% IDENTIFICATION VIEW	XXX	XXX	XXX	XXX
26	ADULT'S POOL	R0-CH-GFL-26	OUTDOOR CAMERA	3000mm	3-12 MM	75°	5% MONITORING VIEW	XXX	XXX	XXX	XXX
27	LAWN / WALKWAY	R0-CH-GFL-27	OUTDOOR CAMERA	3000mm	3-12 MM	75°	10% DETECTION VIEW	XXX	XXX	XXX	XXX
28	COMMUNITY HALL	R0-CH-GFL-28	INDOOR CAMERA	2600mm	3-12 MM	75°	10% DETECTION VIEW	XXX	XXX	XXX	XXX
29	COMMUNITY HALL ENTRY	R0-CH-GFL-29	INDOOR CAMERA	2600mm	3-12 MM	45°	50% RECOGNITION VIEW VIEW	XXX	XXX	XXX	XXX
30	COMMUNITY HALL ENTRY	R0-CH-GFL-30	INDOOR CAMERA	2600mm	3-12 MM	45°	50% RECOGNITION VIEW VIEW	XXX	XXX	XXX	XXX
31	SUN LOUNGE / WALKWAY	R0-CH-GFL-31	OUTDOOR CAMERA	3000mm	3-12 MM	75°	10% DETECTION VIEW	XXX	XXX	XXX	XXX
32	PERIMETER / WALKWAY	R0-CH-GFL-32	OUTDOOR CAMERA	3000mm	3-12 MM	75°	10% DETECTION VIEW	XXX	XXX	XXX	XXX
33	PERIMETER / WALKWAY	R0-CH-GFL-33	OUTDOOR CAMERA	3000mm	3-12 MM	75°	10% DETECTION VIEW	XXX	XXX	XXX	XXX
34	FENCE GATE ENTRY	R0-CH-GFL-34	WDR CAMERA	3000mm	5-50 MM	20°	120% IDENTIFICATION VIEW	XXX	XXX	XXX	XXX

SECURITY		
Drawing title:		
OVERALL GROUND FLOOR PLAN CCTV SYSTEM LAYOUT COMMUNITY CENTER - TH-02		
Architectural Engineer	Electrical Engineer	Structural Engineer
MUSTAFA ABID	MARWAN MOHD.	RIHAM RAMADAN
Registration # 5847	Registration # 80102	Registration # 105992
Scale(s):	Date drawn:	Project no:
1 : 200	10/03/2026	1857
Drawn by:	Checked:	Approved:
JP	MM	JR
Drawing Number: GPCR-TH02-IES-PL-CC2-SEC-VSS-0001-00		