



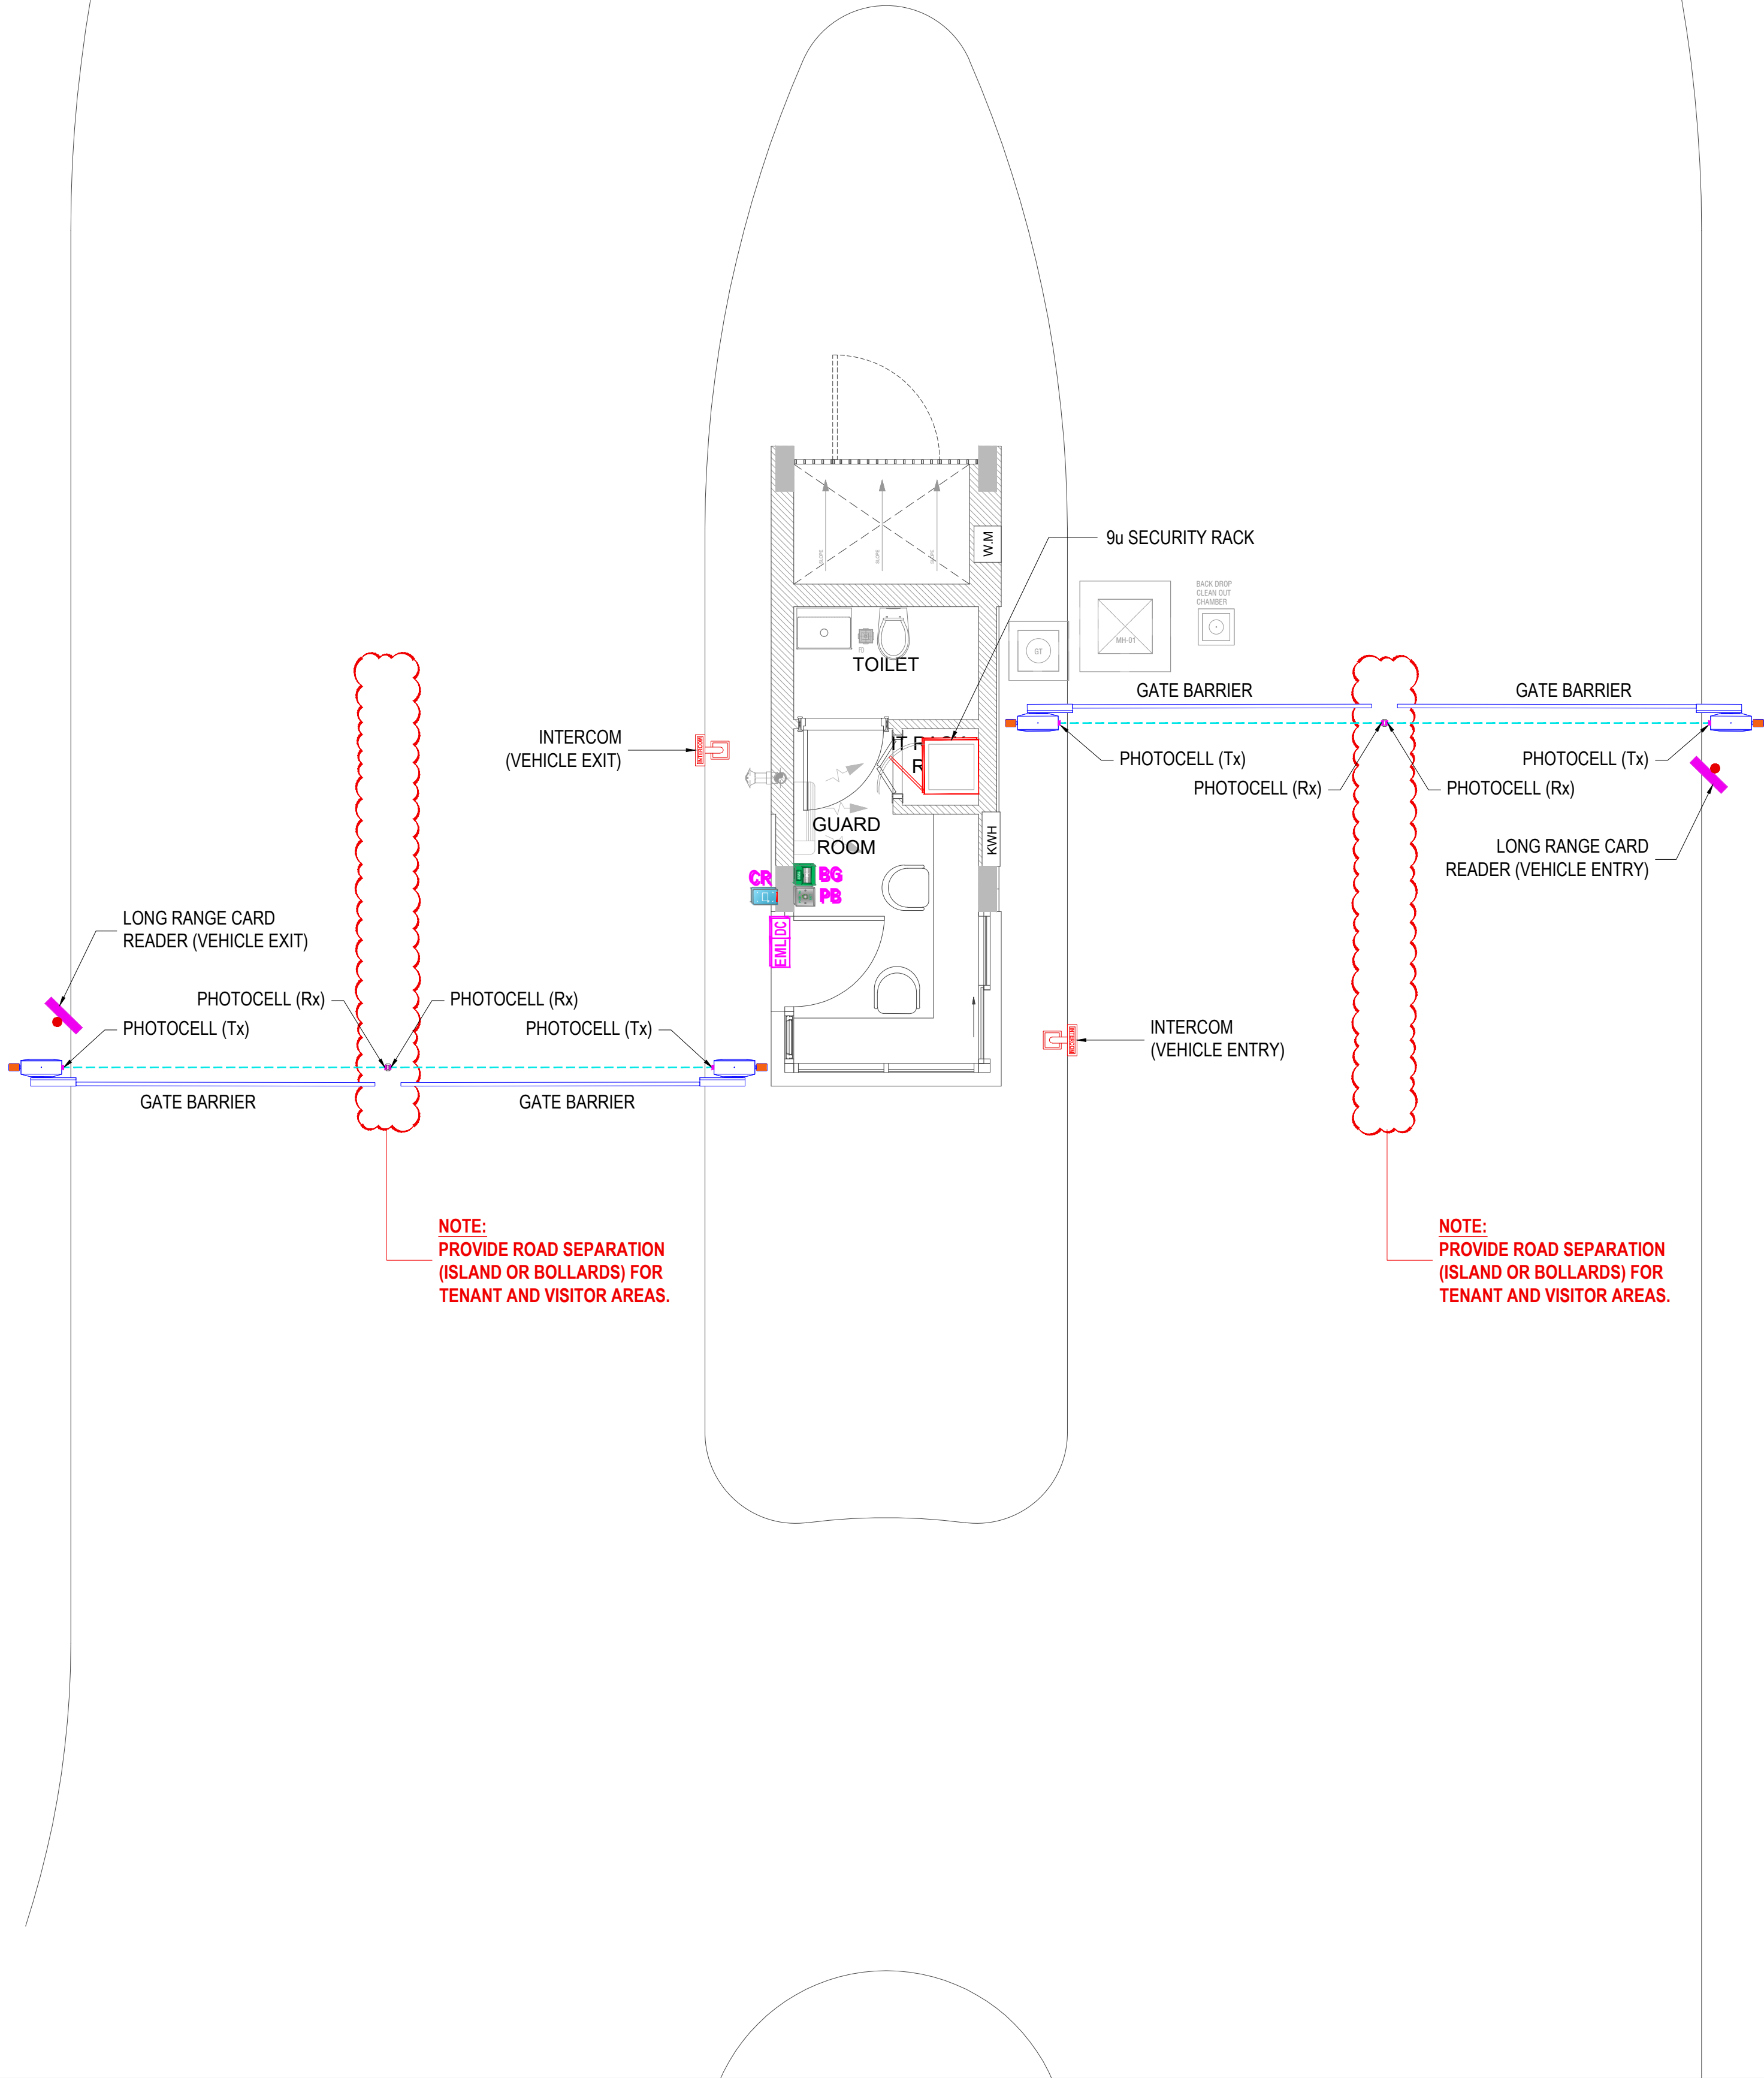

- IES NOTE: CCTV + INTRUSION + ACCESS CONTROL**
1. THE LOCATIONS OF CCTV, ALARM, AND ACS COMPONENTS ARE INDICATED APPROXIMATELY ON THE DRAWINGS AND ARE SUBJECT TO ON-SITE VERIFICATION.
 2. EXACT LOCATIONS AND HEIGHTS OF COMPONENTS WILL BE FINALIZED IN COORDINATION WITH THE CONTRACTOR ON-SITE, CONSIDERING BUILDING LAYOUT, INTERIOR DESIGN, DECORATION, AND ANY OTHER RELEVANT SERVICES OR COMPONENTS.
 3. ON-SITE, COORDINATION WITH THE CONTRACTOR IS ESSENTIAL TO ADDRESS ANY POTENTIAL OBSTRUCTIONS TO THE CAMERA'S FIELD OF VIEW, IN COMPLIANCE WITH DUBAI LAW 12/2016, AS WELL AS TO MITIGATE ELECTROMAGNETIC INTERFERENCE (EMI) IMPACTING ELECTRONIC SECURITY COMPONENTS.
 4. THIS DESIGN WILL BECOME INVALID IF THERE ARE ANY MODIFICATIONS TO THE ARCHITECTURAL PLANS OR CHANGES IN LEGAL REQUIREMENTS.
 5. LOW-LIGHT AREAS SHOULD BE EQUIPPED WITH INFRARED (IR) OR NIGHT VISION CAMERAS TO ENSURE PROPER COVERAGE AND VISIBILITY.

ACCESS CONTROL SYSTEM SCHEDULE		
SYMBOL	DESCRIPTION	TOTAL NO. OF ACS
	CARD READER	1
	BREAK GLASS	1
	PUSH BUTTON	1
	DOOR CONTACT	1
	ELECTRO MAGNETIC LOCK	1
	LONG RANGE CARD READER	2
	INTERCOM	2
	GATE BARRIER	4

LEGEND		
SYMBOL	DESCRIPTION	TOTAL NO.
	9U SECURITY RACK (WALL MOUNTED)	1

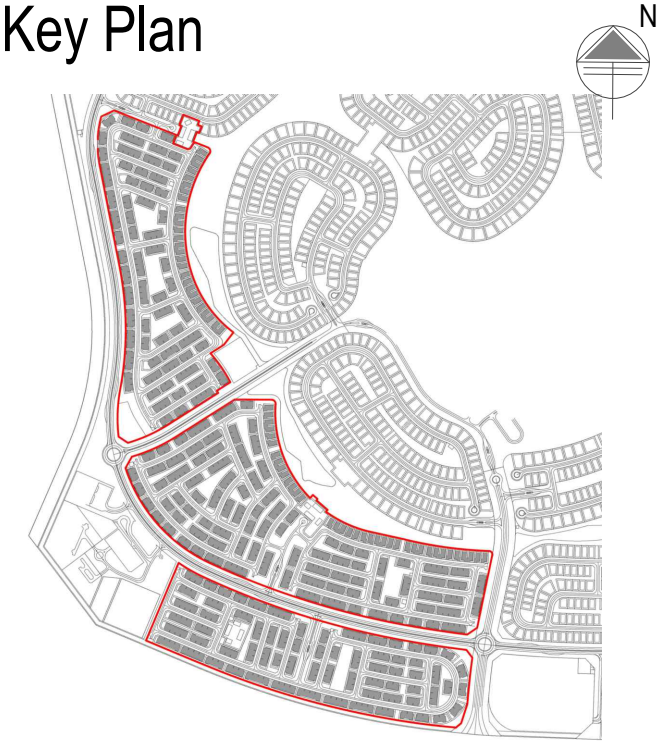

- General Notes :**
01. Do not Scale The Drawings. Follow (The MM) Written Dimensions Unless Otherwise Mentioned.
 02. Each Drawing Shall be Read in Conjunction With all Other Drawings, Specification & the General Standard Details. In Case of Any Discrepancies Bring it to the Knowledge of Engineer and Same to be Resolved Prior to Execution of Work.
 03. Dimensions Shown on These Drawings are Structural Dimensions. Unless Noted Otherwise.
 04. All Levels Indicated On These Drawings are Levels as per the Survey Datum, Same Should be Verified at Site Prior to Execution of Work.
 05. All Levels Indicated On These Drawings are Based On Design Level, Which is Equivalent to Datum Level and Same Should be Verified at Site Prior to Execution of Work.

TENDER DRAWINGS

0010/03/2026JP

TENDER SUBMISSION

No.	Date	Initials	Description
REVISIONS / ISSUE			

THIS DRAWING MUST NOT BE REPRODUCED IN WHOLE OR IN PART WITHOUT THE PRIOR APPROVAL OF ARIF & BINTOK

Status

TENDER SUBMISSION

Client

EMAAR

Lead Consultant

عارف وبن طوق
Arif & Bintok
consulting architects & engineers

POST BOX 3670 DUBAI, U.A.E. TEL: 04-3972888 FAX: 04-3979332
POST BOX 42981 ABU DHABI, U.A.E. TEL: 02-454669 arifbintok@emirates.net.ae

Security Consultant

INTERNATIONAL ELECTRONIC SECURITY
TEL: 04 397 0757, FAX: 04 397 0754
P.O. BOX 12734 DUBAI - U.A.E
ENQUIRIES@IESCONSULTING.AE
AUDIT@IESCONSULTING.AE
WWW.IESCONSULTING.AE

Project Title:

Proposed Residential Townhouses and Standalone Villas TH-1, TH-2, and TH-3 at Grand Polo Club & Resort, Dubai, UAE

Discipline : SECURITY		
Drawing title:		
GUARD HOUSE (TH-02) ACS SYSTEM LAYOUT GUARD HOUSE - TH-02		
Architectural Engineer	Electrical Engineer	Structural Engineer
MUSTAFA ABID	MARWAN MOHD.	RIHAM RAMADAN
Registration # 5847	Registration # 80102	Registration # 105082
Scale(s):	Date drawn:	Project no:
1 : 50	10/03/2026	1857
Drawn by:	Checked :	Approved :
JP	MM	JR
Drawing Number :		GPCR-TH02-IES-PL-GH2-SEC-ACS-0001-00