




This 2D drawing is extracted from 3D BIM Model

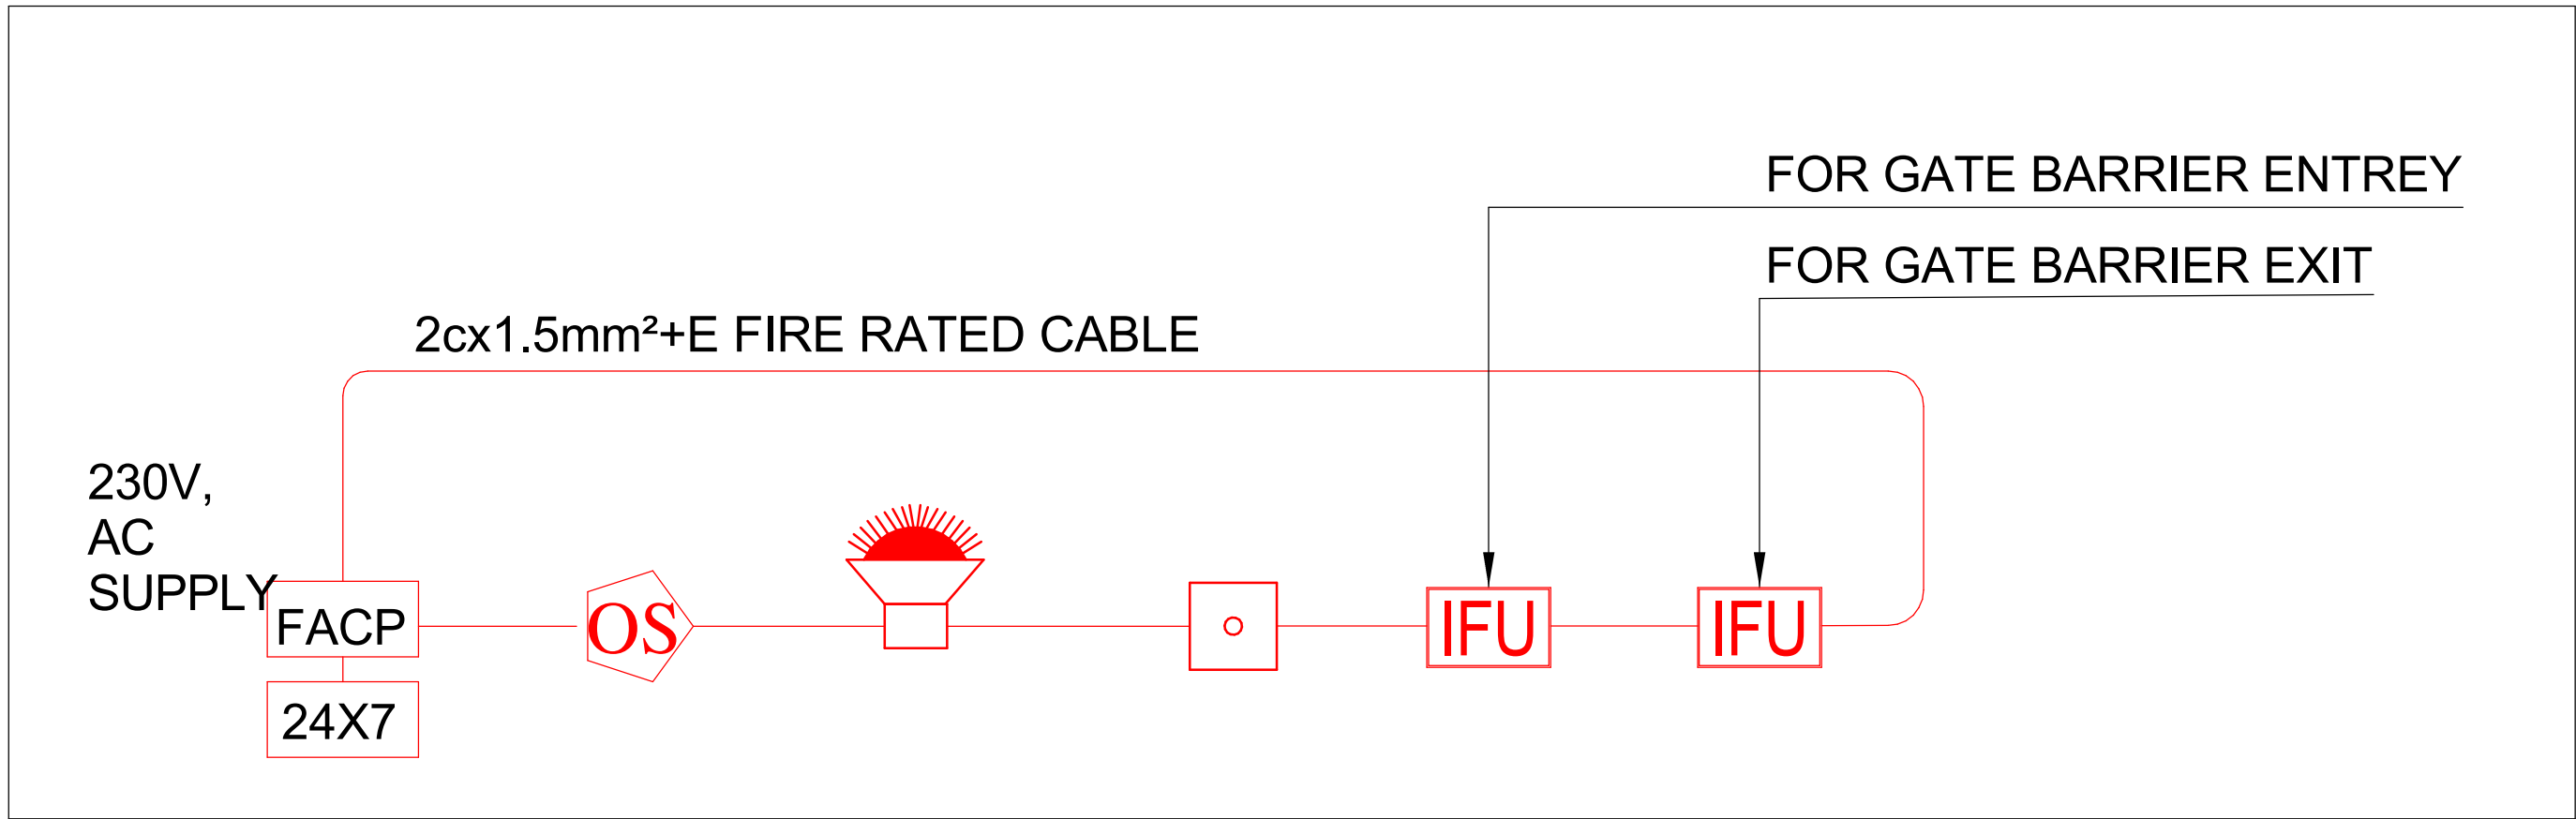

LIFE SAFETY	
FIRE DETECTION & ALARM SYSTEM & EMERGENCY LIGHTING	
SYMBOL	DESCRIPTION
	INTELLIGENT OPTICAL SMOKE DETECTOR WITH BUILT IN ISOLATOR
	MANUAL CALL POINT BUILT IN ISOLATOR
	FIRE ALARM SOUNDER OR HORN WITH FLASHER-W/P
	INTERFACE UNIT WITH DUAL INPUT/OUTPUT CONTROL & MONITOR MODULE
	24x7 PANEL
	INTERFACE UNIT WITH DUAL INPUT/OUTPUT CONTROL & MONITOR MODULE
	ADDRESSABLE EMERGENCY LIGHT, NON-MAINTAINED, COMPACT TYPE, SQUARE (OR) CIRCULAR IN SHAPE SURFACE (OR) SEMI-RECESSED MOUNTED, IP55
	ADDRESSABLE COMPACT & DECORATIVE EDGE LIGHT EXIT LIGHT, MAINTAINED, HANGING (OR) RECESS MOUNTED TYPE, WITH (SINGLE SIDED) GLASS FINISH LEGEND LASER PRINTED. IP20

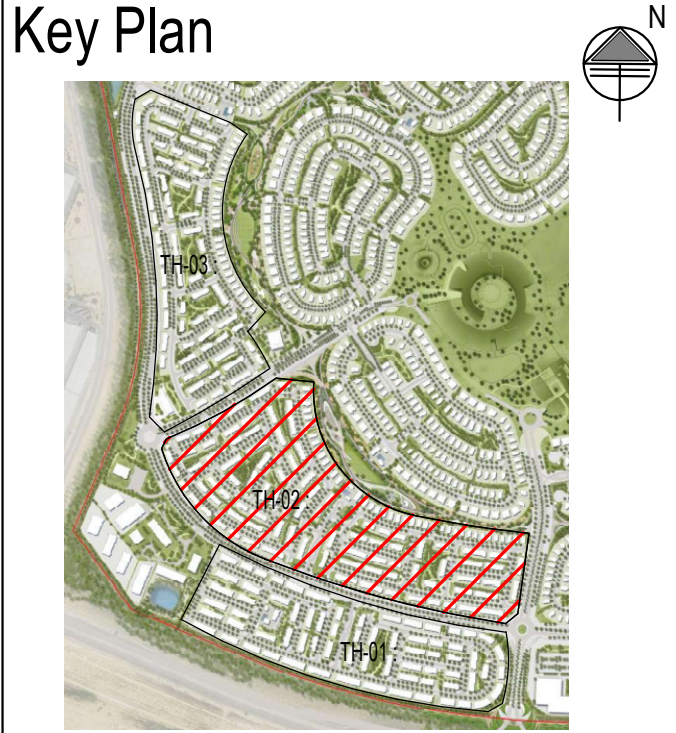

- General Notes :**
01. Do not Scale The Drawings. Follow (The MM) Written Dimensions Unless Otherwise Mentioned.
 02. Each Drawing Shall be Read in Conjunction With all Other Drawings, Specification & the General Standard Details. In Case of Any Discrepancies Bring it to the Knowledge of Engineer and Same to be Resolved Prior to Execution of Work.
 03. Dimensions Shown on These Drawings are Structural Dimensions Unless Noted Otherwise.
 04. All Levels Indicated On These Drawings are Levels as per the Survey Datum, Same Should be Verified at Site Prior to Execution of Work.
 05. All Levels Indicated On These Drawings are Based On Design Level, Which is Equivalent to Datum Level and Same Should be Verified at Site Prior to Execution of Work.

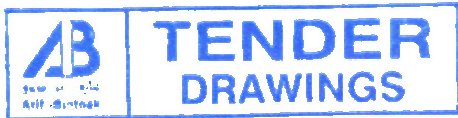

00	10/03/2026	SPG	TENDER SUBMISSION
No.	Date	Initials	Description
REVISIONS / ISSUE			
THIS DRAWING MUST NOT BE REPRODUCED IN WHOLE OR IN PART WITHOUT THE PRIOR APPROVAL OF ARIF & BINTOAK			
Status			
TENDER SUBMISSION			
Client			
EMAAR			
Lead Consultant			
 المستشارين: عارف وبن طوق Arif & BintOak consulting architects & engineers PHOT BOOX 30101 MIDRAH LANE TEL: 02-6228888 FAX: 02-6228888 POST BOX 42081 ABU DHABI UAE TEL: 02-624666 - bntoak@arifbintoak.ae			
Project Title:			
GUARD HOUSE GRANDPOLO CLUB & RESORT, UAE			
Discipline :			
ELECTRICAL			
Drawing title:			
GUARD HOUSE FIRE ALARM SCHEMATIC DIAGRAM			
Architectural Engineer	Electrical Engineer	Structural Engineer	
MUSTAFA ABID	MARWAN MOHD.	RIHAM RAMADAN	
Registration # 5847	Registration # 80102	Registration # 105092	
Scale(s):	Date drawn:	Project no:	
As indicated	10/03/2026	1857	
Drawn by:	Checked :	Approved :	
VPA	HAE	MRM	
Drawing Number :		GPCR-TH02-AB-DRG-ZZZ-ELE-FA-4006-00	