



This 2D drawing is extracted from 3D BIM Model

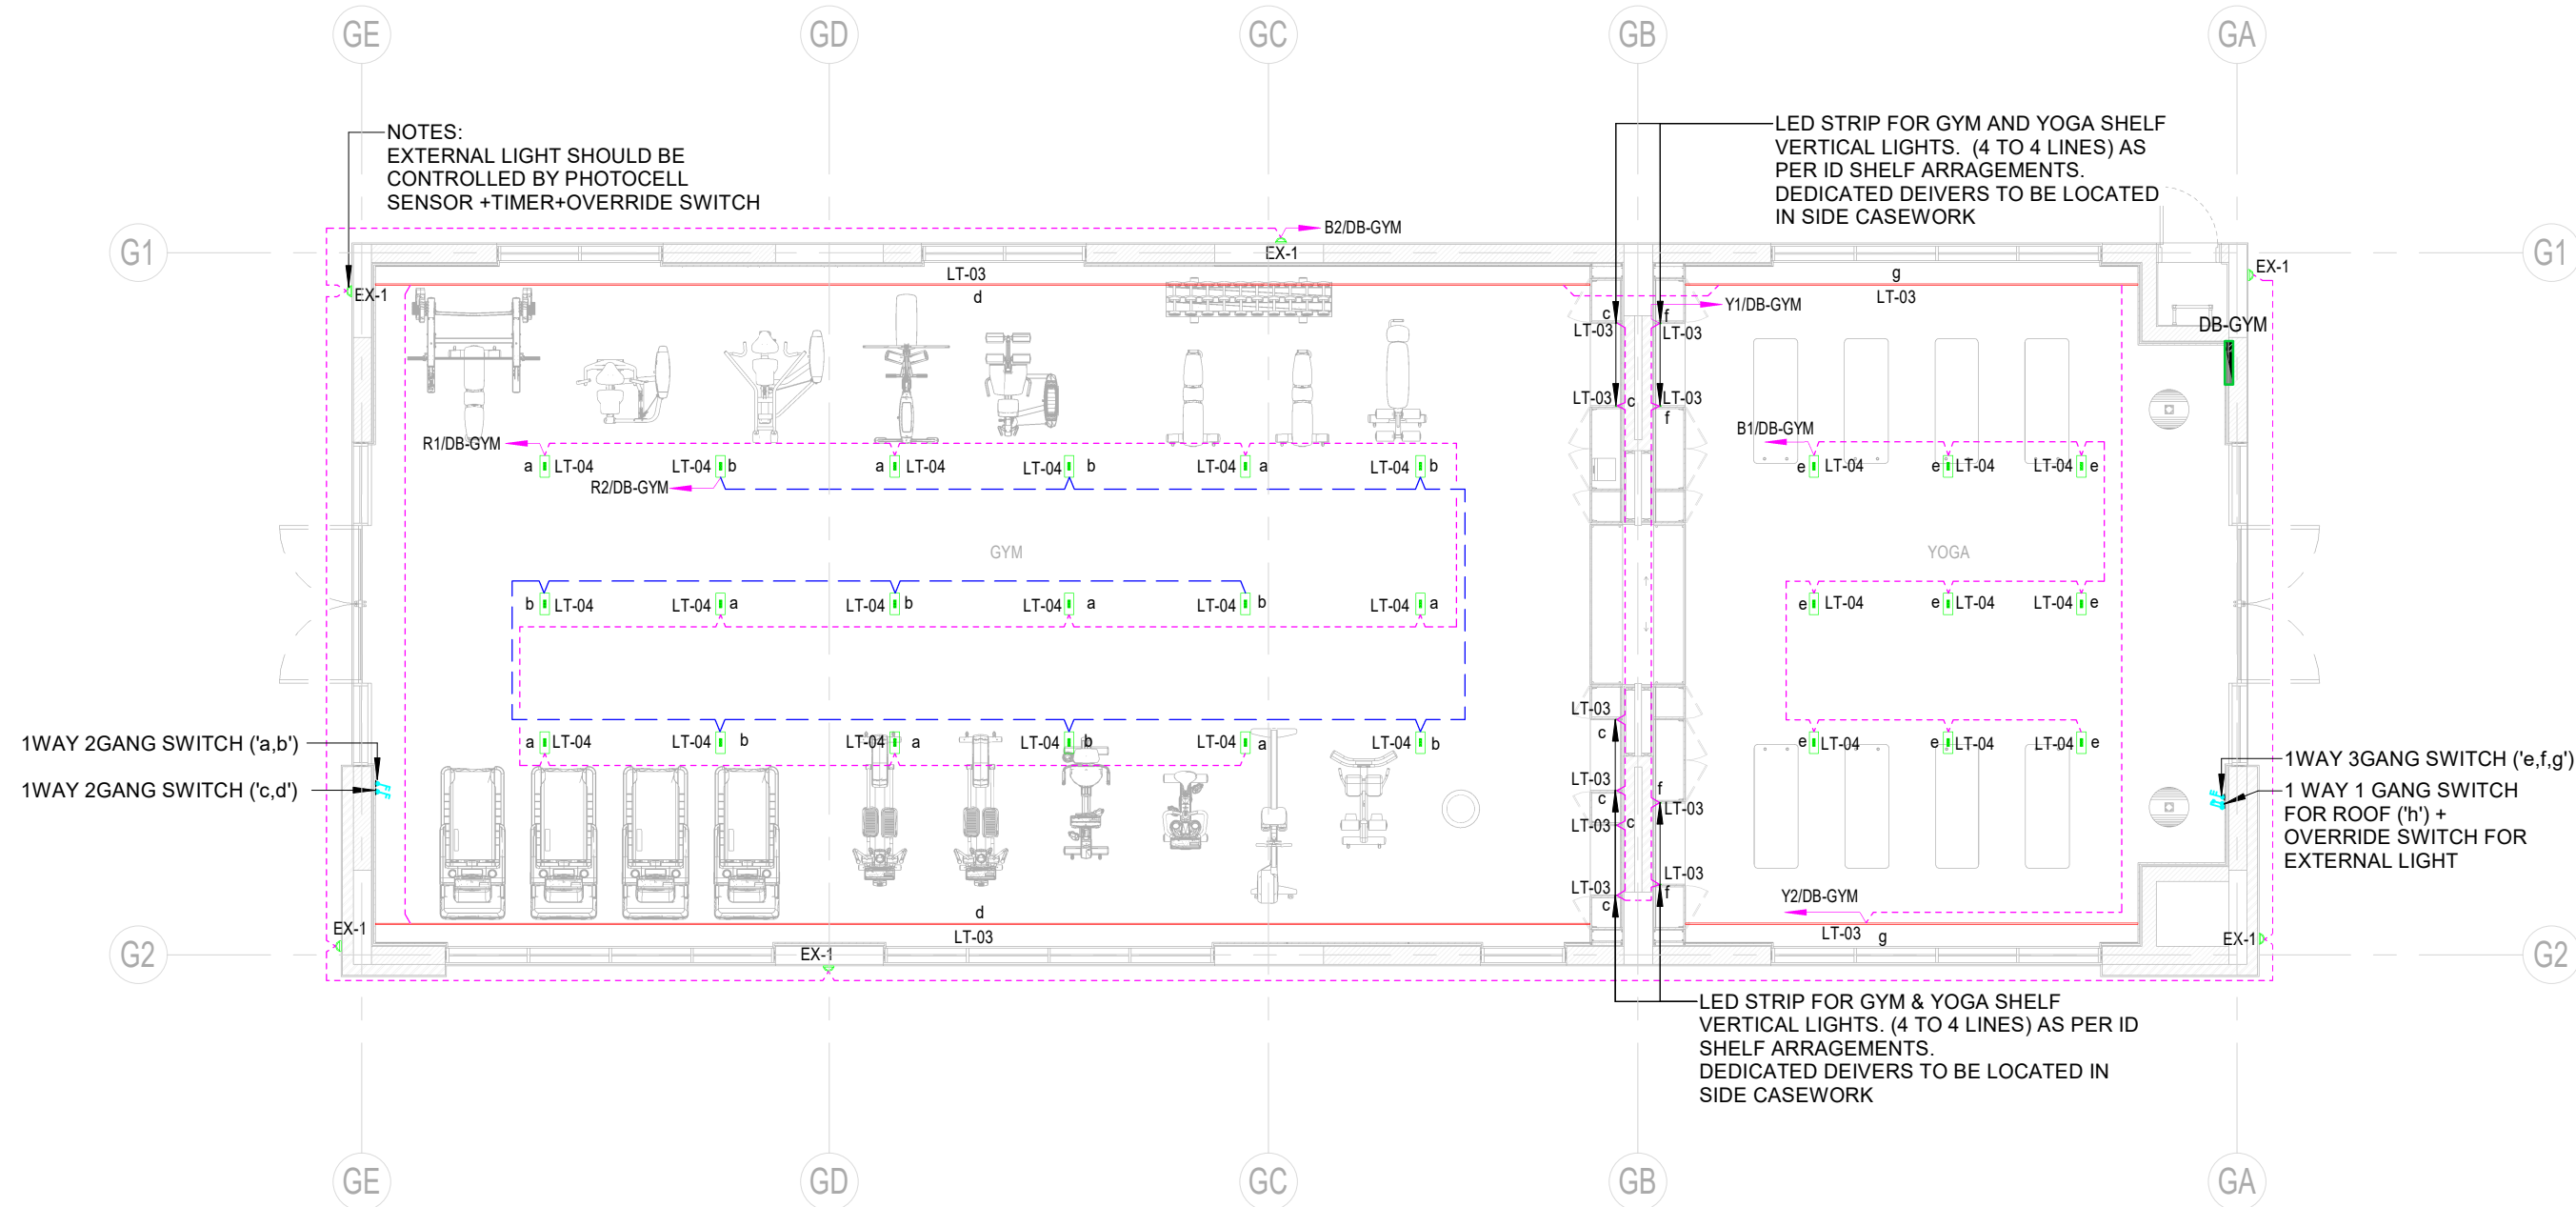

1 01-GROUND FLOOR GYM LIGHTING
1 : 100

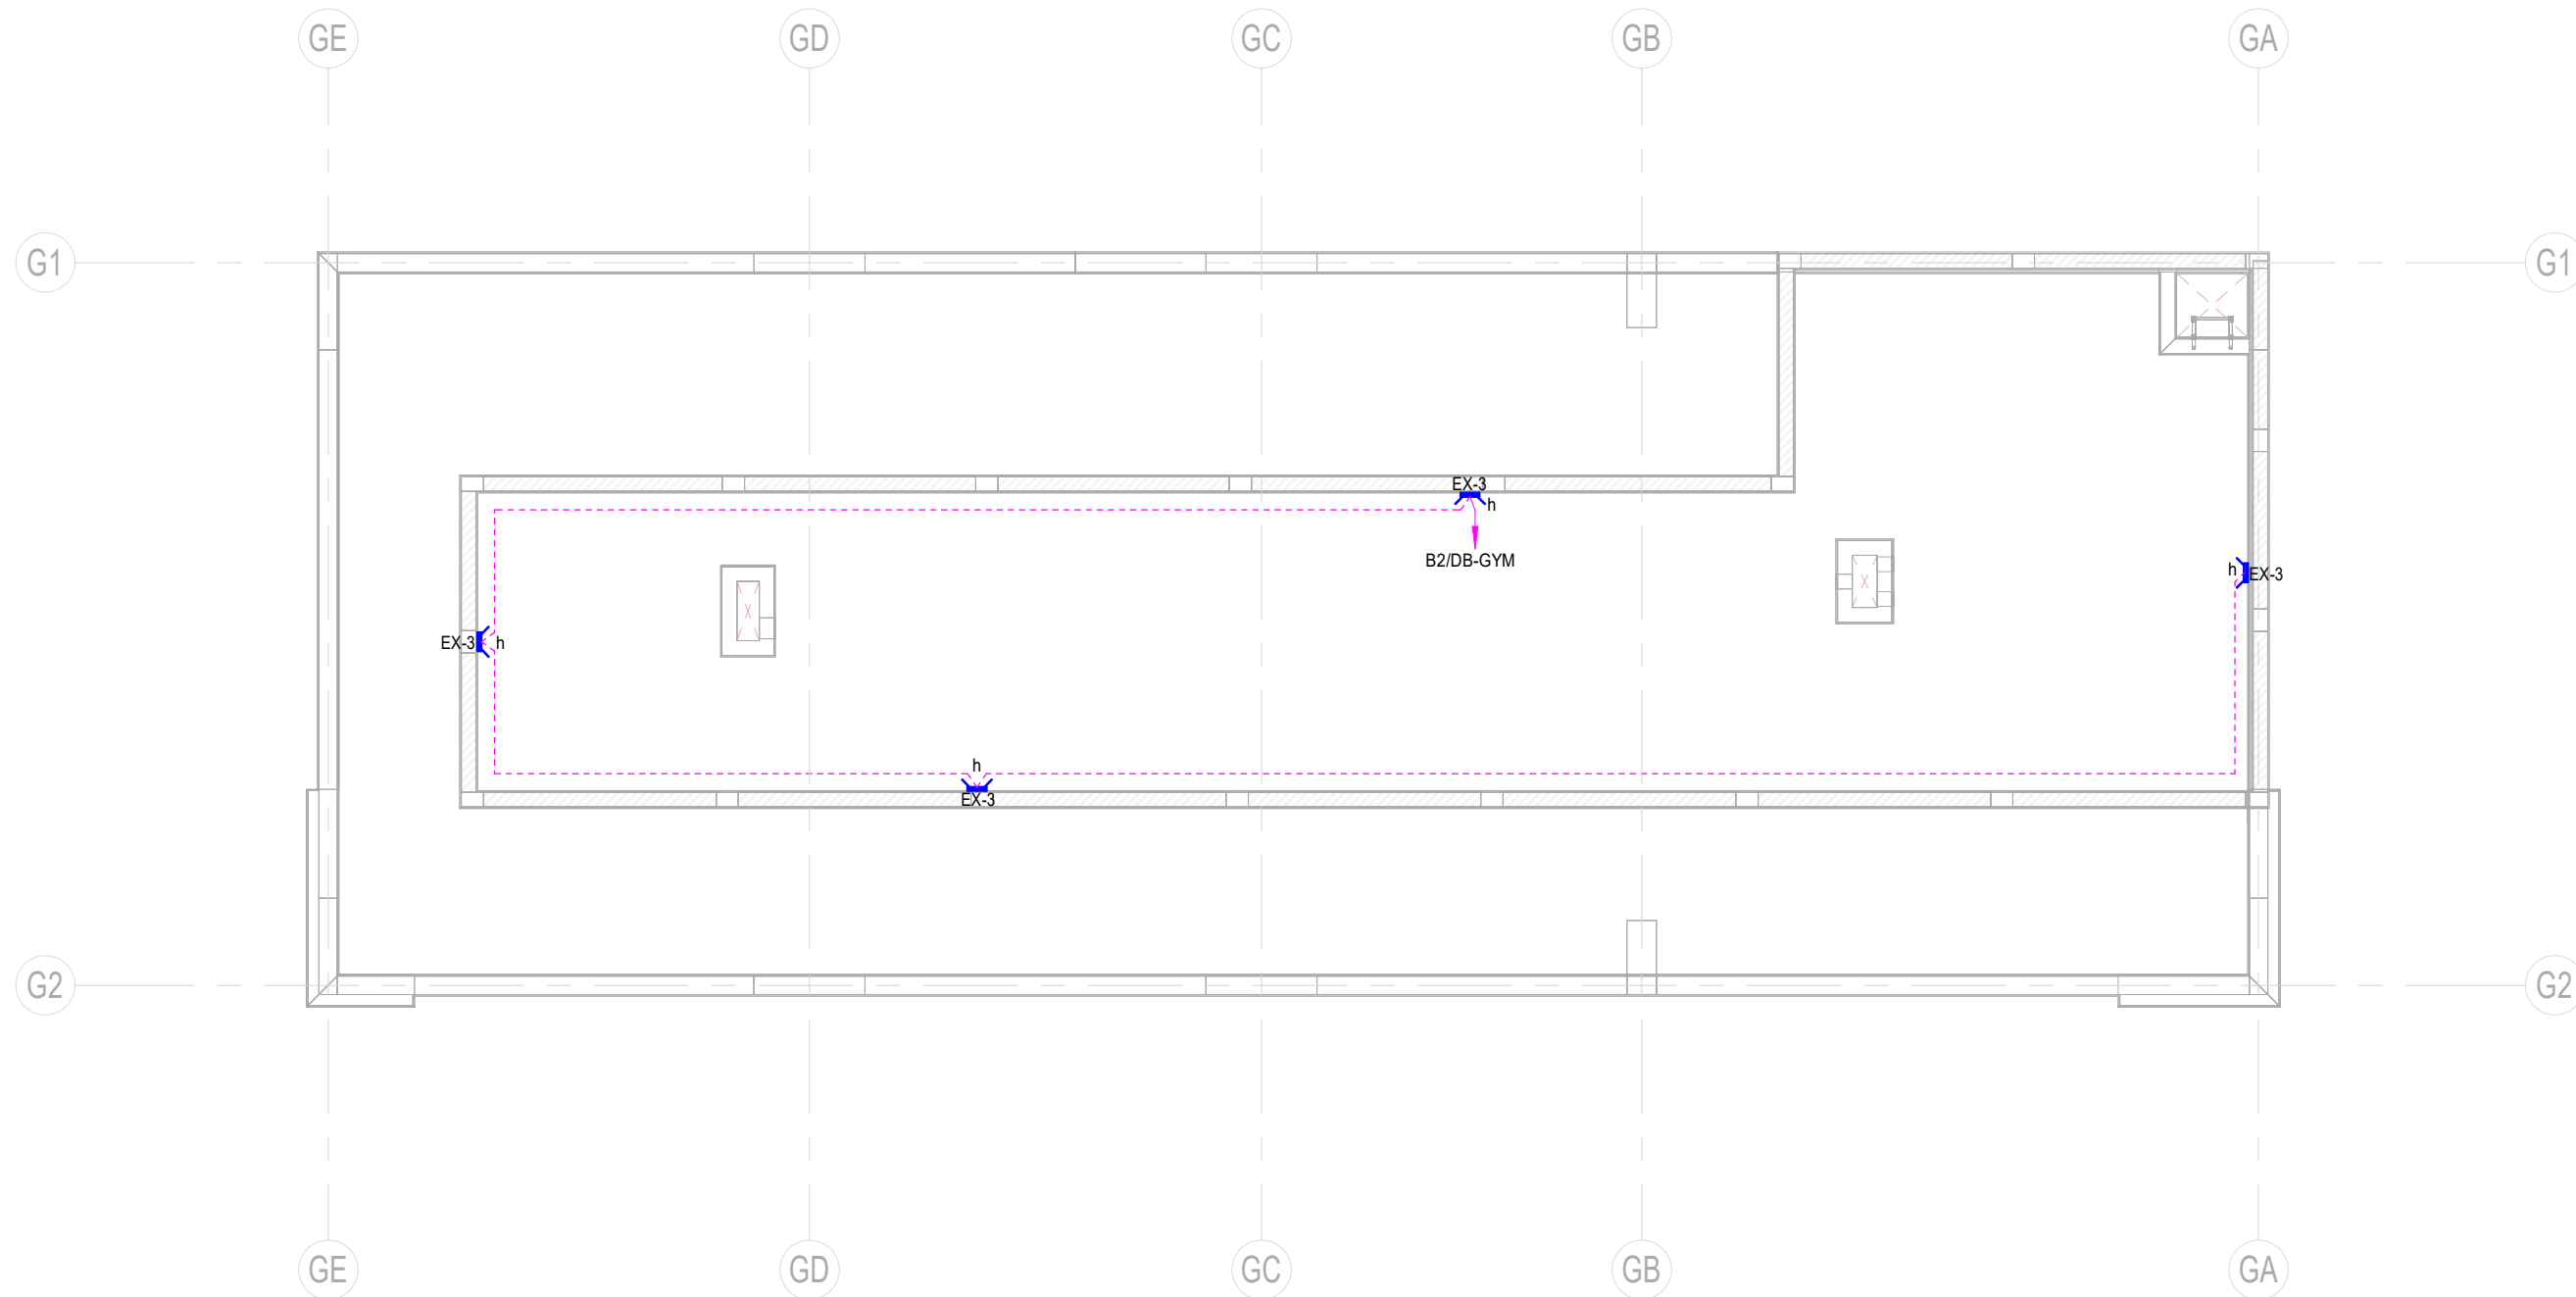

2 03-ROOF GYM LIGHTING
1 : 100

LIGHTING LEGENDS	
SYMBOL	DESCRIPTION
LT-03	10W LED STRIP LINEAR LIGHT
LT-04	12W BALADE LIGHT , IP20
EX-1	15W LED, WALL MOUNTED EXTERNAL DECORATIVE LIGHTS 3000°K (2x7W)
EX-3	15W LED, WALL MOUNTED LIGHT DIE CAST ALUMINUM
	13Amp - 1 WAY 1 GANG SWITCH.
	13Amp - 1 WAY 3 GANG SWITCH.
	13Amp - OVERRIDE SWITCH.
	13Amp - 1 WAY 1 GANG SWITCH + OVERRIDE SWITCH
DB-X-X	ELECTRICAL FINAL DISTRIBUTION BOARD (DB) X INDICATING FLOOR REF, Y INDICATING FLAT REF.

NOTE:
EXTERNAL LIGHT SHOULD BE CONTROLLED BY
PHOTOCELL SENSOR + TIMER + OVERRIDE SWITCH



- General Notes :**
- Do not Scale The Drawings. Follow (The MM) Written Dimensions Unless Otherwise Mentioned.
 - Each Drawing Shall be Read in Conjunction With all Other Drawings, Specification & the General Standard Details. In Case of Any Discrepancies Bring it to the Knowledge of Engineer and Same to be Resolved Prior to Execution of Work.
 - Dimensions Shown on These Drawings are Structural Dimensions Unless Noted Otherwise.
 - All Levels Indicated On These Drawings are Levels as per the Survey Datum, Same Should be Verified at Site Prior to Execution of Work.
 - All Levels Indicated On These Drawings are Based On Design Level, Which is Equivalent to Datum Level and Same Should be Verified at Site Prior to Execution of Work.



00	10/03/2026	VPA	TENDER SUBMISSION
No.	Date	Initials	Description
REVISIONS / ISSUE			
THIS DRAWING MUST NOT BE REPRODUCED IN WHOLE OR IN PART WITHOUT THE PRIOR APPROVAL OF ARIF & BINTOAK			
Status	TENDER SUBMISSION		
Client	EMAAR		
Lead Consultant	 اريف وبن طوق Arif & BintOak consulting architects & engineers P.O. BOX 4281 ABU DHABI, U.A.E. TEL: 02-4522888 FAX: 02-4522852 P.O. BOX 4281 ABU DHABI, U.A.E. TEL: 02-4524668 arifbint@arifbint.com.ae		
Project Title:	COMMUNITY CENTER - TH02 GRANDPOLP CLUB & RESORT, UAE		
Discipline :	ELECTRICAL		
Drawing title:	GYM GROUND & ROOF FLOOR PLAN LIGHTING LAYOUT		
Architectural Engineer	Electrical Engineer	Structural Engineer	
MUSTAFA ABID	MARWAN MOHD.	RIHAM RAMADAN	
Registration # 5847	Registration # 80102	Registration # 105092	
Scale(s): 1 : 100	Date drawn: 10/03/2026	Project no: 1857	
Drawn by: VPA	Checked: HAE	Approved: MRM	
Drawing Number:	GPCR-TH02-AB-DRG-ZZZ-ELE-EL-3002-00		