



This 2D drawing is extracted from 3D BIM Model

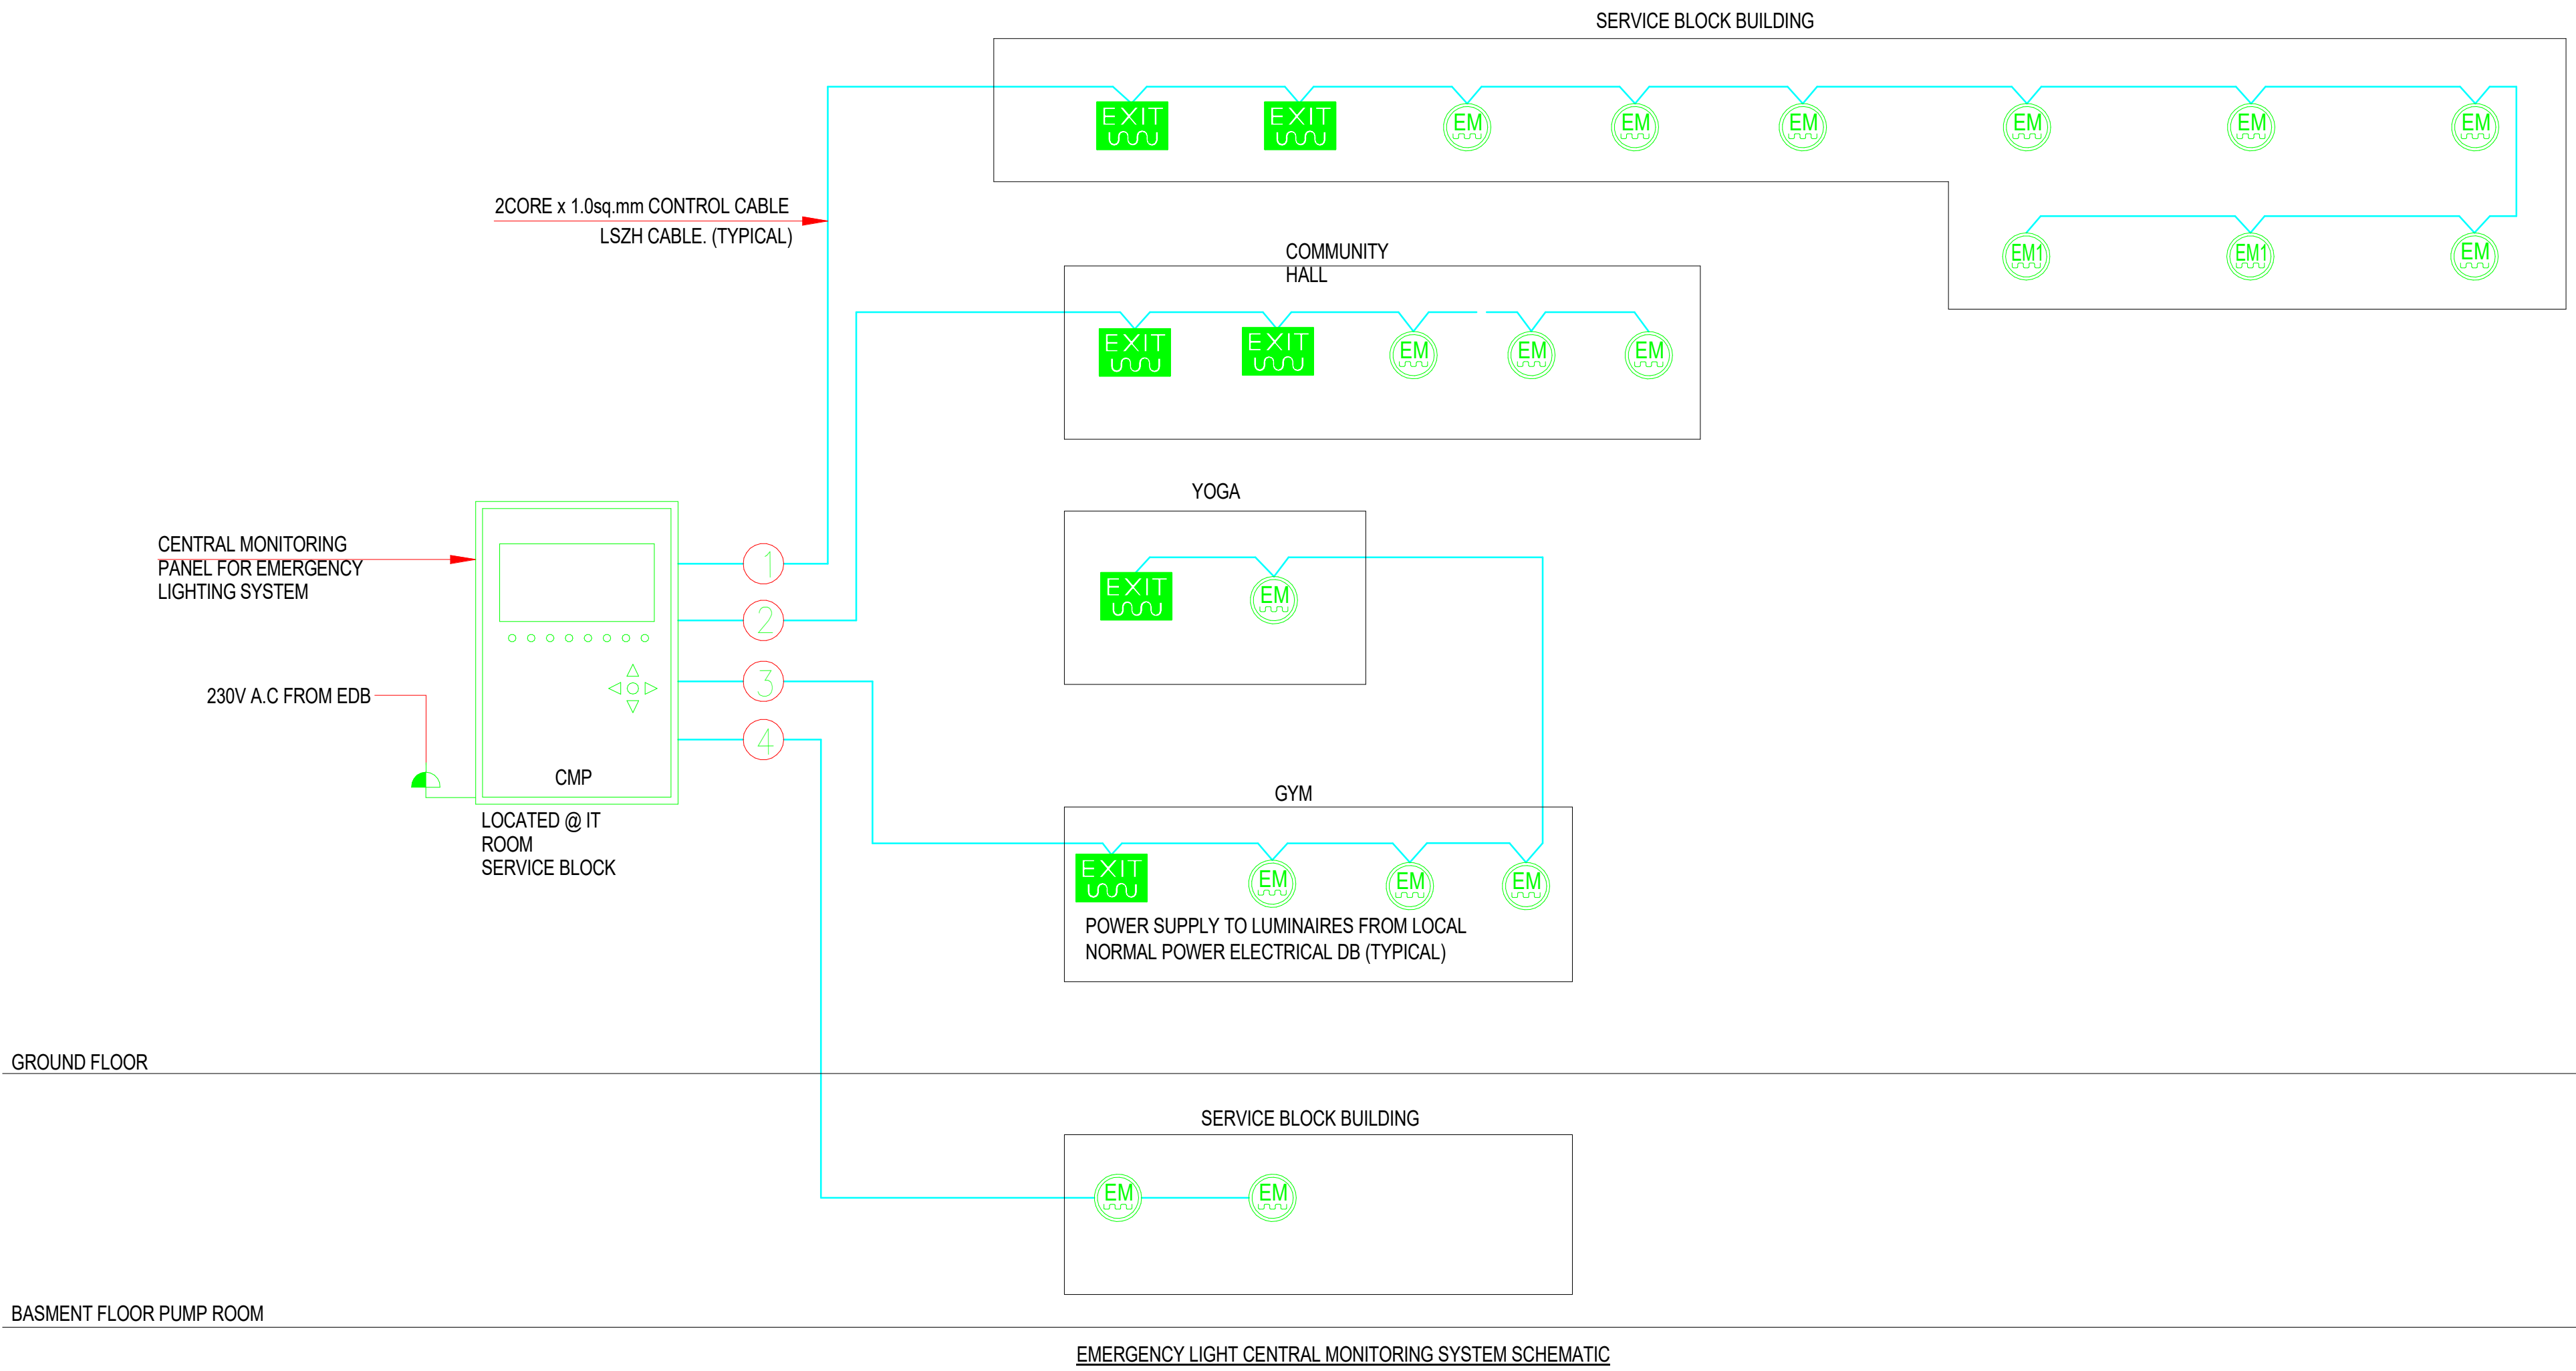


EMERGENCY LIGHT CENTRAL MONITORING SYSTEM SCHEMATIC

Key Plan

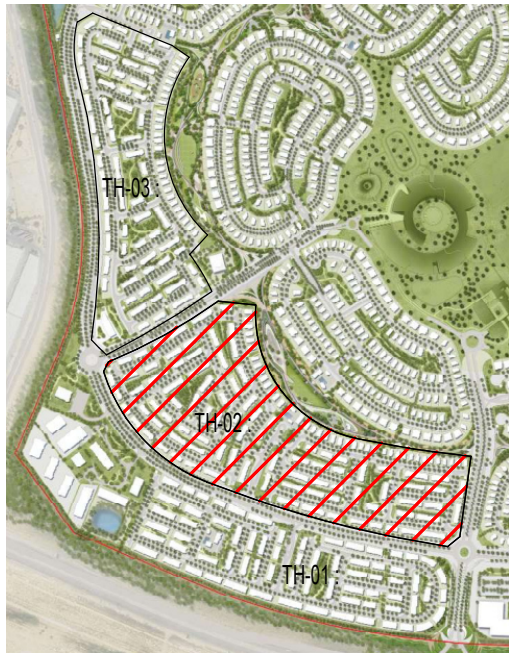

General Notes :

01. Do not Scale The Drawings. Follow (The MM) Written Dimensions Unless Otherwise Mentioned.
02. Each Drawing Shall be Read in Conjunction With all Other Drawings, Specification & the General Standard Details. In Case of Any Discrepancies Bring it to the Knowledge of Engineer and Same to be Resolved Prior to Execution of Work.
03. Dimensions Shown on These Drawings are Structural Dimensions Unless Noted Otherwise.
04. All Levels Indicated On These Drawings are Levels as per the Survey Datum, Same Should be Verified at Site Prior to Execution of Work.
05. All Levels Indicated On These Drawings are Based On Design Level, Which is Equivalent to Datum Level and Same Should be Verified at Site Prior to Execution of Work.

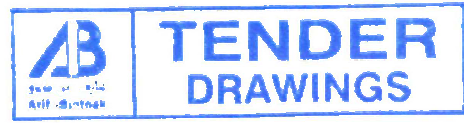

No.	Date	Initials	Description
-----	------	----------	-------------

REVISIONS / ISSUE

THIS DRAWING MUST NOT BE REPRODUCED IN WHOLE OR IN PART WITHOUT THE PRIOR APPROVAL OF ARIF & BINTOAK

TENDER SUBMISSION

Client

Lead Consultant



Project Title:

COMMUNITY CENTER -TH02
GRANDPOLP CLUB & RESORT, UAE

Discipline : ELECTRICAL

Drawing title:
COMMUNITY CENTER
EMERGENCY LIGHTING SINGLE
LINE DIAGRAM

Architectural Engineer	Electrical Engineer	Structural Engineer
MUSTAFA ABID	MARWAN MOHD.	RIHAM RAMADAN
Registration # 5847	Registration # 80102	Registration # 105092
Scale(s): 1 : 100	Date drawn: 10/03/2026	Project no: 1857
Drawn by: VPA	Checked: HAE	Approved: MRM

Drawing Number : GPCR-TH02-AB-DRG-ZZZ-ELE-EM-3022-00