

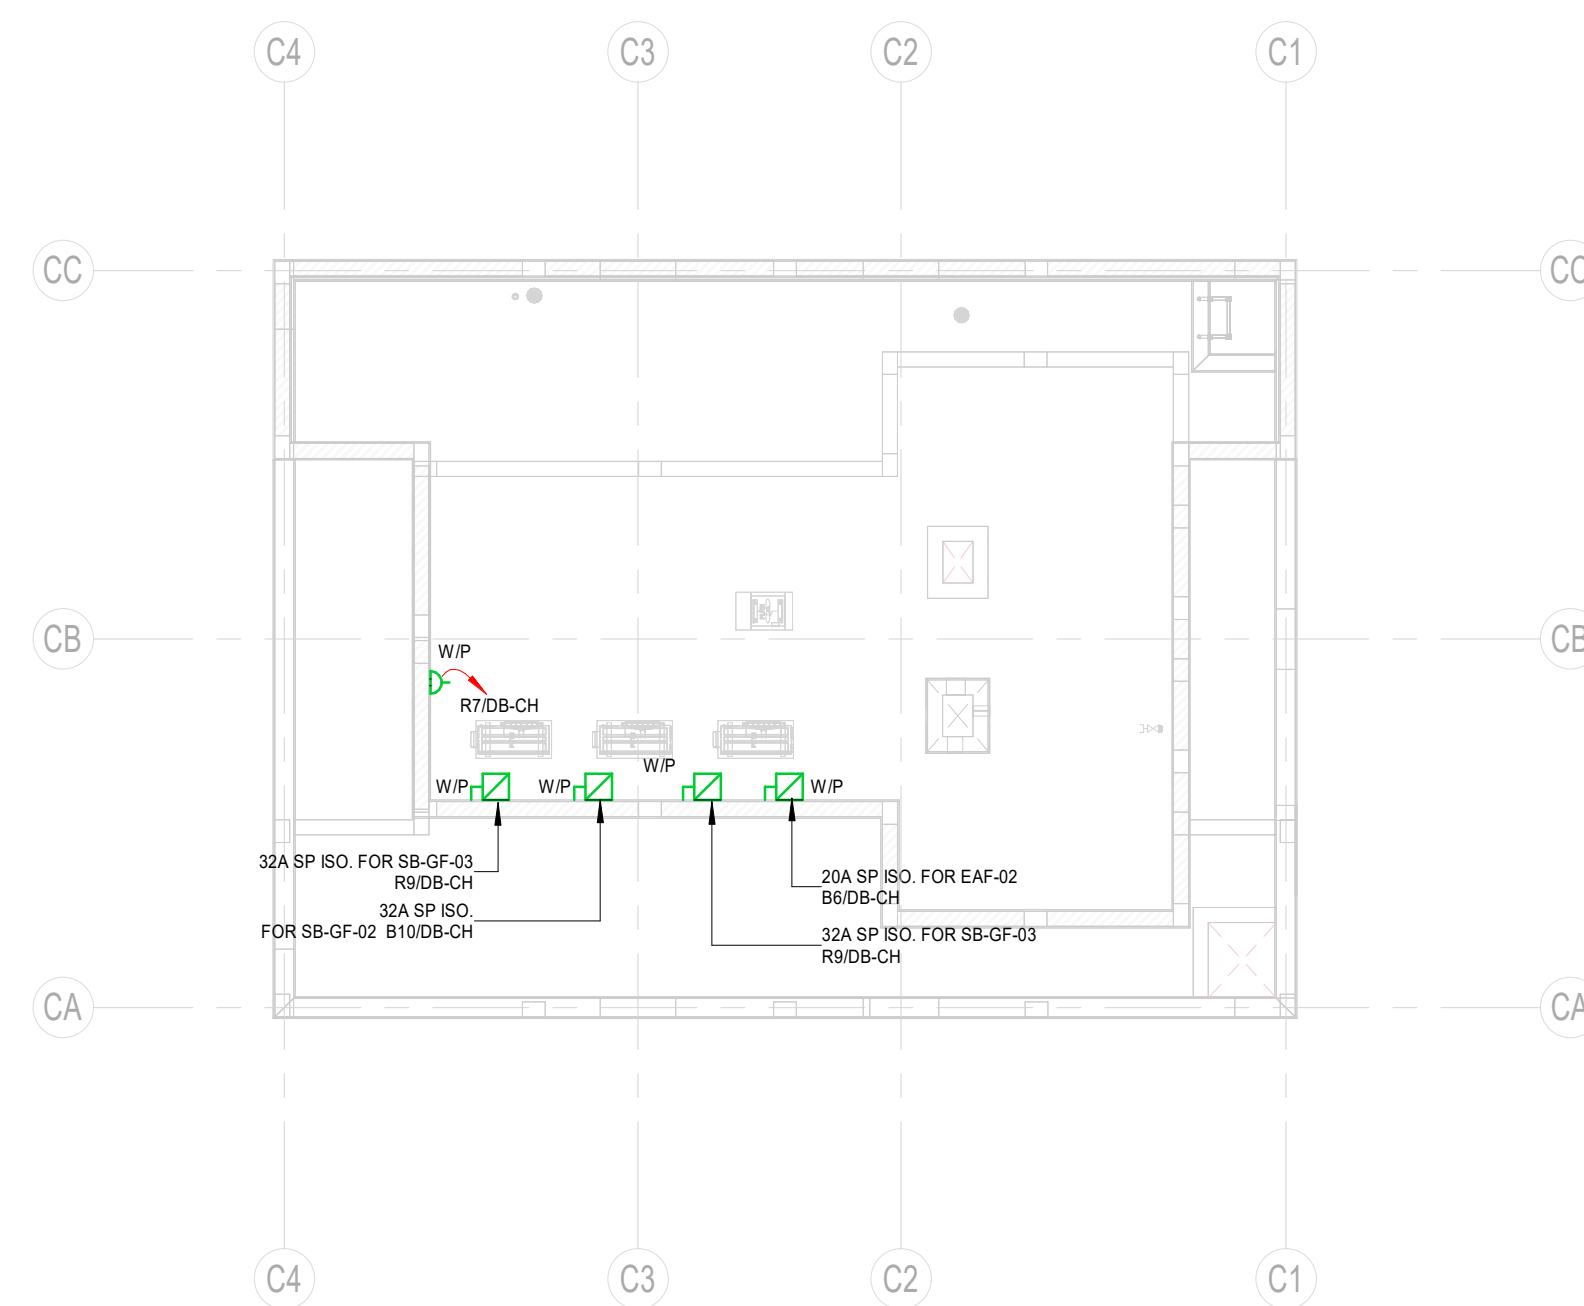


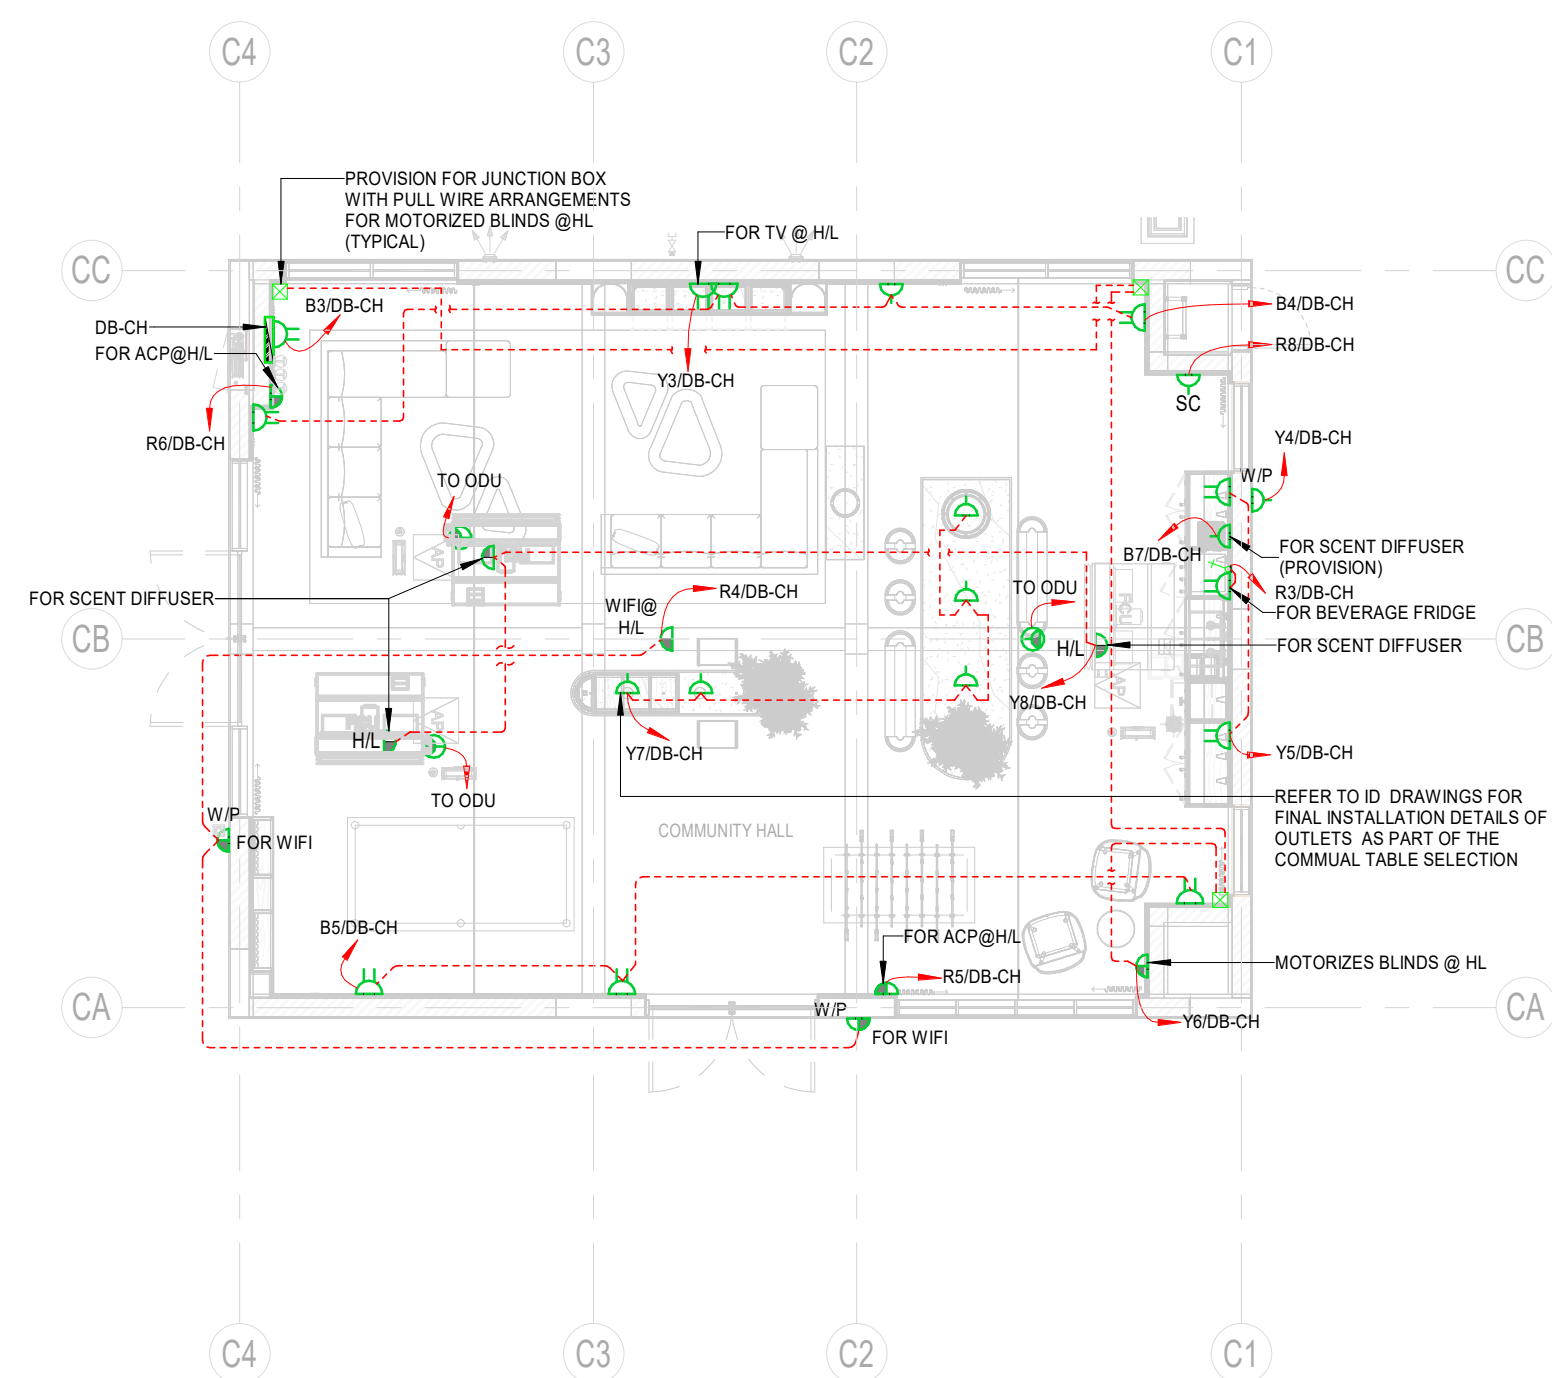

POWER LEGENDS	
	13A SINGLE SWITCHED SOCKET OUTLET
	13A TWIN SWITCHED SOCKET OUTLET
	FLEX OUTLET
	13A UN SWITCHED FUSED SPUR OUTLET
	13A SWITCHED FUSED SPUR OUTLET
	20A DP SWITCH WITH NEON SIGN INDICATOR.
 FCU	13A SWITCHED SPUR OUTLET WITH NEON INDICATOR FOR AC UNIT.
	SINGLE PHASE ISOLATOR IP 65 (RATING AS INDICATED)
	THREE PHASE ISOLATOR IP 65 (RATING AS INDICATED)
 DB-X-X	ELECTRICAL FINAL DISTRIBUTION BOARD (DB) ‘X’ INDICATING FLOOR REF, ‘Y’ INDICATING FLAT REF.
ABBREVIATION	
‘WP’ - WEATHER PROOF ‘HD’ - HAND DRYER	

	Key Plan
--	----------

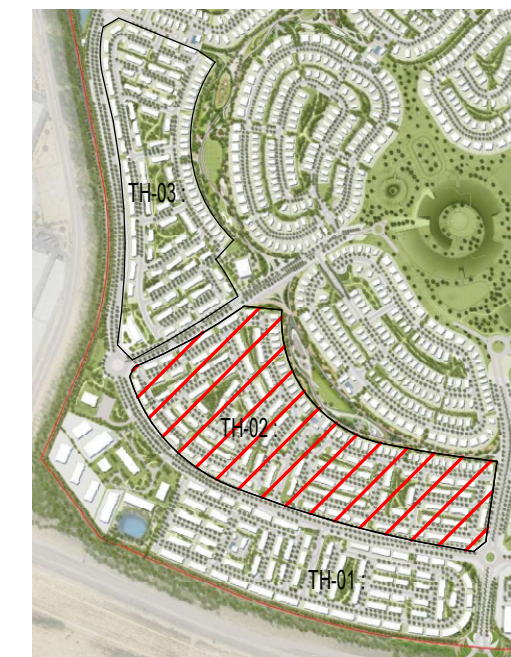

General Notes :

01. Do not Scale The Drawings. Follow The (MM) Written Dimensions Unless Otherwise Mentioned.
02. Each Drawing Shall be Read in Conjunction With all Other Drawings Specification & the General Standard Details. In Case of Any Discrepancies Bring it to the Knowledge of Engineer and Same to be Resolved Prior to Execution of Work.
03. Dimensions Shown on These Drawings are Structural Dimensions Unless Noted Otherwise.
04. All Levels Indicated On These Drawings are Levels as per the Survey Datum, Same Should be Verified at Site Prior to Execution of Work.
05. All Levels Indicated On These Drawings are Based On Design Level, Which is Equivalent to Datum Level and Same Should be Verified at Site Prior to Execution of Work.



00	10/03/2026	VPA	TENDER SUBMISSION
No.	Date	Initials	Description
REVISIONS / ISSUE			

THIS DRAWING MUST NOT BE REPRODUCED IN WHOLE OR IN PART WITHOUT THE PRIOR APPROVAL OF ARIF & BINTOAK

Status	TENDER SUBMISSION
--------	-------------------

Client

EMAAR

Lead Consultant



Project Title:

COMMUNITY CENTER -TH02
GRANDPOLP CLUB & RESORT, UAE

Discipline : **ELECTRICAL**

Drawing title:
**COMMUNITY HALL GROUND &
ROOF FLOOR PLAN POWER
LAYOUT**

Architectural Engineer	Electrical Engineer	Structural Engineer
MUSTAFA ABID	MARWAN MOHD.	RIHAM RAMADAN
Registration # 5847	Registration # 60102	Registration # 105092
Scale(s): 1 : 100	Date drawn: 10/03/2026	Project no: 1857
Drawn by: VPA	Checked : HAE	Approved : MRM

Drawing Number :	GPCR-TH02-AB-DRG-ZZZ-ELE-EP-3003-01
------------------	-------------------------------------