



This 2D drawing is extracted from 3D BIM Model

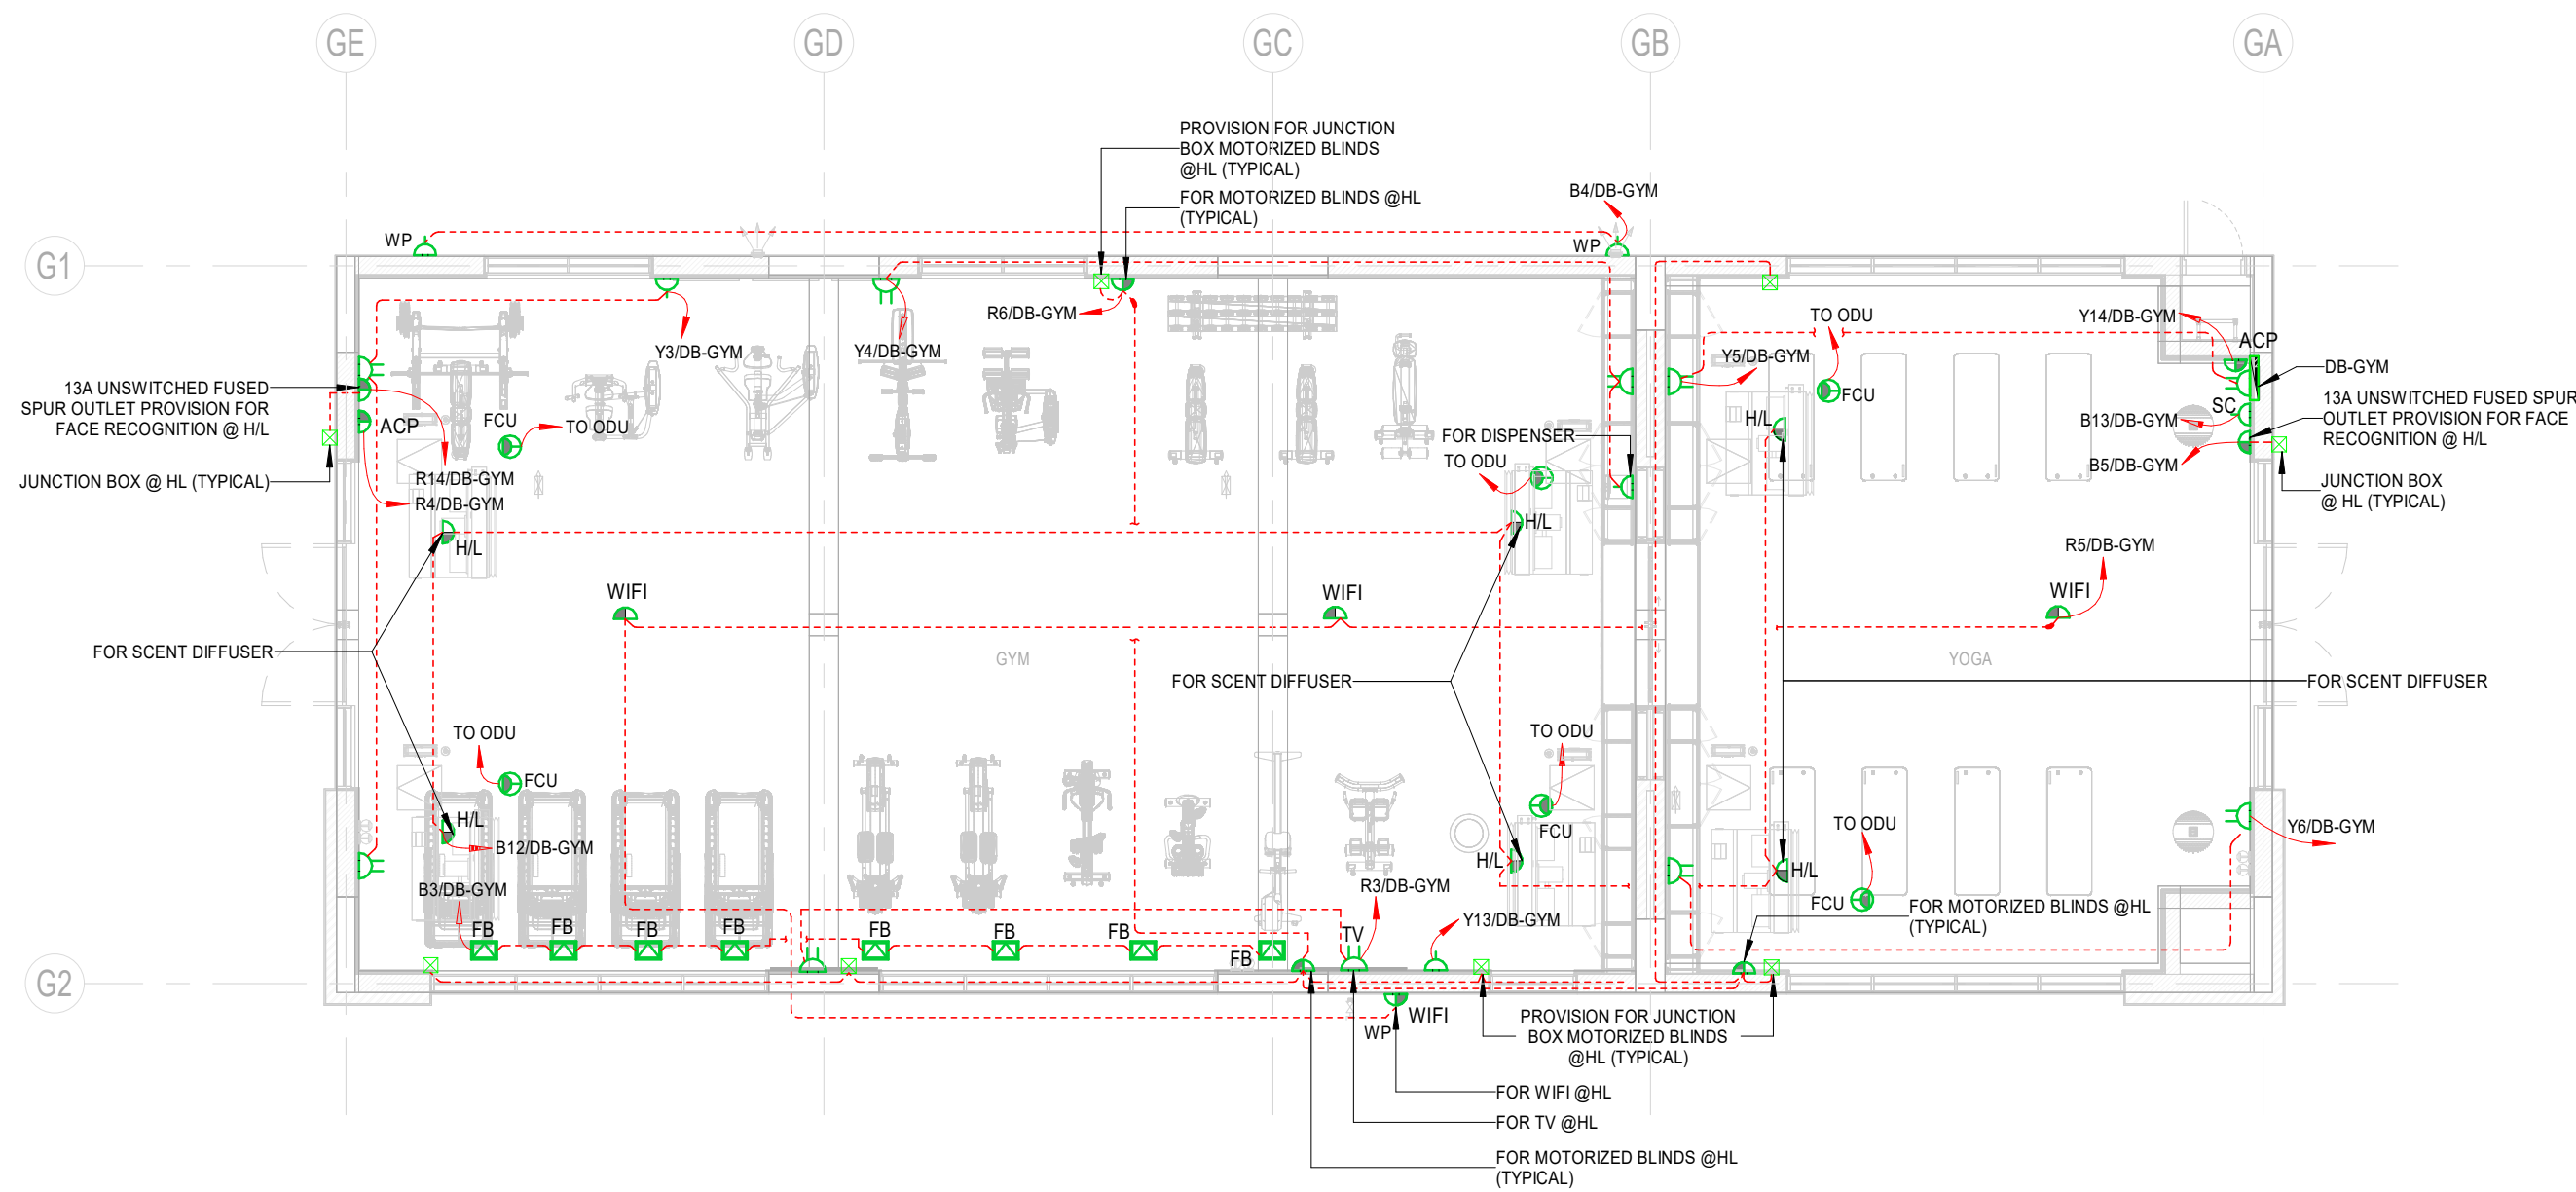


1 01-GROUND FLOOR GYM POWER  
1 : 100

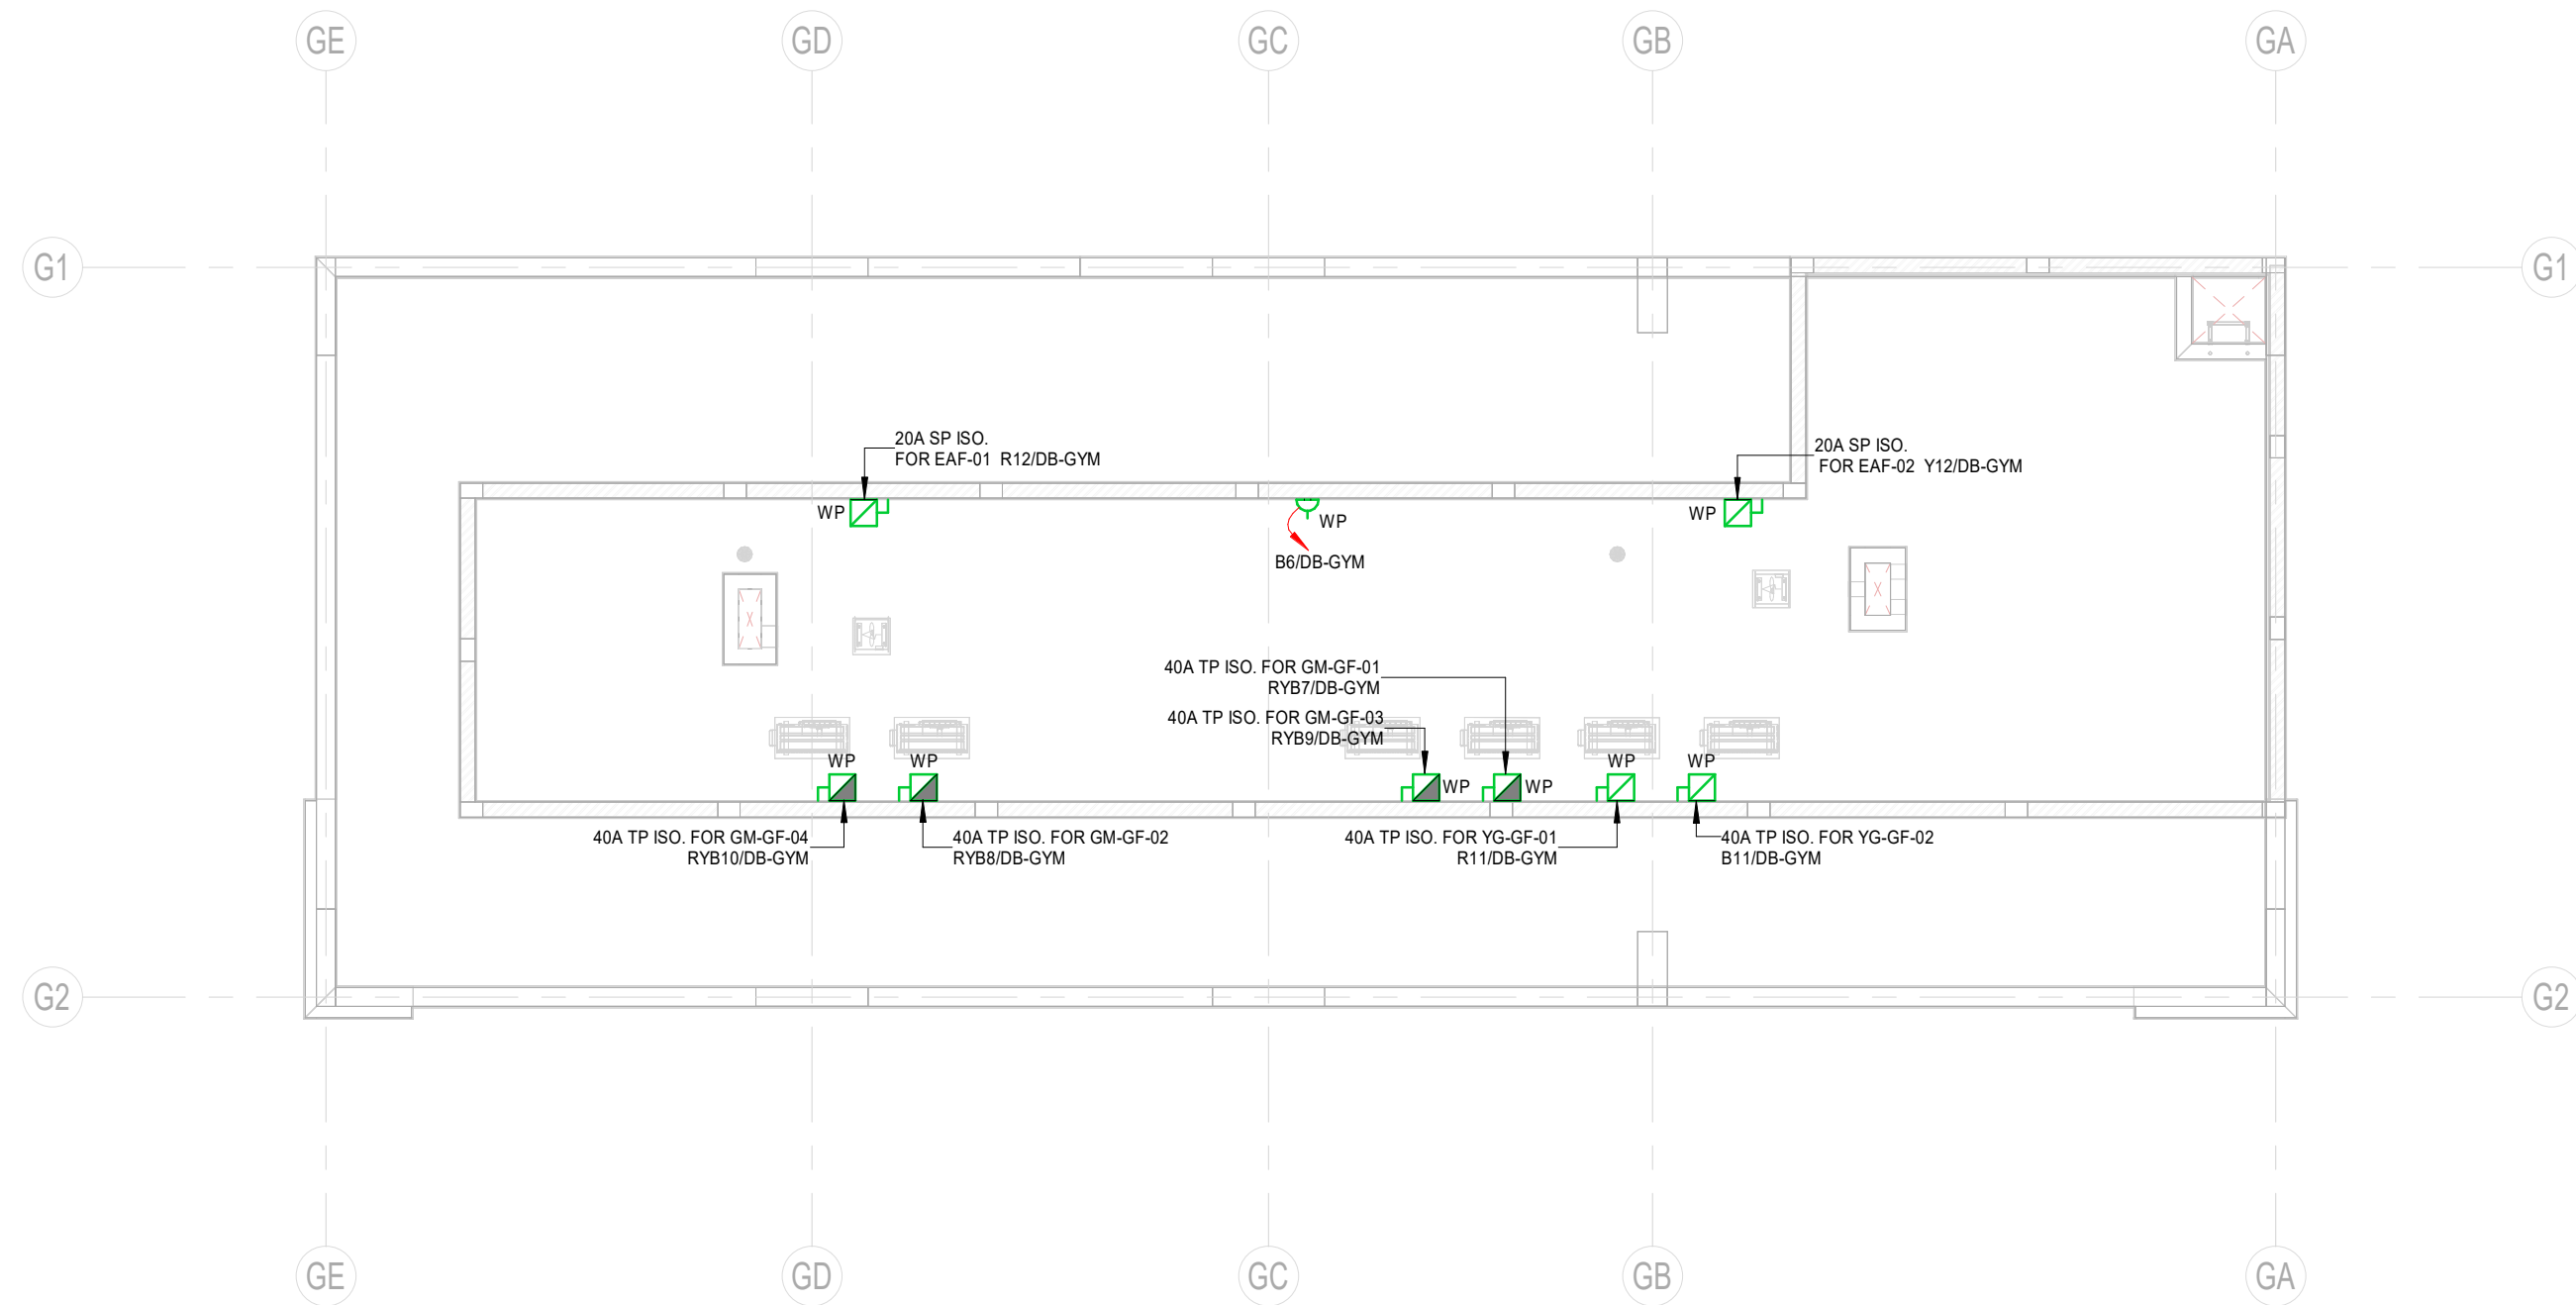


2 02-ROOF GYM POWER  
1 : 100

| POWER LEGENDS |                                                            |
|---------------|------------------------------------------------------------|
|               | 13A SINGLE SWITCHED SOCKET OUTLET                          |
|               | 13A TWIN SWITCHED SOCKET OUTLET                            |
|               | FLOOR BOX (13A SINGLE SOCKET)                              |
|               | FLEX OUTLET                                                |
|               | 13A UN SWITCHED FUSED SPUR OUTLET                          |
|               | 13A SWITCHED FUSED SPUR OUTLET                             |
|               | 20A DP SWITCH WITH NEON SIGN INDICATOR.                    |
|               | 20A FLEX OUTLET                                            |
|               | 13A SWITCHED SPUR OUTLET WITH NEON INDICATOR FOR A/C UNIT. |
|               | SINGLE PHASE ISOLATOR IP 65 (RATING AS INDICATED)          |
|               | THREE PHASE ISOLATOR IP 65 (RATING AS INDICATED)           |
|               | ELECTRICAL FINAL DISTRIBUTION BOARD (DB)                   |
|               | 'X' INDICATING FLOOR REF, 'X' INDICATING FLAT REF.         |
| ABBREVIATION  |                                                            |
| 'WP'          | - WEATHER PROOF                                            |
| 'HD'          | - HAND DRYER                                               |

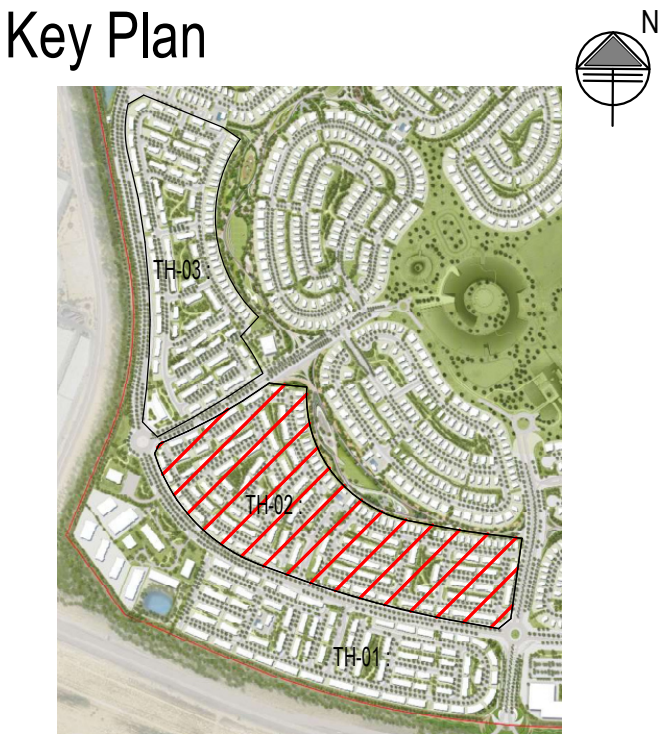

- General Notes :**
01. Do not Scale The Drawings. Follow (The MM) Written Dimensions Unless Otherwise Mentioned.
  02. Each Drawing Shall be Read in Conjunction With all Other Drawings, Specification & the General Standard Details. In Case of Any Discrepancies Bring it to the Knowledge of Engineer and Same to be Resolved Prior to Execution of Work.
  03. Dimensions Shown on These Drawings are Structural Dimensions Unless Noted Otherwise.
  04. All Levels Indicated On These Drawings are Levels as per the Survey Datum, Same Should be Verified at Site Prior to Execution of Work.
  05. All Levels Indicated On These Drawings are Based On Design Level, Which is Equivalent to Datum Level and Same Should be Verified at Site Prior to Execution of Work.

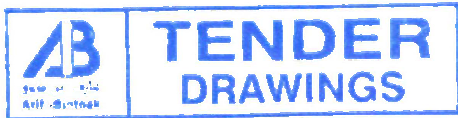

| 00                                                                                                   | 10/03/2026                                           | VPA                   | TENDER SUBMISSION |
|---|------------------------------------------------------|-----------------------|-------------------|
| No.                                                                                                  | Date                                                 | Initials              | Description       |
| REVISIONS / ISSUE                                                                                    |                                                      |                       |                   |
| THIS DRAWING MUST NOT BE REPRODUCED IN WHOLE OR IN PART WITHOUT THE PRIOR APPROVAL OF ARIF & BINTOAK |                                                      |                       |                   |
| Status                                                                                               | TENDER SUBMISSION                                    |                       |                   |
| Client                                                                                               | EMAAR                                                |                       |                   |
| Lead Consultant                                                                                      |                                                      |                       |                   |
| Project Title:                                                                                       | COMMUNITY CENTER - TH02 GRANDPOLP CLUB & RESORT, UAE |                       |                   |
| Discipline :                                                                                         | ELECTRICAL                                           |                       |                   |
| Drawing title:                                                                                       | GYM GROUND & ROOF FLOOR PLAN POWER LAYOUT            |                       |                   |
| Architectural Engineer                                                                               | Electrical Engineer                                  | Structural Engineer   |                   |
| MUSTAFA ABID                                                                                         | MARWAN MOHD.                                         | RIHAM RAMADAN         |                   |
| Registration # 5847                                                                                  | Registration # 80102                                 | Registration # 105092 |                   |
| Scale(s):<br>1 : 100                                                                                 | Date drawn:<br>10/03/2026                            | Project no:<br>1857   |                   |
| Drawn by:<br>VPA                                                                                     | Checked:<br>HAE                                      | Approved:<br>MRM      |                   |
| Drawing Number :                                                                                     | GPCR-TH02-AB-DRG-ZZZ-ELE-EP-3005-00                  |                       |                   |