

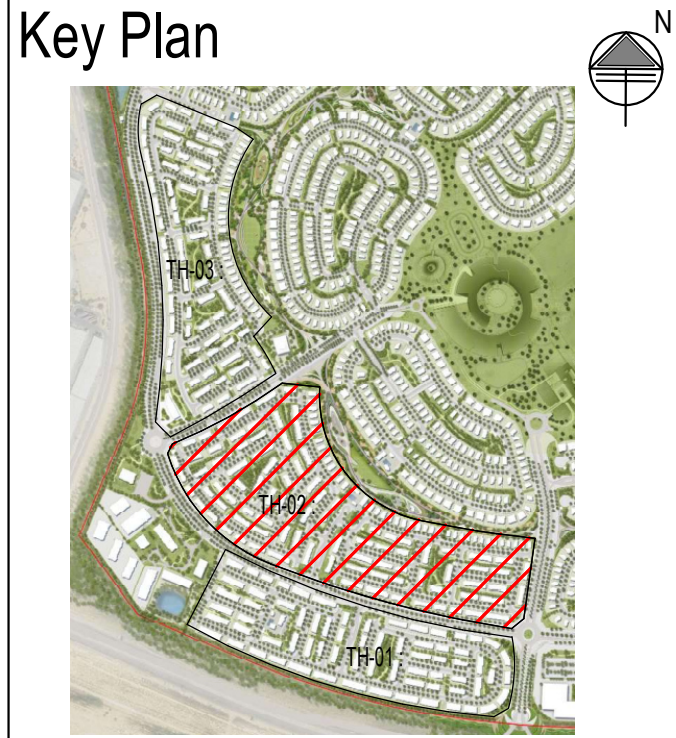
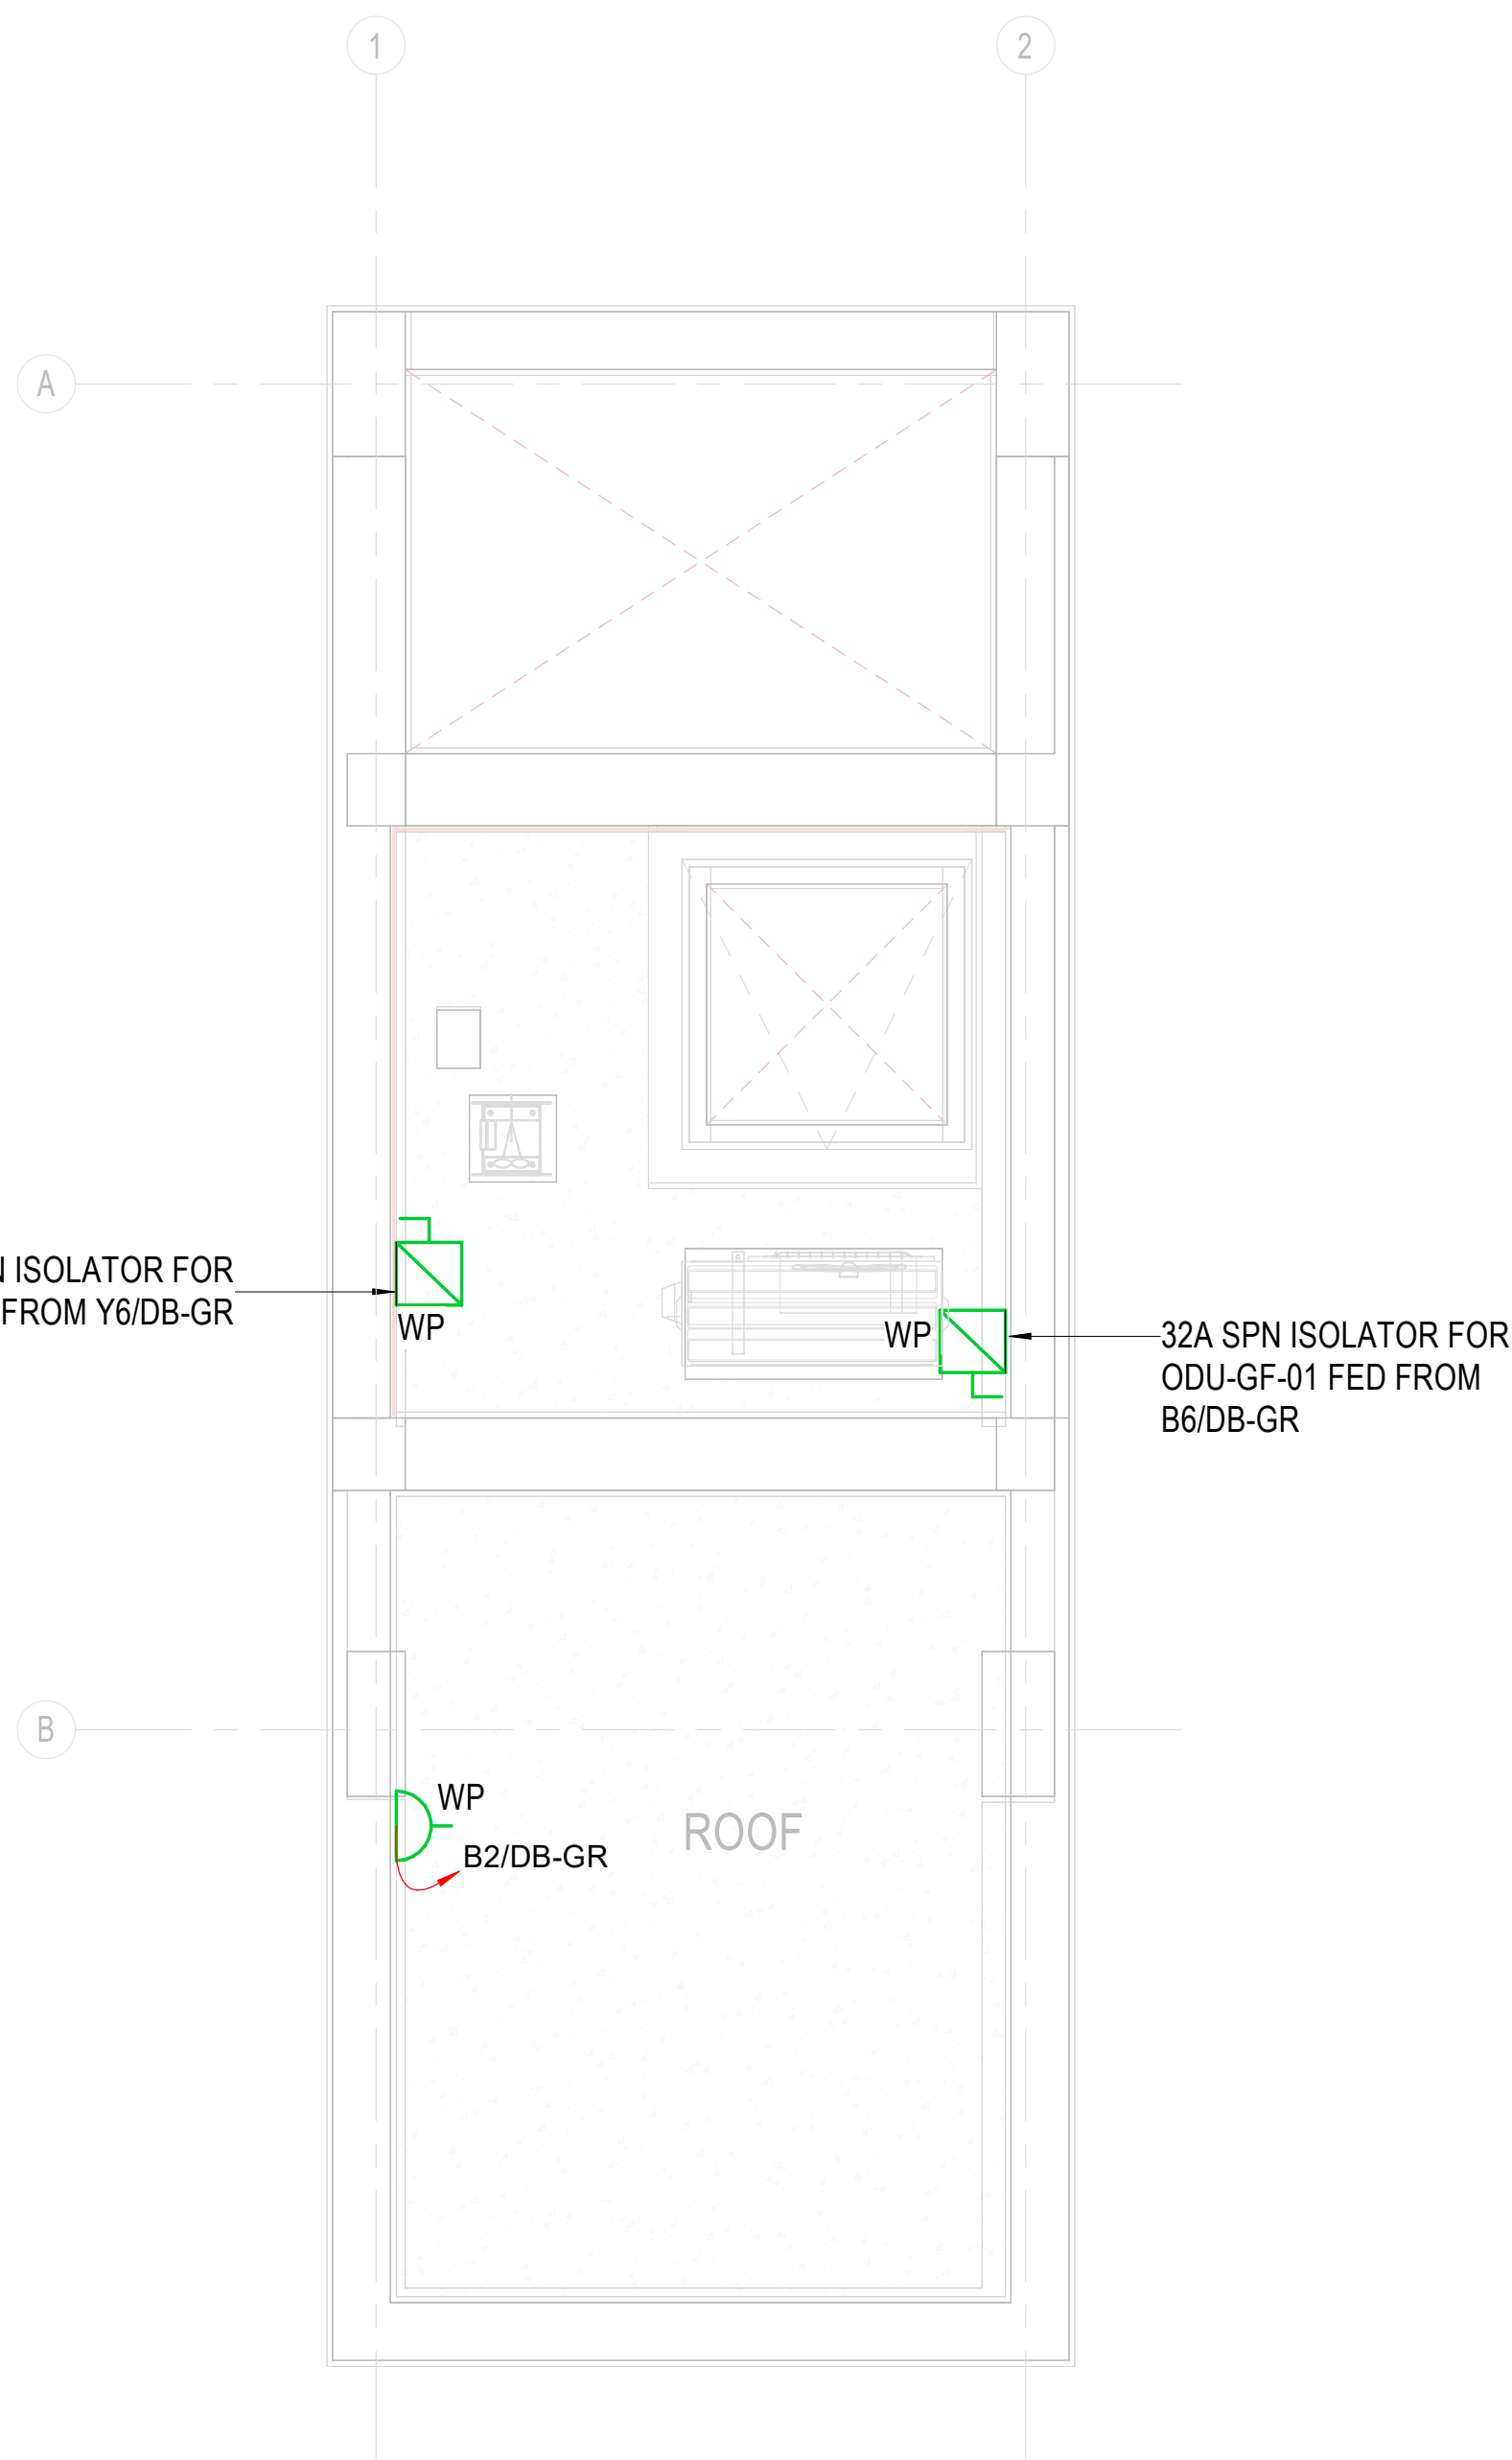


This 2D drawing is extracted from 3D BIM Model

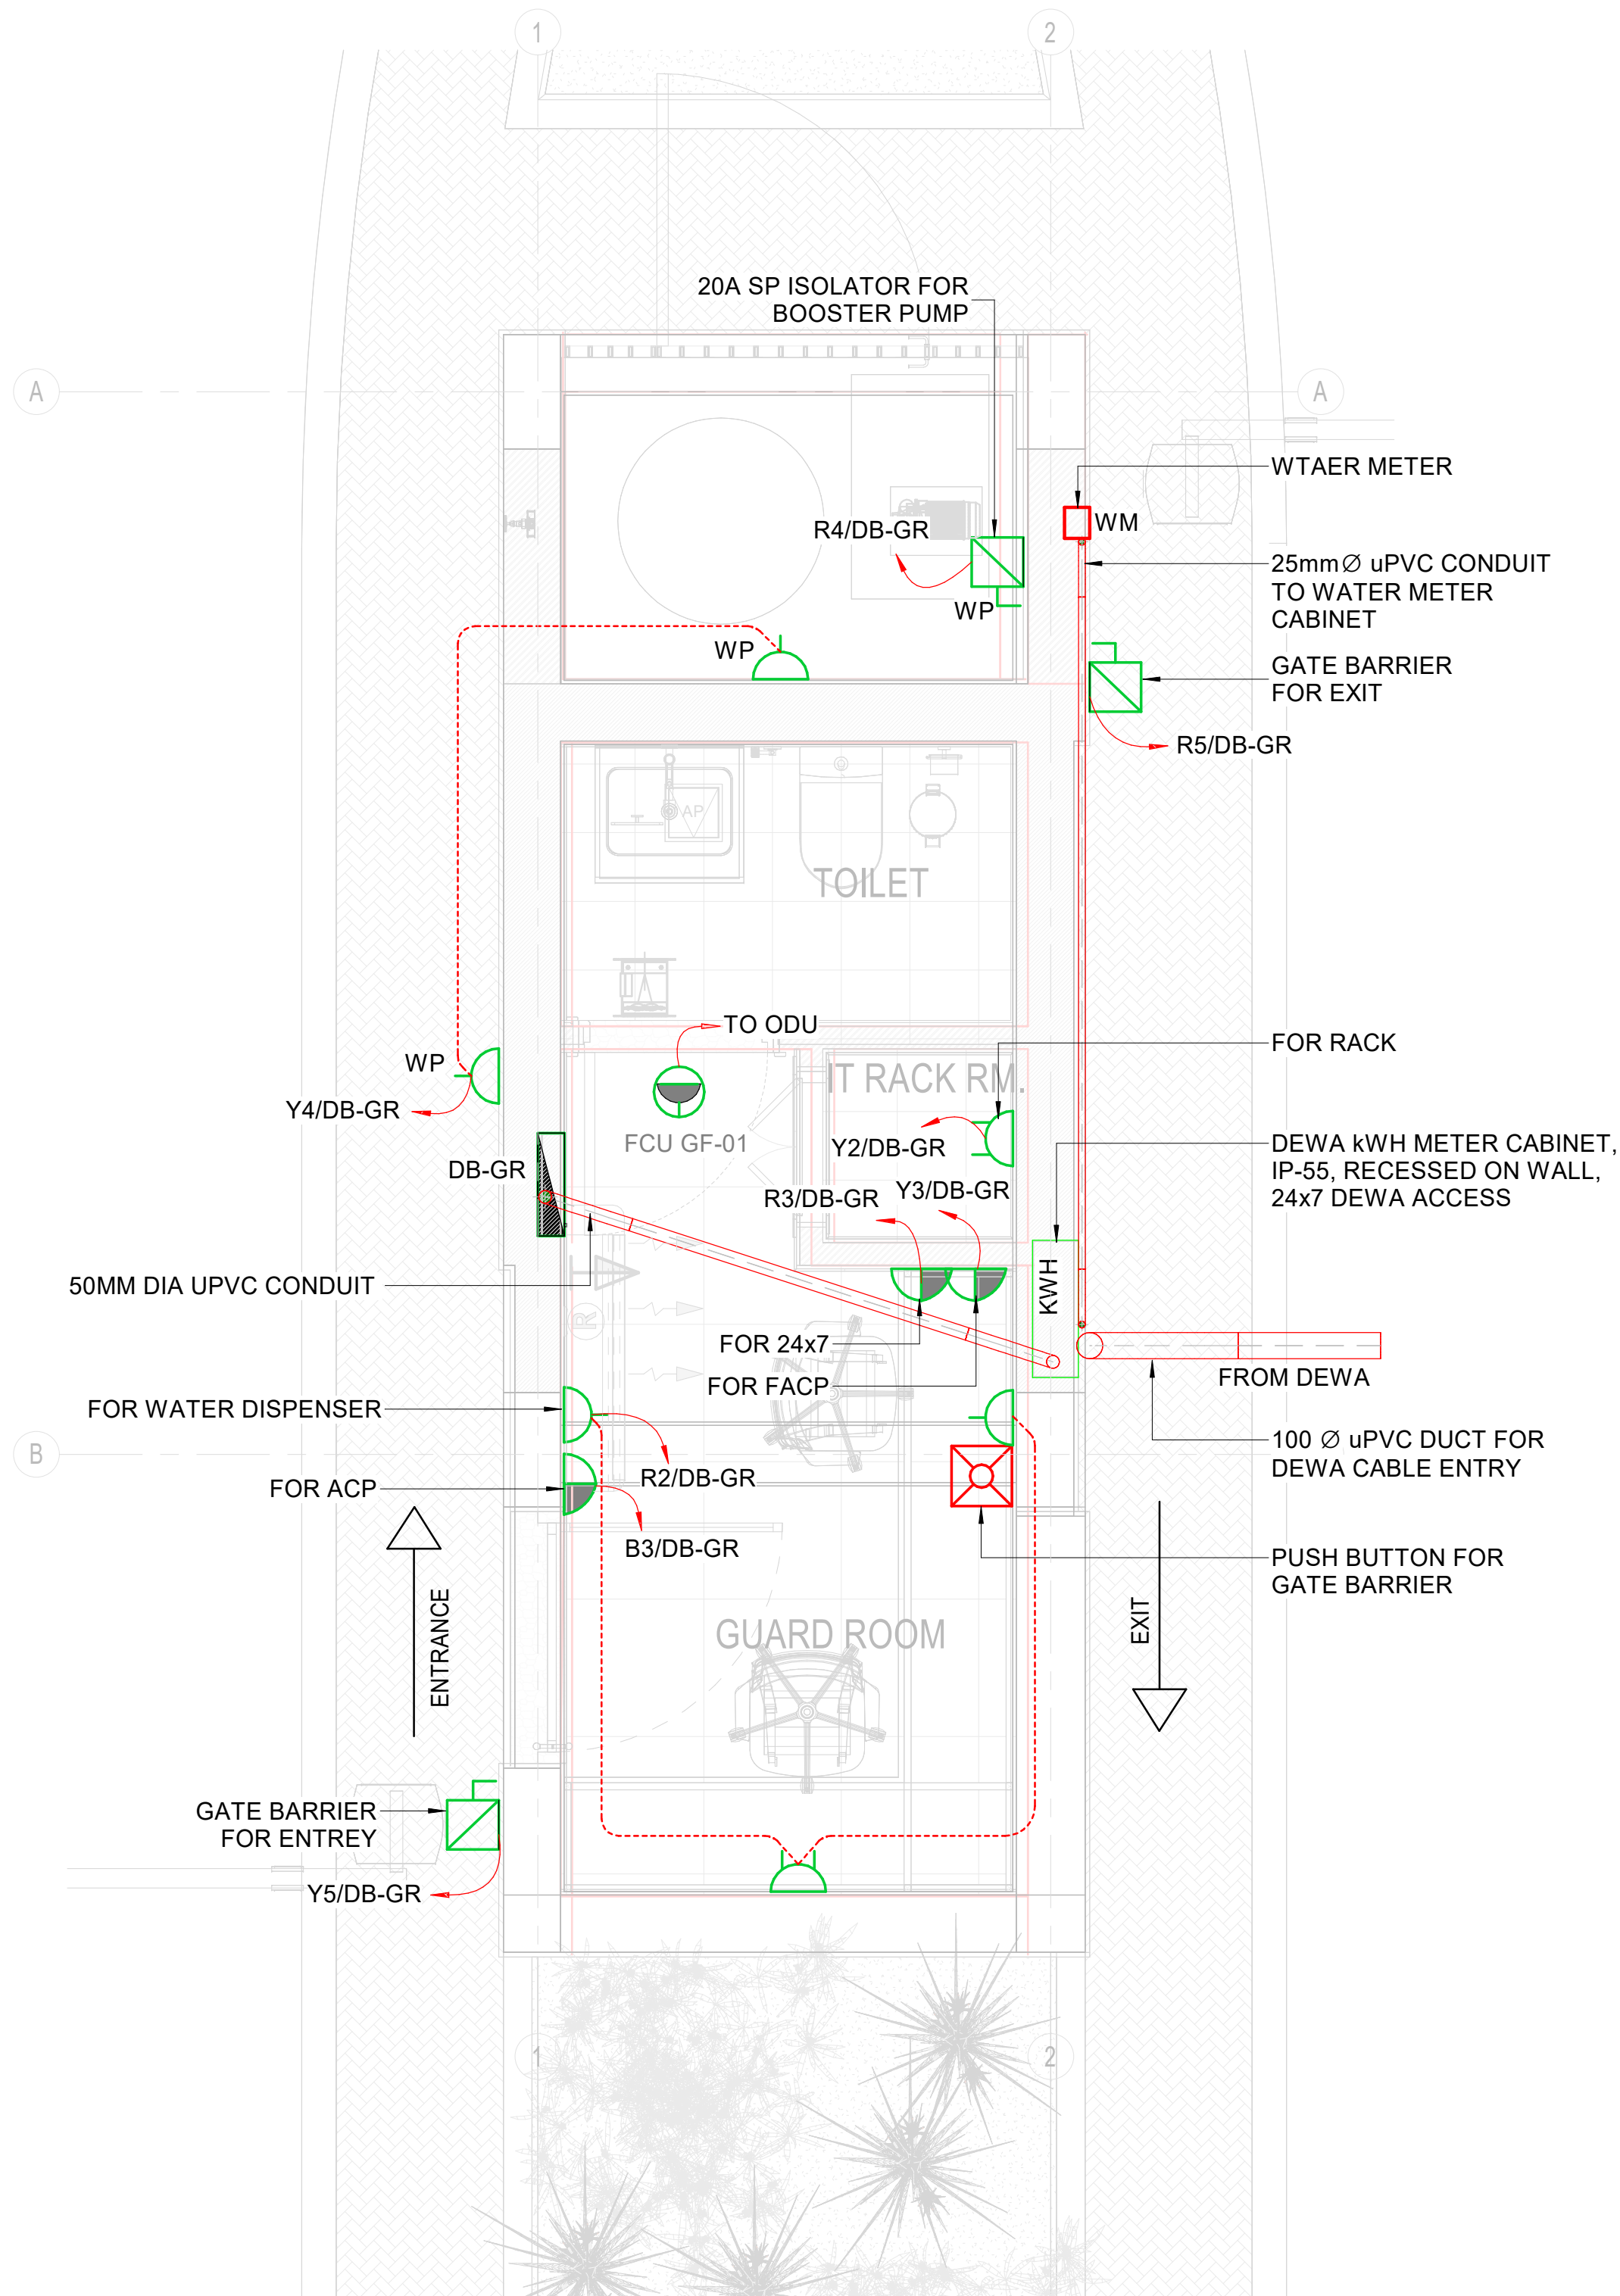

- General Notes :**
01. Do not Scale The Drawings. Follow (The MM) Written Dimensions Unless Otherwise Mentioned.
 02. Each Drawing Shall be Read in Conjunction With all Other Drawings, Specification & the General Standard Details. In Case of Any Discrepancies Bring it to the Knowledge of Engineer and Same to be Resolved Prior to Execution of Work.
 03. Dimensions Shown on These Drawings are Structural Dimensions Unless Noted Otherwise.
 04. All Levels Indicated On These Drawings are Levels as per the Survey Datum, Same Should be Verified at Site Prior to Execution of Work.
 05. All Levels Indicated On These Drawings are Based On Design Level, Which is Equivalent to Datum Level and Same Should be Verified at Site Prior to Execution of Work.

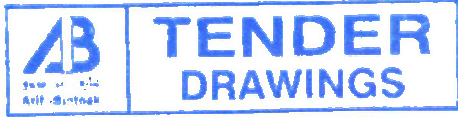

No.	10/03/2026	SPG	TENDER SUBMISSION
No.	Date	Initials	Description
REVISIONS / ISSUE			
THIS DRAWING MUST NOT BE REPRODUCED IN WHOLE OR IN PART WITHOUT THE PRIOR APPROVAL OF ARIF & BINTOAK			
Status	TENDER SUBMISSION		
Client	EMAAR		
Lead Consultant	 الأستاذي : عارف وبن طوق Arif & BintOak consulting architects & engineers POST BOX 3476 DUBAI UAE TEL: 04-3372884 FAX: 04-3372852 POST BOX 42861 ABU DHABI UAE TEL: 02-655566 website@arifbintoak.com.ae		
Project Title:	GUARD HOUSE GRANDPOLO CLUB & RESORT, UAE		
Discipline :	ELECTRICAL		
Drawing title:	GUARD HOUSE GROUND & ROOF FLOOR PLAN POWER LAYOUT		
Architectural Engineer	Electrical Engineer	Structural Engineer	
MUSTAFA ABID	MARWAN MOHD.	RIHAM RAMADAN	
Registration # 5847	Registration # 80102	Registration # 105092	
Scale(s): As indicated	Date drawn: 10/03/2026	Project no: 1857	
Drawn by: VPA	Checked: HAE	Approved : MRM	
Drawing Number :	GPCR-TH02-AB-DRG-ZZZ-ELE-EP-4001-00		