




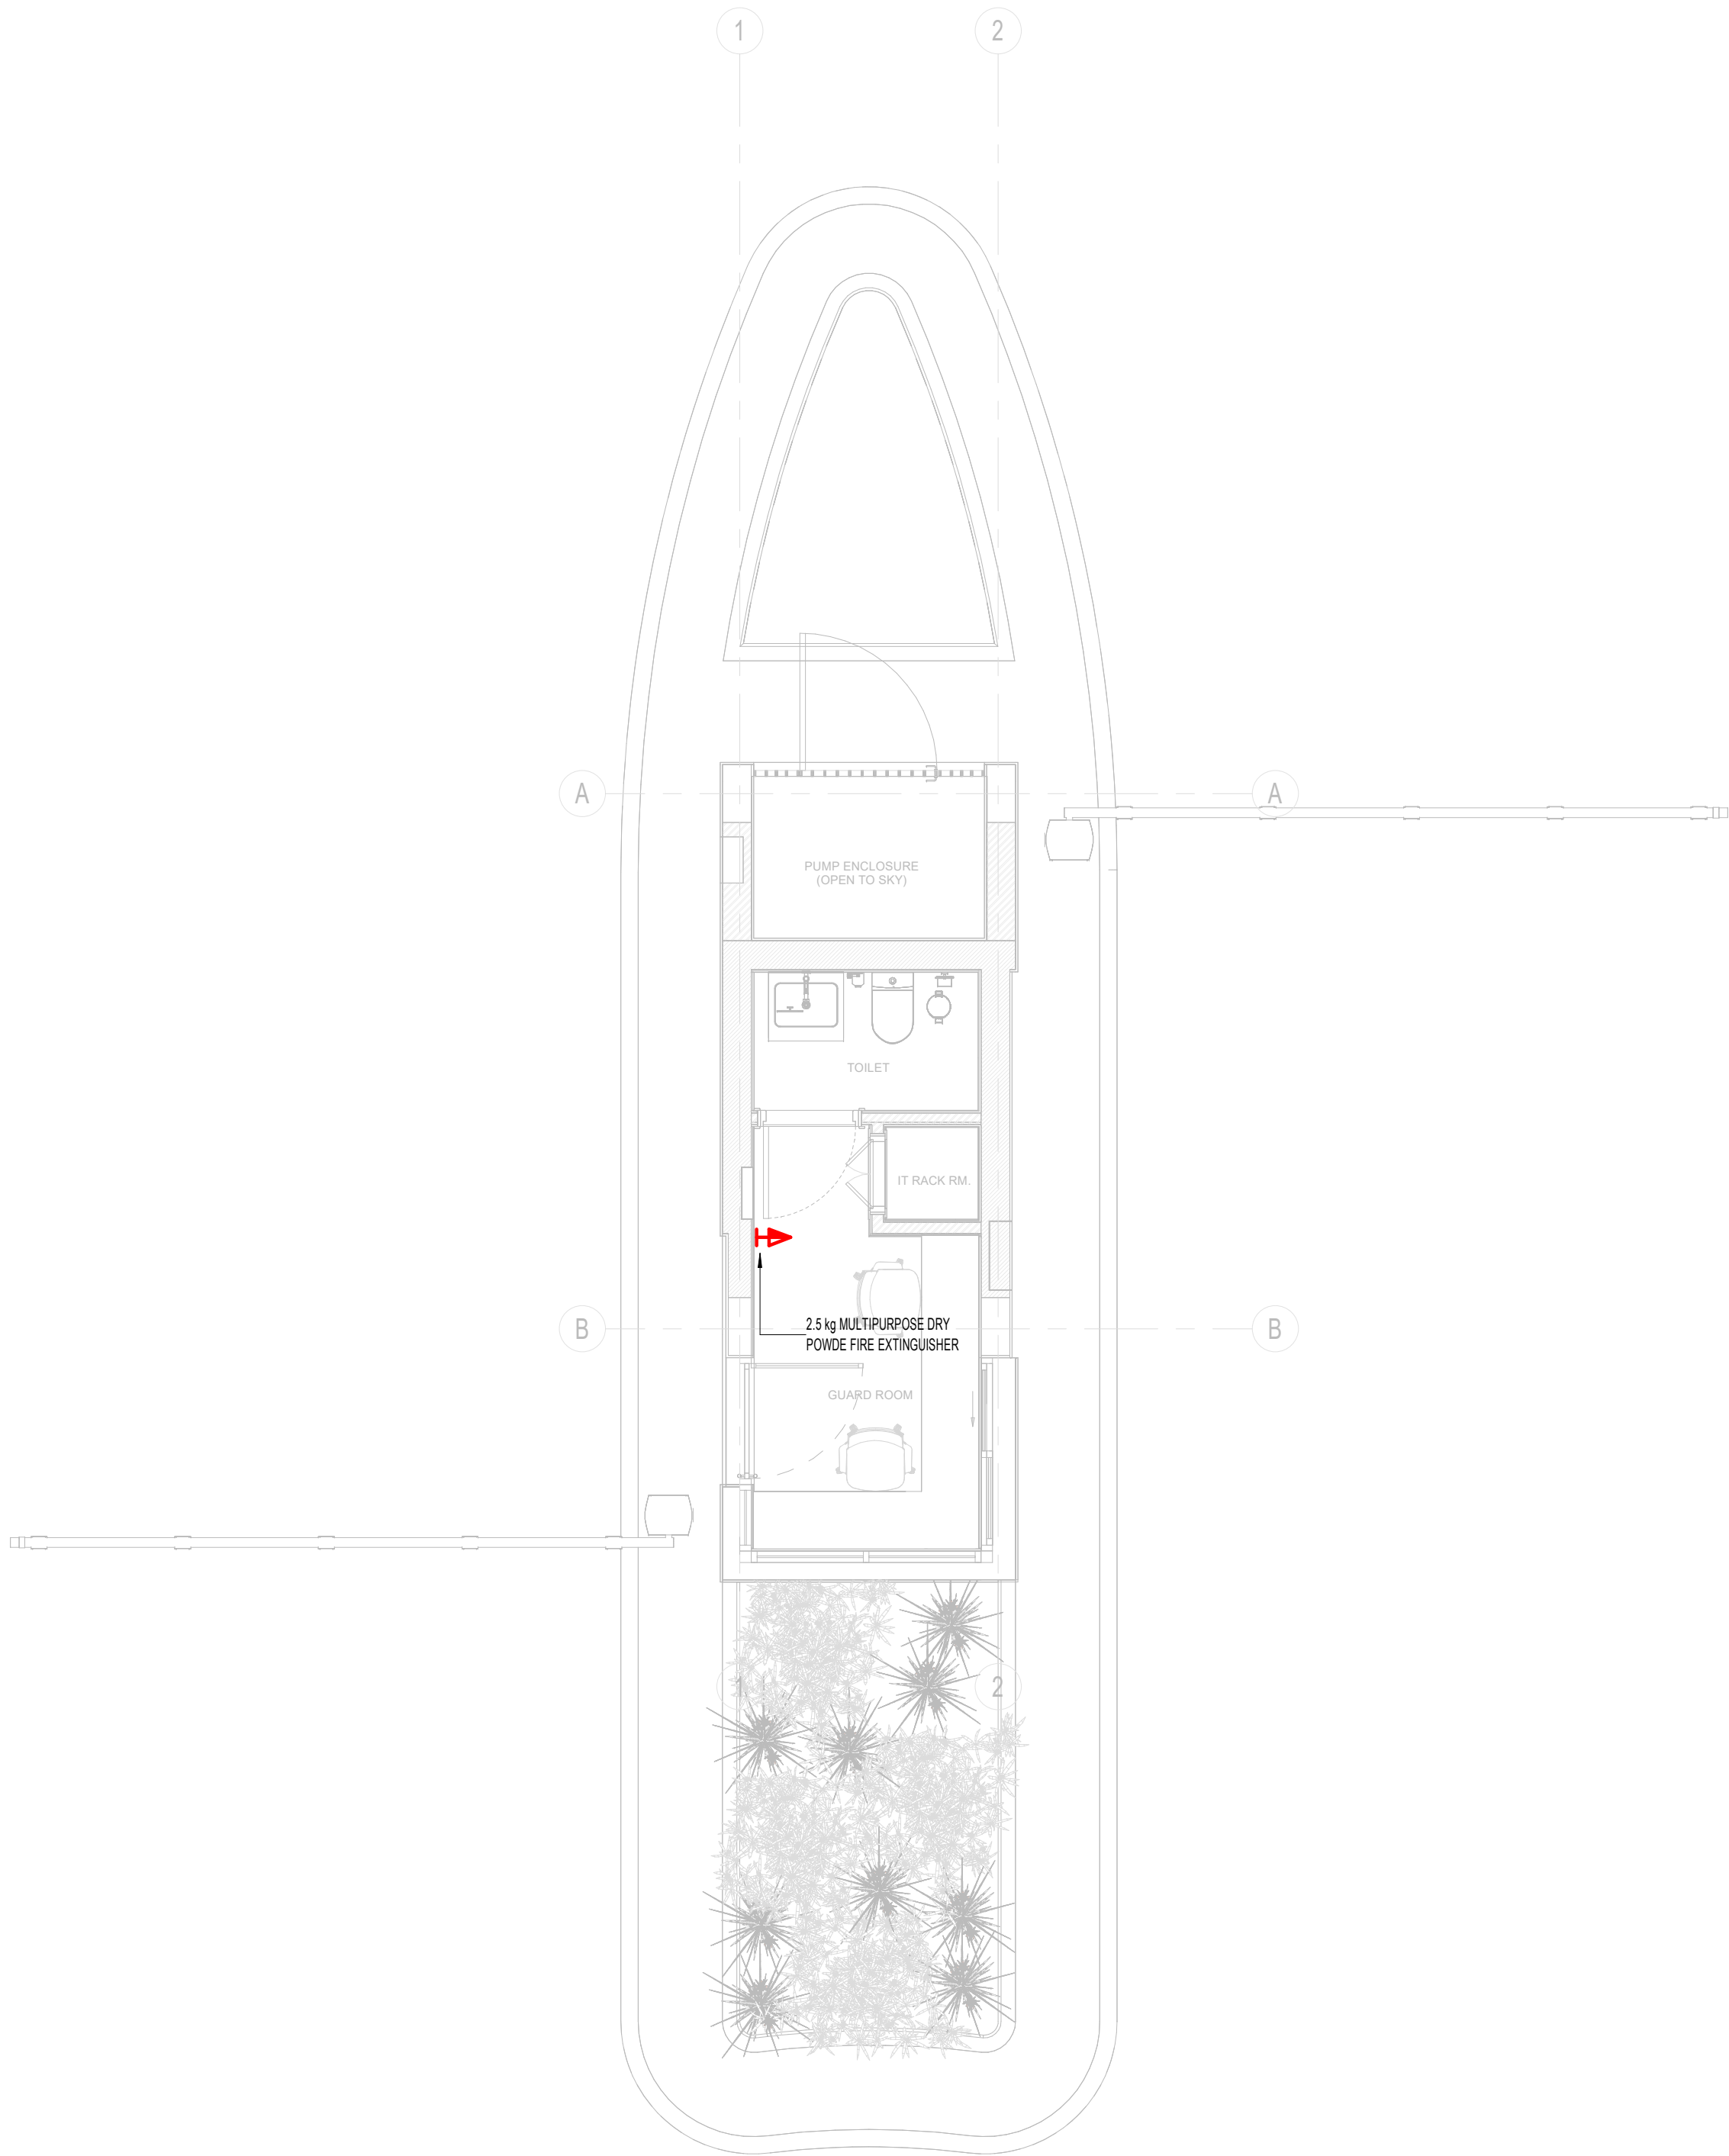

1 GROND FLOOR PLAN FIRE FIGHTING LAYOUT
1 : 50

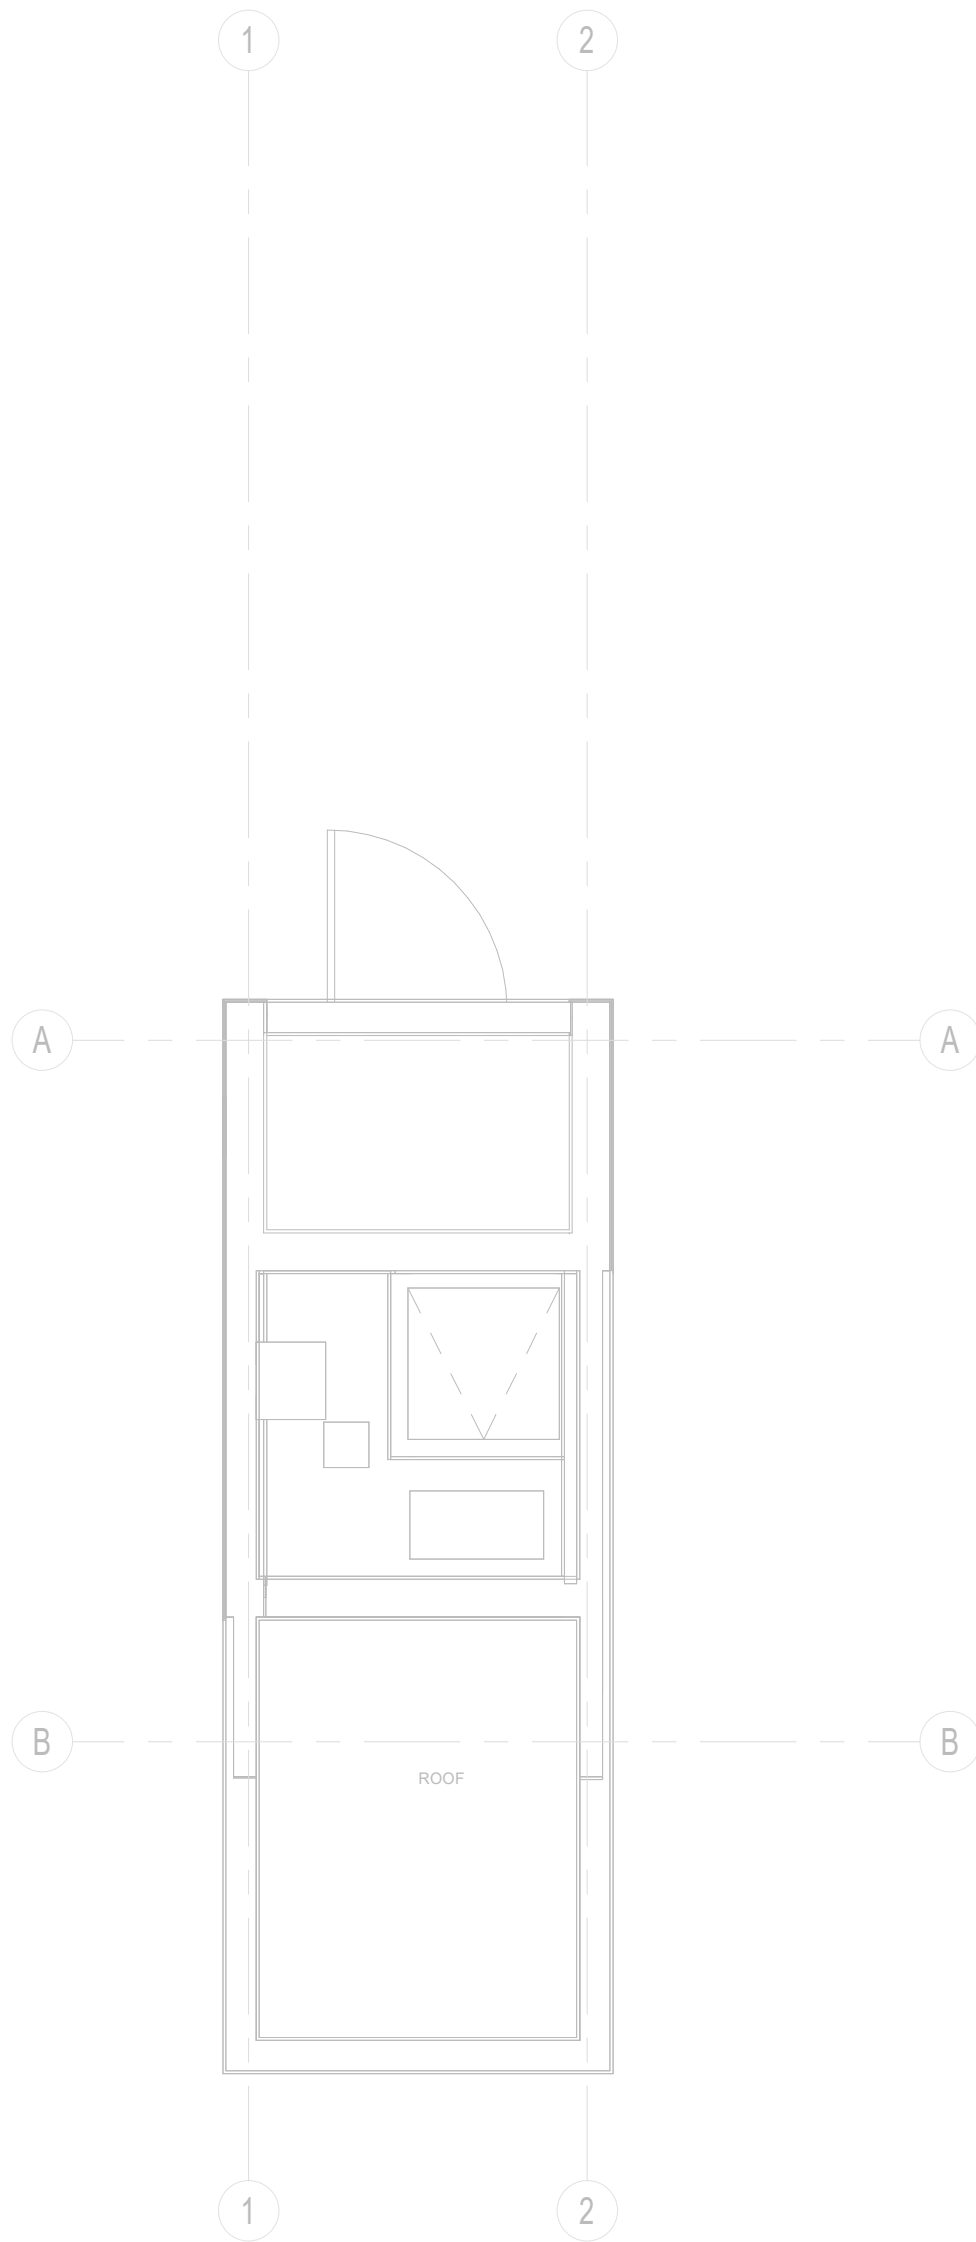

2 ROOF FLOOR PLAN FIRE FIGHTING LAYOUT
1 : 50

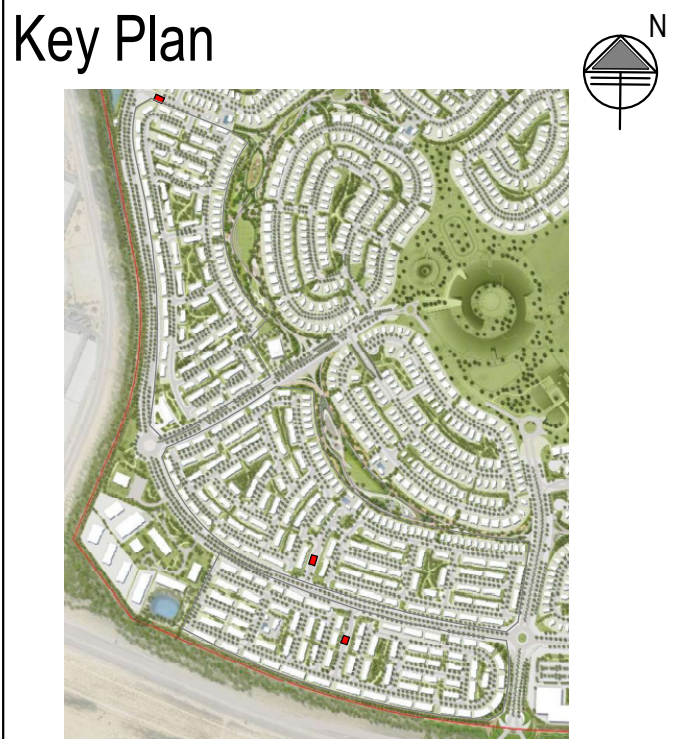

- General Notes :**
- 01. Do not Scale The Drawings. Follow (The MM) Written Dimensions Unless Otherwise Mentioned.
 - 02. Each Drawing Shall be Read in Conjunction With all Other Drawings Specification & the General Standard Details. In Case of Any Discrepancies Bring it to the Knowledge of Engineer and Same to be Resolved Prior to Execution of Work.
 - 03. Dimensions Shown on These Drawings are Structural Dimensions. Unless Noted Otherwise.
 - 04. All Levels Indicated On These Drawings are Levels as per the the Survey Datum, Same Should be Verified at Site Prior to Execution of Work.
 - 05. All Levels Indicated On These Drawings are Based On Design Level, Which is Equivalent to Datum Level and Same Should be Verified at Site Prior to Execution of Work.



00	10/03/2026	LSG	TENDER SUBMISSION
00	16/01/2026	LSG	DETAILED DESIGN SUBMISSION
00	31/10/2025	LSG	SCHEMATIC DESIGN SUBMISSION
00	15/10/2025	IMS	SCHEMATIC SUBMISSION-50%
00	01/09/2025	LSG	CONCEPT DESIGN SUBMISSION

No.	Date	Initials	Description
-----	------	----------	-------------

REVISIONS / ISSUE

THIS DRAWING MUST NOT BE REPRODUCED IN WHOLE OR IN PART WITHOUT THE PRIOR APPROVAL OF ARIF & BINTOAK

Status
TENDER SUBMISSION

Client
EMAAR



Project Title:
Proposed Residential Townhouses
and Standalone Villas
TH-1, TH-2, and TH-3 at Grand Polo
Club & Resort, Dubai, UAE

Discipline :
MECHANICAL

Drawing title:
GUARD HOUSE FIRE LAYOUT

Architectural Engineer	Electrical Engineer	Structural Engineer
MUSTAFA ABID	MARWAN MOHD.	RIHAM RAMADAN
Registration # 5847	Registration # 80102	Registration # 105092
Scale(s): 1 : 50	Date: 10/03/2026	Project no: 1830
Drawn by: LSG	Checked: MAV	Approved: MRM

Drawing Number : GPCR-TH02-AB-DRG-ZZZ-MEC-FF-6403-00