




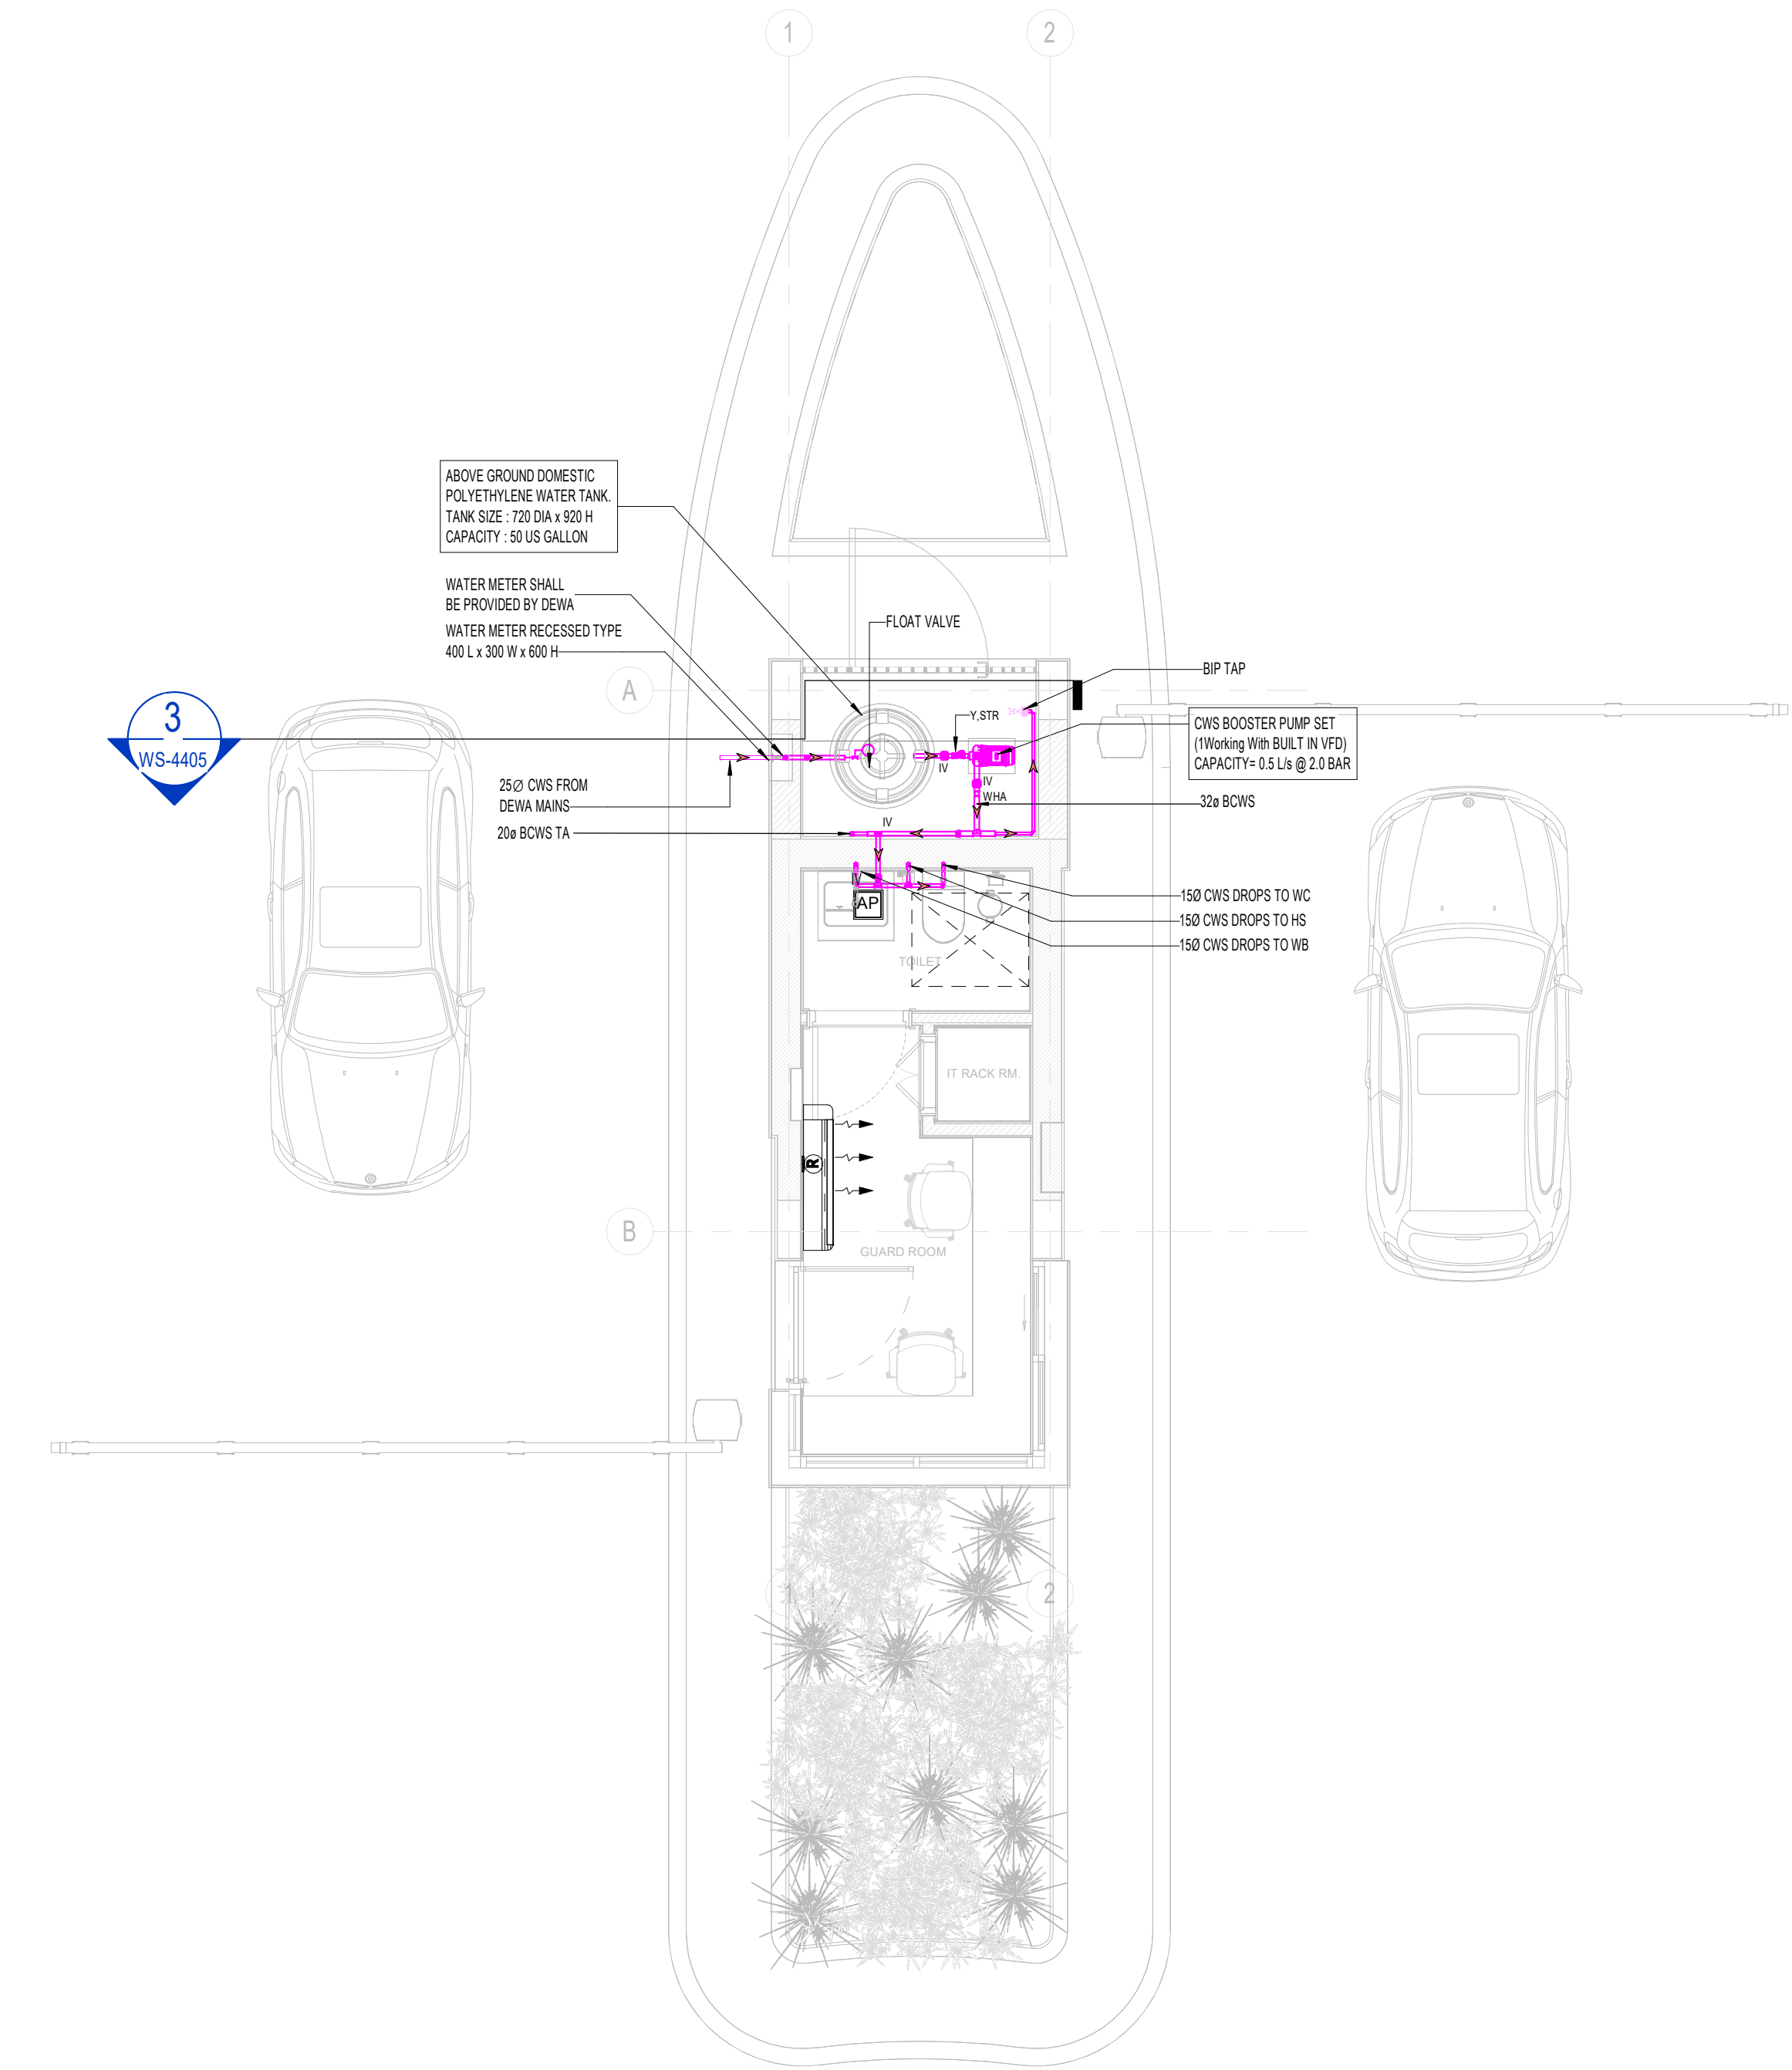

1 GROND FLOOR PLAN WATER SUPPLY LAYOUT  
1 : 50

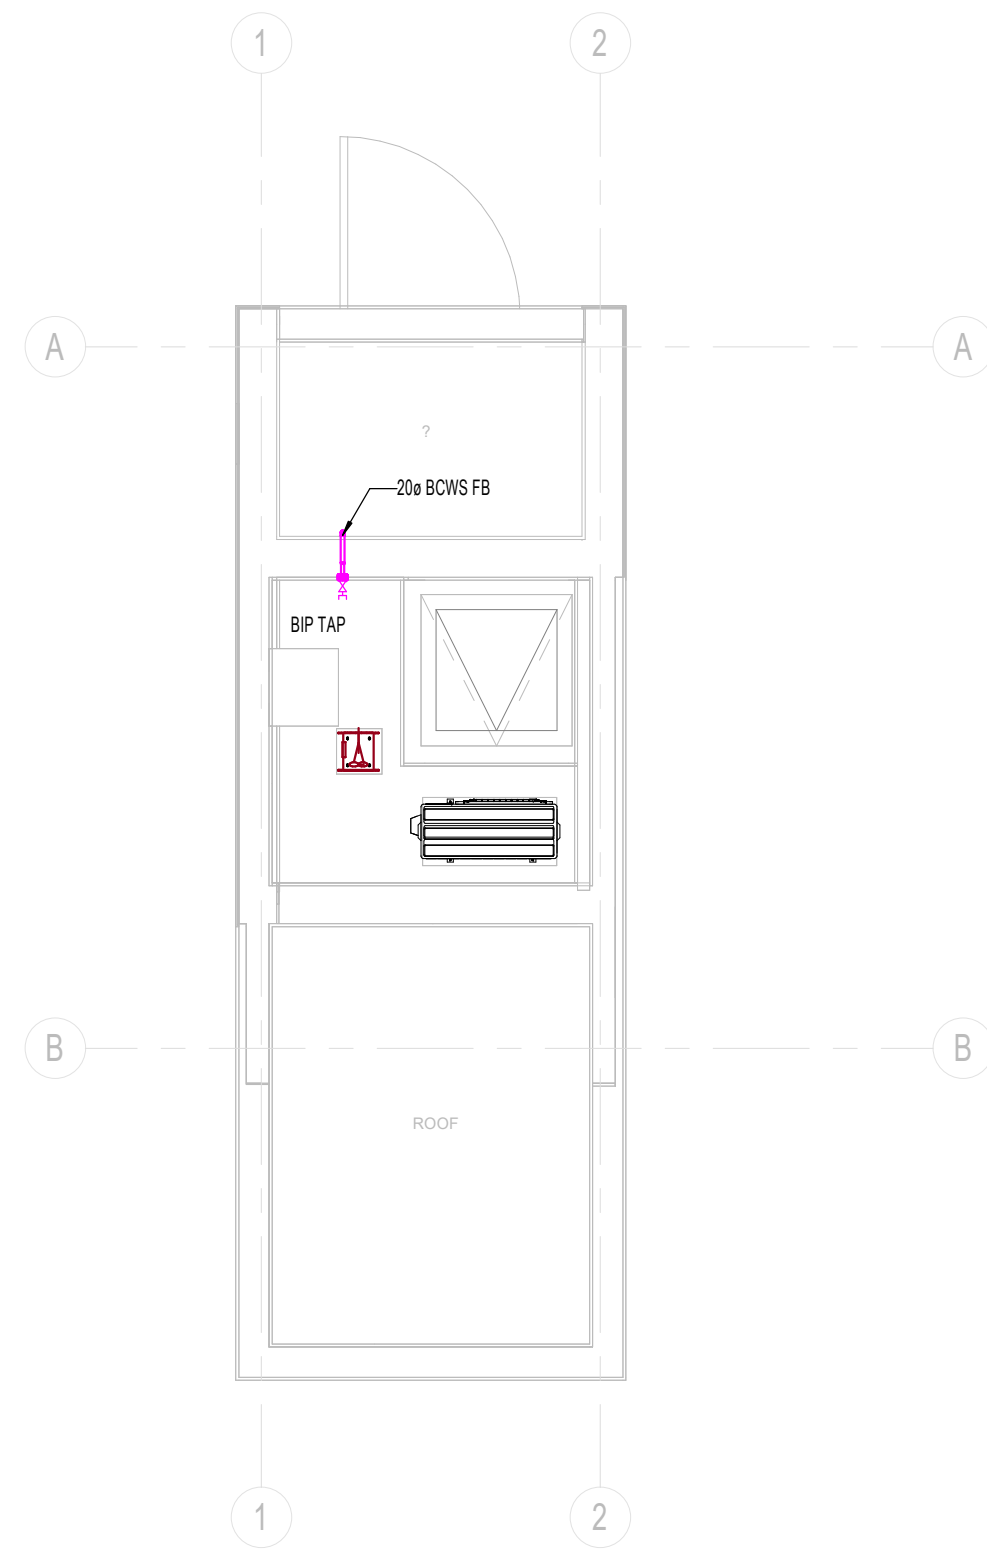


2 ROOF FLOOR PLAN WATER SUPPLY LAYOUT  
1 : 50

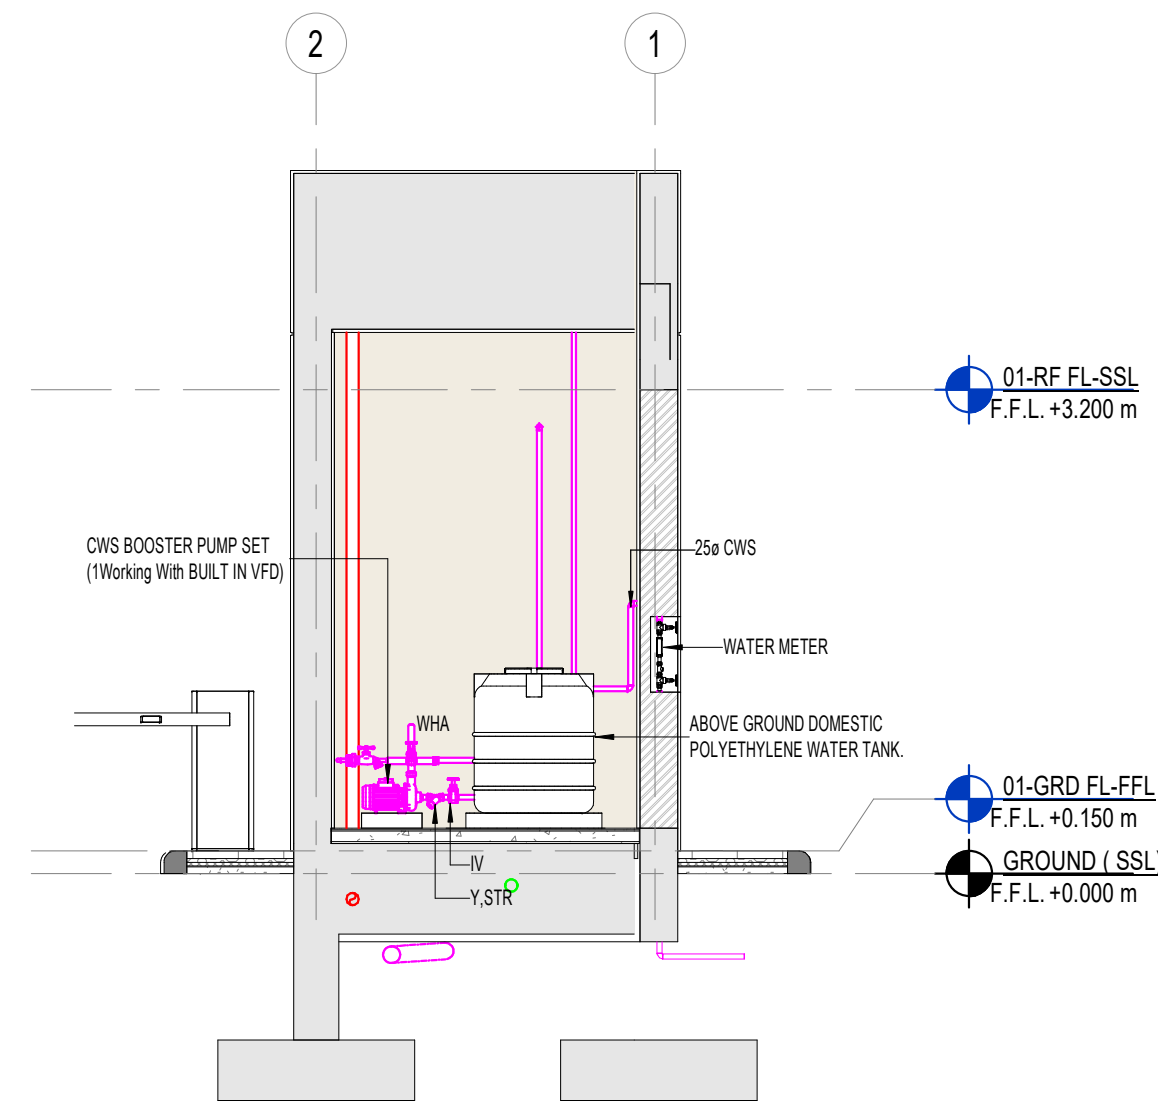


3 WATER SUPPLY PUMP ROOM  
1 : 50

| GHs PUMP SCHEDULE   |                       |                     |                                             |           |       |      |                       |             |        |      |                           |   |
|---|-----------------------|---------------------|---------------------------------------------|-----------|-------|------|-----------------------|-------------|--------|------|---------------------------|---|
| SI No   | EQUIPMENT DESCRIPTION | SERVICE             | TYPE                                        | LOCATION  | FLOW  | HEAD | TOTAL NO.OF PUMP SETS | NO.OF PUMPS |        |      | ESTIMATED EACH PUMP POWER | REMARK   |
|   |                       |                     |                                             |           | (L/s) | (m)  |                       | DUTY        | ASSIST | S/BY | kW                        |   |
| 1   | Water Booster pump    | Water Booster pumps | Compact Horizontal End Suction Built In VFD | Pump room | 0.50  | 19   | 1                     | 1           | 0      | 0    | 0.37                      | Skid Mounted Smart Starter Panel, pump shall be Built In VFD, Controlled by PLC of the packaged unit, with a built in pressure vessel. |
| NOTES:   |                       |                     |                                             |           |       |      |                       |             |        |      |                           |   |
| 1 - CONTRACTOR SHALL PROVIDE THE PUMP HEAD CALCULATION BASED ON INSTALLED PIPING CONNECTIONS, FITTINGS AS PER SITE CONDITION FOR ENGINEERS APPROVAL. |                       |                     |                                             |           |       |      |                       |             |        |      |                           |   |

| GHs - Water Tank |                       |              |                   |              |               |         |
|------------------|-----------------------|--------------|-------------------|--------------|---------------|---------|
| SI No            | EQUIPMENT DESCRIPTION | SERVICE      | TYPE              | LOCATION     | WATER STORAGE | REMARK  |
|                  |                       |              |                   |              | US Gallons    |         |
| 1                | Water Tank            | Water Supply | POLYETHYLENE TANK | Above ground | 50.00         | 1<br>NA |

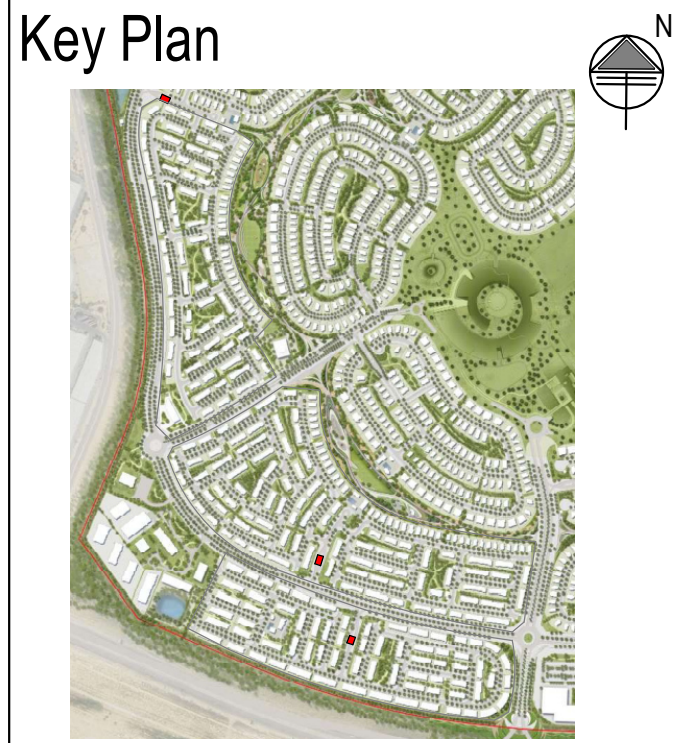

- General Notes :**
- Do not Scale The Drawings. Follow (The MM) Written Dimensions Unless Otherwise Mentioned.
  - Each Drawing Shall be Read in Conjunction With all Other Drawings Specification & the General Standard Details. In Case of Any Discrepancies Bring it to the Knowledge of Engineer and Same to be Resolved Prior to Execution of Work.
  - Dimensions Shown on These Drawings are Structural Dimensions. Unless Noted Otherwise.
  - All Levels Indicated On These Drawings are Levels as per the the Survey Datum, Same Should be Verified at Site Prior to Execution of Work.
  - All Levels Indicated On These Drawings are Based On Design Level, Which is Equivalent to Datum Level and Same Should be Verified at Site Prior to Execution of Work.

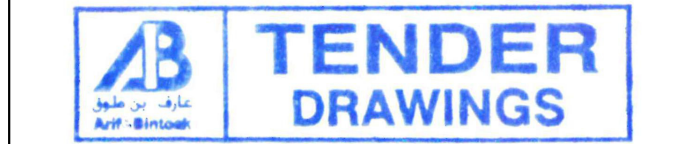

|    |            |     |                             |
|----|------------|-----|-----------------------------|
| 00 | 10/03/2026 | LSG | TENDER SUBMISSION           |
| 00 | 16/01/2026 | LSG | DETAILED DESIGN SUBMISSION  |
| 00 | 31/10/2025 | LSG | SCHEMATIC DESIGN SUBMISSION |
| 00 | 15/10/2025 | IMS | SCHEMATIC SUBMISSION-50%    |
| 00 | 01/09/2025 | LSG | CONCEPT DESIGN SUBMISSION   |

REVISIONS / ISSUE

THIS DRAWING MUST NOT BE REPRODUCED IN WHOLE OR IN PART WITHOUT THE PRIOR APPROVAL OF ARIF & BINTOAK

Status: TENDER SUBMISSION

Client:

EMAAR

Lead Consultant:



Project Title:  
Proposed Residential Townhouses and Standalone Villas  
TH-1, TH-2, and TH-3 at Grand Polo Club & Resort, Dubai, UAE

Discipline: MECHANICAL

Drawing title:  
GUARD HOUSE WATER SUPPLY LAYOUT

|                        |                      |                       |
|------------------------|----------------------|-----------------------|
| Architectural Engineer | Electrical Engineer  | Structural Engineer   |
| MUSTAFA ABID           | MARWAN MOHD.         | RIHAM RAMADAN         |
| Registration # 5847    | Registration # 60102 | Registration # 105092 |

|                     |                     |                     |
|---------------------|---------------------|---------------------|
| Scale(s):<br>1 : 50 | Date:<br>10/03/2026 | Project no:<br>1830 |
|---------------------|---------------------|---------------------|

|                  |                 |                  |
|------------------|-----------------|------------------|
| Drawn by:<br>LSG | Checked:<br>MAV | Approved:<br>MRM |
|------------------|-----------------|------------------|

Drawing Number: GPCR-TH02-AB-DRG-ZZZ-MEC-WS-4405-00