




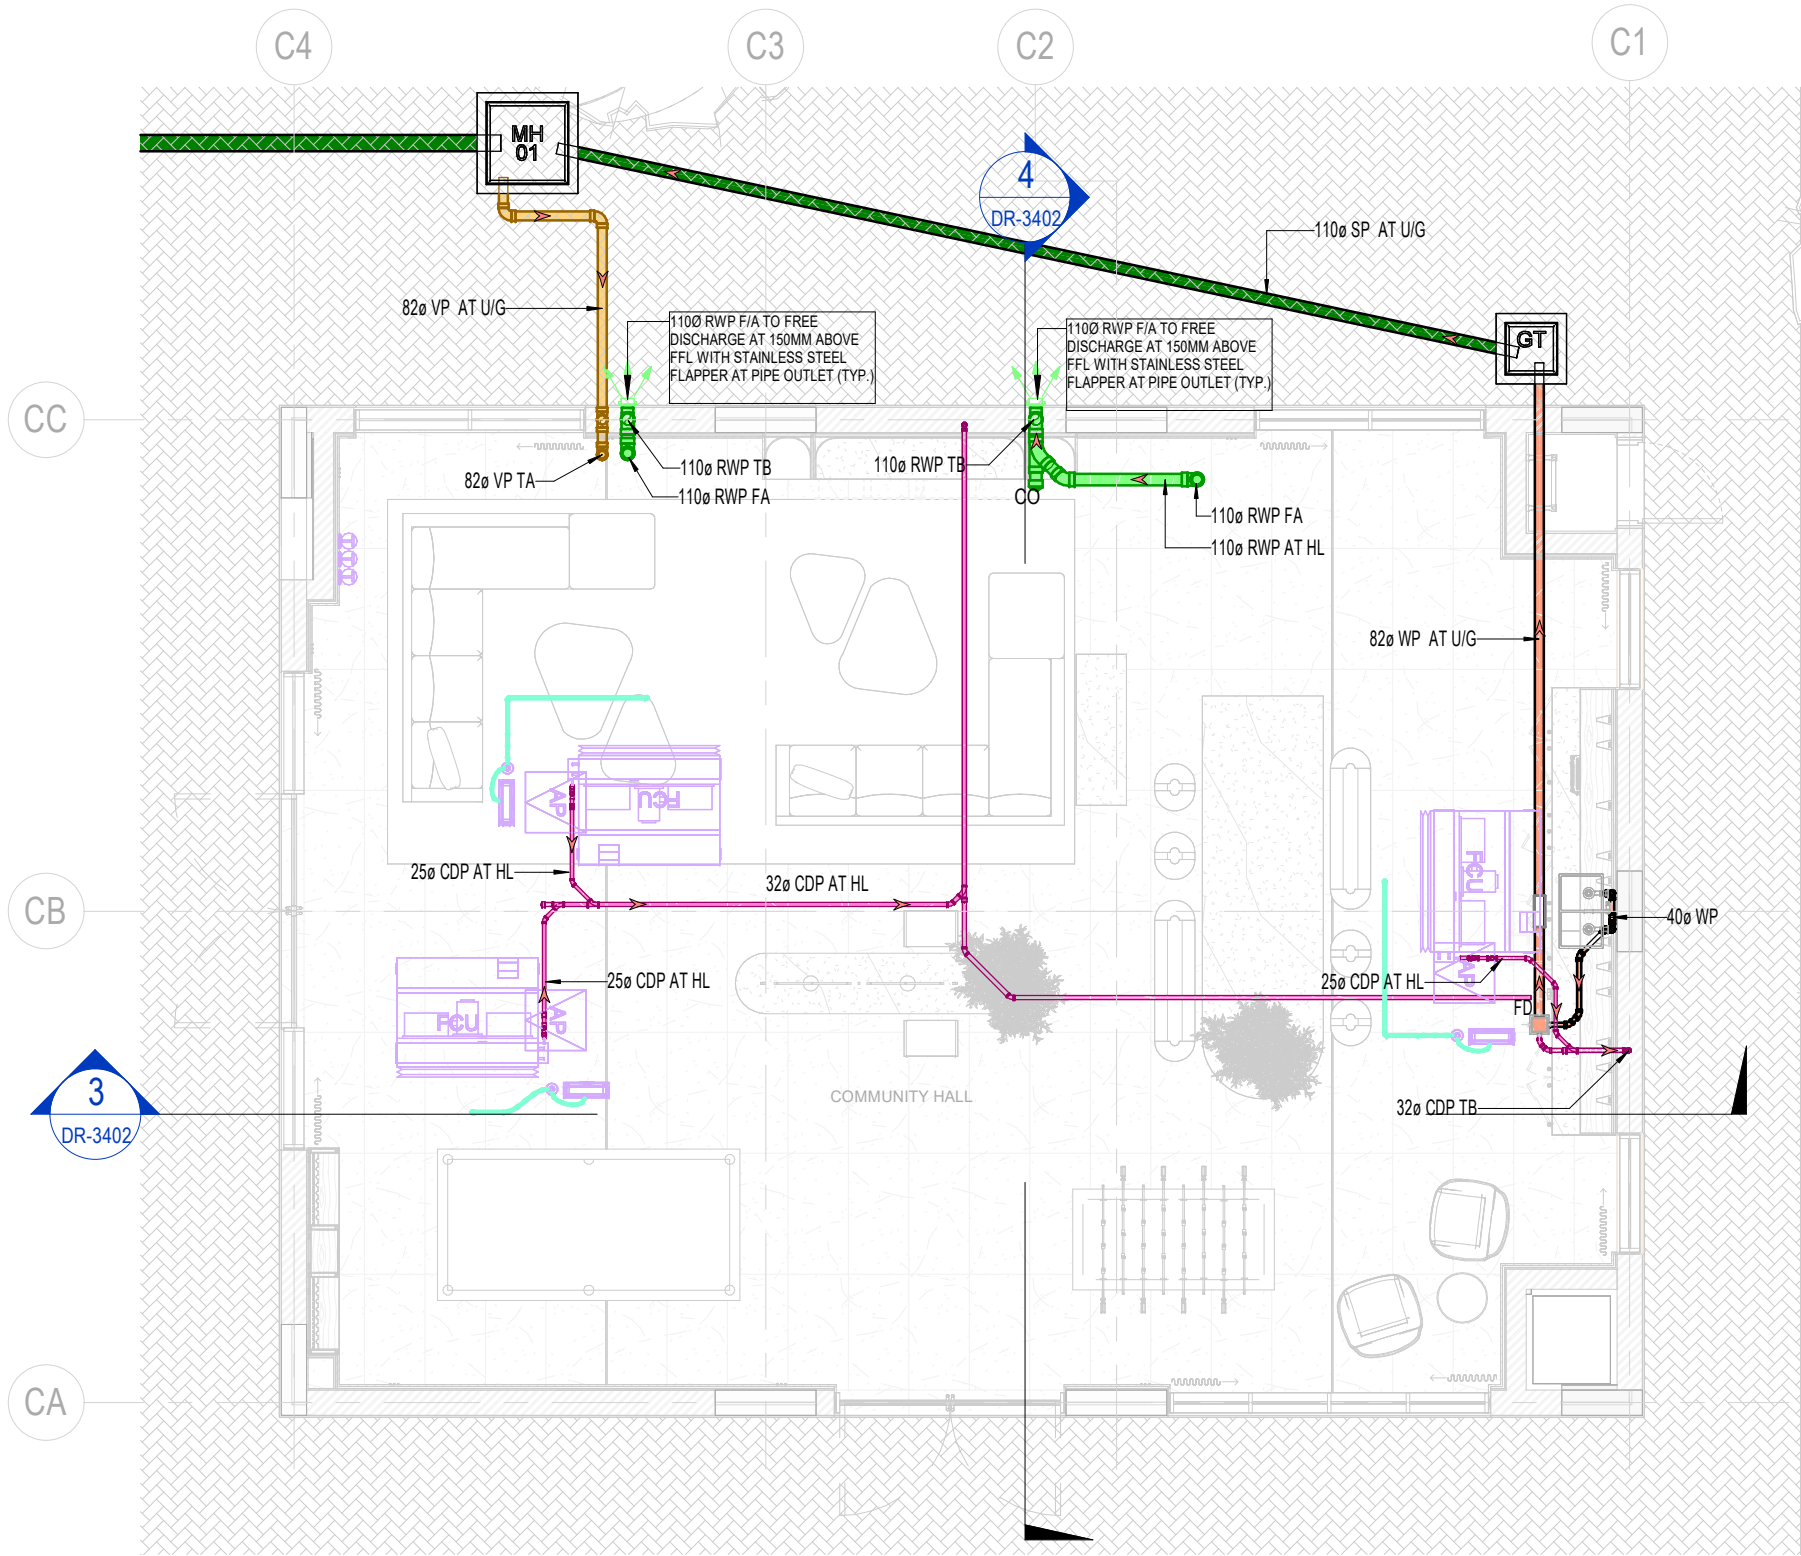


1 GROUND FLOOR DRAINAGE LAYOUT-COMMUNITY HALL
1 : 75

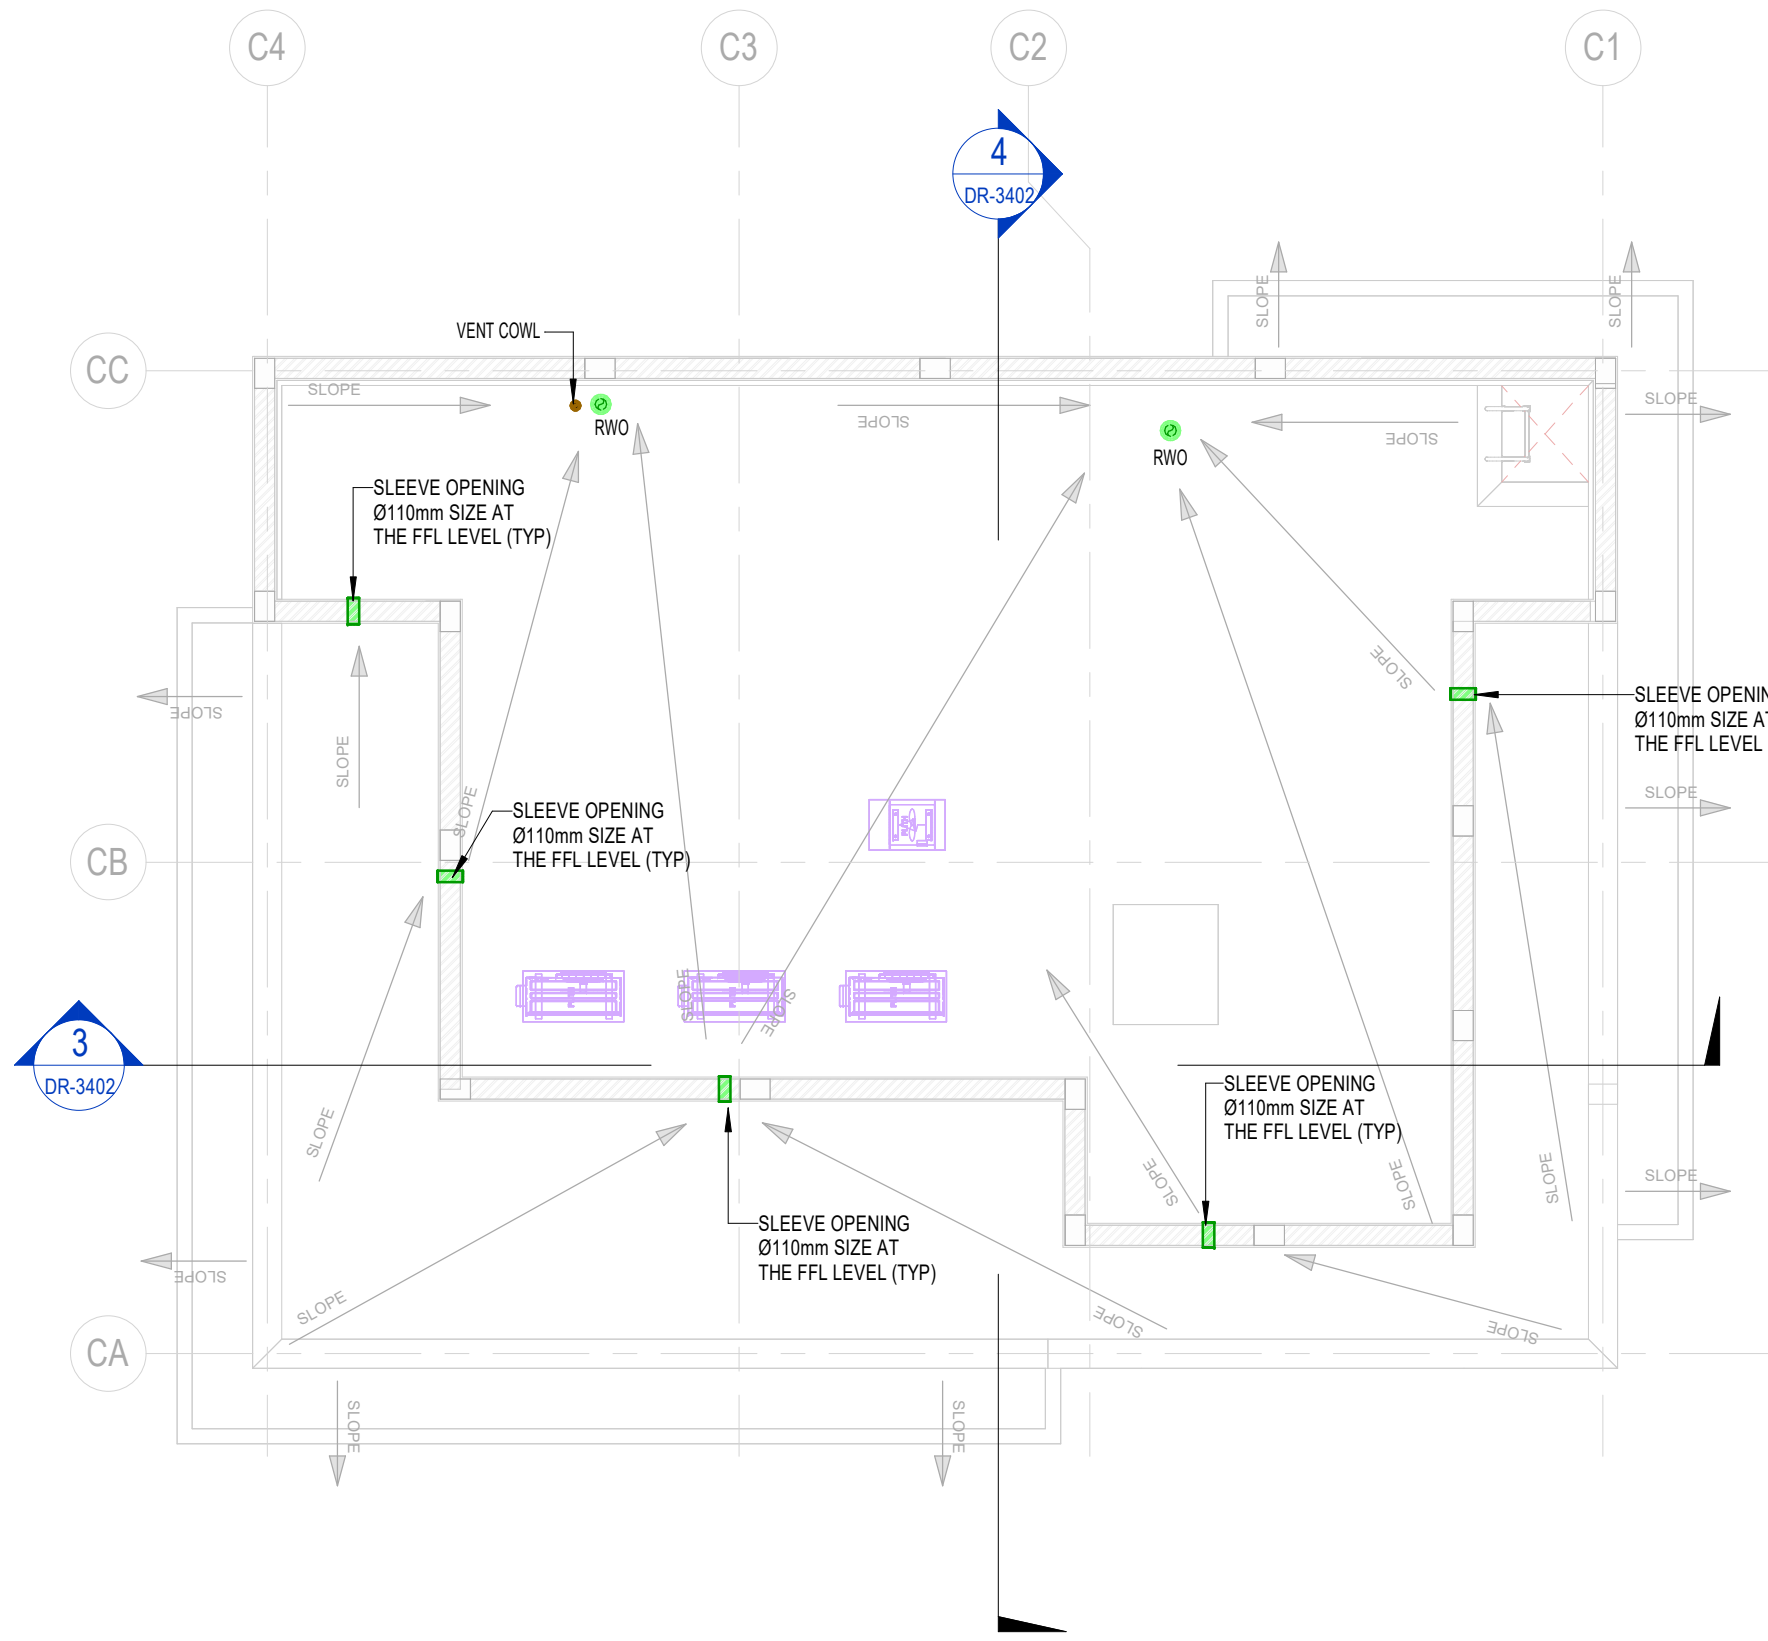


2 ROOF FLOOR DRAINAGE LAYOUT-COMMUNITY HALL
1 : 75

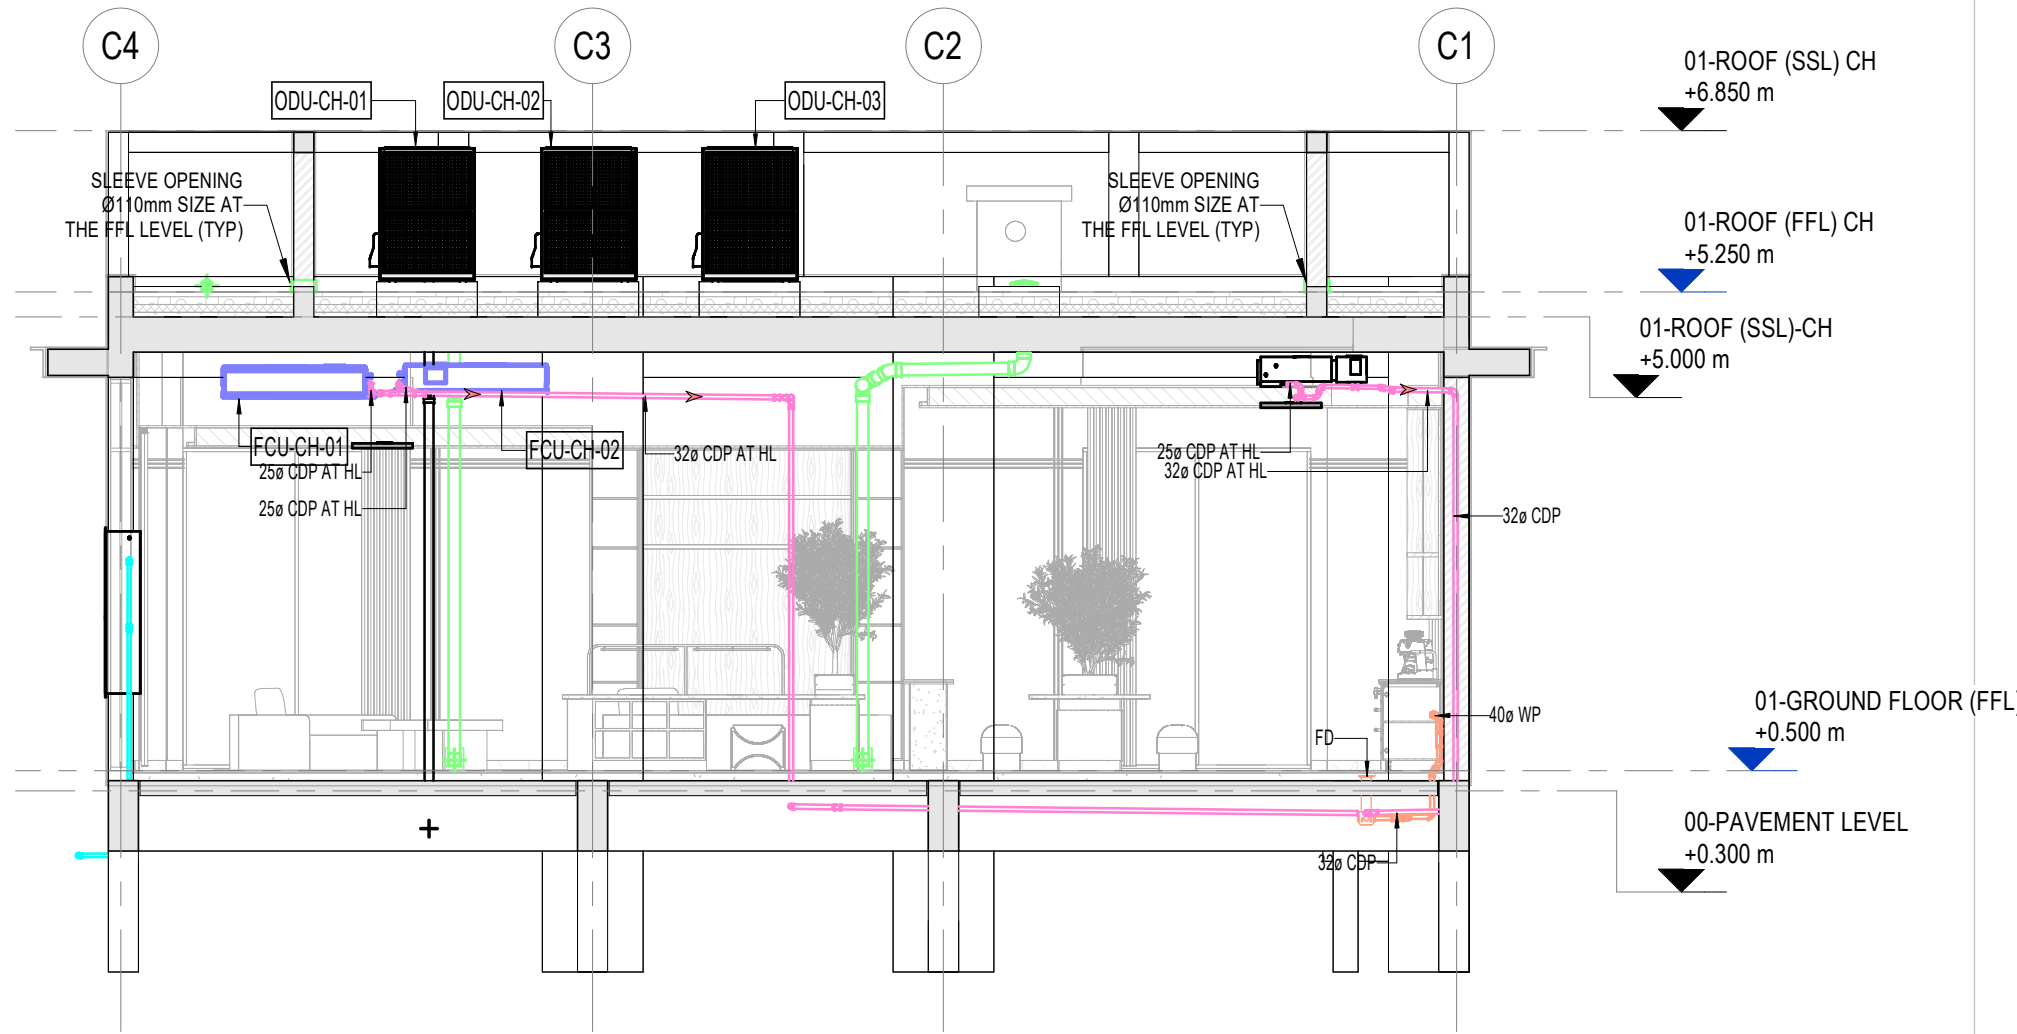

3 COMMUNITY HALL DRAINAGE SECTION 01
1 : 75

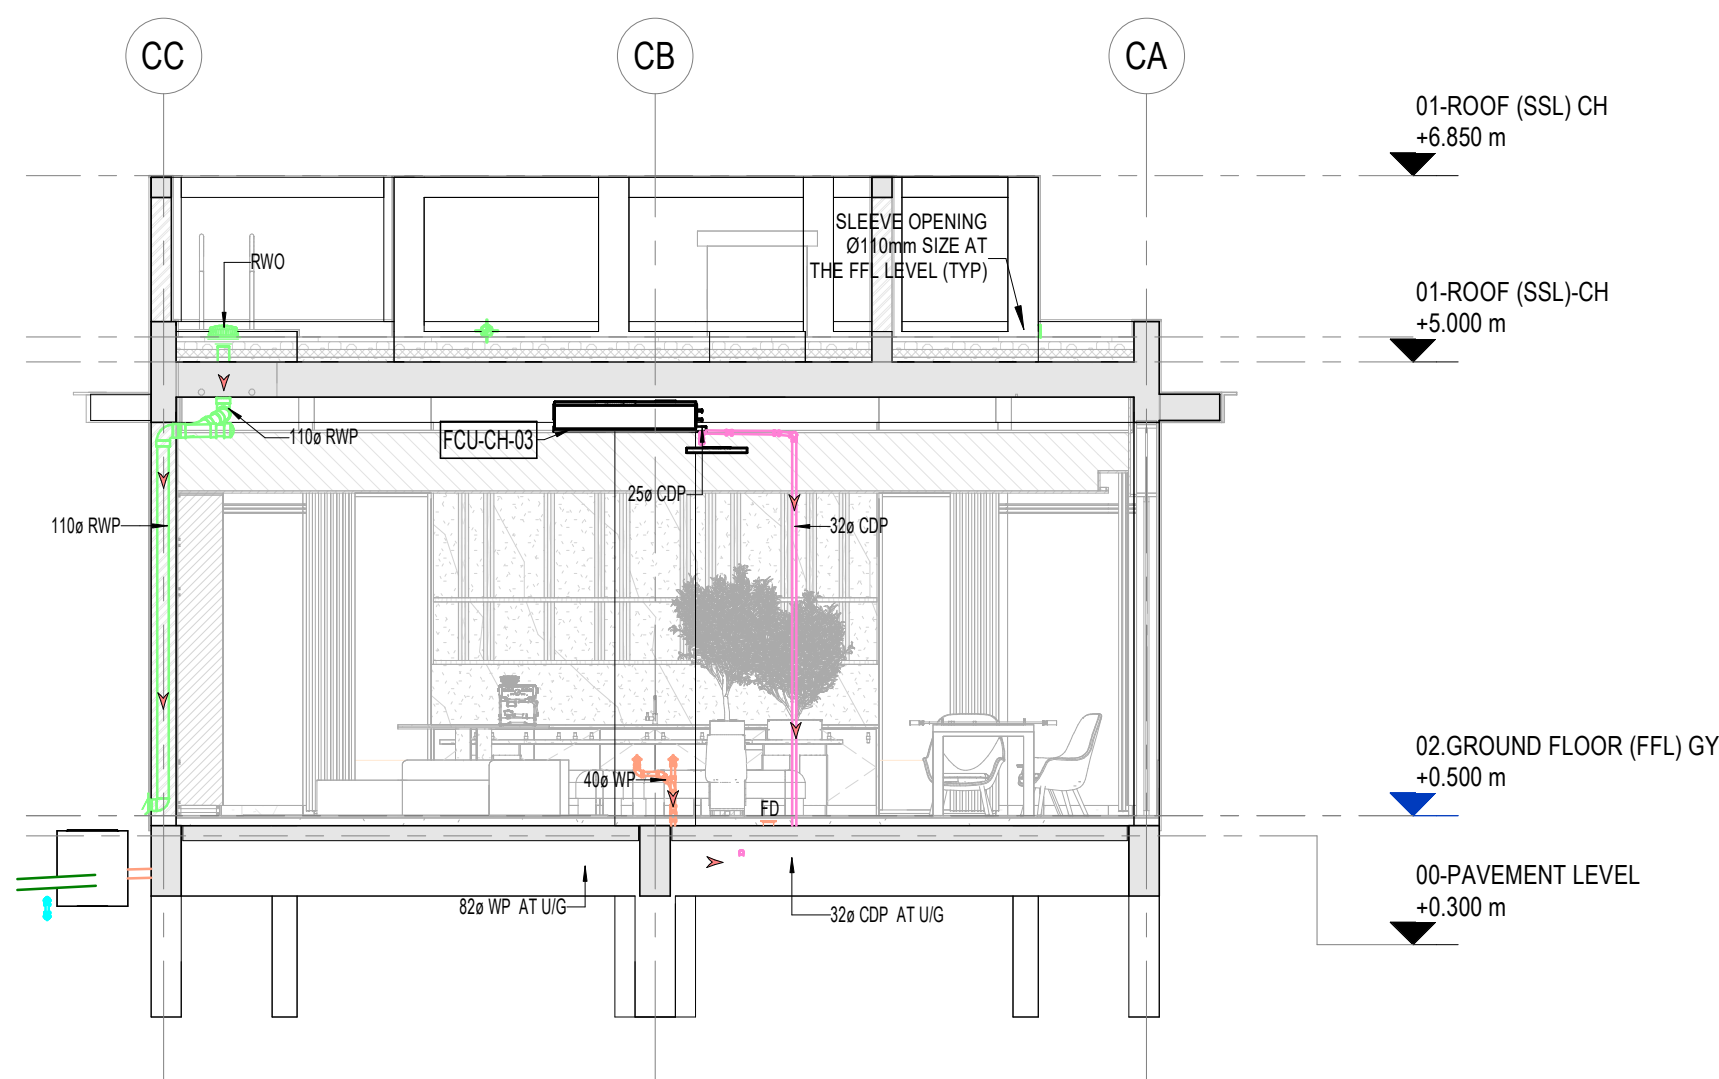


4 COMMUNITY HALL DRAINAGE SECTION 02
1 : 75

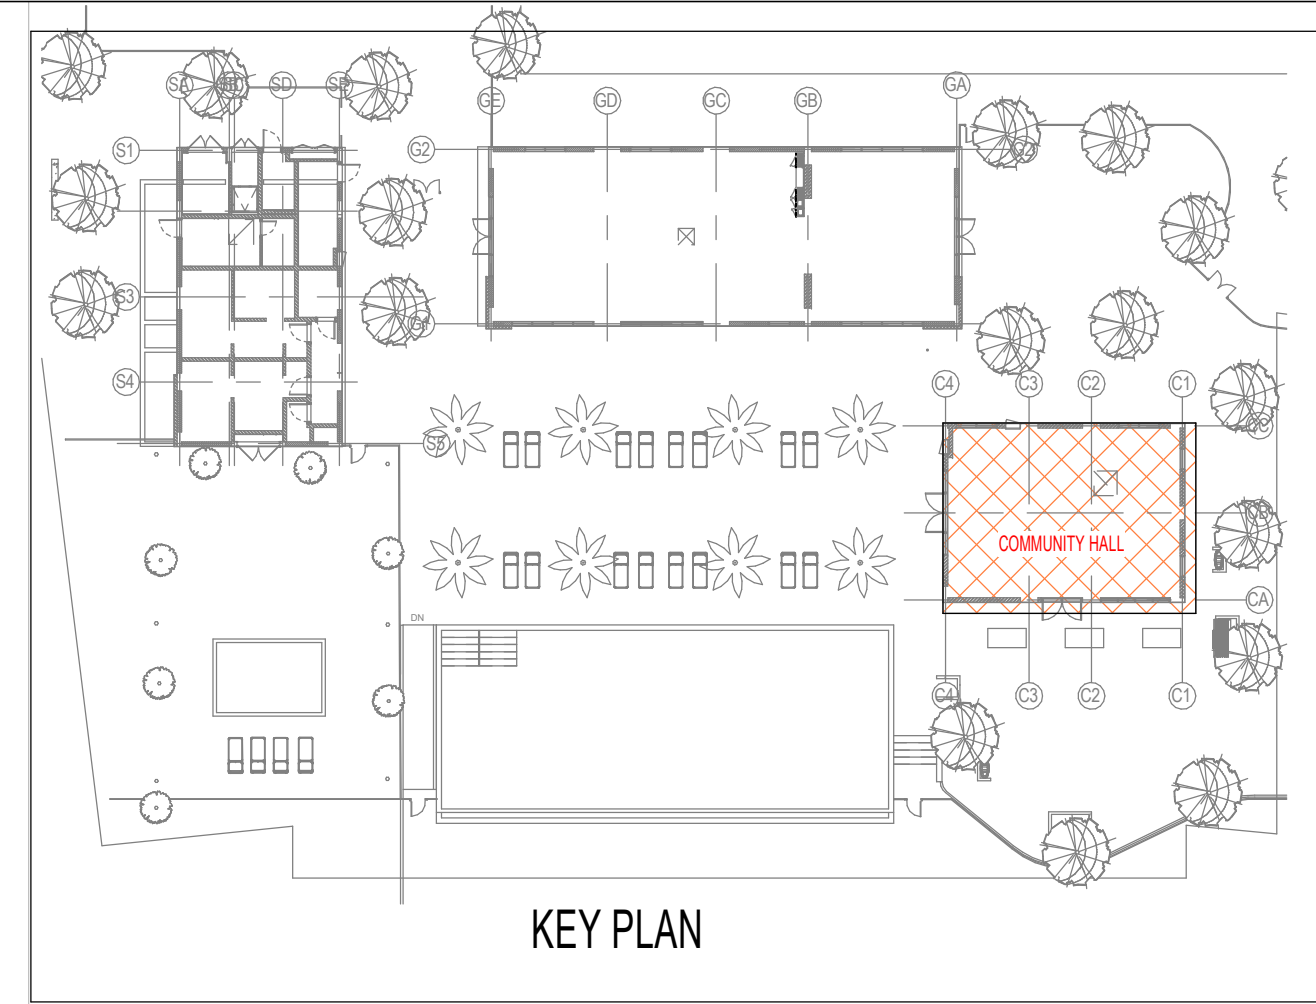

NOTES :-
1. ALL LEVELS, MH & DGT SHOWN IN LAYOUT ARE TENTATIVE FINAL SIZES & DEPTH TO BE COORDINATED BY CONTRACTOR AS PER SITE CONDITION.
2. VENT PIPE CONNECTION SHALL BE PROVIDED AS PER AUTHORITY REGULATIONS.
3. CONTRACTOR SHALL DO THE NECESSARY EXTERNAL CONNECTION TO A MA. 10m OUTSIDE THE VILLA PLOT BOUNDARY.
4. ALL MANHOLES WITH IN THE VILLA PLOT PAVED /HANDSCAPED AREAS BE RECESSED TYPE, AND LEVEL SHALL BE COORDINATED WITH THE FINISHES ON SITE AS PER ARCHITECT DRAWINGS


NOTES:-	
• ALL DIMENSIONS ARE IN MILLIMETERS UNLESS OTHERWISE SPECIFIED	
• ALL SERVICES OUTLETS ON THIS DRAWINGS ARE INDICATIVE ONLY. THE CONTRACTOR SHALL PREPARE DETAILED SHOP DRAWINGS AFTER COORDINATING PRIOR TO EXECUTION OF WORK.	
LEGEND	
	SOIL PIPE (SP)
	WASTE PIPE (WP)
	VENT PIPE (VP)
	RAIN WATER PIPE (RWP)
	CONDENSATE DRAIN PIPE (CDP)
	PALINTER DRAIN PIPE (PDP)
	PRESSURE PIPE (HPP)
MH	MANHOLE
GT	GULLY TRAP
SD	SHOWER DRAIN
FD	FLOOR DRAIN
CB	CATCH BASIN
PBMH	PRESSURE BREAKING MANHOLE
ST	SAND TRAP
PDO	PLANTER DRAIN OUTLET
RWO	RAIN WATER OUTLET
FCO	FLOOR CLEAN OUT
CO	CLEAN OUT
F/A	FROM ABOVE
F/B	FROM BELOW
T/A	TO ABOVE
T/B	TO BELOW
H/L	HIGH LEVEL
L/L	LOW LEVEL
DTLL	DROP TO LOW LEVEL

Key Plan

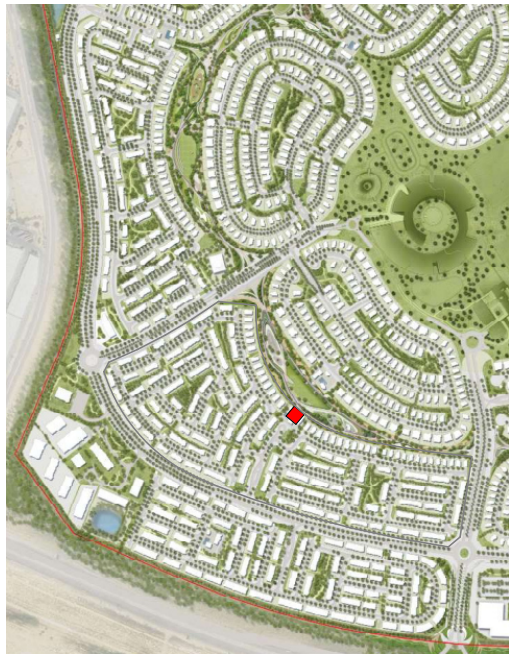

General Notes :

- Do not Scale The Drawings. Follow (The MM) Written Dimensions Unless Otherwise Mentioned.
- Each Drawing Shall be Read in Conjunction With all Other Drawings Specification & the General Standard Details. In Case of Any Discrepancies Bring it to the Knowledge of Engineer and Same to be Resolved Prior to Execution of Work.
- Dimensions Shown on These Drawings are Structural Dimensions. Unless Noted Otherwise.
- All Levels Indicated On These Drawings are Levels as per the Survey Datum, Same Should be Verified at Site Prior to Execution of Work.
- All Levels Indicated On These Drawings are Based On Design Level, Which is Equivalent to Datum Level and Same Should be Verified at Site Prior to Execution of Work.

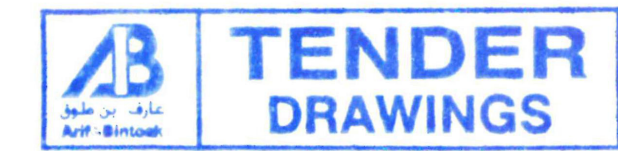

No.	Date	Initials	Description
00	10/03/2024	LSG	TENDER SUBMISSION
00	16/01/2026	LSG	DETAILED DESIGN SUBMISSION
00	31/10/2025	LSG	SCHEMATIC DESIGN SUBMISSION
00	15/10/2025	LSG	SCHEMATIC SUBMISSION-50%
00	01/09/2025	LSG	CONCEPT DESIGN SUBMISSION

REVISIONS / ISSUE

THIS DRAWING MUST NOT BE REPRODUCED IN WHOLE OR IN PART WITHOUT THE PRIOR APPROVAL OF ARIF & BINTOAK

TENDER SUBMISSION

Client
EMAAR

Lead Consultant
Arif & Bintook
consulting architects & engineers
POST BOX 5070 DUBAI, UAE TEL: 04-3372886 FAX: 04-3372832
POST BOX 5081 ABU DHABI, UAE TEL: 02-4566666

Project Title:
Proposed Residential Townhouses
and Standalone Villas
TH-1, TH-2, and TH-3 at Grand Polo
Club & Resort, Dubai, UAE

Discipline : **MECHANICAL**

Drawing title:
**COMMUNITY HALL
GROUND & ROOF FLOOR
DRAINAGE LAYOUT**

Architectural Engineer	Electrical Engineer	Structural Engineer
MUSTAFA ABID	MARWAN MOHD.	RIHAM RAMADAN
Registration # 5847	Registration # 80102	Registration # 105892
Scale(s): As indicated	Date: 10/03/2026	Project no: 1857
Drawn by: LSG	Checked: MAV	Approved: MRM

Drawing Number : **GPCR-TH02-AB-DRG-ZZZ-MEC-DR-3402-00**