
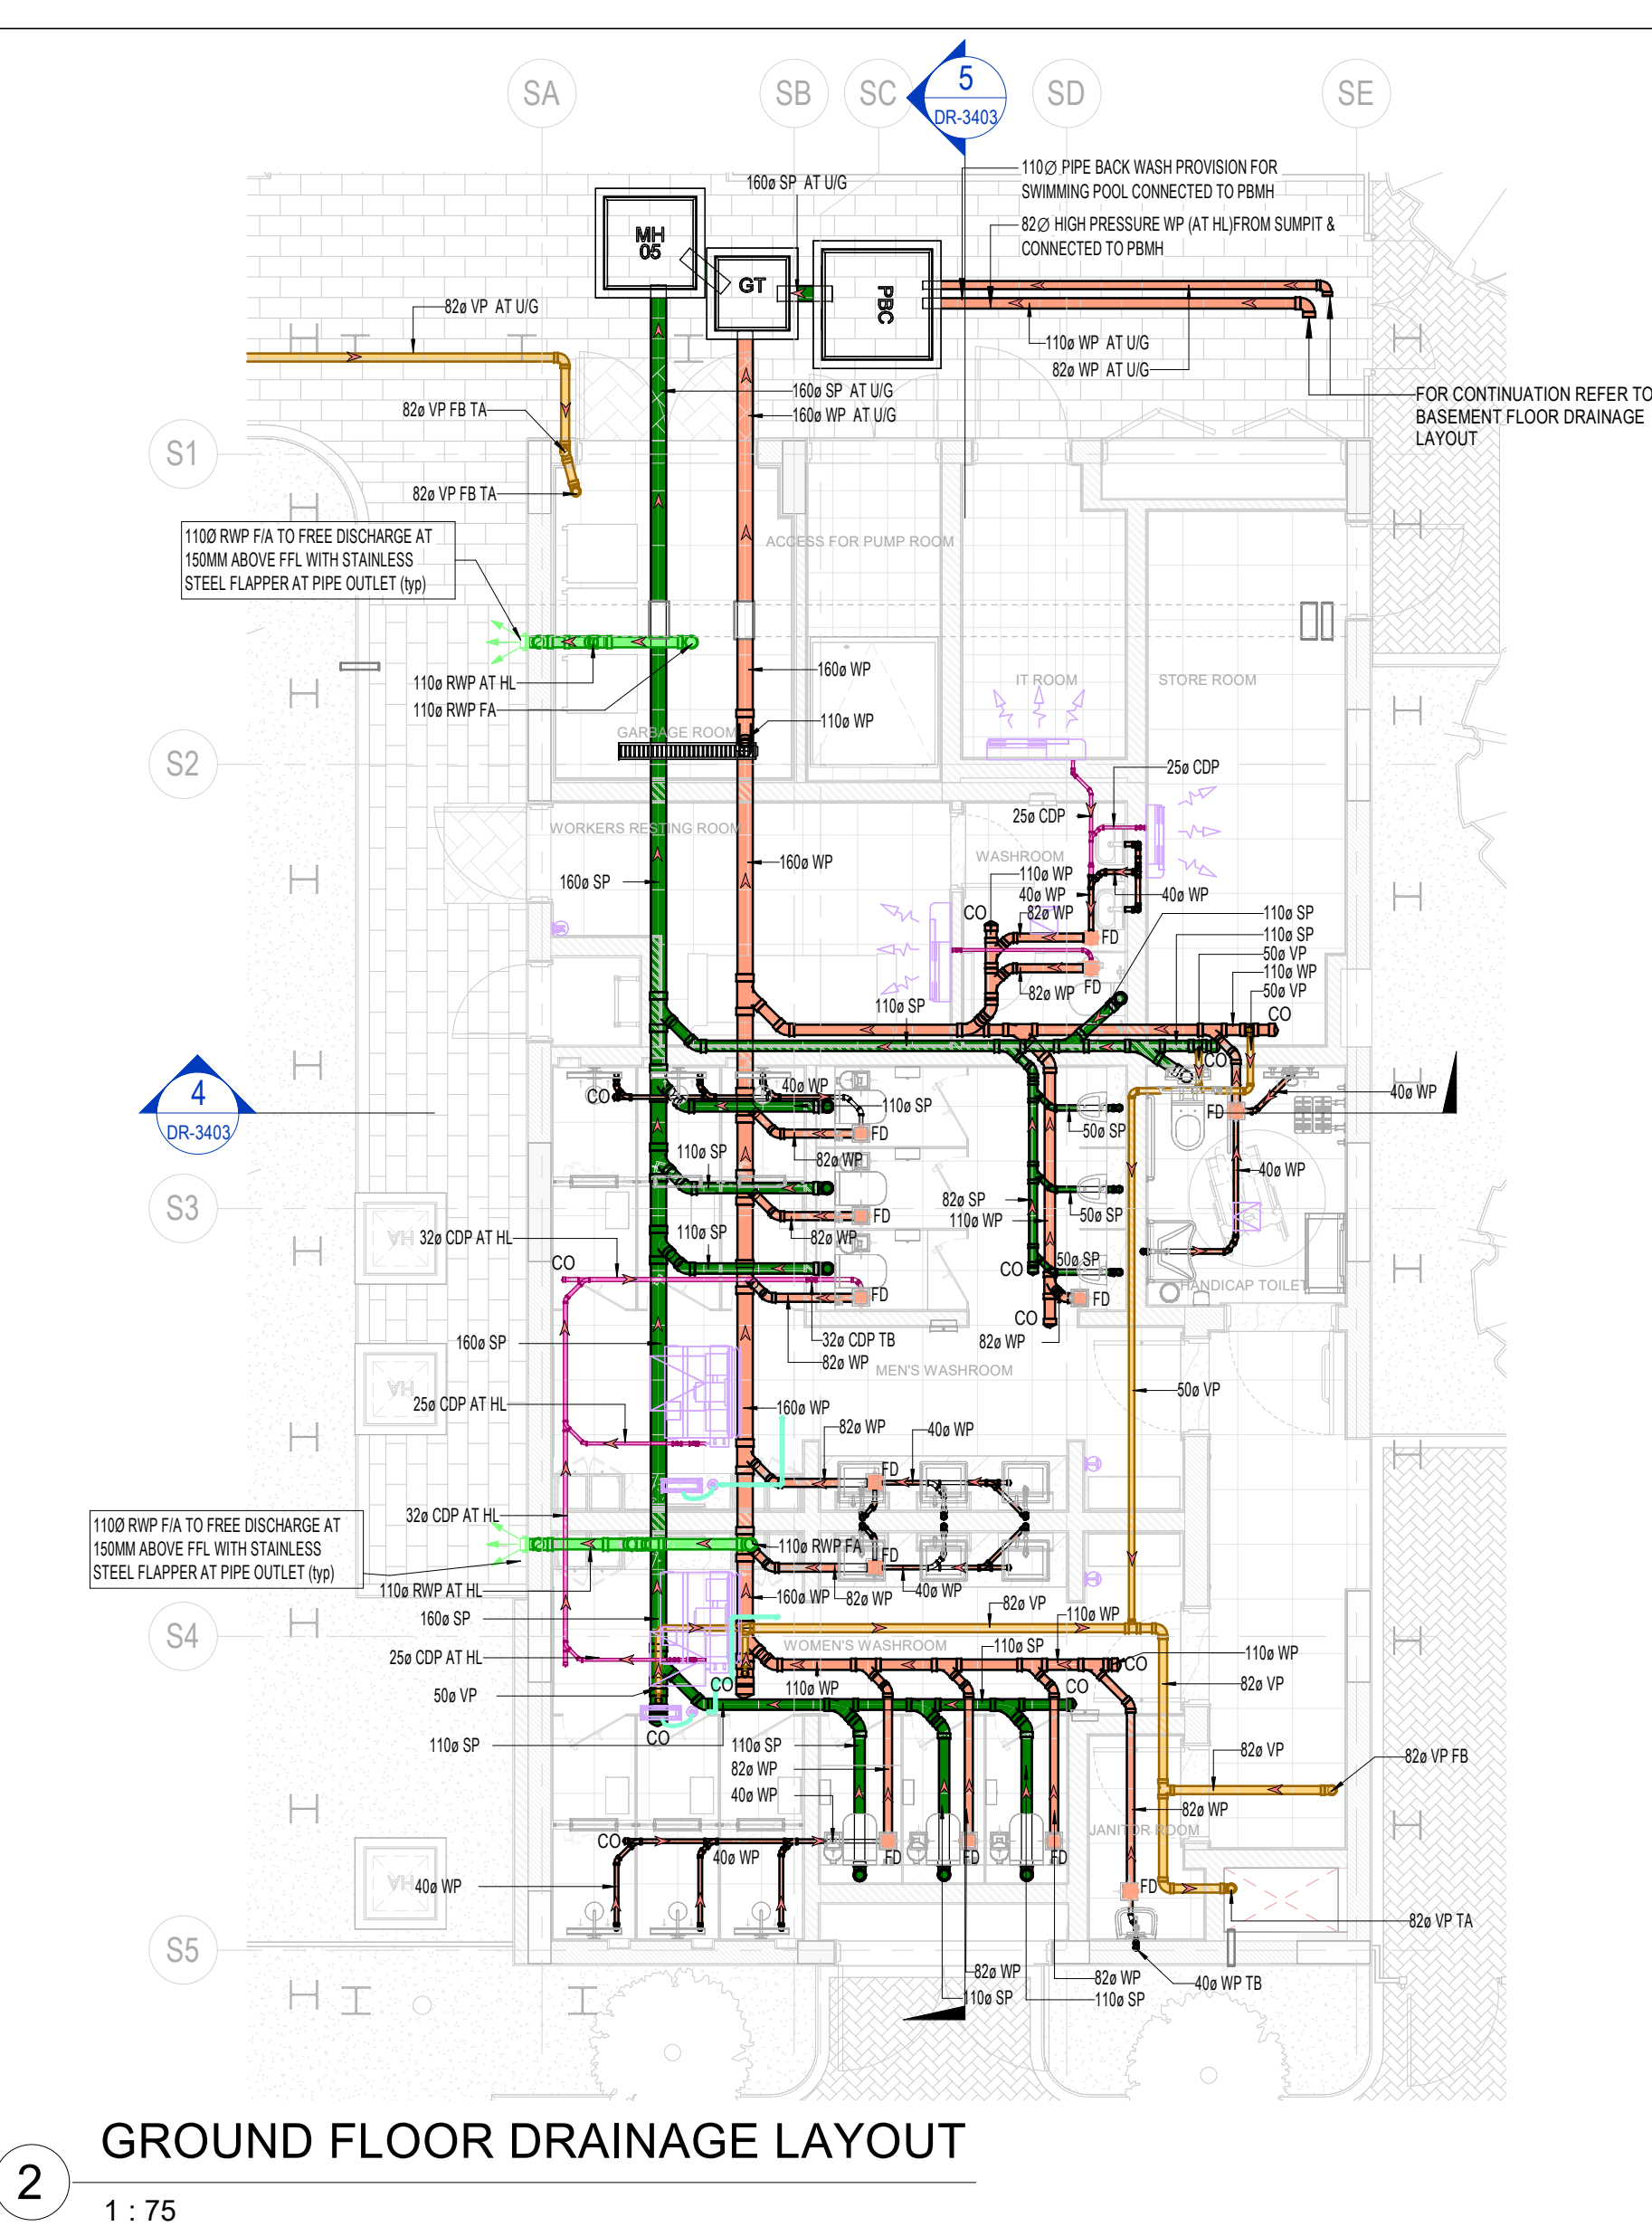


This 2D drawing is extracted from 3D BIM Model

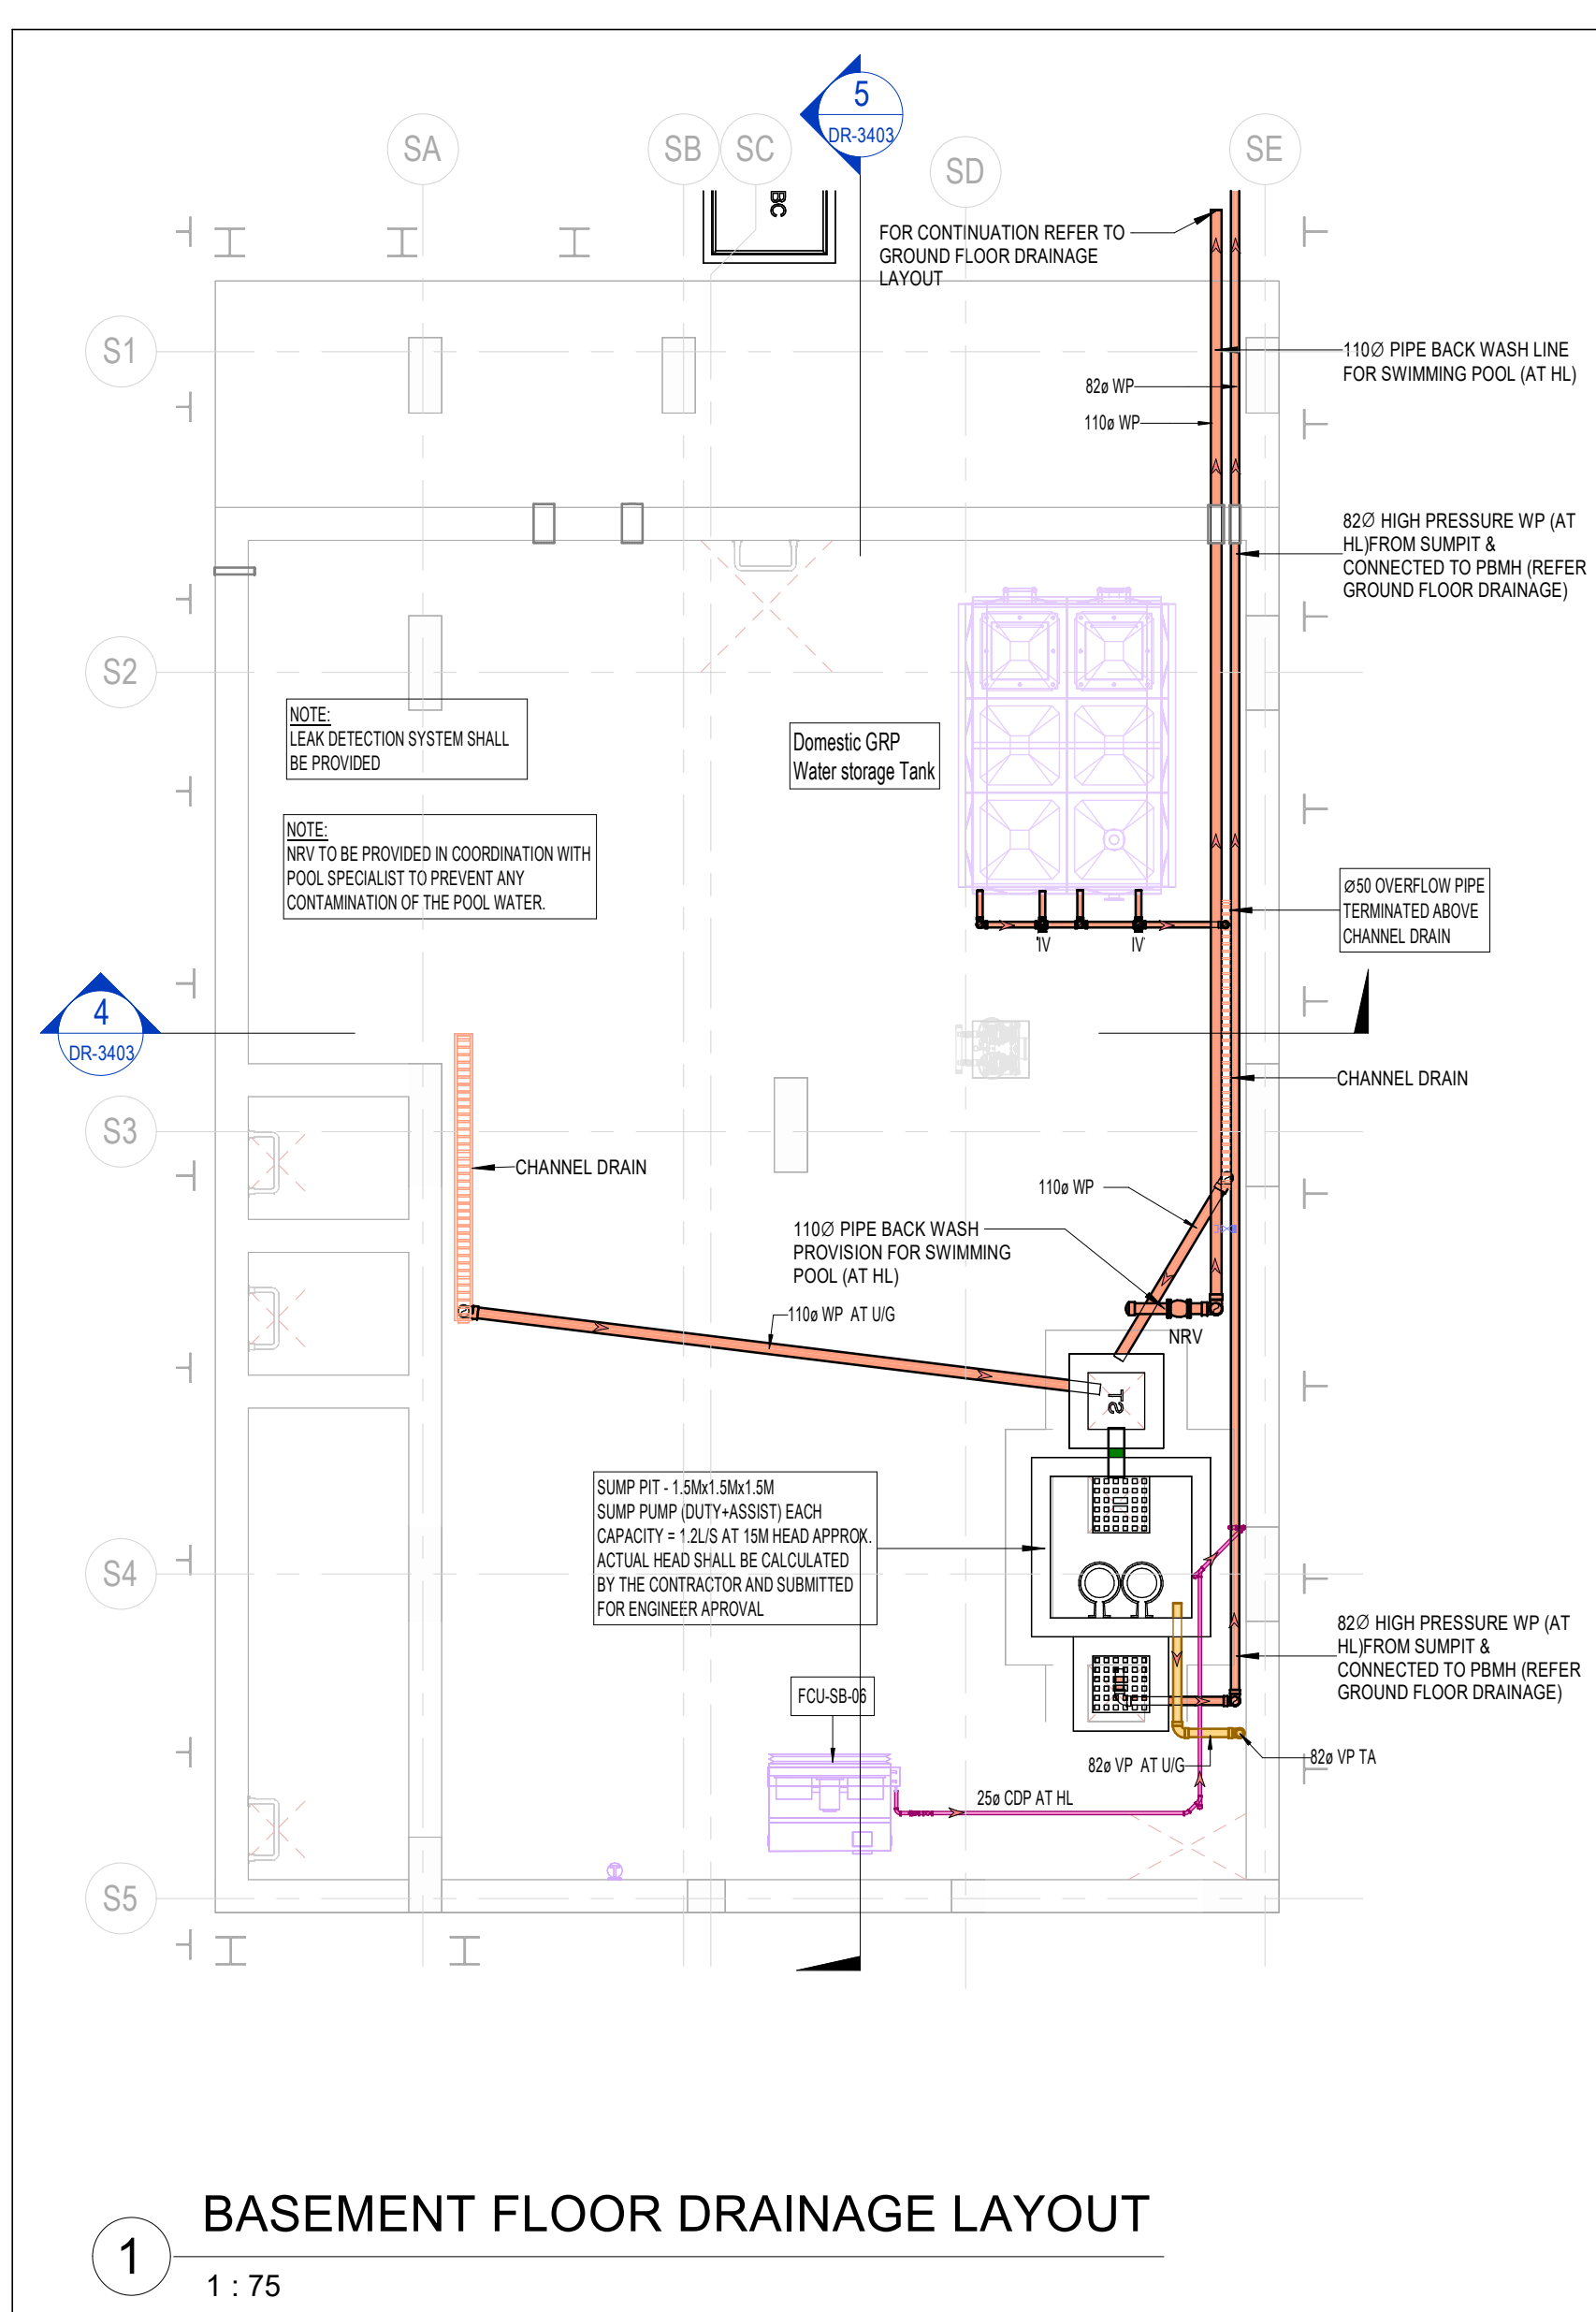


NOTES:-

- ALL DIMENSIONS ARE IN MILLIMETERS UNLESS OTHERWISE SPECIFIED
- ALL SERVICES OUTLETS ON THIS DRAWINGS ARE INDICATIVE ONLY. THE CONTRACTOR SHALL PREPARE DETAILED SHOP DRAWINGS AFTER COORDINATING PRIOR TO EXECUTION OF WORK.

LEGEND



—	SOIL PIPE (SP)
—	WASTE PIPE (WP)
—	VENT PIPE (VP)
—	RAIN WATER PIPE (RWP)
—	CONDENSATE DRAIN PIPE (CDP)
—	PALNTER DRAIN PIPE (PDP)
—	PRESSURE PIPE (HPP)
MH	MANHOLE
GT	GULLY TRAP
SD	SHOWER DRAIN
FD	FLOOR DRAIN
CB	CATCH BASIN
PBMH	PRESSURE BREAKING MANHOLE
ST	SAND TRAP
PDO	PLANTER DRAIN OUTLET
RWO	RAIN WATER OUTLET
FCO	FLOOR CLEAN OUT
CO	CLEAN OUT
F/A	FROM ABOVE
F/B	FROM BELOW
T/A	TO ABOVE
T/B	TO BELOW
H/L	HIGH LEVEL
L/L	LOW LEVEL
DTLL	DROP TO LOW LEVEL

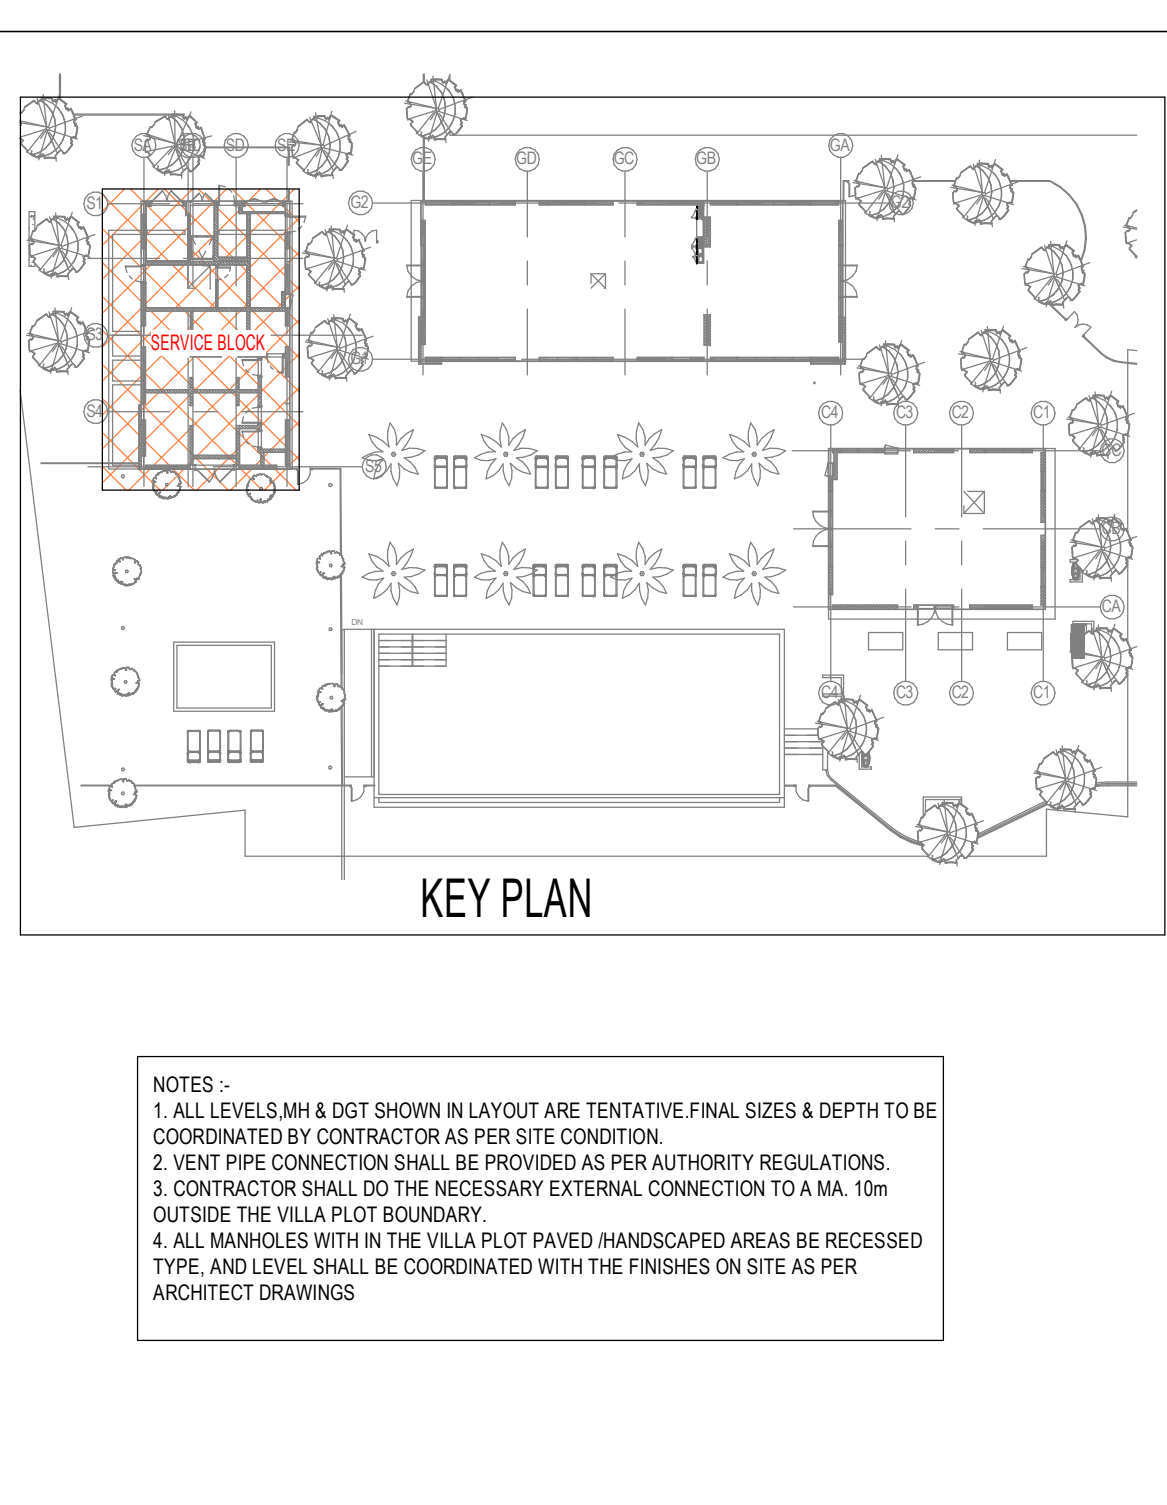

Key Plan

General Notes :

- Do not Scale The Drawings. Follow (The MM) Written Dimensions Unless Otherwise Mentioned.
- Each Drawing Shall be Read in Conjunction With all Other Drawings Specification & the General Standard Details. In Case of Any Discrepancies Bring it to the Knowledge of Engineer and Same to be Resolved Prior to Execution of Work.
- Dimensions Shown on These Drawings are Structural Dimensions. Unless Noted Otherwise.
- All Levels Indicated On These Drawings are Levels as per the the Survey Datum, Same Should be Verified at Site Prior to Execution of Work.
- All Levels Indicated On These Drawings are Based On Design Level, Which is Equivalent to Datum Level and Same Should be Verified at Site Prior to Execution of Work.

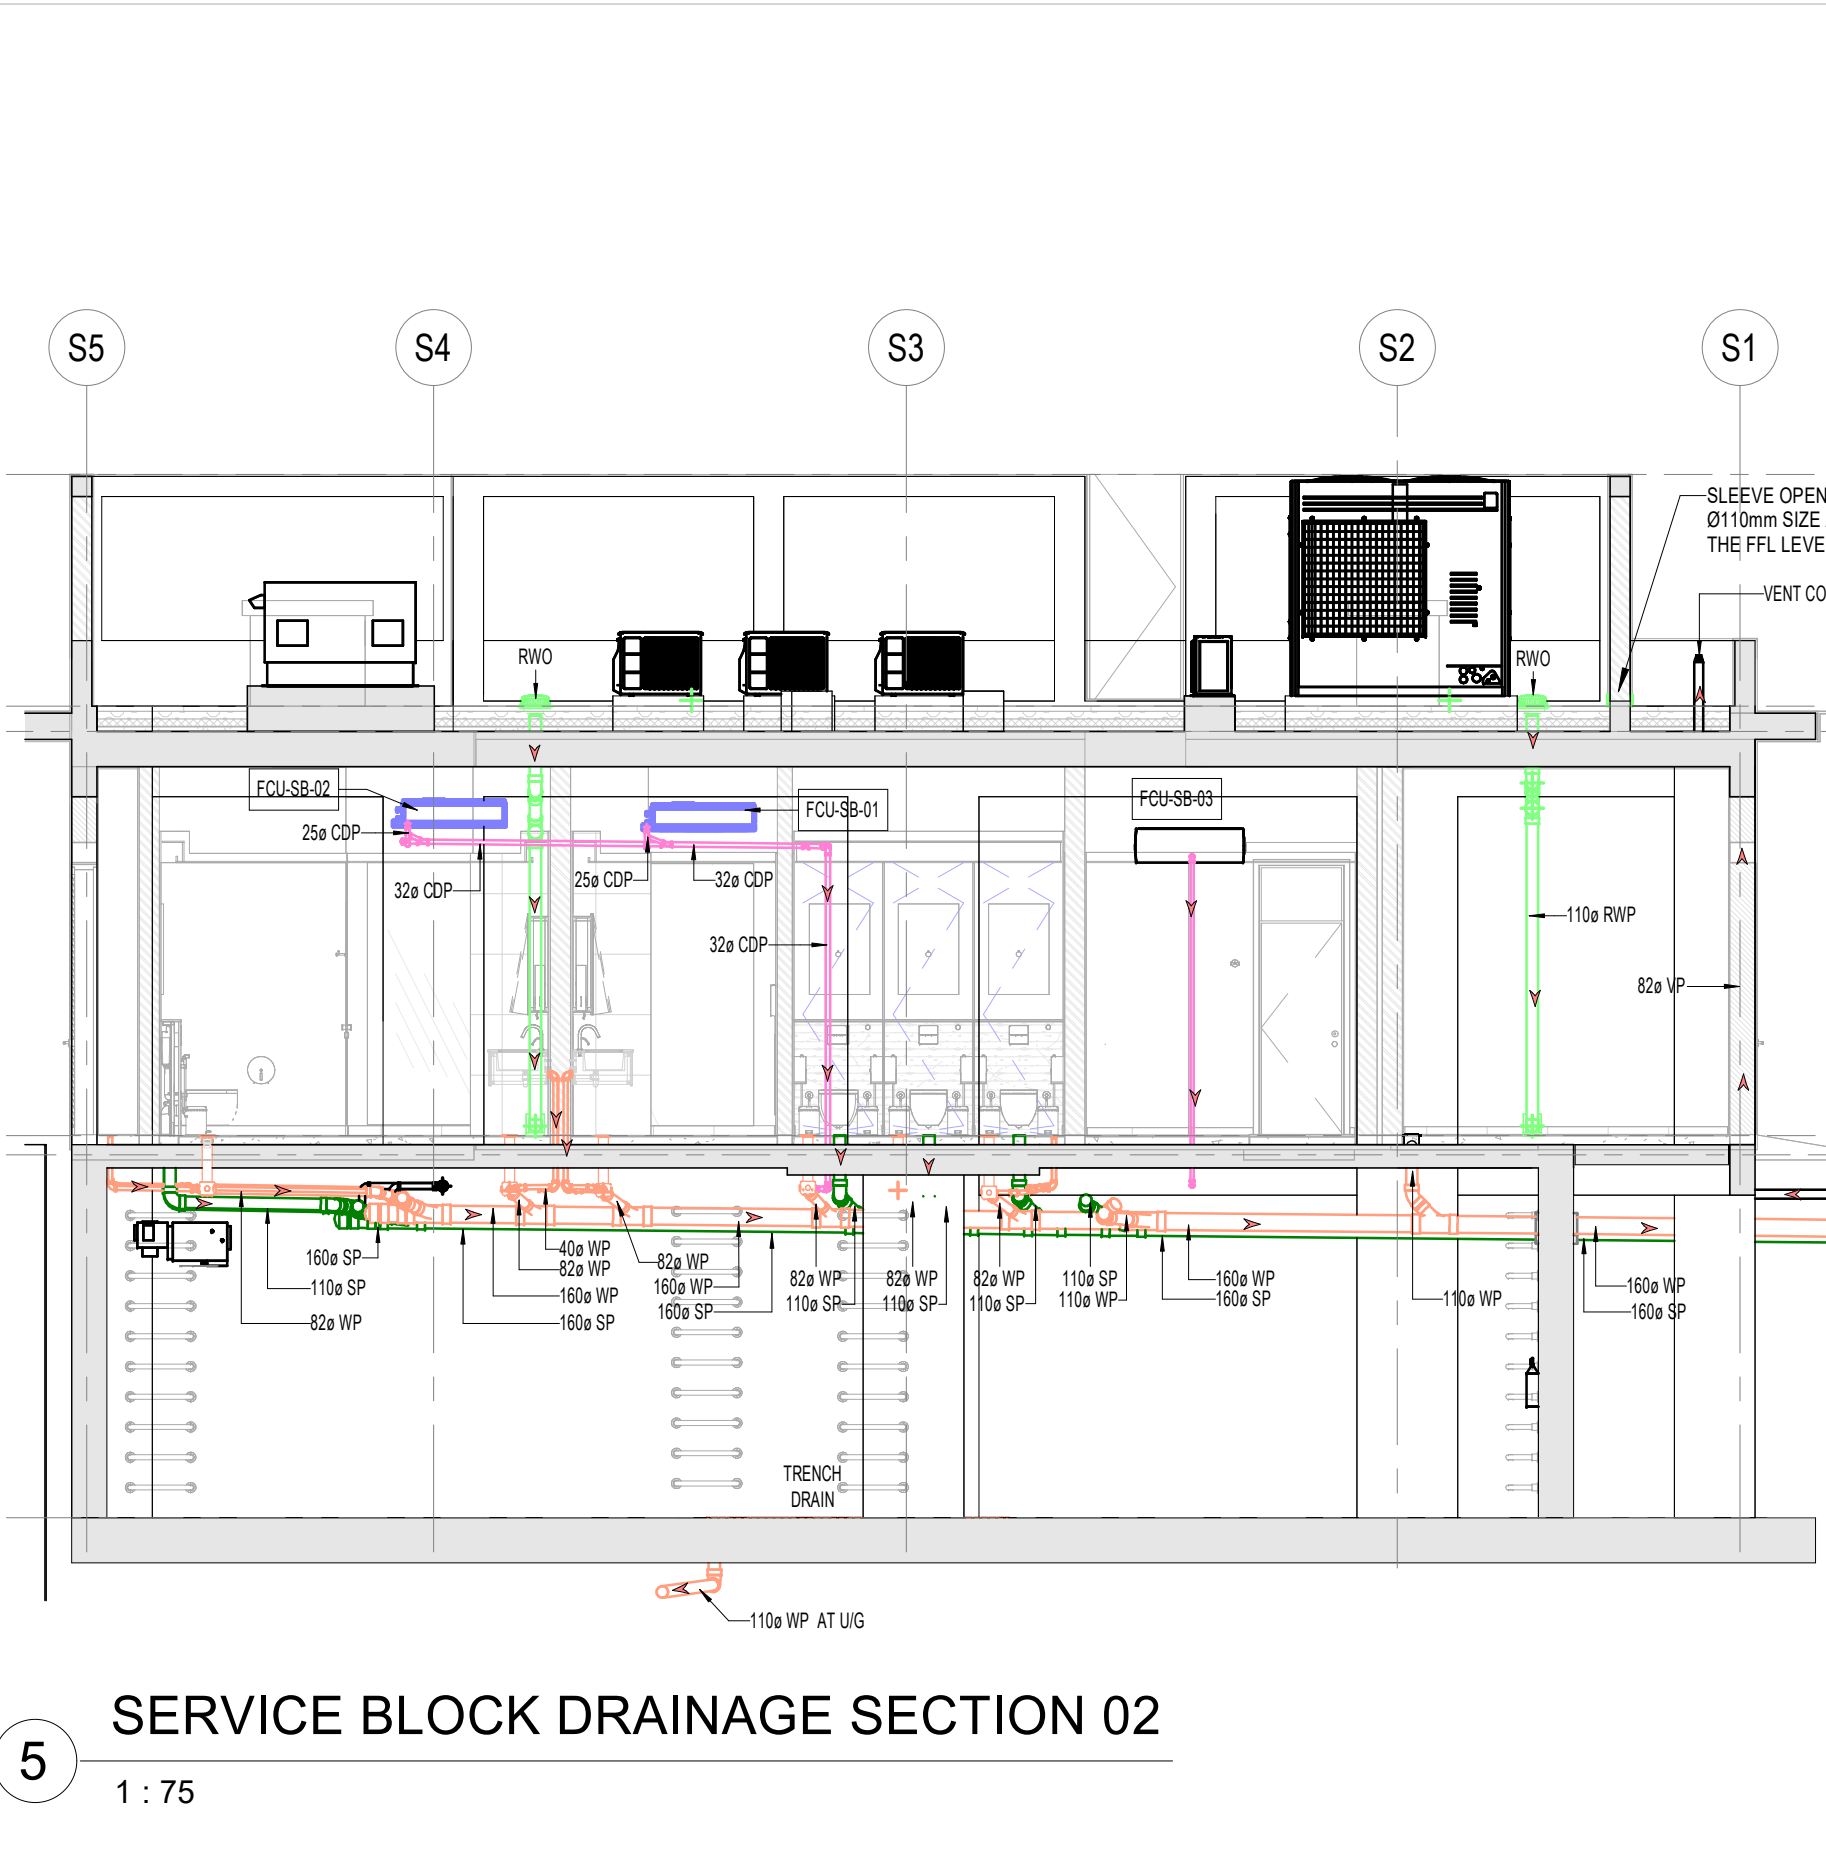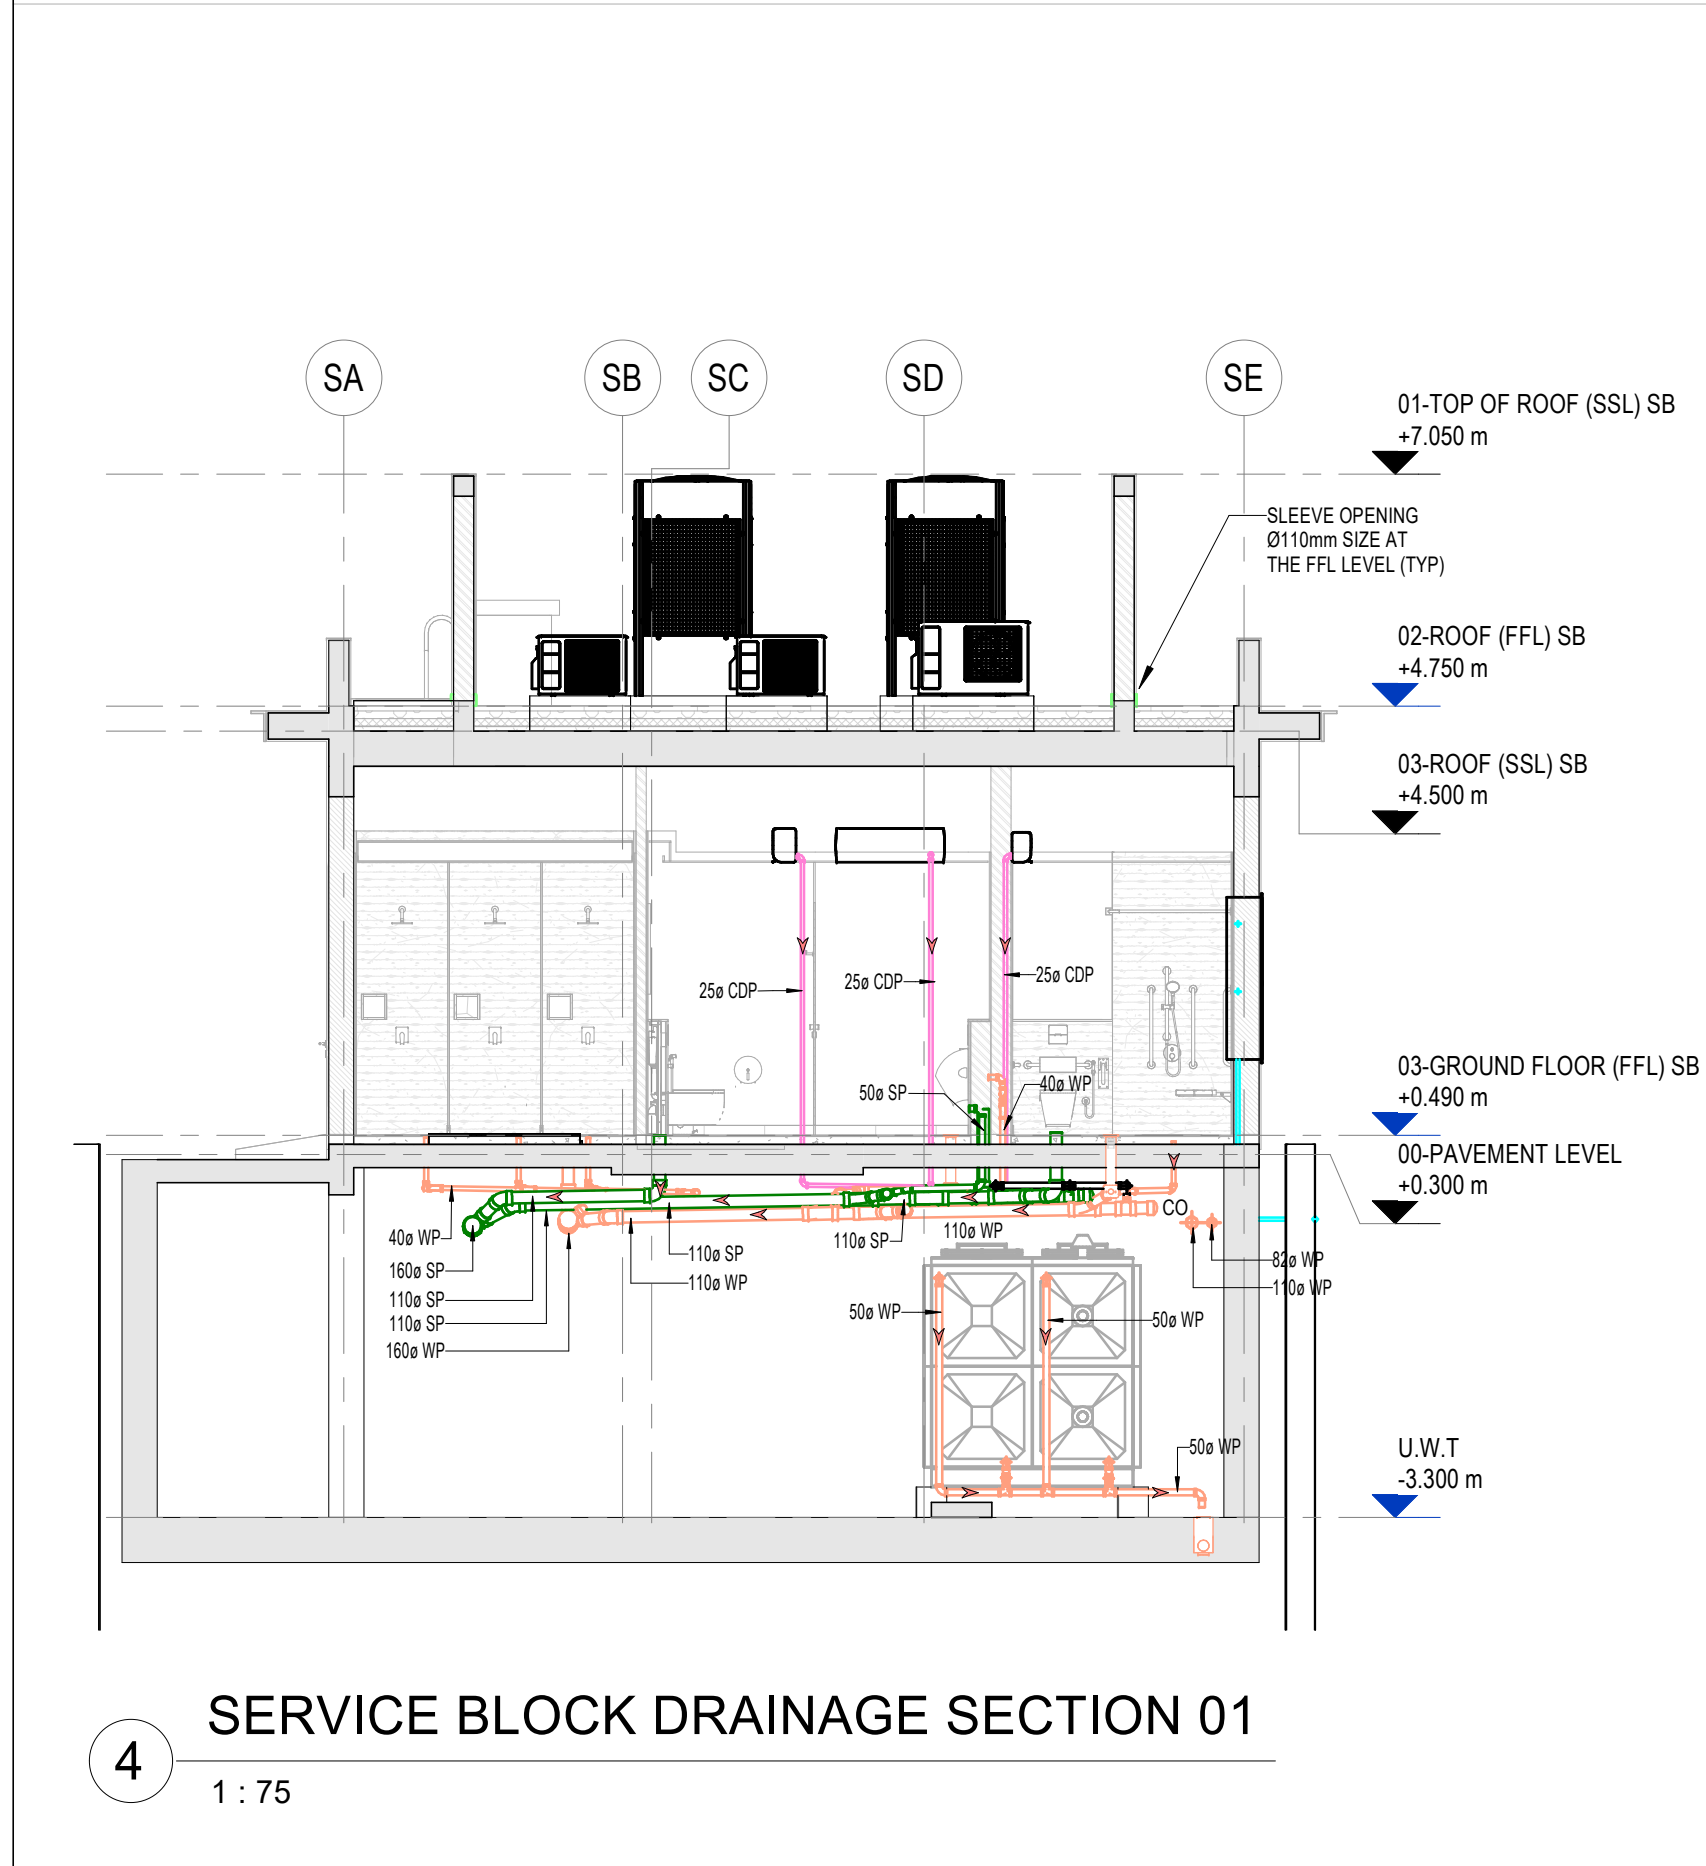


NOTES:-

- ALL DIMENSIONS ARE IN MILLIMETERS UNLESS OTHERWISE SPECIFIED
- ALL SERVICES OUTLETS ON THIS DRAWINGS ARE INDICATIVE ONLY. THE CONTRACTOR SHALL PREPARE DETAILED SHOP DRAWINGS AFTER COORDINATING PRIOR TO EXECUTION OF WORK.

LEGEND

—	SOIL PIPE (SP)
—	WASTE PIPE (WP)
—	VENT PIPE (VP)
—	RAIN WATER PIPE (RWP)
—	CONDENSATE DRAIN PIPE (CDP)
—	PALNTER DRAIN PIPE (PDP)
—	PRESSURE PIPE (HPP)
MH	MANHOLE
GT	GULLY TRAP
SD	SHOWER DRAIN
FD	FLOOR DRAIN
CB	CATCH BASIN
PBMH	PRESSURE BREAKING MANHOLE
ST	SAND TRAP
PDO	PLANTER DRAIN OUTLET
RWO	RAIN WATER OUTLET
FCO	FLOOR CLEAN OUT
CO	CLEAN OUT
F/A	FROM ABOVE
F/B	FROM BELOW
T/A	TO ABOVE
T/B	TO BELOW
H/L	HIGH LEVEL
L/L	LOW LEVEL
DTLL	DROP TO LOW LEVEL

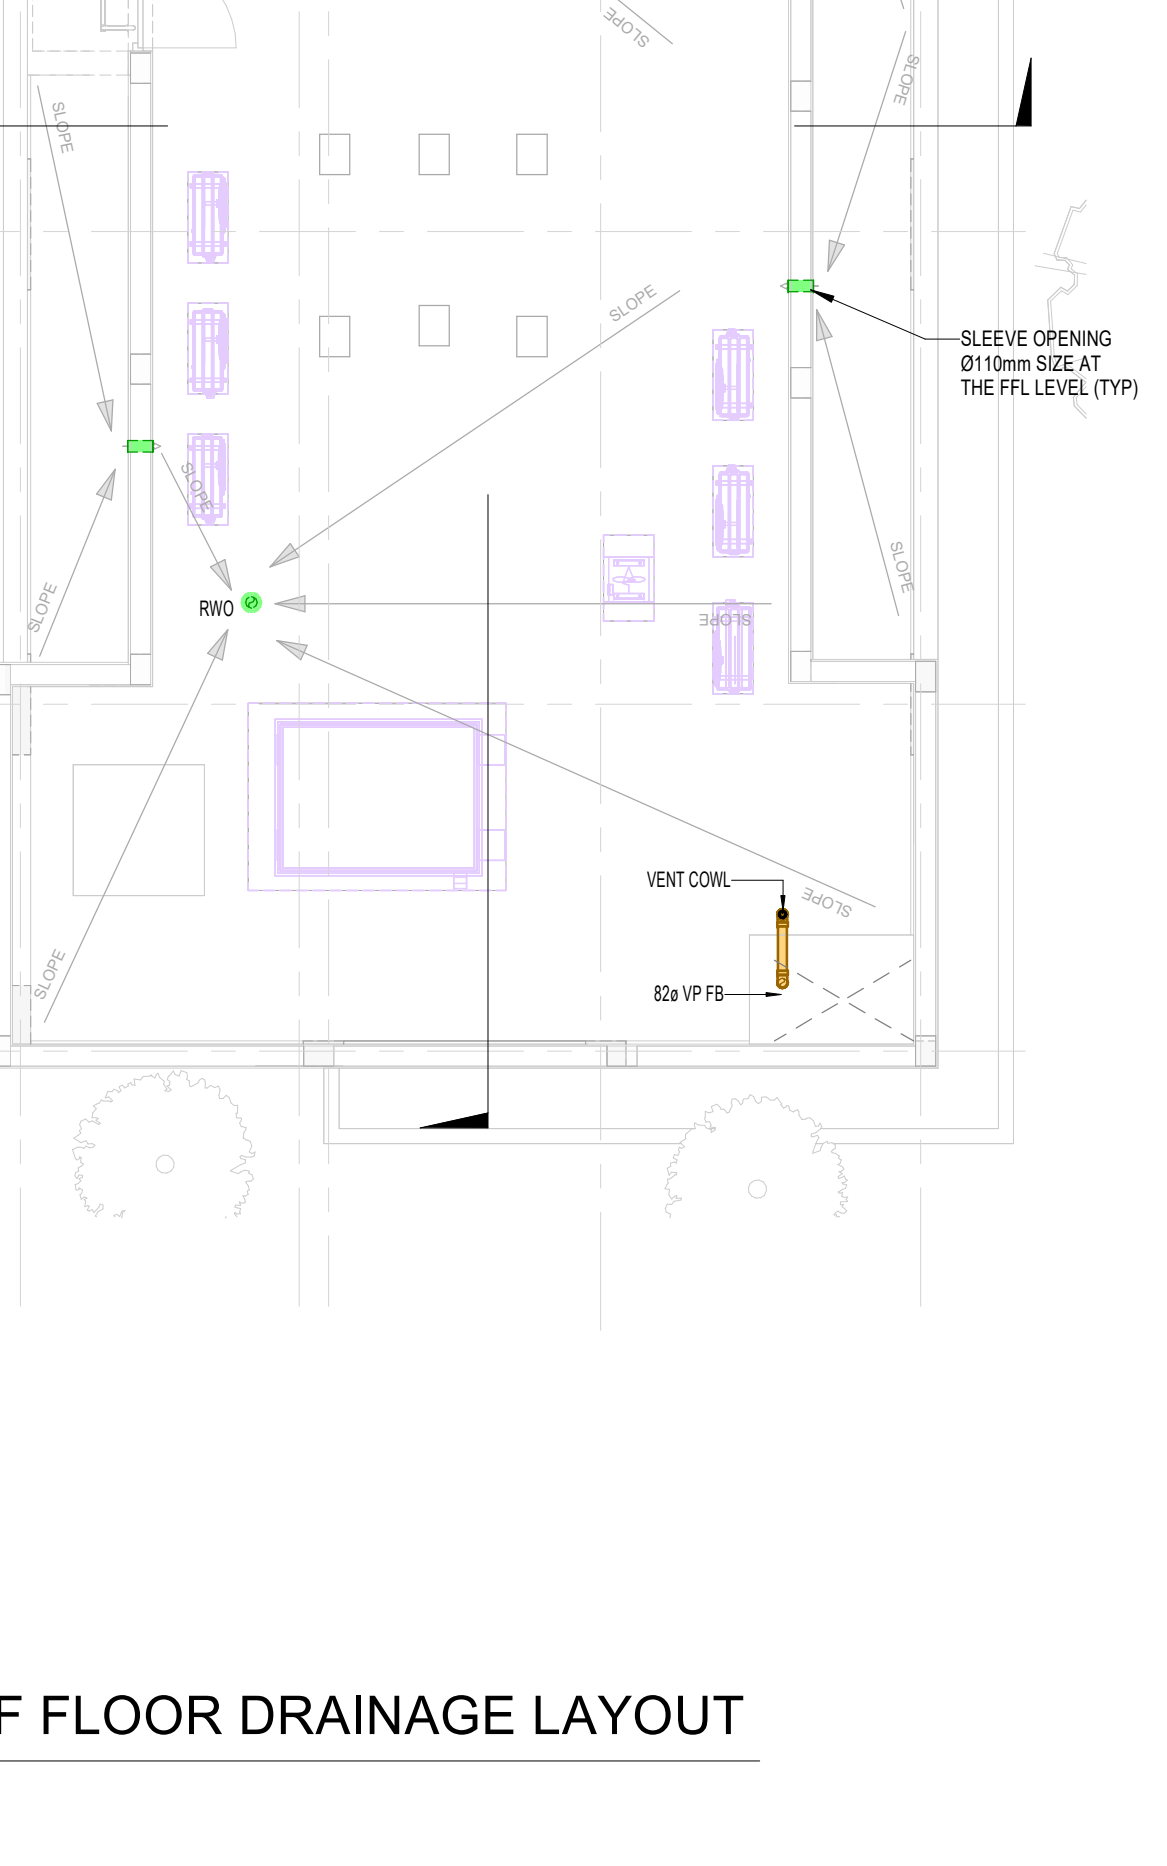

TENDER SUBMISSION

EMAAR

Lead Consultant

Arif & Bintok
consulting architects & engineers

Project Title:
Proposed Residential Townhouses and Standalone Villas
TH-1, TH-2, and TH-3 at Grand Polo Club & Resort, Dubai, UAE

Discipline: **MECHANICAL**

Drawing title:
SERVICE BLOCK BASEMENT, GROUND & ROOF FLOOR DRAINAGE LAYOUT

Architectural Engineer	Electrical Engineer	Structural Engineer
MUSTAFA ABID	MARWAN MOHD.	RIHAM RAMADAN
Registration # 5847	Registration # 60102	Registration # 106092
Scale(s): As indicated	Date: 10/03/2026	Project no: 1857
Drawn by: LSG	Checked: MAV	Approved: MRM

Drawing Number: GPCR-TH02-AB-DRG-ZZZ-MEC-DR-3403-00