




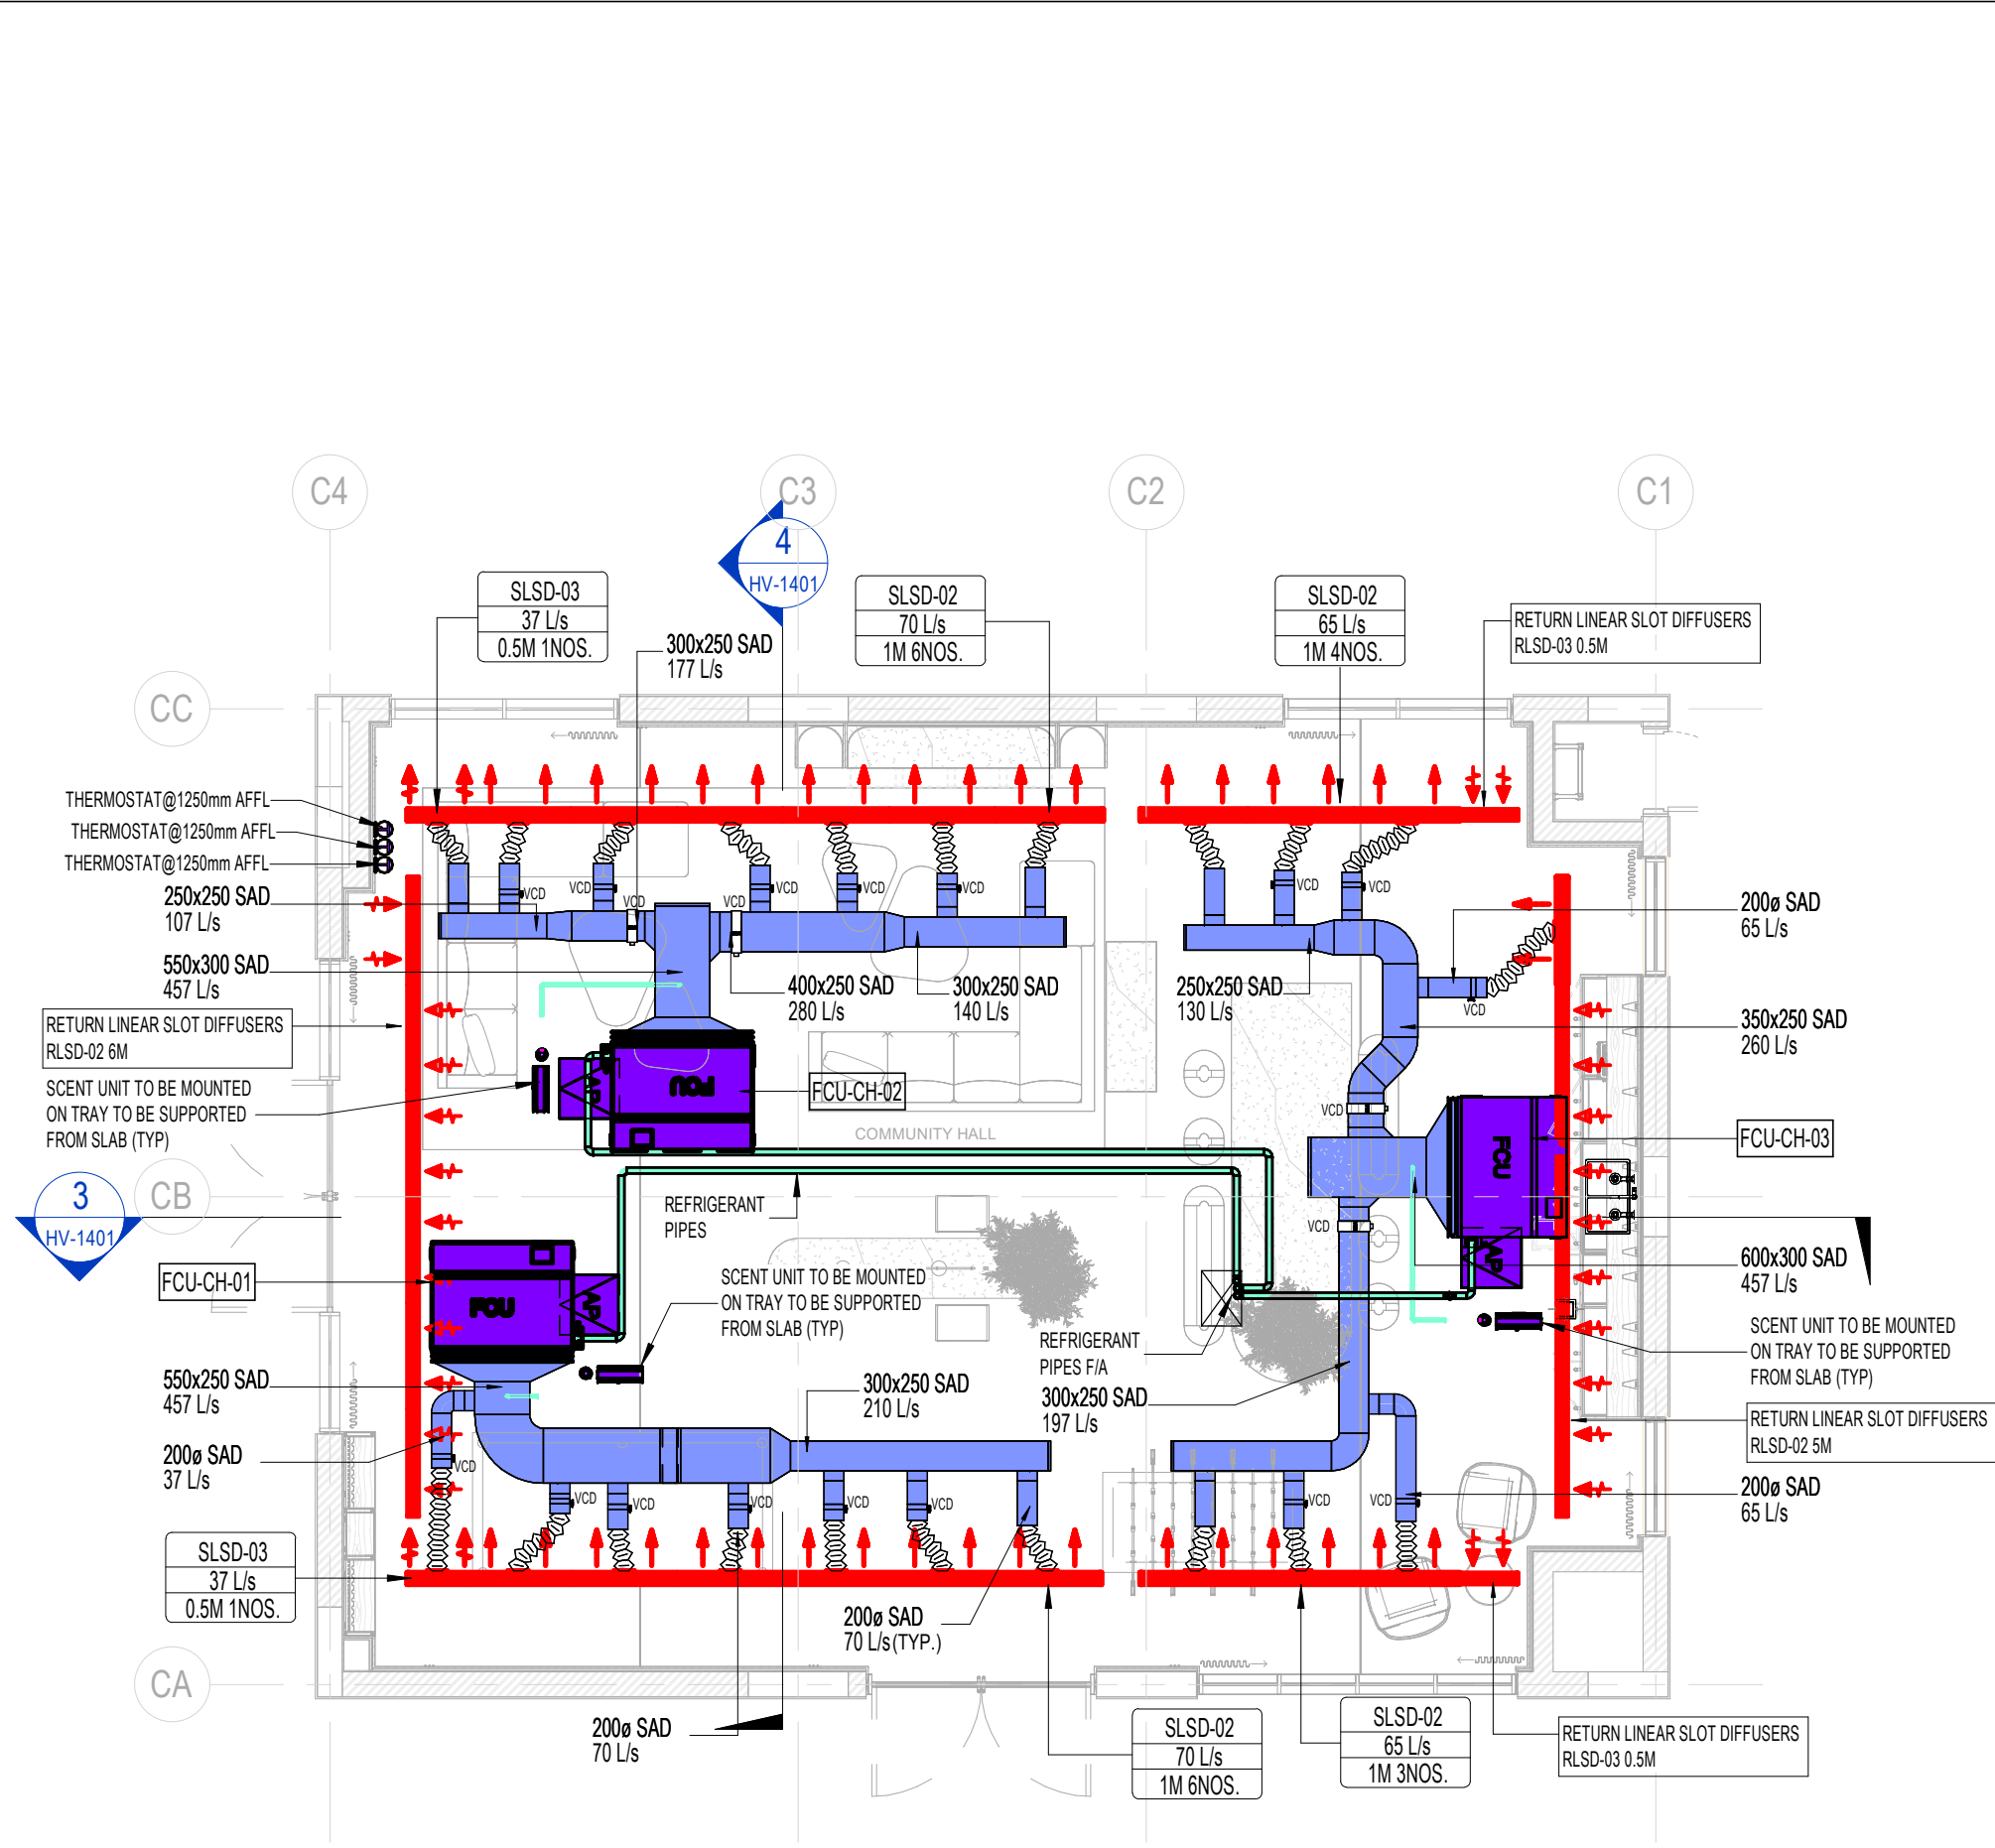


1 GROUND FLOOR HVAC LAYOUT-COMMUNITY HALL
1 : 75

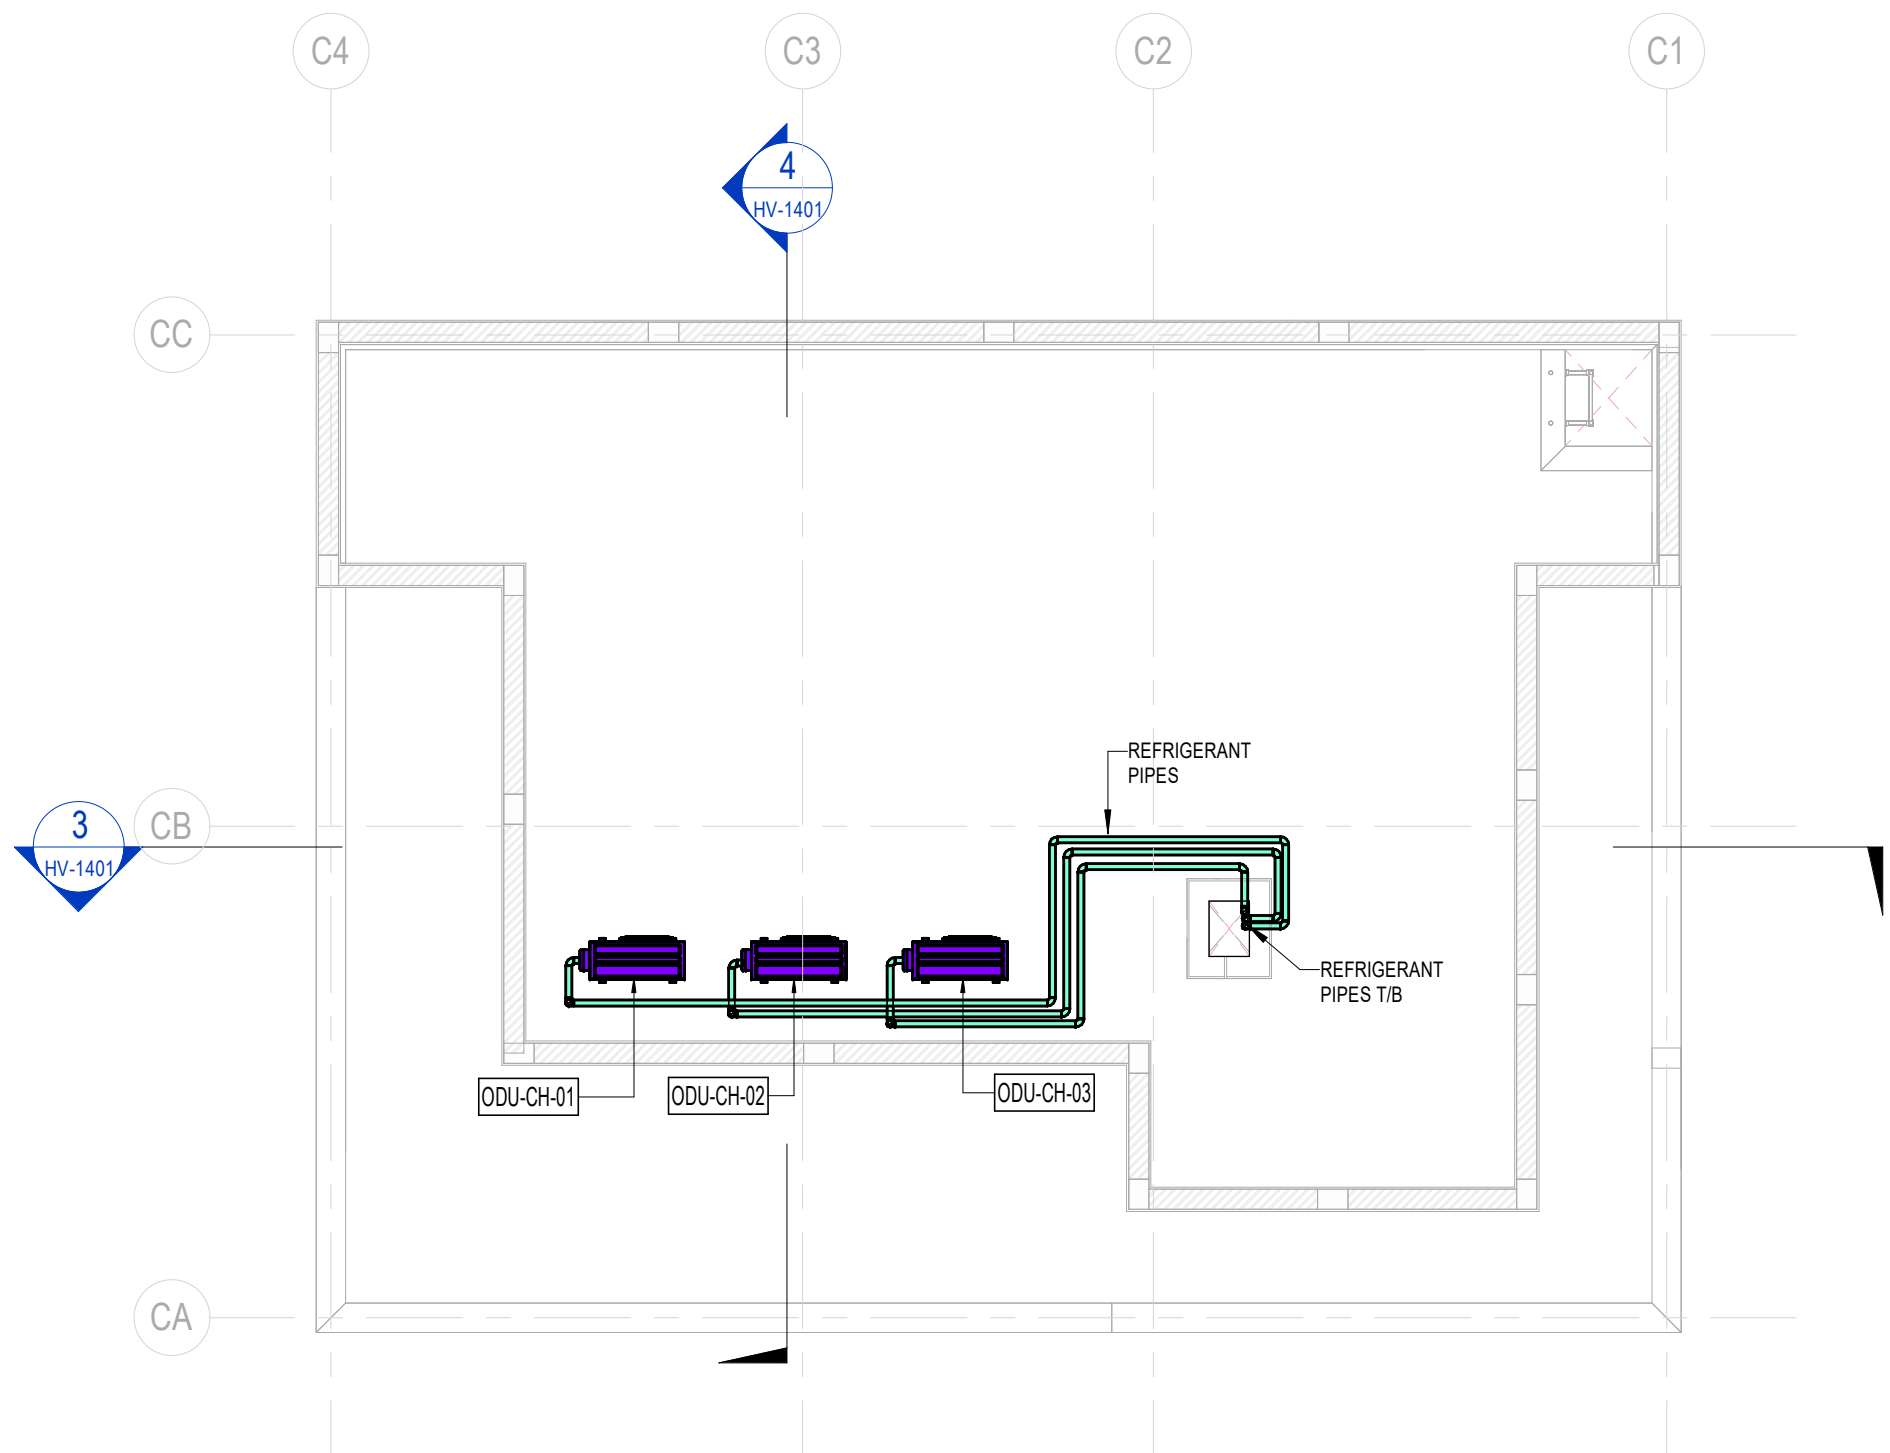


2 ROOF FLOOR HVAC LAYOUT-COMMUNITY HALL
1 : 75

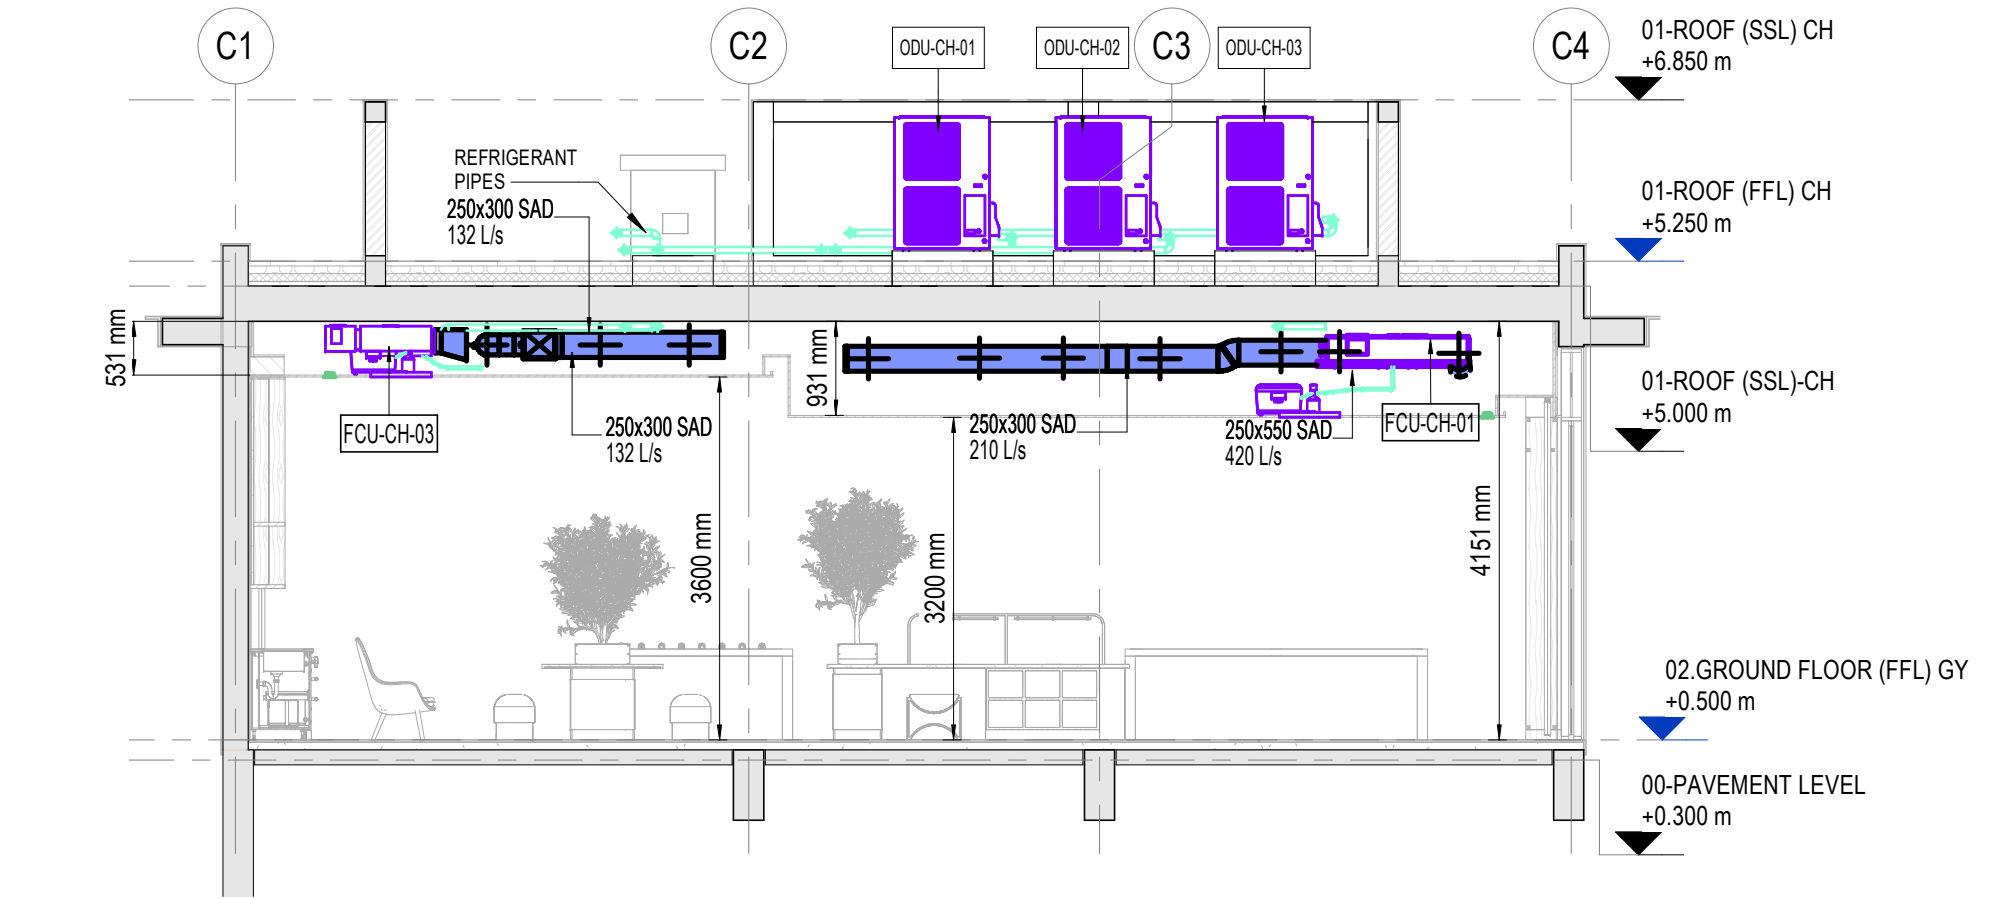


3 COMMUNITY HALL AC SECTION 01
1 : 75

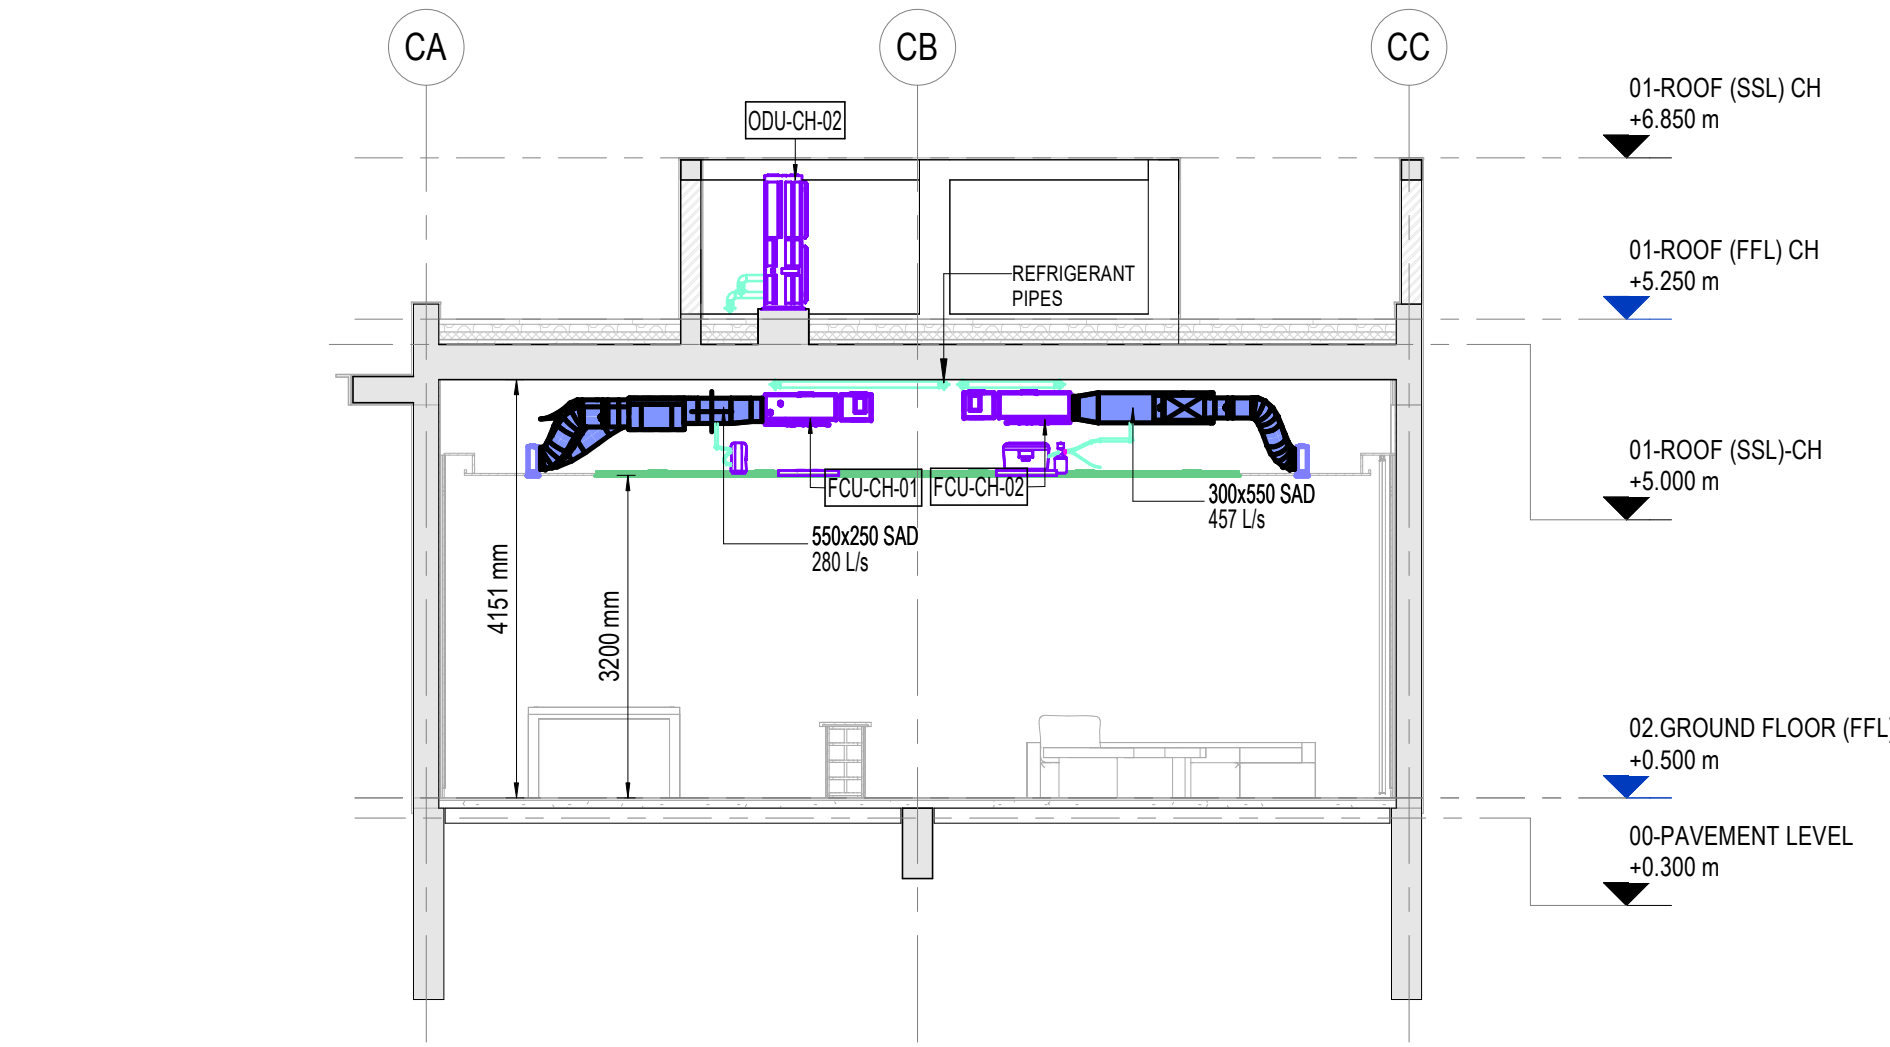

4 COMMUNITY HALL AC SECTION 02
1 : 75

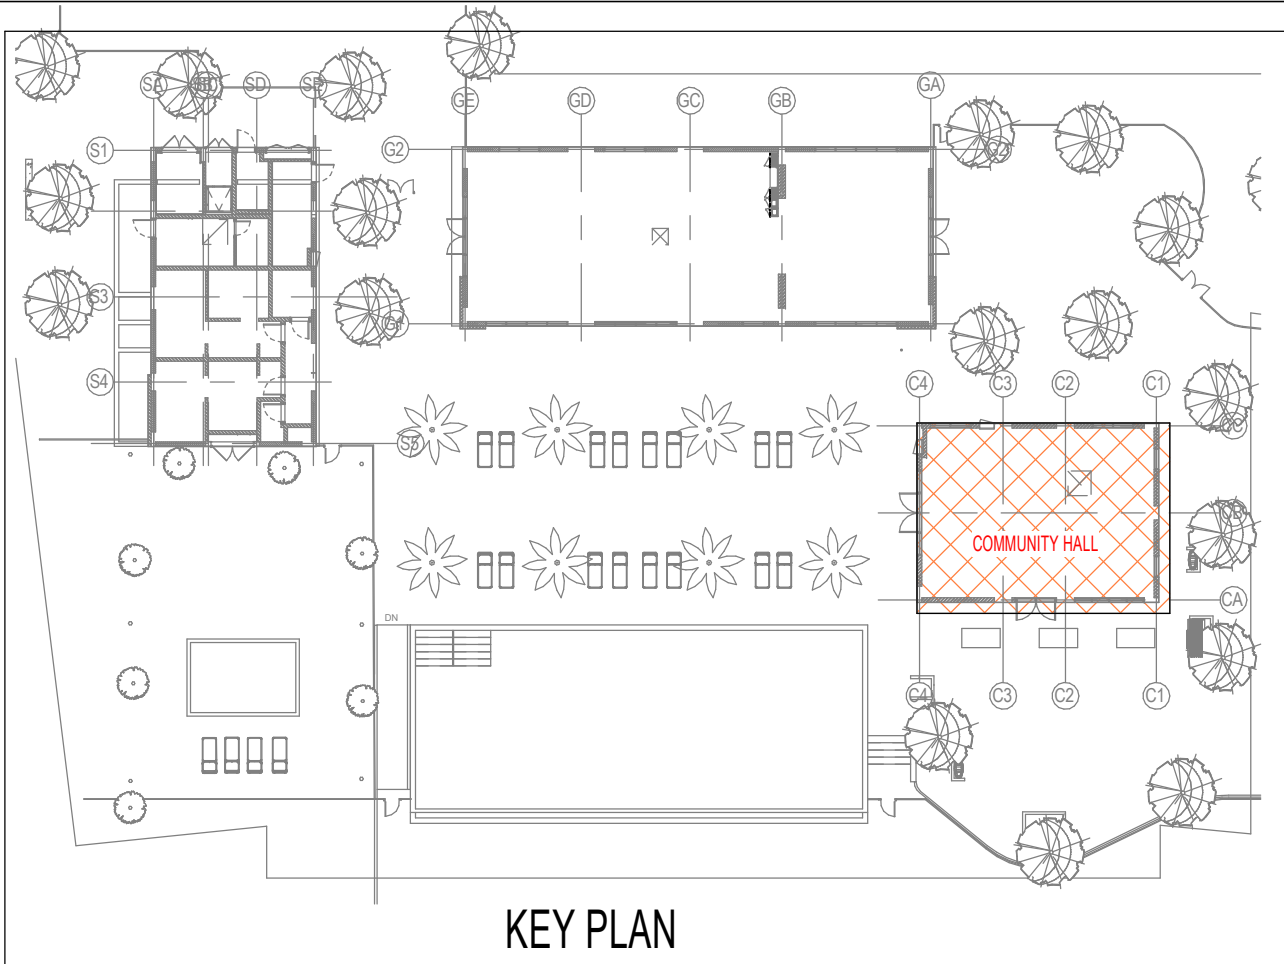

SUPPLY & RETURN LINEAR SLOT DIFFUSERS SCHEDULE						
UNIT NO.	DESCRIPTION	SLOTS		PLENUM BOX		CAPACITY RANGE (LPS)
		NO.	WIDTH (mm)	LENGTH (mm)	INLET Ø (mm)	
SLSD 01 RLSD 01	SUPPLY & RETURN LINEAR SLOT DIFFUSER	1	20	1000	Ø 150	0 TO 47
SLSD 02 RLSD 02	SUPPLY & RETURN LINEAR SLOT DIFFUSER	2	20	1000	Ø 200	48 TO 70
SLSD 03 RLSD 03	SUPPLY & RETURN LINEAR SLOT DIFFUSER	2	20	500	Ø 150	up TO 47
SLSD 04 RLSD 04	SUPPLY & RETURN LINEAR SLOT DIFFUSER	2	20	1500	Ø 150	50 TO 110

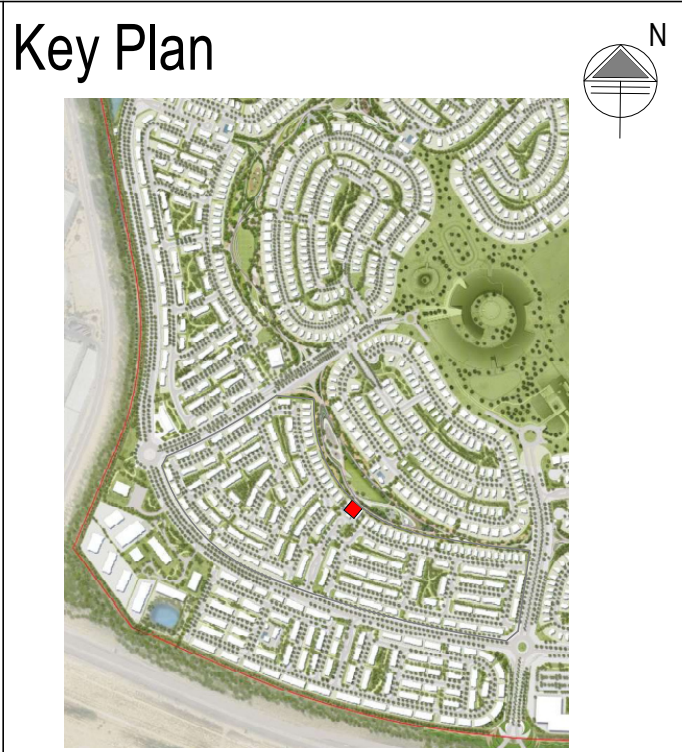

- General Notes :**
01. Do not Scale The Drawings. Follow (The MM) Written Dimensions Unless Otherwise Mentioned.
 02. Each Drawing Shall be Read in Conjunction With all Other Drawings Specification & the General Standard Details. In Case of Any Discrepancies Bring it to the Knowledge of Engineer and Same to be Resolved Prior to Execution of Work.
 03. Dimensions Shown on These Drawings are Structural Dimensions. Unless Noted Otherwise.
 04. All Levels Indicated On These Drawings are Levels as per the Survey Datum, Same Should be Verified at Site Prior to Execution of Work.
 05. All Levels Indicated On These Drawings are Based On Design Level, Which is Equivalent to Datum Level and Same Should be Verified at Site Prior to Execution of Work.



00	10/03/2026	LSG	TENDER SUBMISSION
00	16/01/2026	LSG	DETAILED DESIGN SUBMISSION
00	31/10/2025	LSG	SCHEMATIC DESIGN SUBMISSION
00	15/10/2025	LSG	SCHEMATIC SUBMISSION-50%
00	01/09/2025	LSG	CONCEPT DESIGN SUBMISSION

No.	Date	Initials	Description
-----	------	----------	-------------

REVISIONS / ISSUE	
-------------------	--

THIS DRAWING MUST NOT BE REPRODUCED IN WHOLE OR IN PART WITHOUT THE PRIOR APPROVAL OF ARIF & BINTOAK

Status

TENDER SUBMISSION

Client

EMAAR

Lead Consultant



Project Title:
Proposed Residential Townhouses
and Standalone Villas
TH-1, TH-2, and TH-3 at Grand Polo
Club & Resort, Dubai, UAE

Discipline : MECHANICAL

Drawing title:
**COMMUNITY HALL
GROUND & ROOF FLOOR
AC LAYOUT**

Architectural Engineer	Electrical Engineer	Structural Engineer
MUSTAFA ABID	MARWAN MOHD.	RIHAM RAMADAN
Registration # 5847	Registration # 60102	Registration # 105892
Scale(s): As indicated	Date: 10/03/2026	Project no: 1857
Drawn by: LSG	Checked: MAV	Approved: MRM

Drawing Number : GPCR-TH02-AB-DRG-ZZZ-MEC-HV-1401-00