




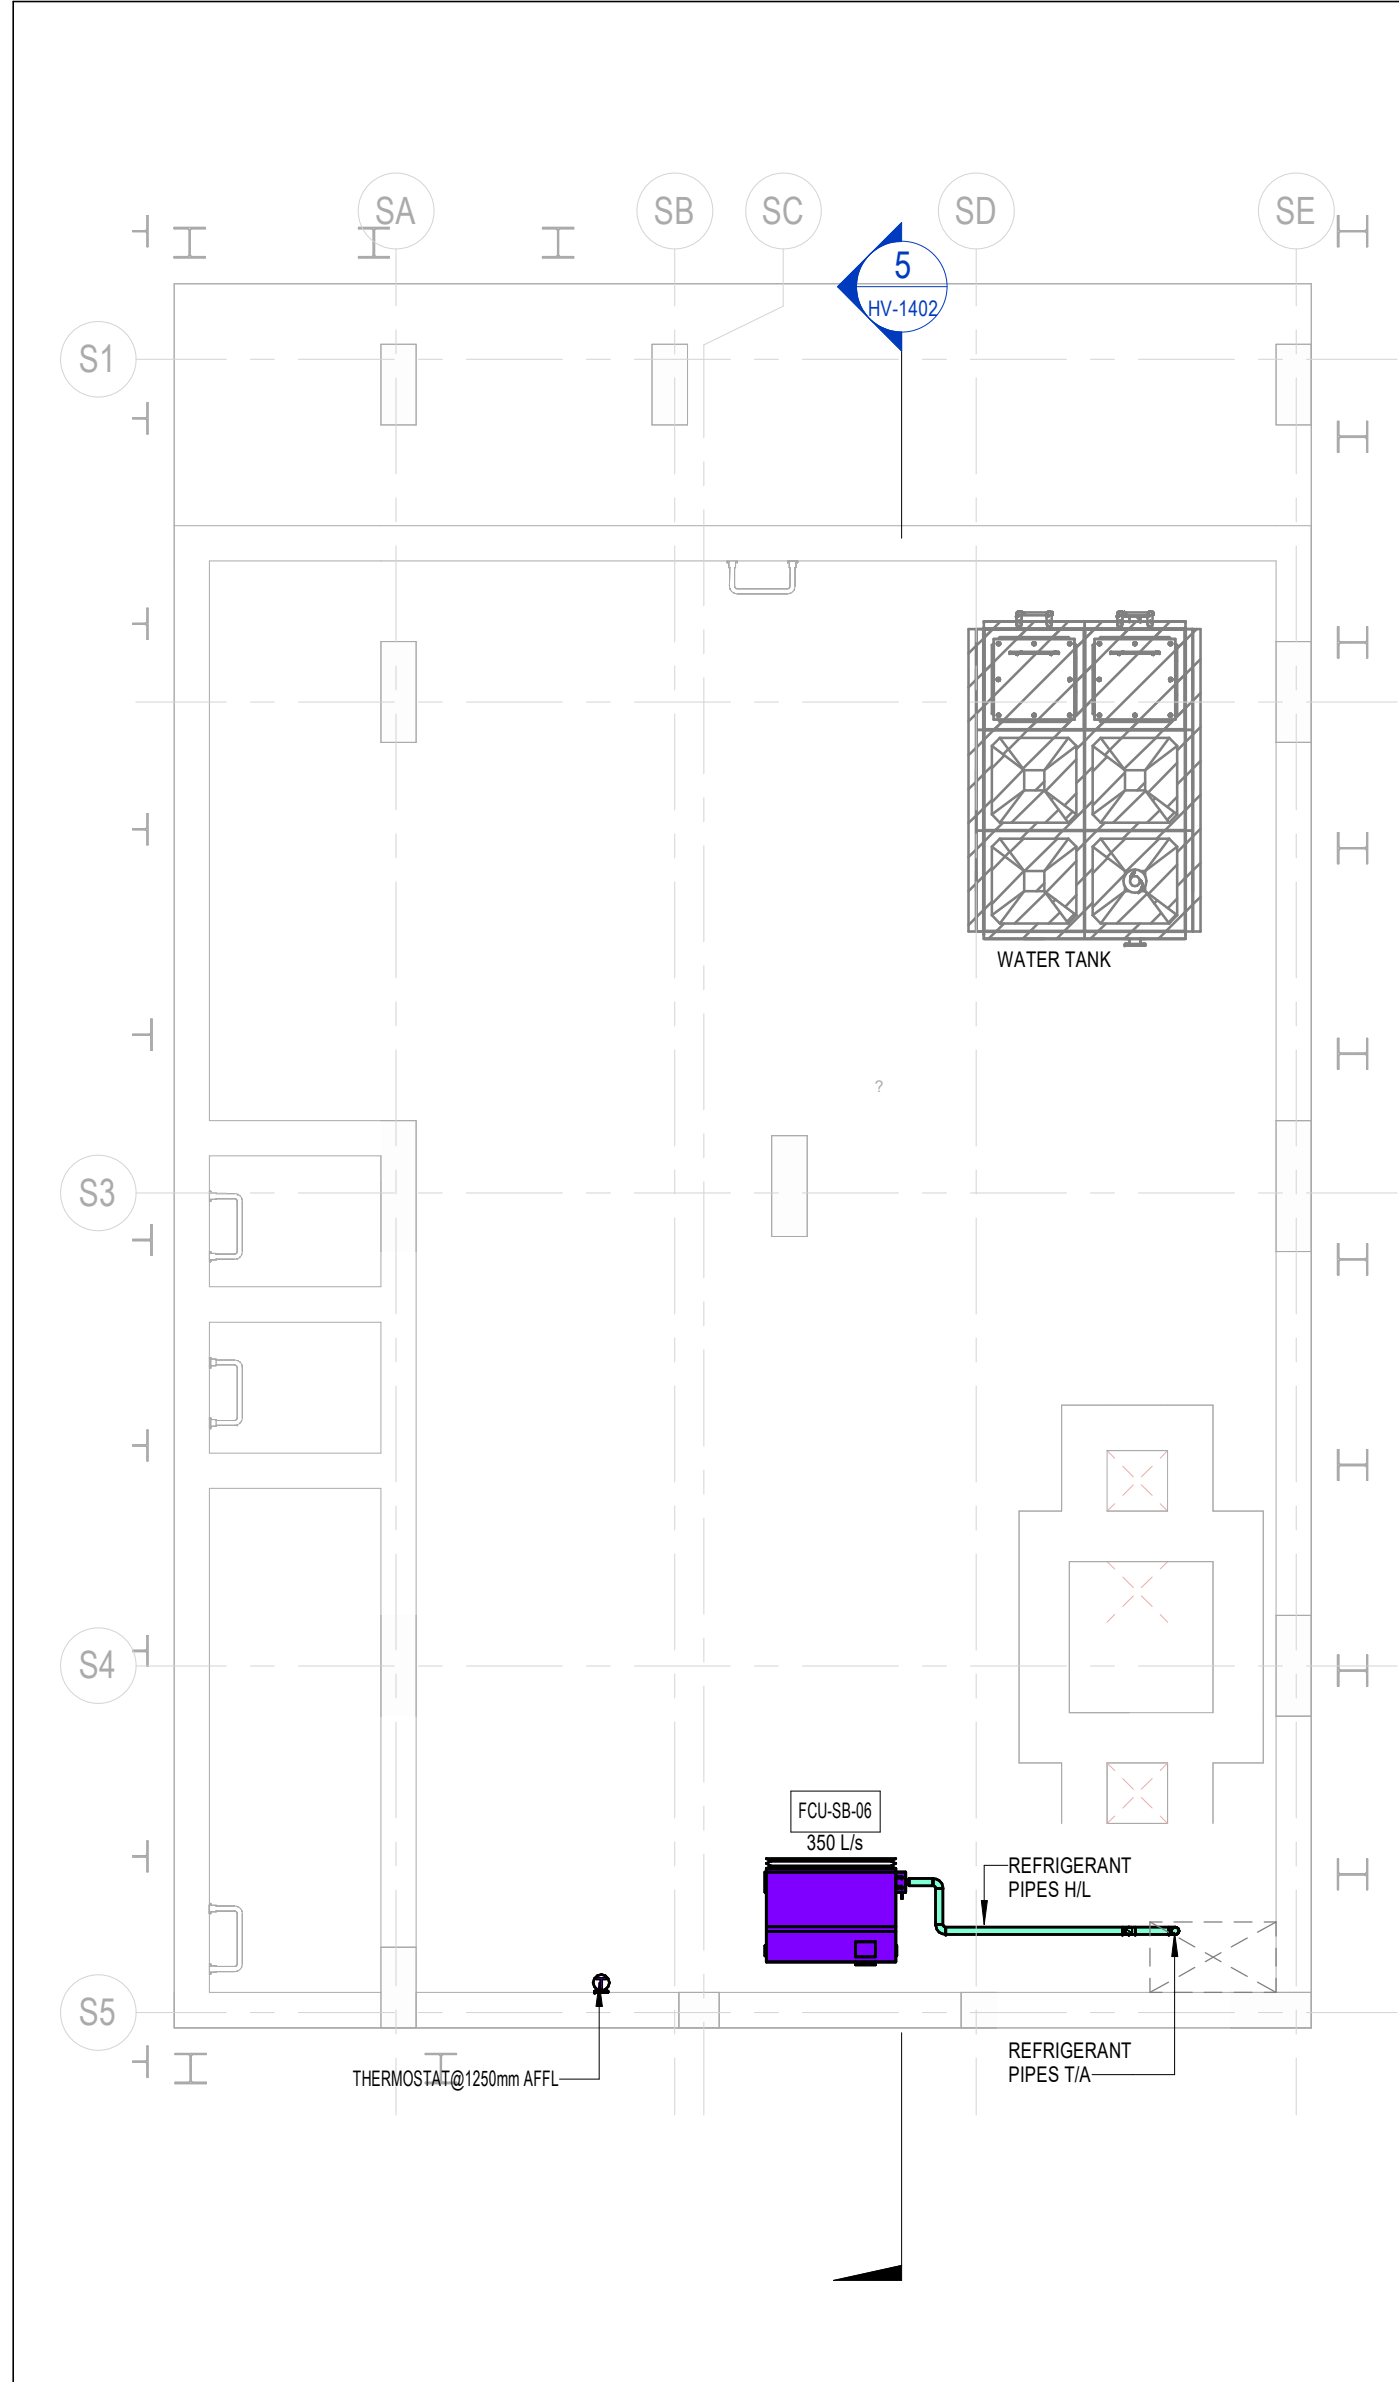


1 BASEMENT FLOOR HVAC LAYOUT
1 : 75

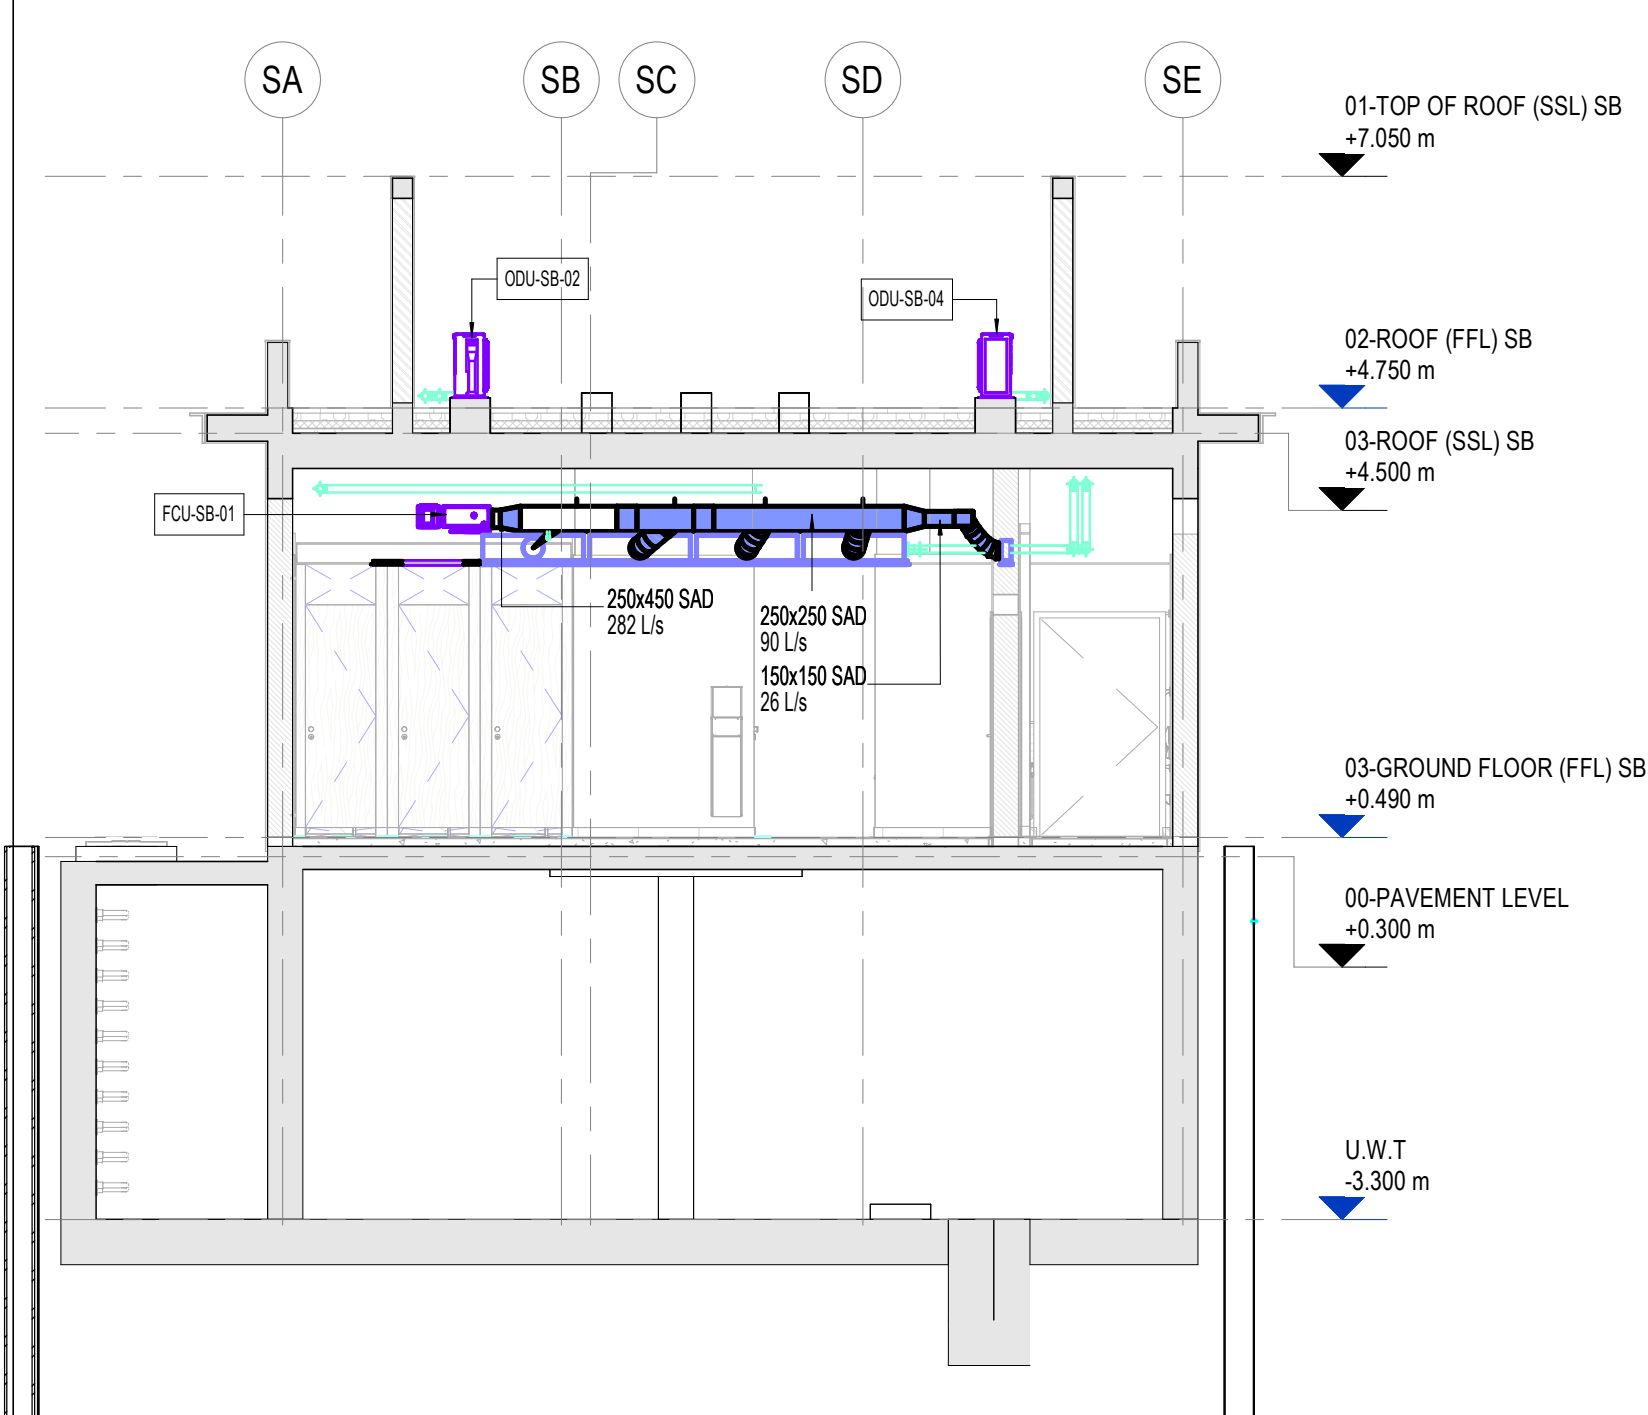


4 SERVICE BLOCK AC SECTION 01
1 : 75

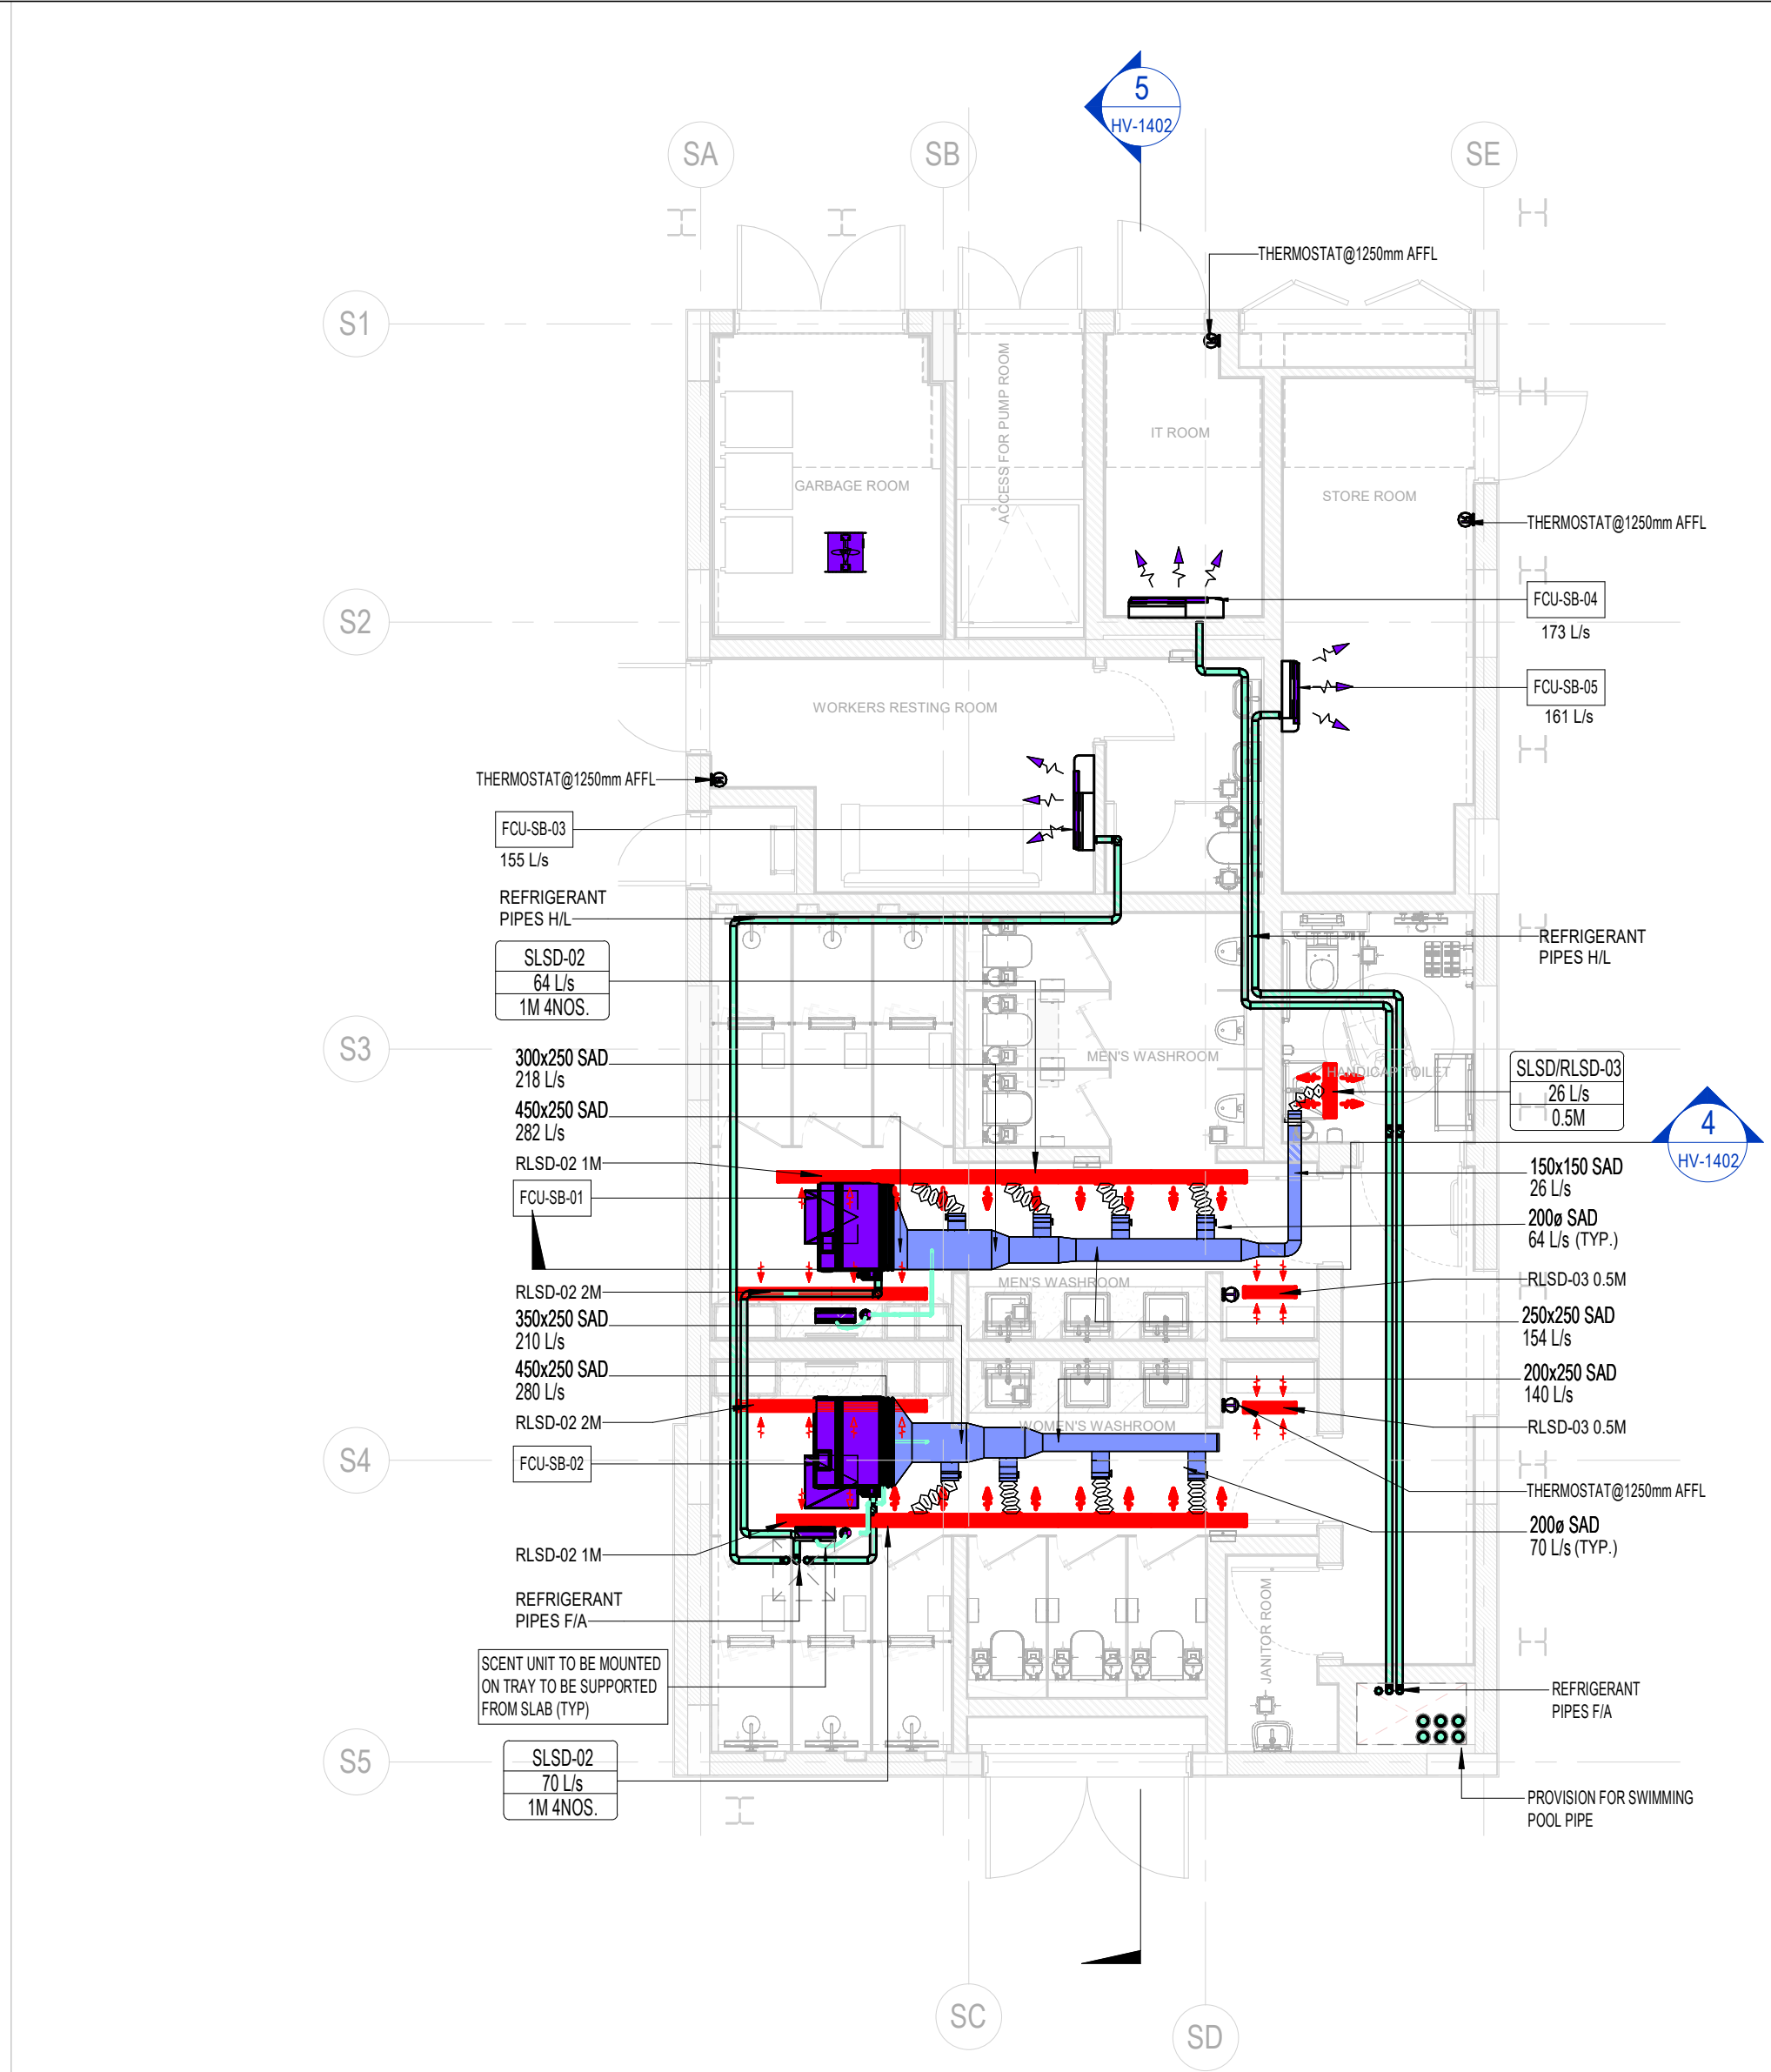

2 GROUND FLOOR HVAC LAYOUT-SERVICE BLOCK
1 : 75

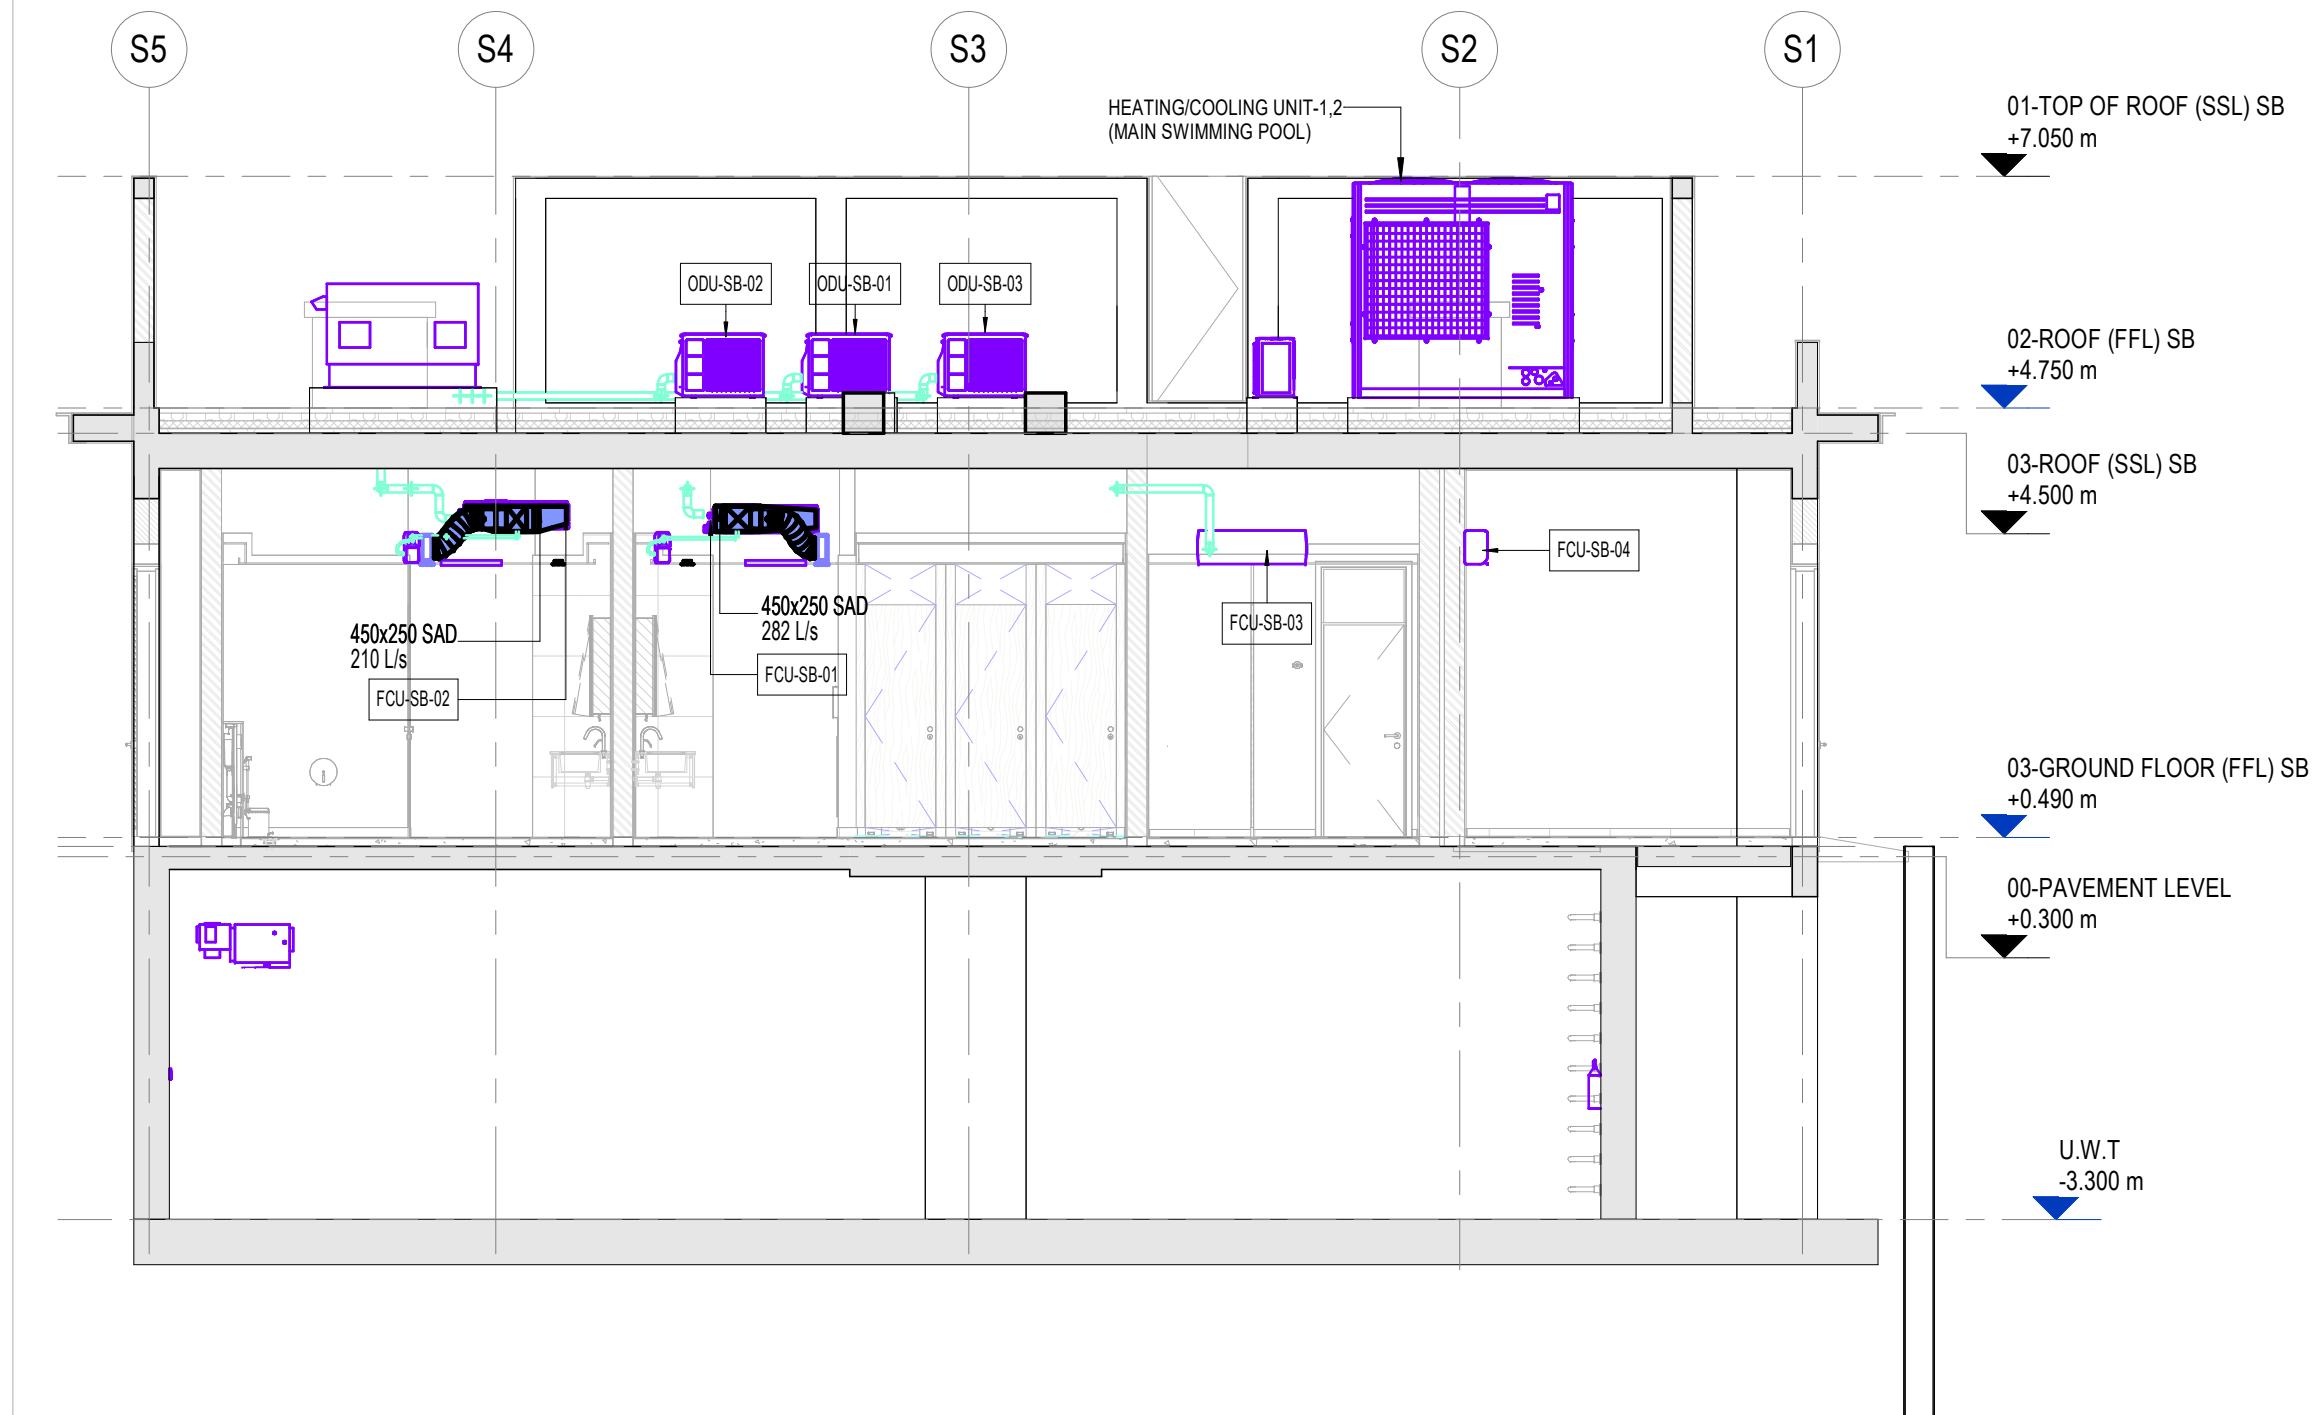


5 SERVICE BLOCK AC SECTION 02
1 : 75

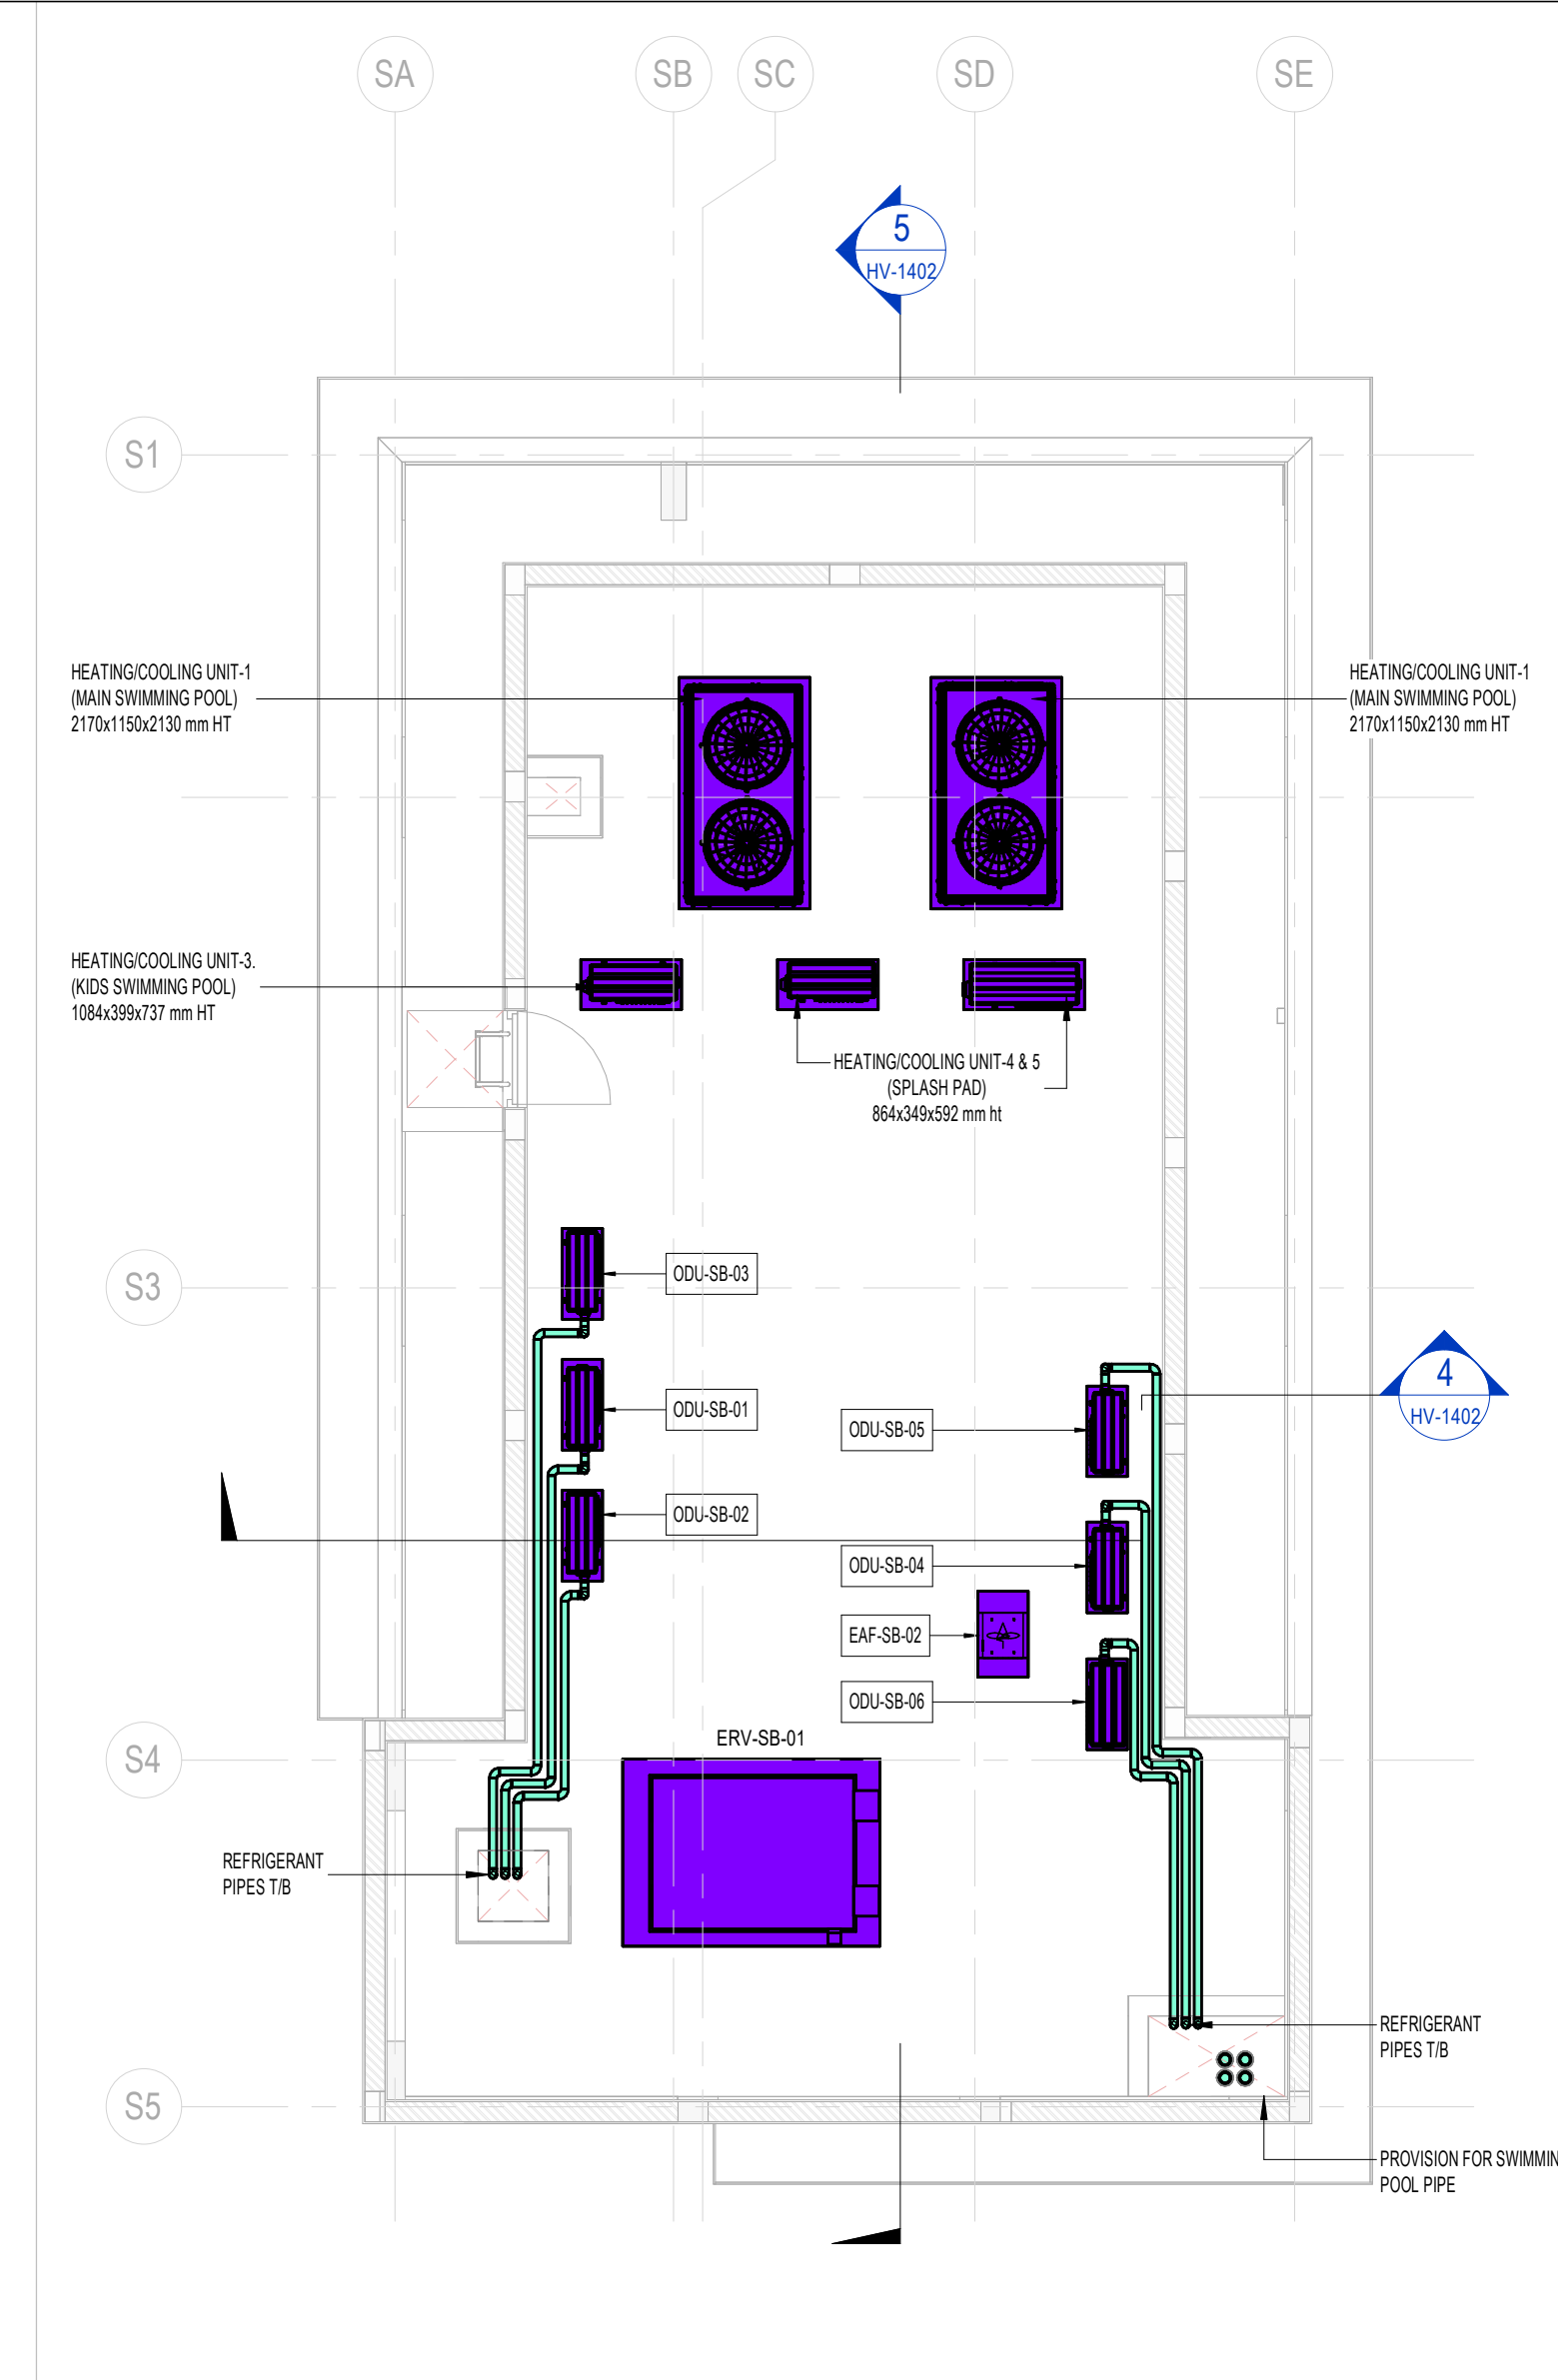

3 ROOF FLOOR HVAC LAYOUT-SERVICE BLOCK
1 : 75

SUPPLY & RETURN LINEAR SLOT DIFFUSERS SCHEDULE						
UNIT NO.	DESCRIPTION	SLOTS		PLENUM BOX		CAPACITY RANGE (LPS)
		NO.	WIDTH (mm)	LENGTH (mm)	INLET Ø (mm)	
SLSD 01 RLSD 01	SUPPLY & RETURN LINEAR SLOT DIFFUSER	1	20	1000	Ø 150	0 TO 47
SLSD 02 RLSD 02	SUPPLY & RETURN LINEAR SLOT DIFFUSER	2	20	1000	Ø 200	48 TO 70
SLSD 03 RLSD 03	SUPPLY & RETURN LINEAR SLOT DIFFUSER	2	20	500	Ø 150	up TO 47
SLSD 04 RLSD 04	SUPPLY & RETURN LINEAR SLOT DIFFUSER	2	20	1500	Ø 150	50 TO 110

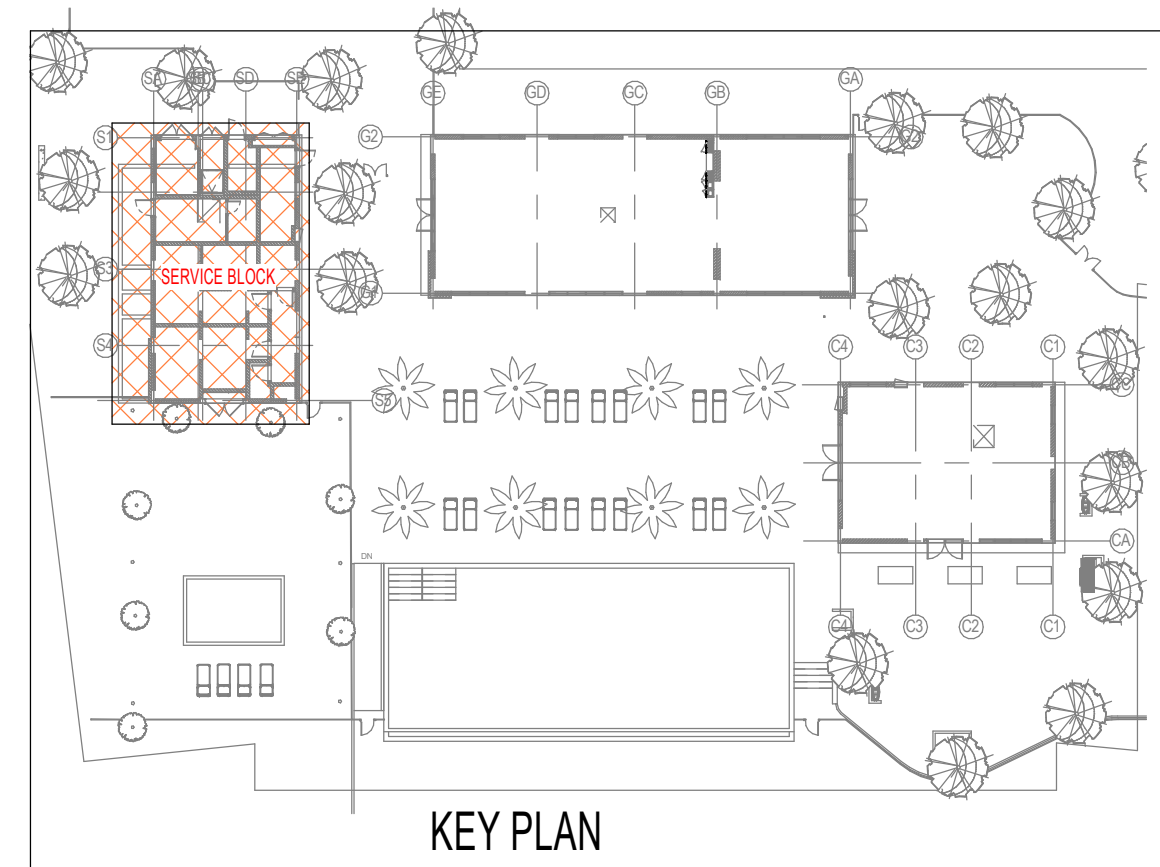

Key Plan

General Notes :

01. Do not Scale The Drawings. Follow (The MM) Written Dimensions Unless Otherwise Mentioned.

02. Each Drawing Shall be Read in Conjunction With all Other Drawings Specification & the General Standard Details. In Case of Any Discrepancies Bring it to the Knowledge of Engineer and Same to be Resolved Prior to Execution of Work.

03. Dimensions Shown on These Drawings are Structural Dimensions. Unless Noted Otherwise.

04. All Levels Indicated On These Drawings are Levels as per the the Survey Datum, Same Should be Verified at Site Prior to Execution of Work.

05. All Levels Indicated On These Drawings are Based On Design Level, Which is Equivalent to Datum Level and Same Should be Verified at Site Prior to Execution of Work.

0010/03/2026LSGTENDER SUBMISSION

0016/01/2026LSGDETAILED DESIGN SUBMISSION

0031/10/2025LSGSCHEMATIC DESIGN SUBMISSION

0015/10/2025LSGSCHEMATIC SUBMISSION-50%

0001/09/2025LSGCONCEPT DESIGN SUBMISSION

No.

Date

Initials

Description

REVISIONS / ISSUE

THIS DRAWING MUST NOT BE REPRODUCED IN WHOLE OR IN PART WITHOUT THE PRIOR APPROVAL OF ARIF & BINTOAK

Status

TENDER SUBMISSION

Client

EMAAR

Lead Consultant

المستشار
عارف وبن طوق
Arif & Bint oak
consulting architects & engineers

POST BOX 5070 DUBAI UAE TEL: 04-3372886 FAX: 04-3372832
POST BOX 52081 ABU DHABI UAE TEL: 02-5546055 arif@arifbintoak.ae

Project Title:

Proposed Residential Townhouses and Standalone Villas
TH-1, TH-2, and TH-3 at Grand Polo Club & Resort, Dubai, UAE

Discipline:

MECHANICAL

Drawing title:

SERVICE BLOCK
BASEMENT, GROUND & ROOF FLOOR
AC LAYOUT

Architectural Engineer

Electrical Engineer

Structural Engineer

MUSTAFA ABID

MARWAN MOHD.

RIHAM RAMADAN

Registration # 5847

Registration # 80102

Registration # 105892

Scale(s):

Date:

Project no:

As indicated

10/03/2026

1857

Drawn by:

Checked:

Approved:

LSG

MAV

MRM

Drawing Number:

GPCR-TH02-AB-DRG-ZZZ-MEC-HV-1402-00

This 2D drawing is extracted from 3D BIM Model

3/9/2026 9:33:03 AM

© AB 1 A1 Title Block - BIM Standard Ver: 2.0