




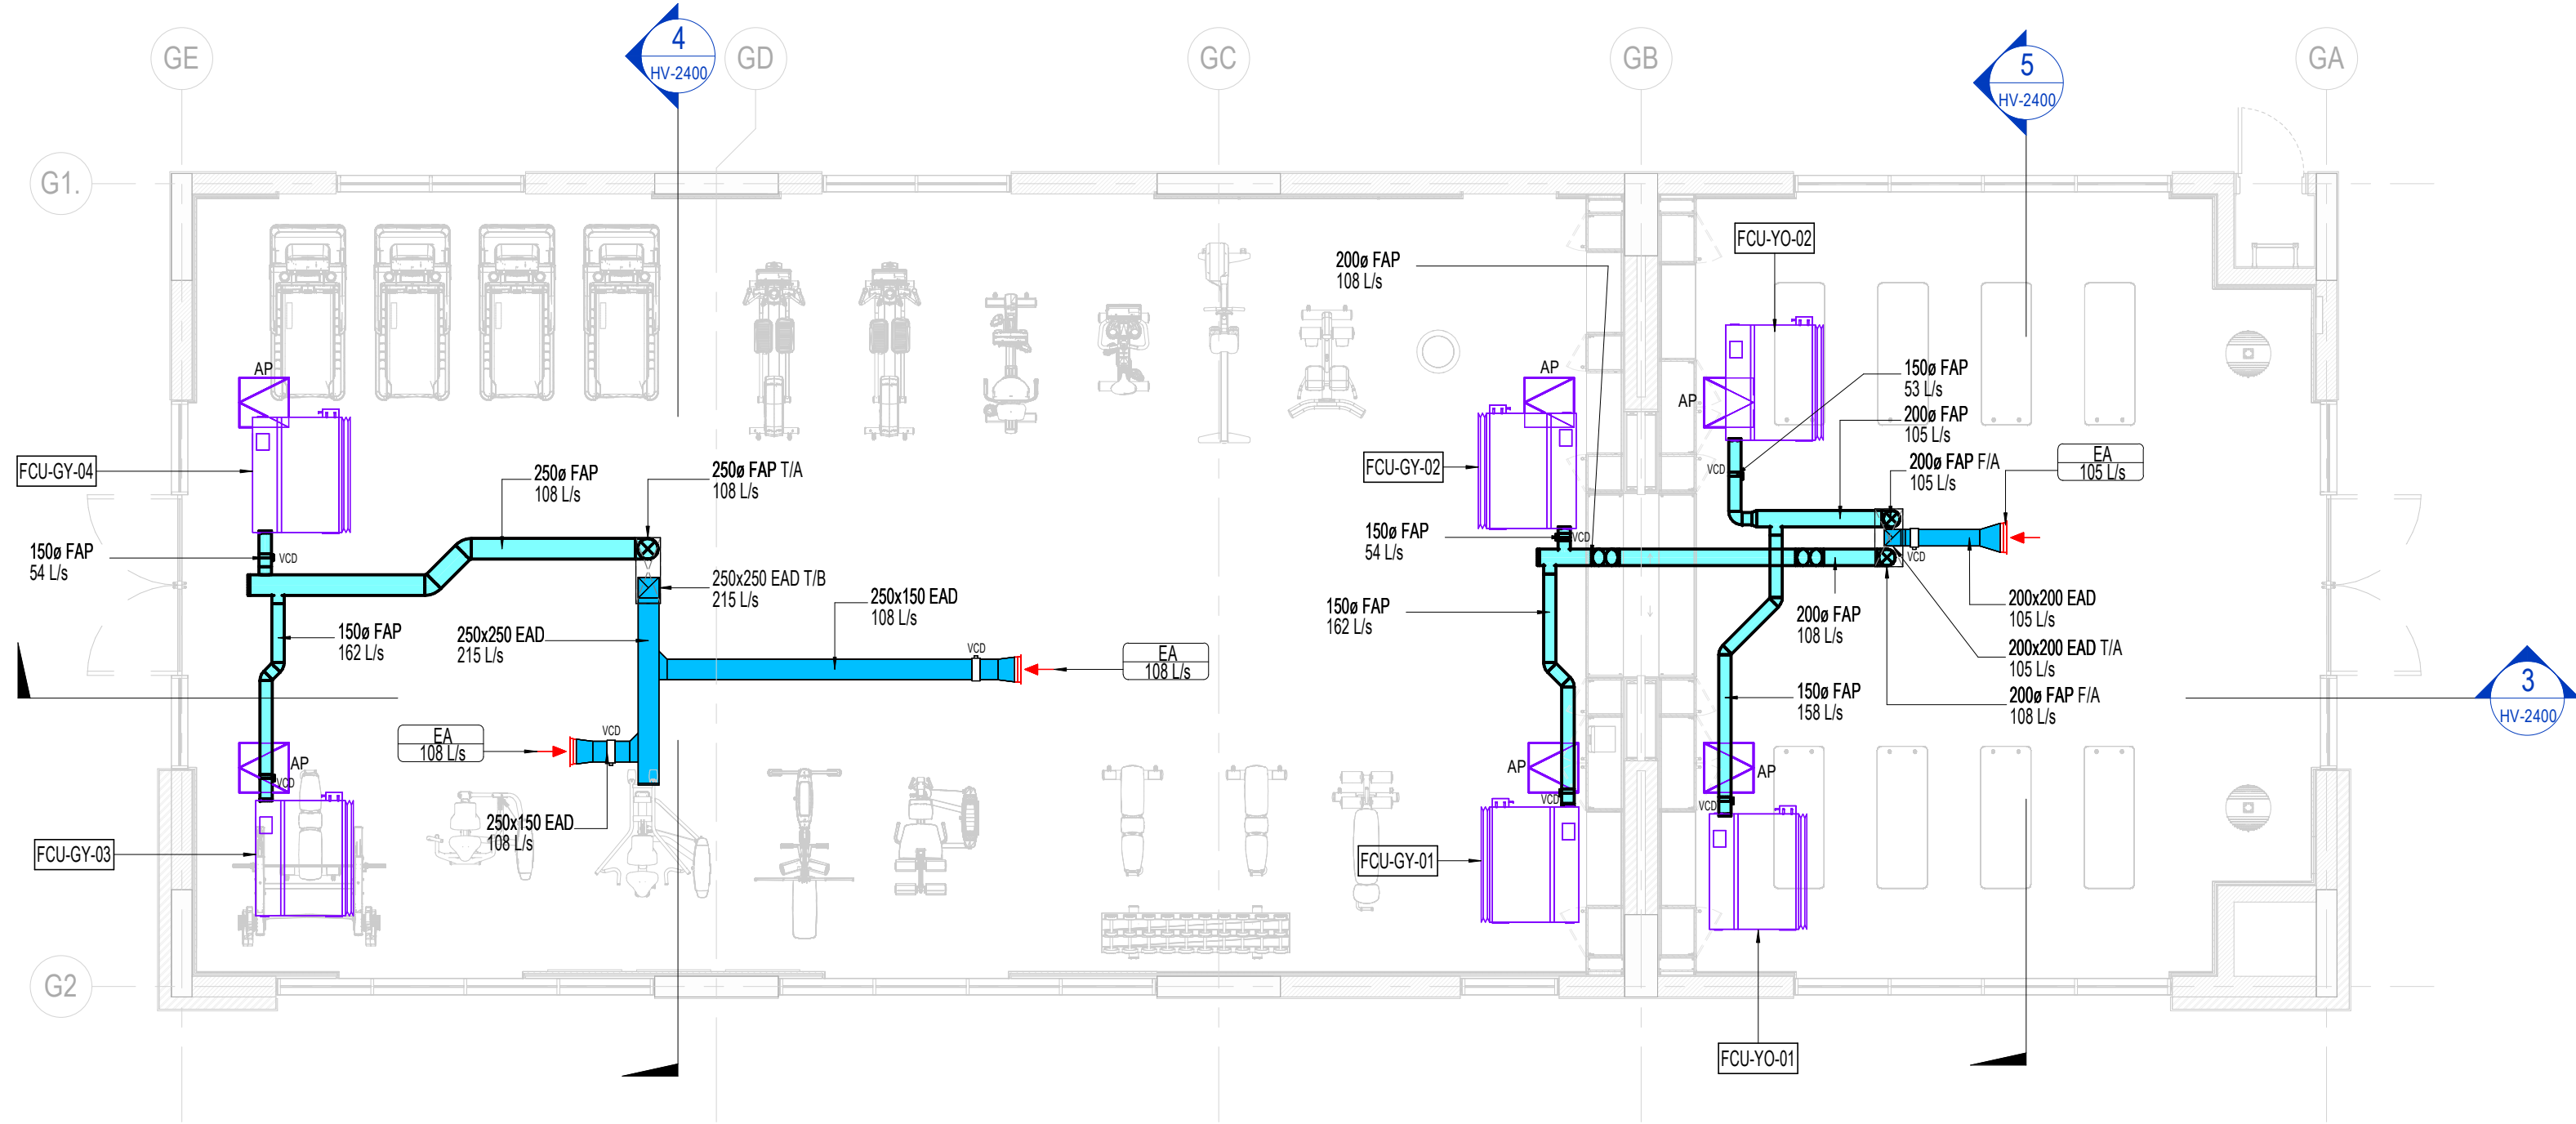


1 GROUND FLOOR VENTILATION LAYOUT-GYM&YOGA
1 : 75

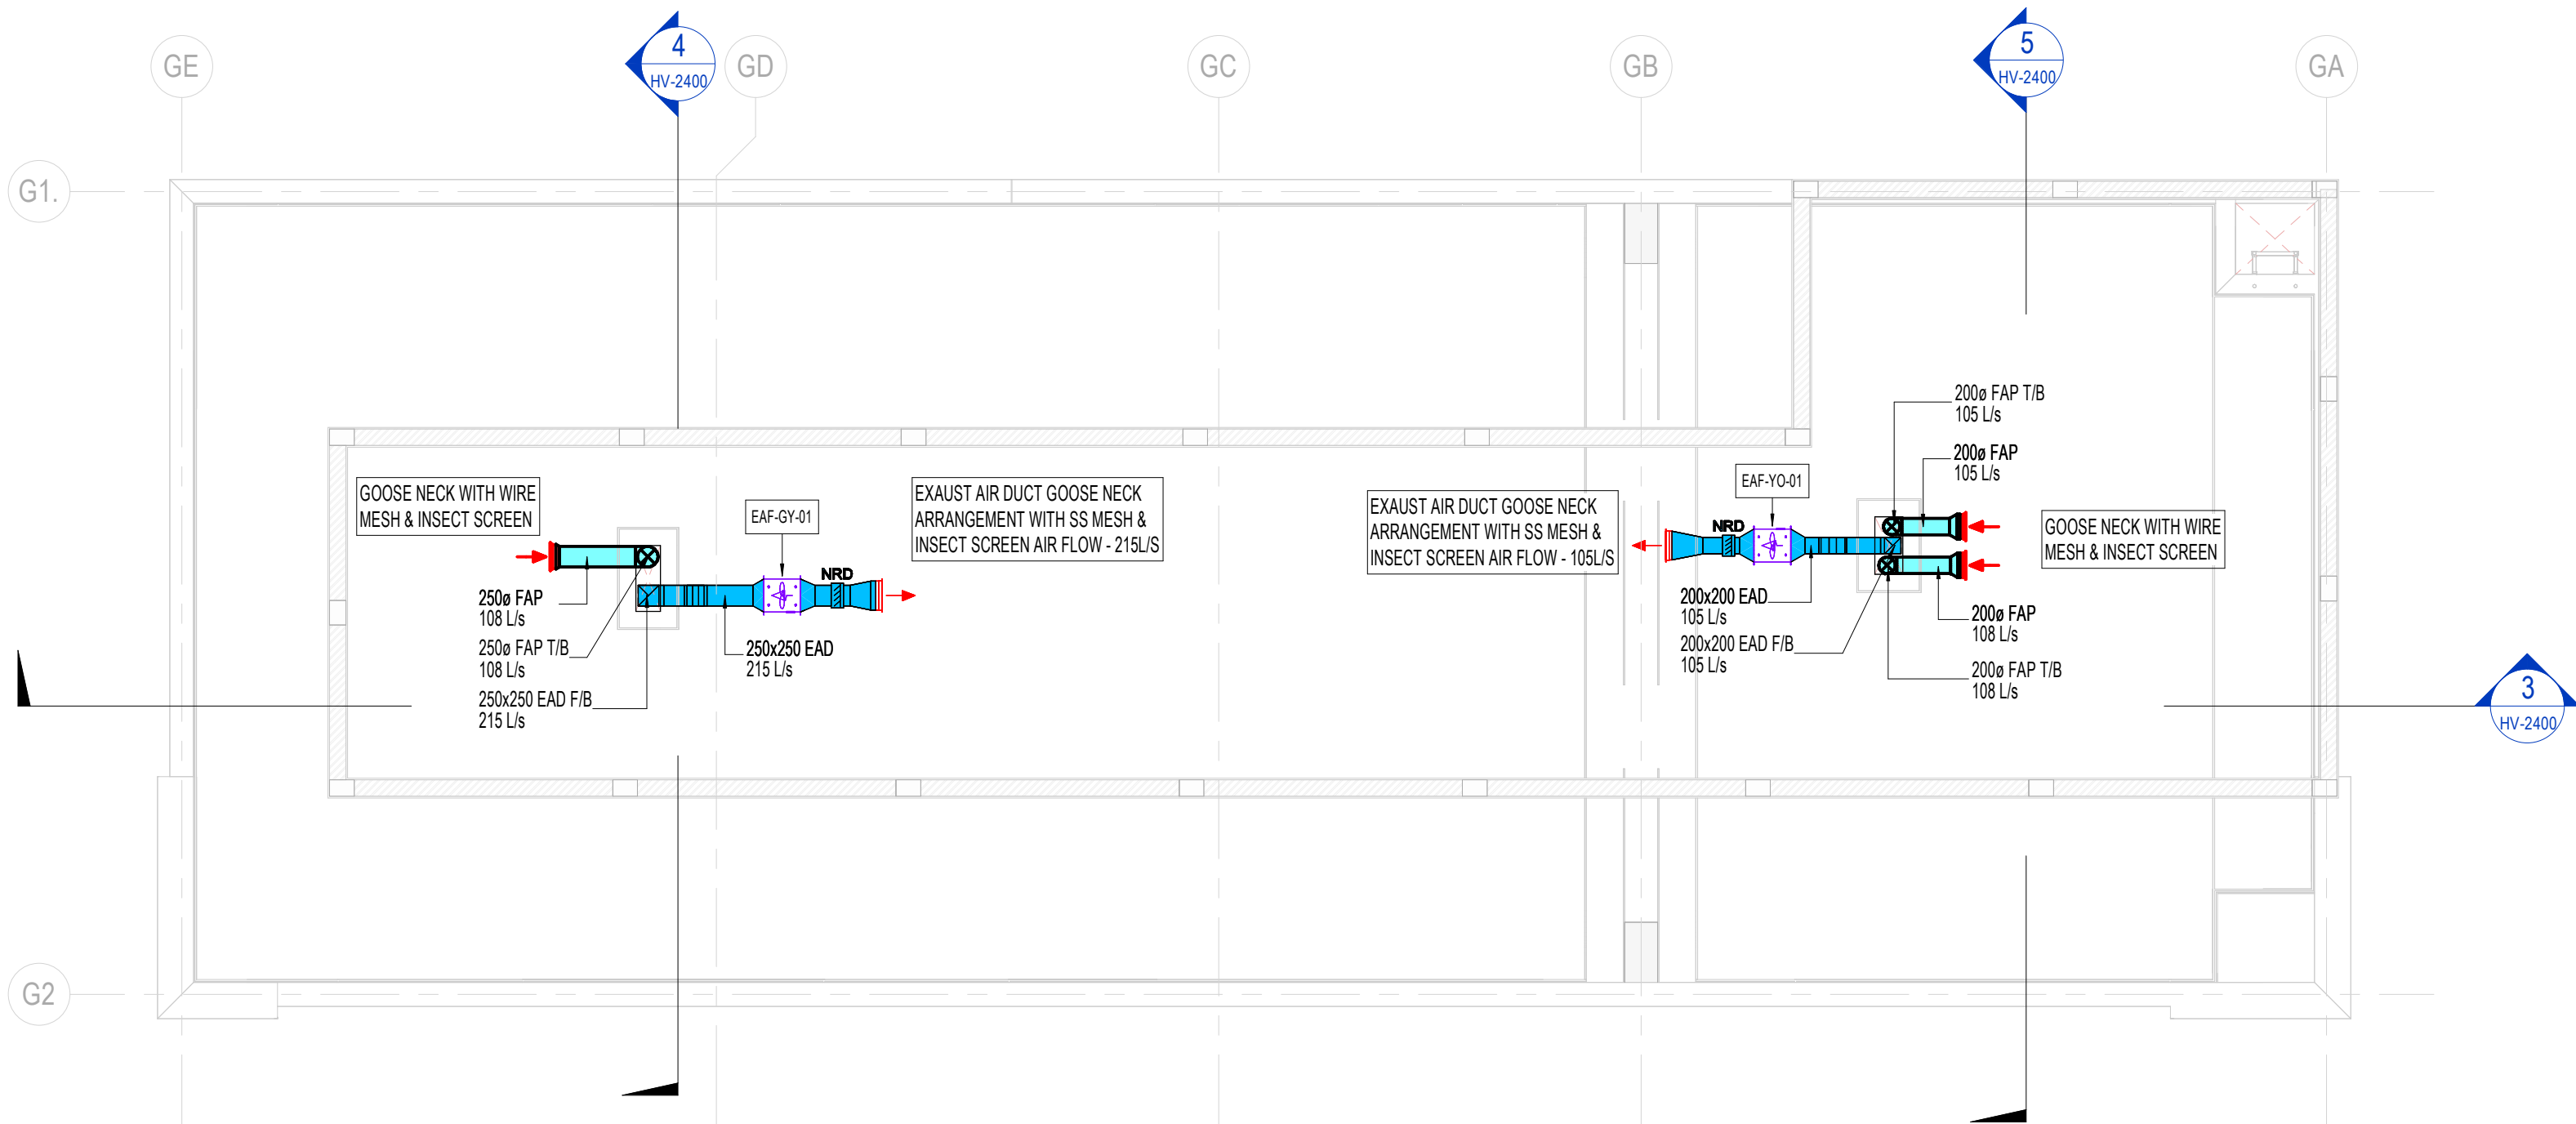

2 ROOF FLOOR VENTILATION LAYOUT-GYM&YOGA
1 : 75

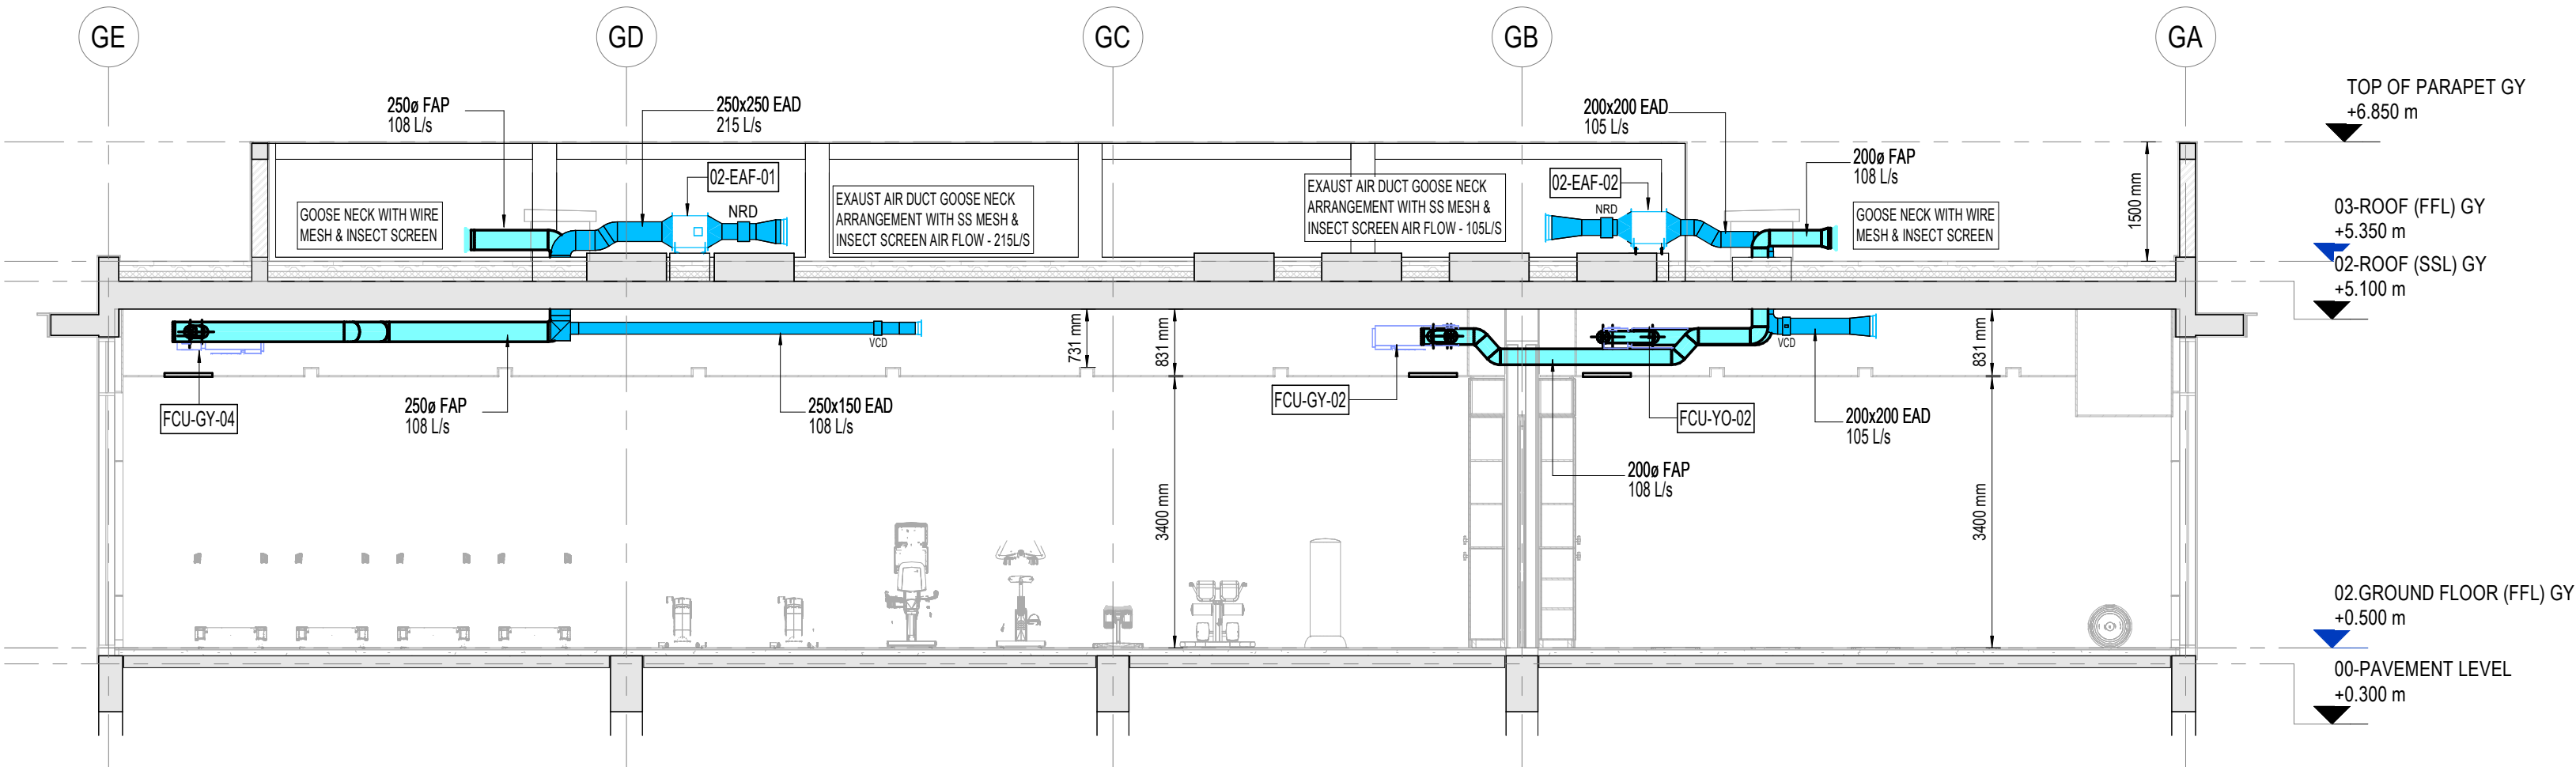


3 GYM&YOGA VENTILATION SECTION 02
1 : 75

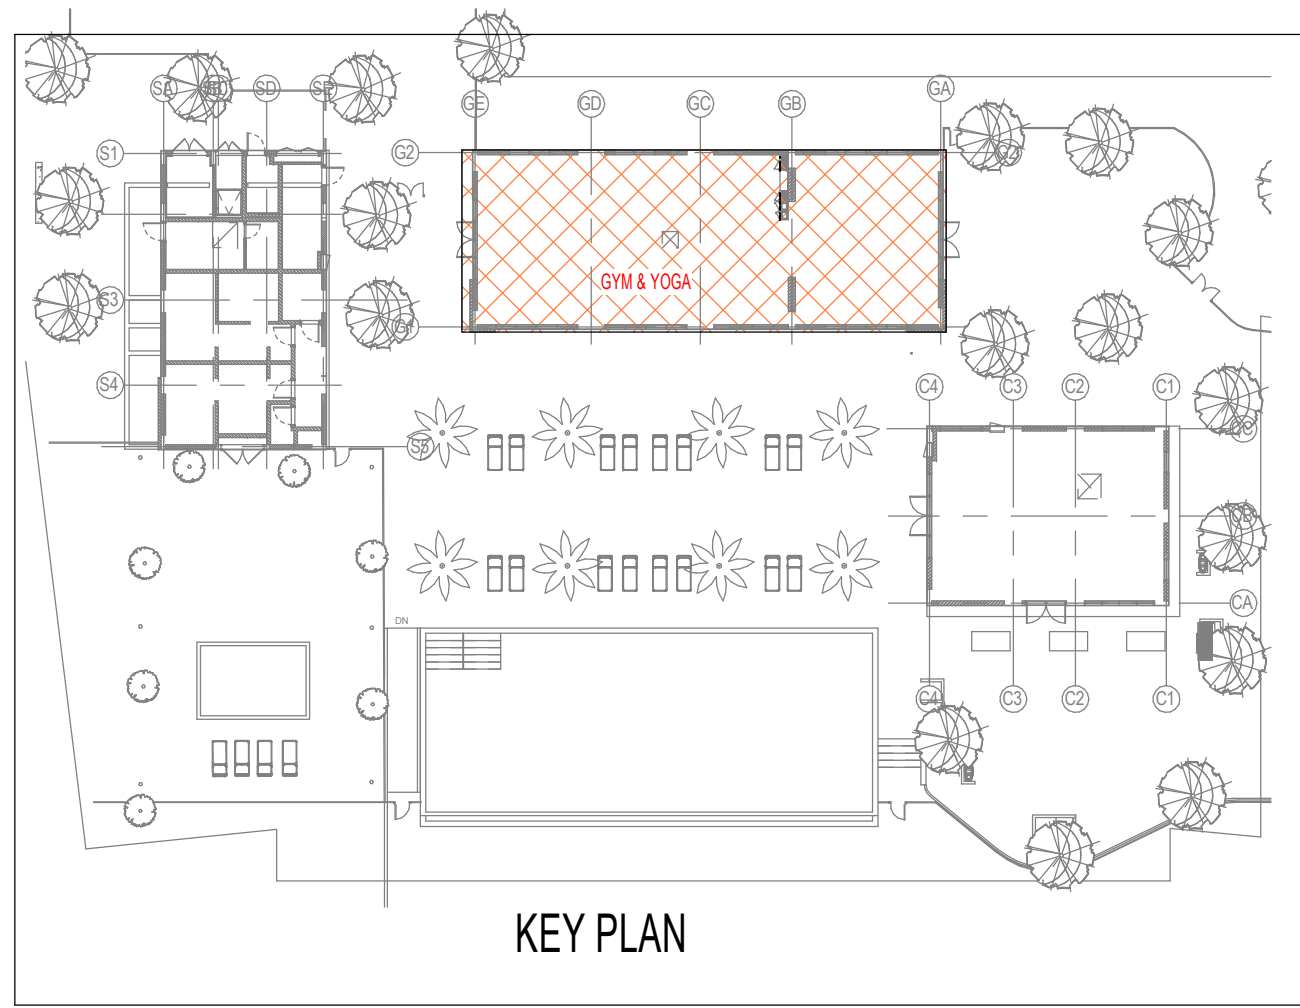


Key Plan

General Notes :

01. Do not Scale The Drawings. Follow (The MM) Written Dimensions Unless Otherwise Mentioned.
02. Each Drawing Shall be Read in Conjunction With all Other Drawings Specification & the General Standard Details. In Case of Any Discrepancies Bring it to the Knowledge of Engineer and Same to be Resolved Prior to Execution of Work.
03. Dimensions Shown on These Drawings are Structural Dimensions Unless Noted Otherwise.
04. All Levels Indicated On These Drawings are Levels as per the Survey Datum, Same Should be Verified at Site Prior to Execution of Work.
05. All Levels Indicated On These Drawings are Based On Design Level, Which is Equivalent to Datum Level and Same Should be Verified at Site Prior to Execution of Work.

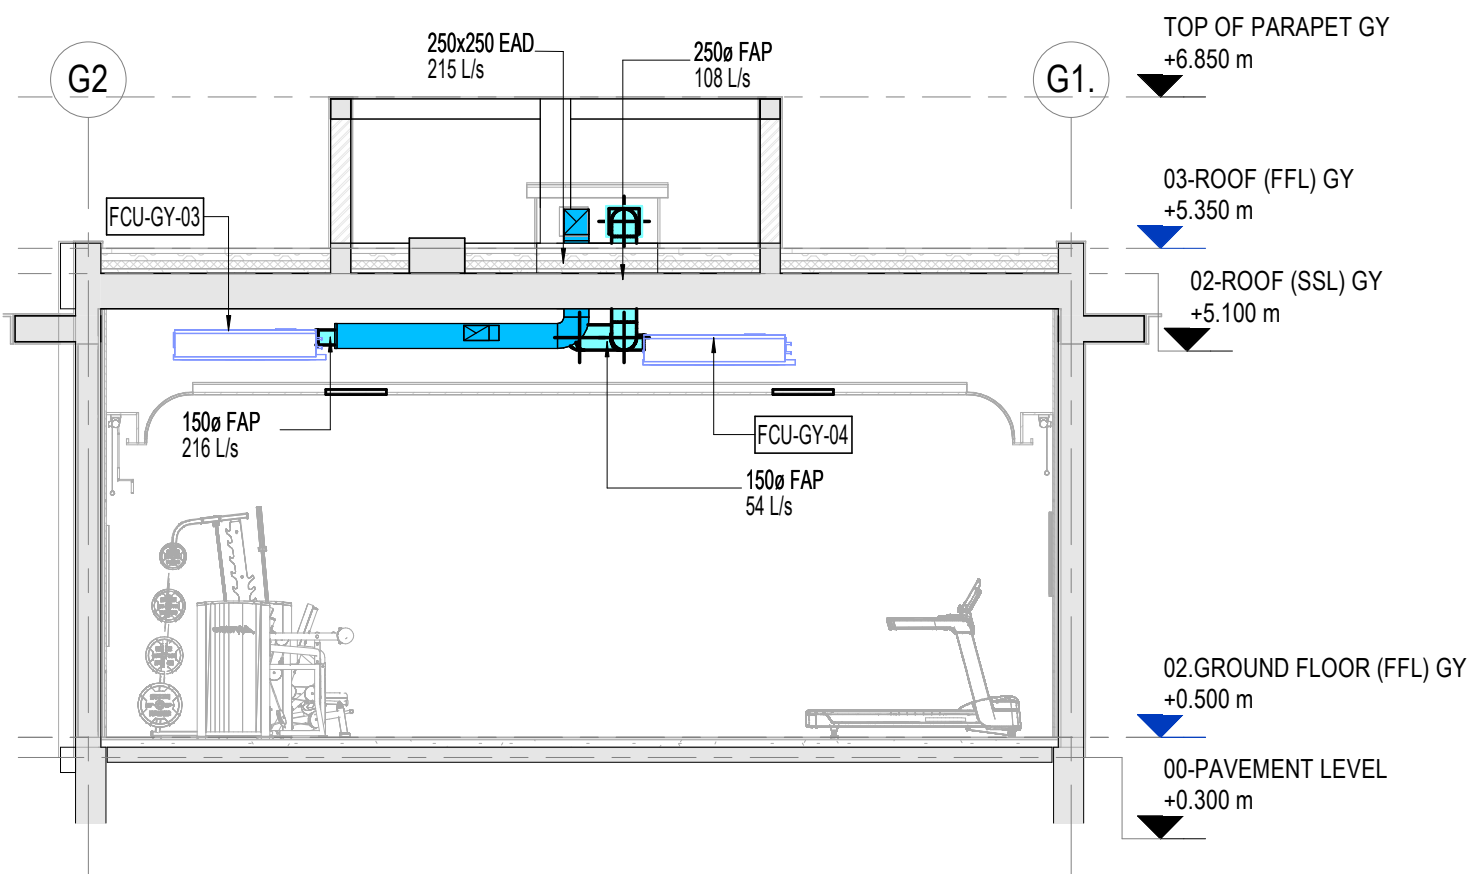

4 GYM&YOGA VENTILATION SECTION 01
1 : 75

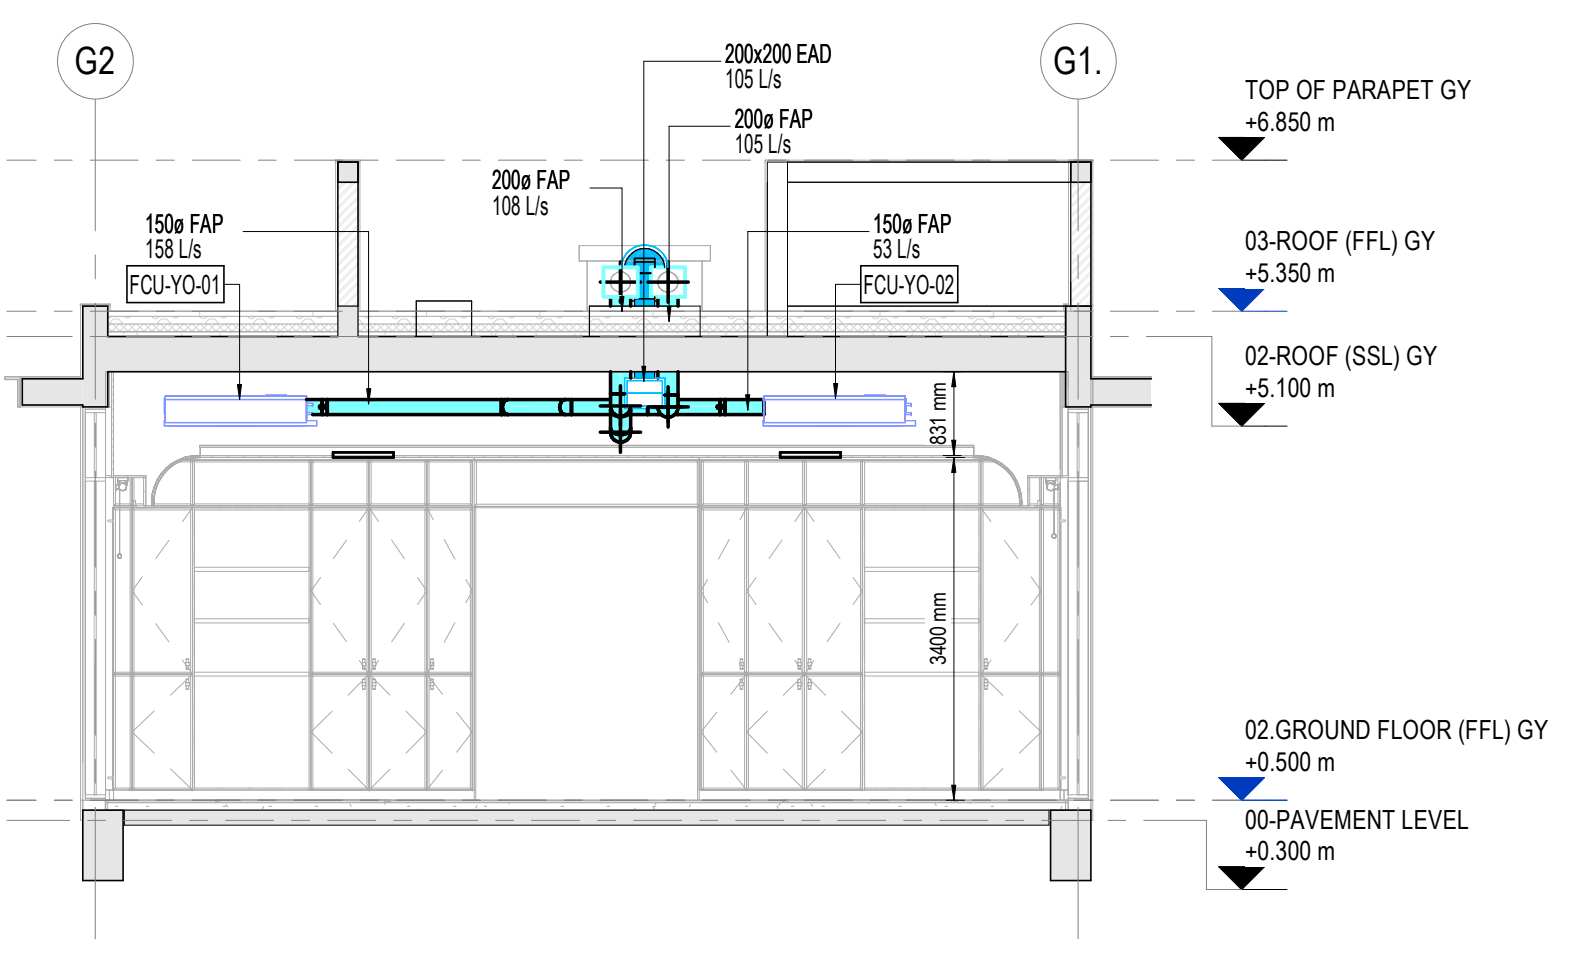

5 GYM&YOGA VENTILATION SECTION 03
1 : 75

TENDER DRAWINGS

00 10/03/2024 LSG TENDER SUBMISSION

00 16/01/2024 LSG DETAILED DESIGN SUBMISSION

00 31/10/2025 LSG SCHEMATIC DESIGN SUBMISSION

00 15/10/2025 LSG SCHEMATIC SUBMISSION-50%

00 01/09/2025 LSG CONCEPT DESIGN SUBMISSION

REVISIONS / ISSUE

THIS DRAWING MUST NOT BE REPRODUCED IN WHOLE OR IN PART WITHOUT THE PRIOR APPROVAL OF ARIF & BINTOAK

Status: TENDER SUBMISSION

Client: EMAAR

Lead Consultant: Arif & BintOak

Project Title: Proposed Residential Townhouses and Standalone Villas TH-1, TH-2, and TH-3 at Grand Polo Club & Resort, Dubai, UAE

Discipline: MECHANICAL

Drawing title: YOGA & GYM GROUND & FIRST FLOOR VENTILATION LAYOUT

Architectural Engineer: MUSTAFA ABID

Electrical Engineer: MARWAN MOHD.

Structural Engineer: RIHAM RAMADAN

Registration # 5847

Registration # 80102

Registration # 105892

Scale(s): As indicated

Date: 10/03/2026

Project no: 1857

Drawn by: LSG

Checked: MAV

Approved: MRM

Drawing Number: GPCR-TH02-AB-DRG-ZZZ-MEC-HV-2400-00