




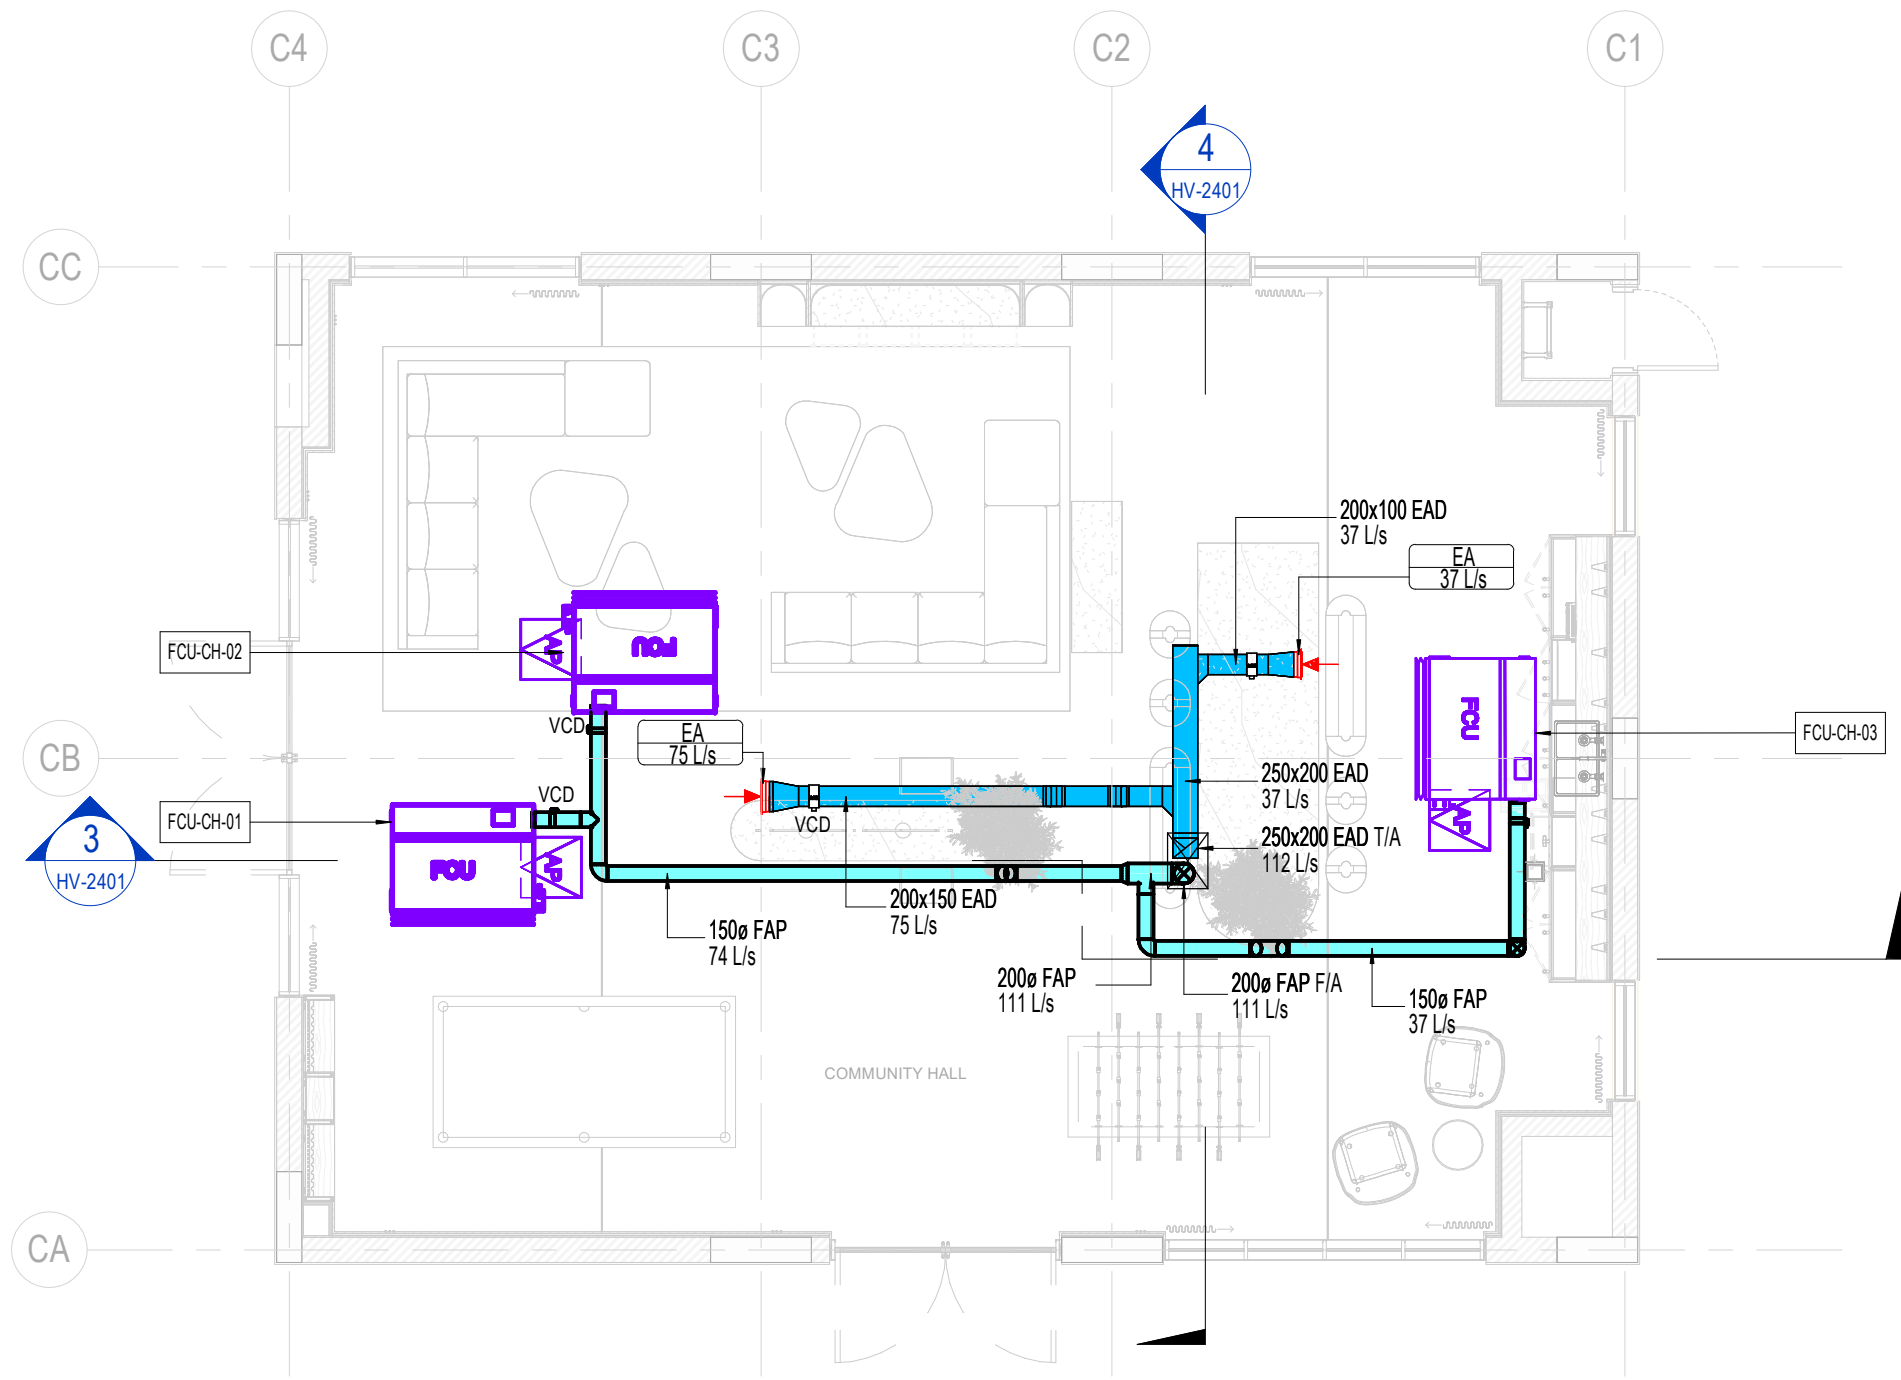


1 GROUND FLOOR VENTILATION LAYOUT-COMMUNITY HALL
1 : 75

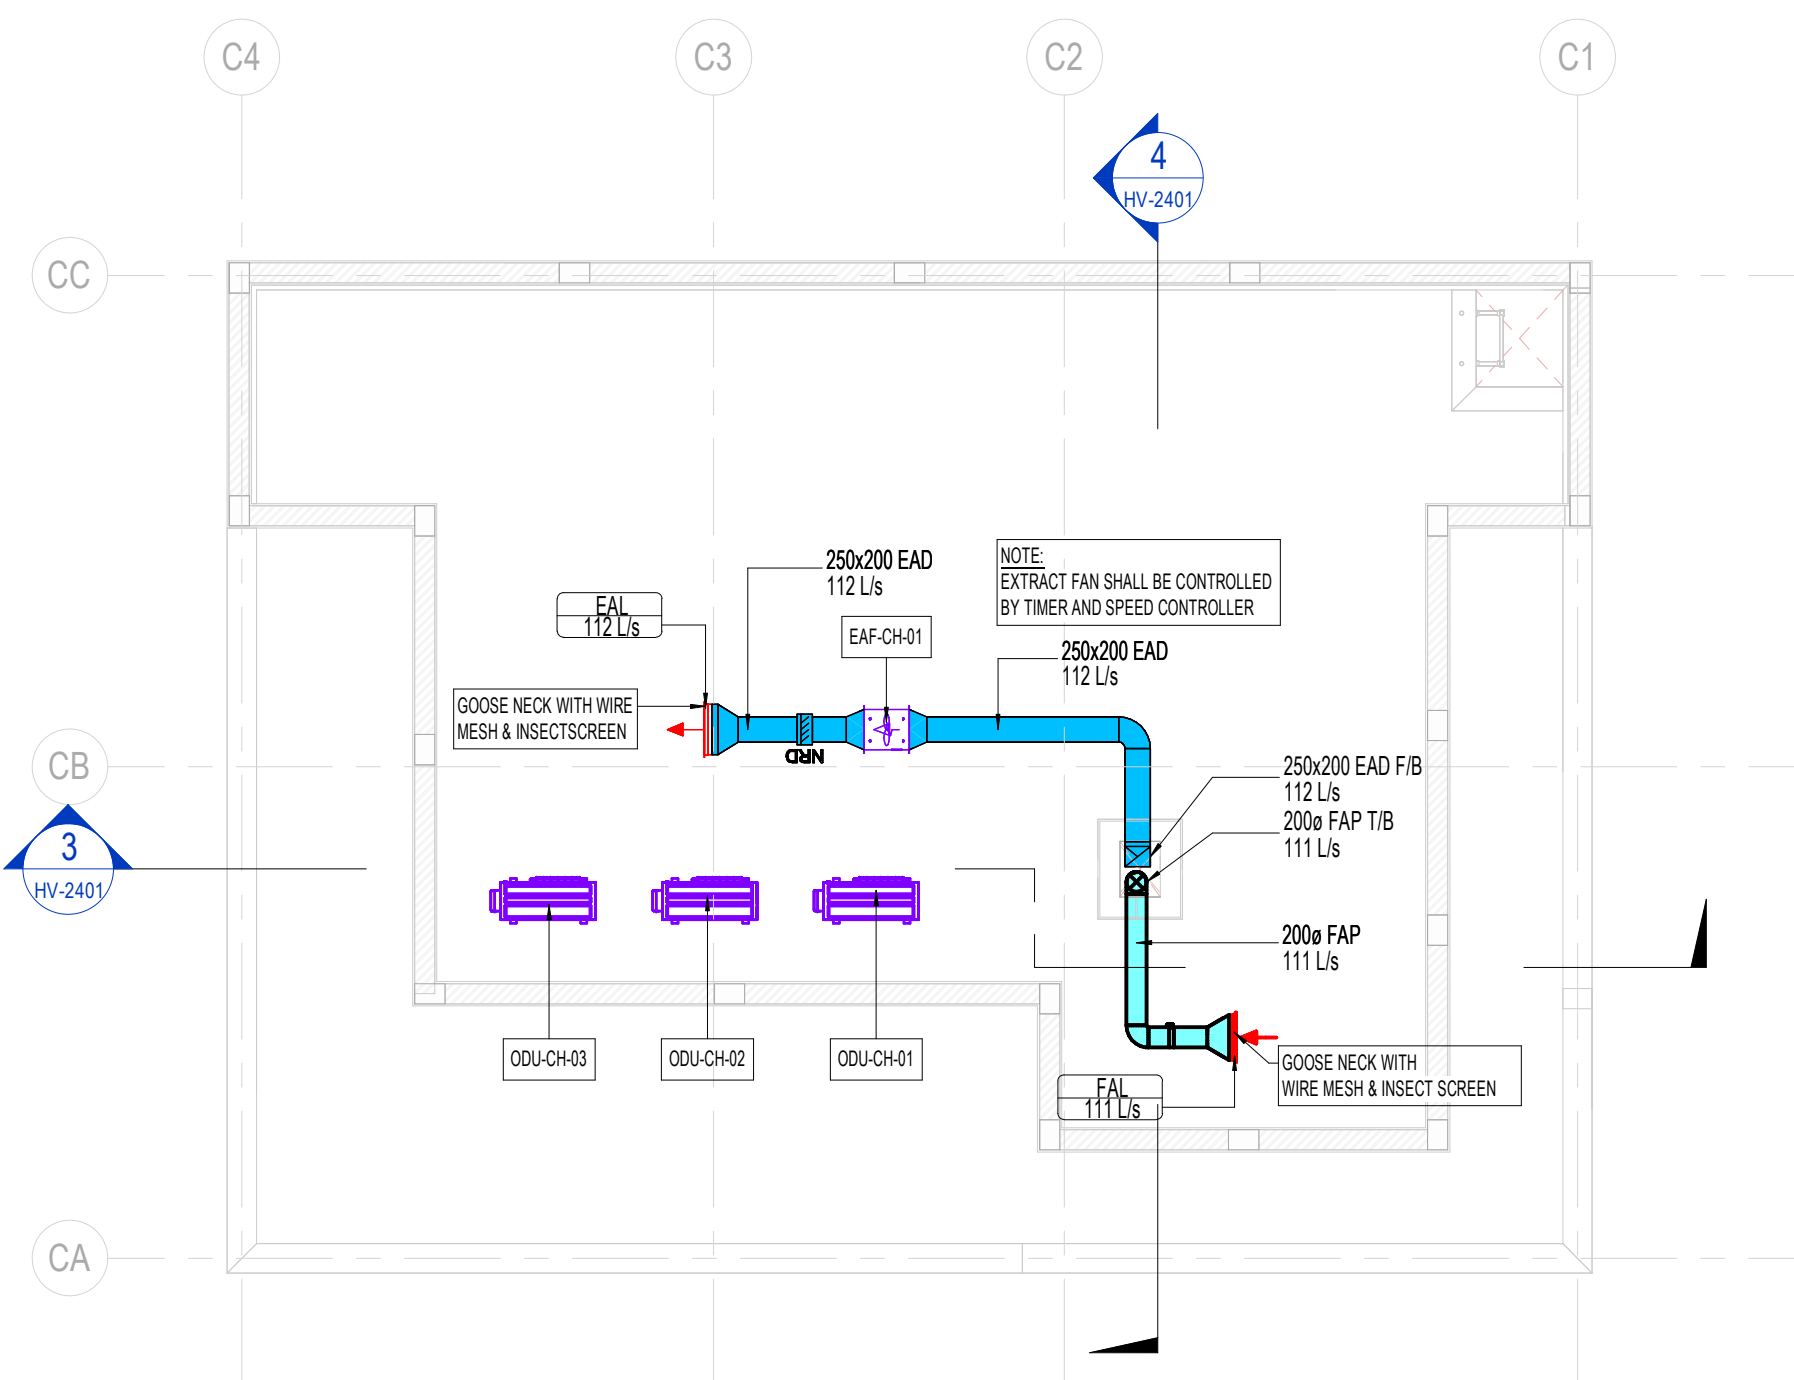


2 ROOF FLOOR VENTILATION LAYOUT-COMMUNITY HALL
1 : 75

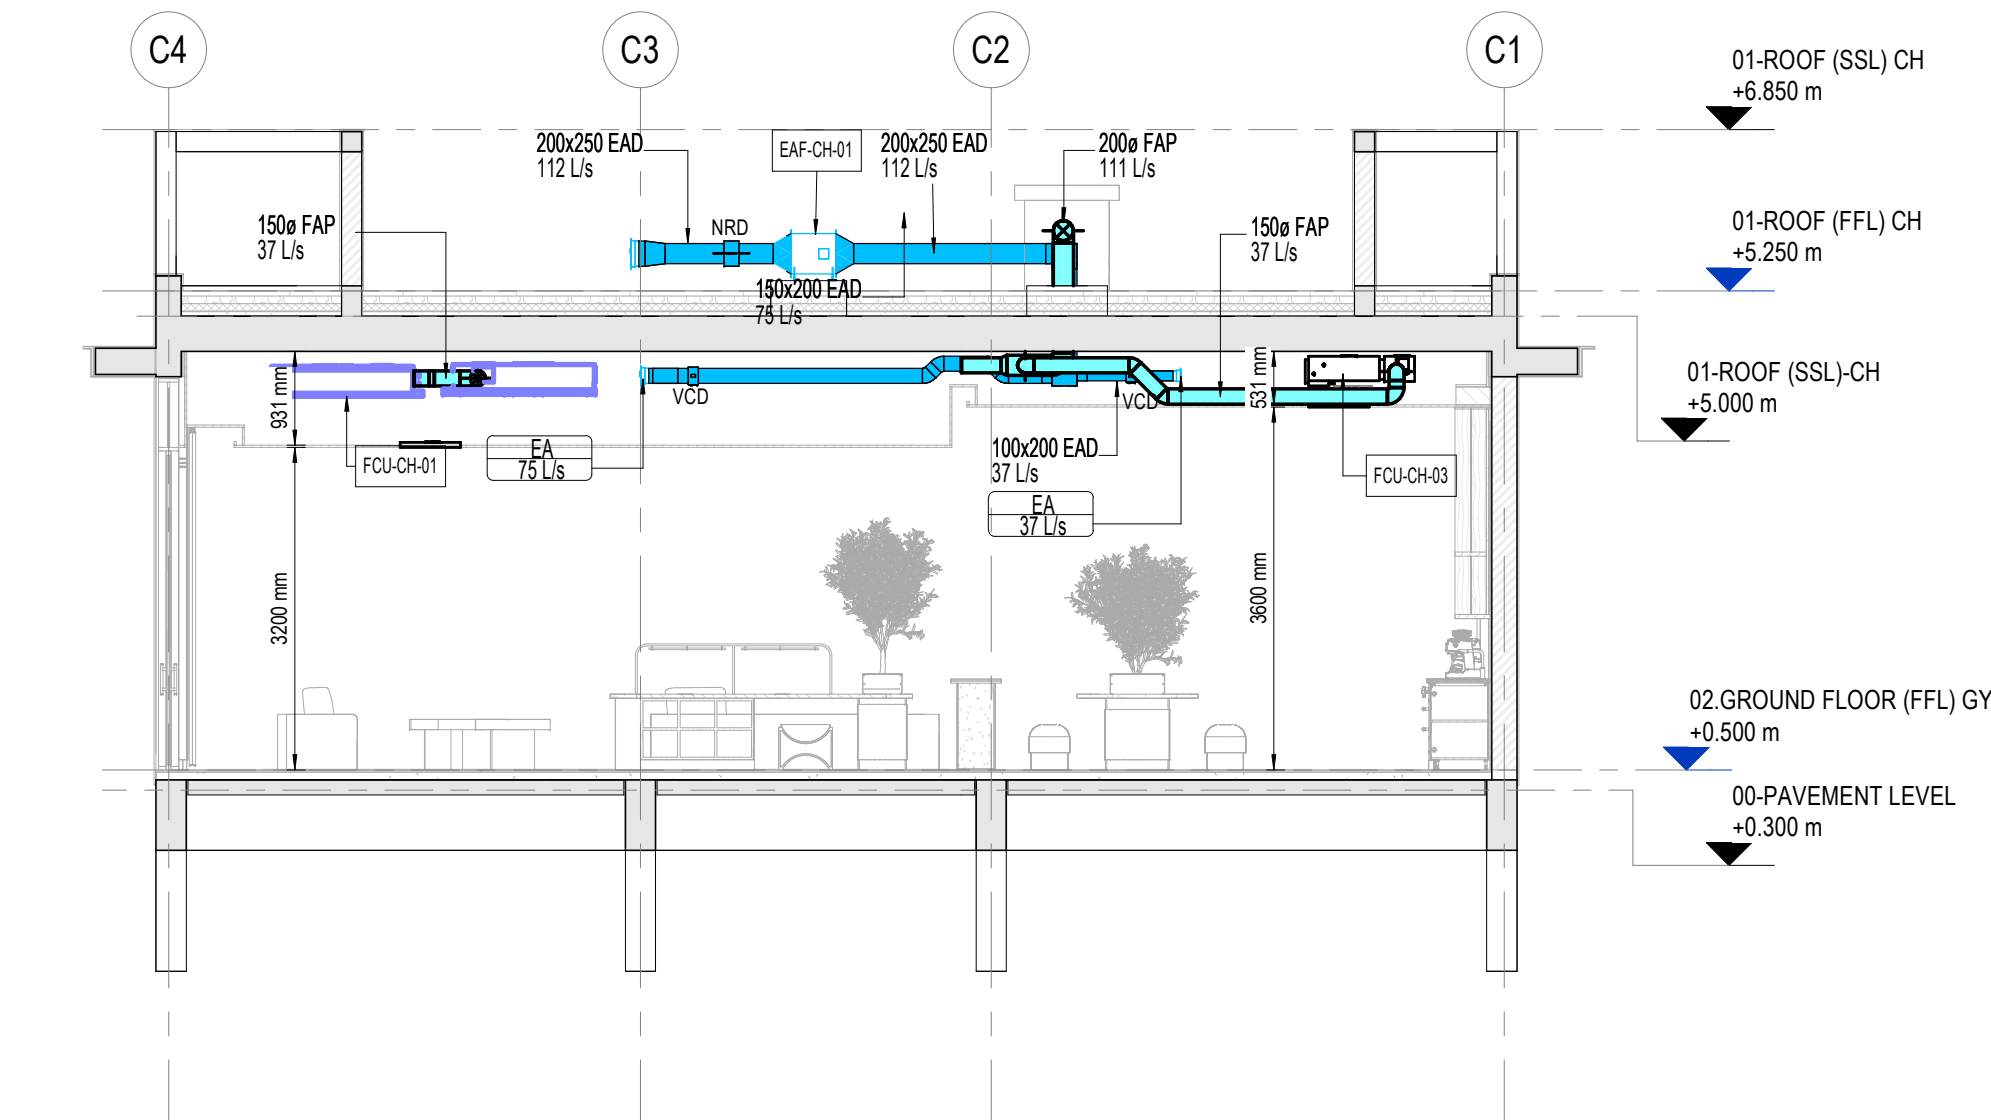

3 COMMUNITY HALL VENTILATION SECTION 01
1 : 75

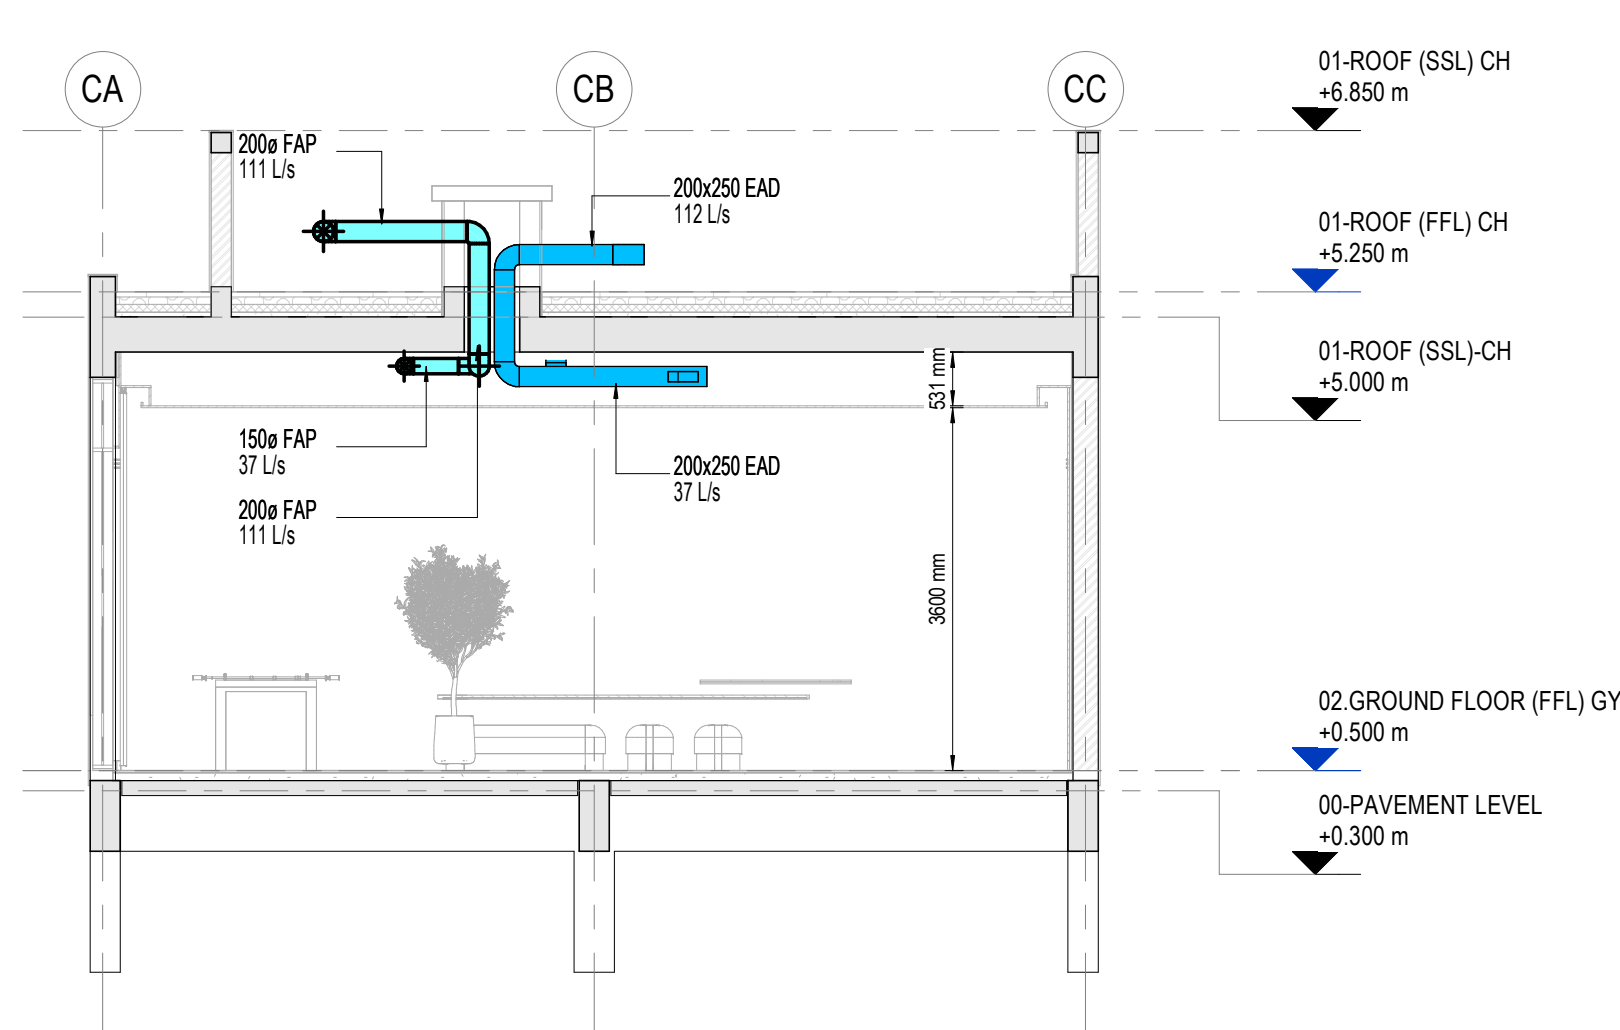


4 COMMUNITY HALL VENTILATION SECTION 02
1 : 75

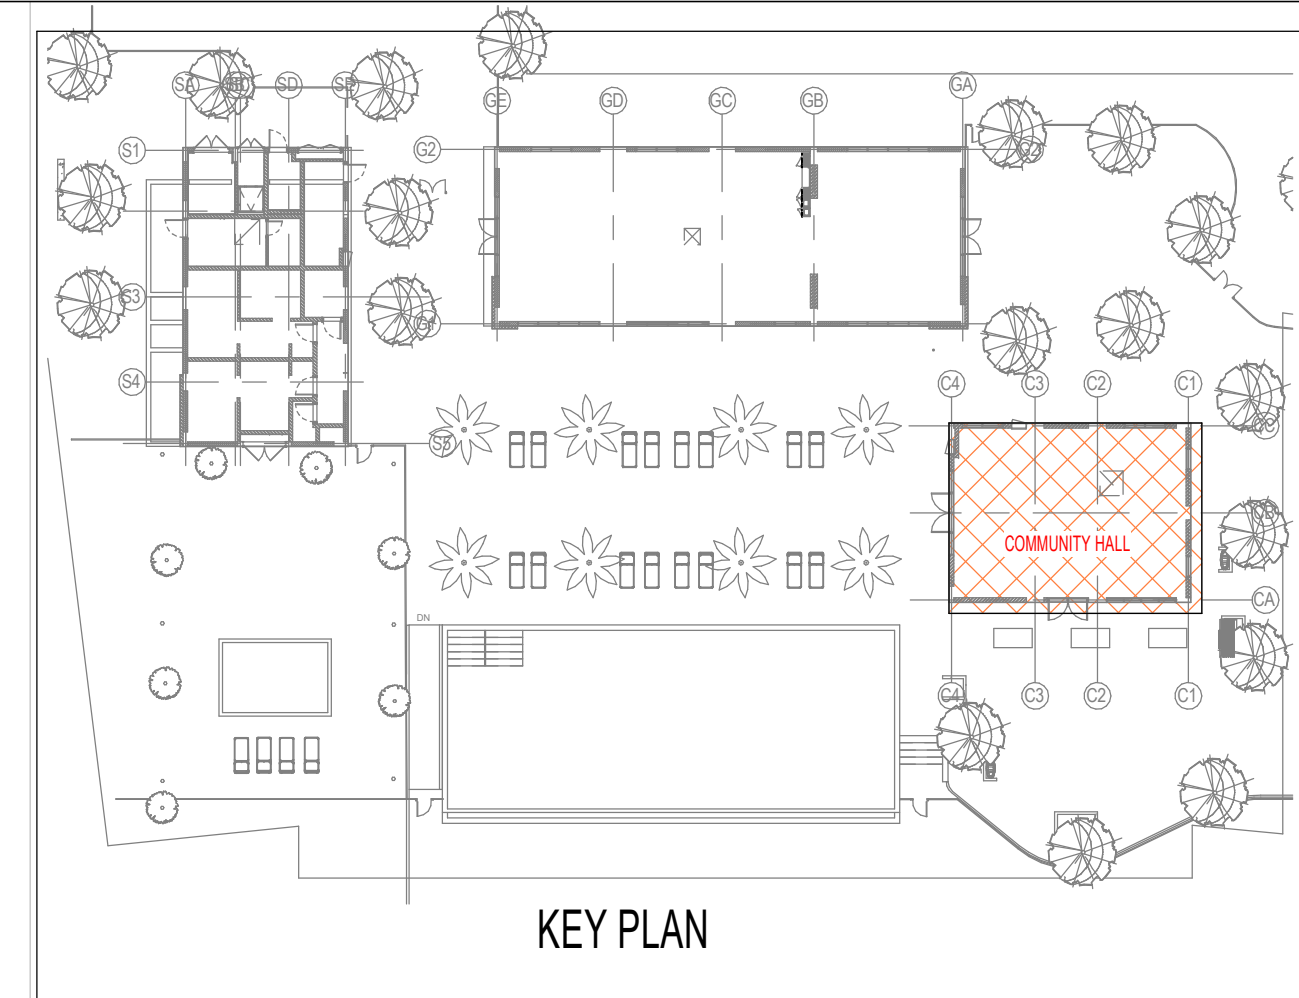

Key Plan

General Notes :

01. Do not Scale The Drawings. Follow (The MM) Written Dimensions Unless Otherwise Mentioned.
02. Each Drawing Shall be Read in Conjunction With all Other Drawings Specification & the General Standard Details. In Case of Any Discrepancies Bring it to the Knowledge of Engineer and Same to be Resolved Prior to Execution of Work.
03. Dimensions Shown on These Drawings are Structural Dimensions. Unless Noted Otherwise.
04. All Levels Indicated On These Drawings are Levels as per the Survey Datum, Same Should be Verified at Site Prior to Execution of Work.
05. All Levels Indicated On These Drawings are Based On Design Level, Which is Equivalent to Datum Level and Same Should be Verified at Site Prior to Execution of Work.

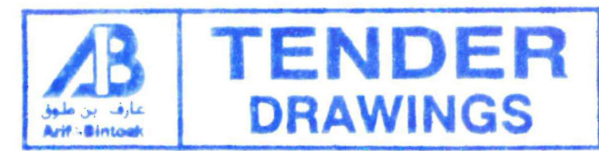

00	10/03/2024	LSG	TENDER SUBMISSION
00	16/01/2024	LSG	DETAILED DESIGN SUBMISSION
00	31/10/2025	LSG	SCHEMATIC DESIGN SUBMISSION
00	15/10/2025	LSG	SCHEMATIC SUBMISSION-50%
00	01/09/2025	LSG	CONCEPT DESIGN SUBMISSION
No.	Date	Initials	Description
REVISIONS / ISSUE			
THIS DRAWING MUST NOT BE REPRODUCED IN WHOLE OR IN PART WITHOUT THE PRIOR APPROVAL OF ARIF & BINTOAK			
Status			
TENDER SUBMISSION			
Client			
EMAAR			
Lead Consultant			
 اريف وبن طوق Arif & Bintook consulting architects & engineers POST BOX 5070 DUBAI, UAE TEL: 04-3372886 FAX: 04-3372832 POST BOX 5081 ABU DHABI, UAE TEL: 02-4546651 arif@arifbintook.ae			
Project Title:			
Proposed Residential Townhouses and Standalone Villas TH-1, TH-2, and TH-3 at Grand Polo Club & Resort, Dubai, UAE			
Discipline:			
MECHANICAL			
Drawing title:			
COMMUNITY HALL GROUND & FIRST FLOOR VENTILATION LAYOUT			
Architectural Engineer	Electrical Engineer	Structural Engineer	
MUSTAFA ABID	MARWAN MOHD.	RIHAM RAMADAN	
Registration # 5847	Registration # 80102	Registration # 105892	
Scale(s):	Date:	Project no:	
As indicated	10/03/2026	1857	
Drawn by:	Checked:	Approved:	
LSG	MAV	MRM	
Drawing Number:		GPCR-TH02-AB-DRG-ZZZ-MEC-HV-2401-00	