




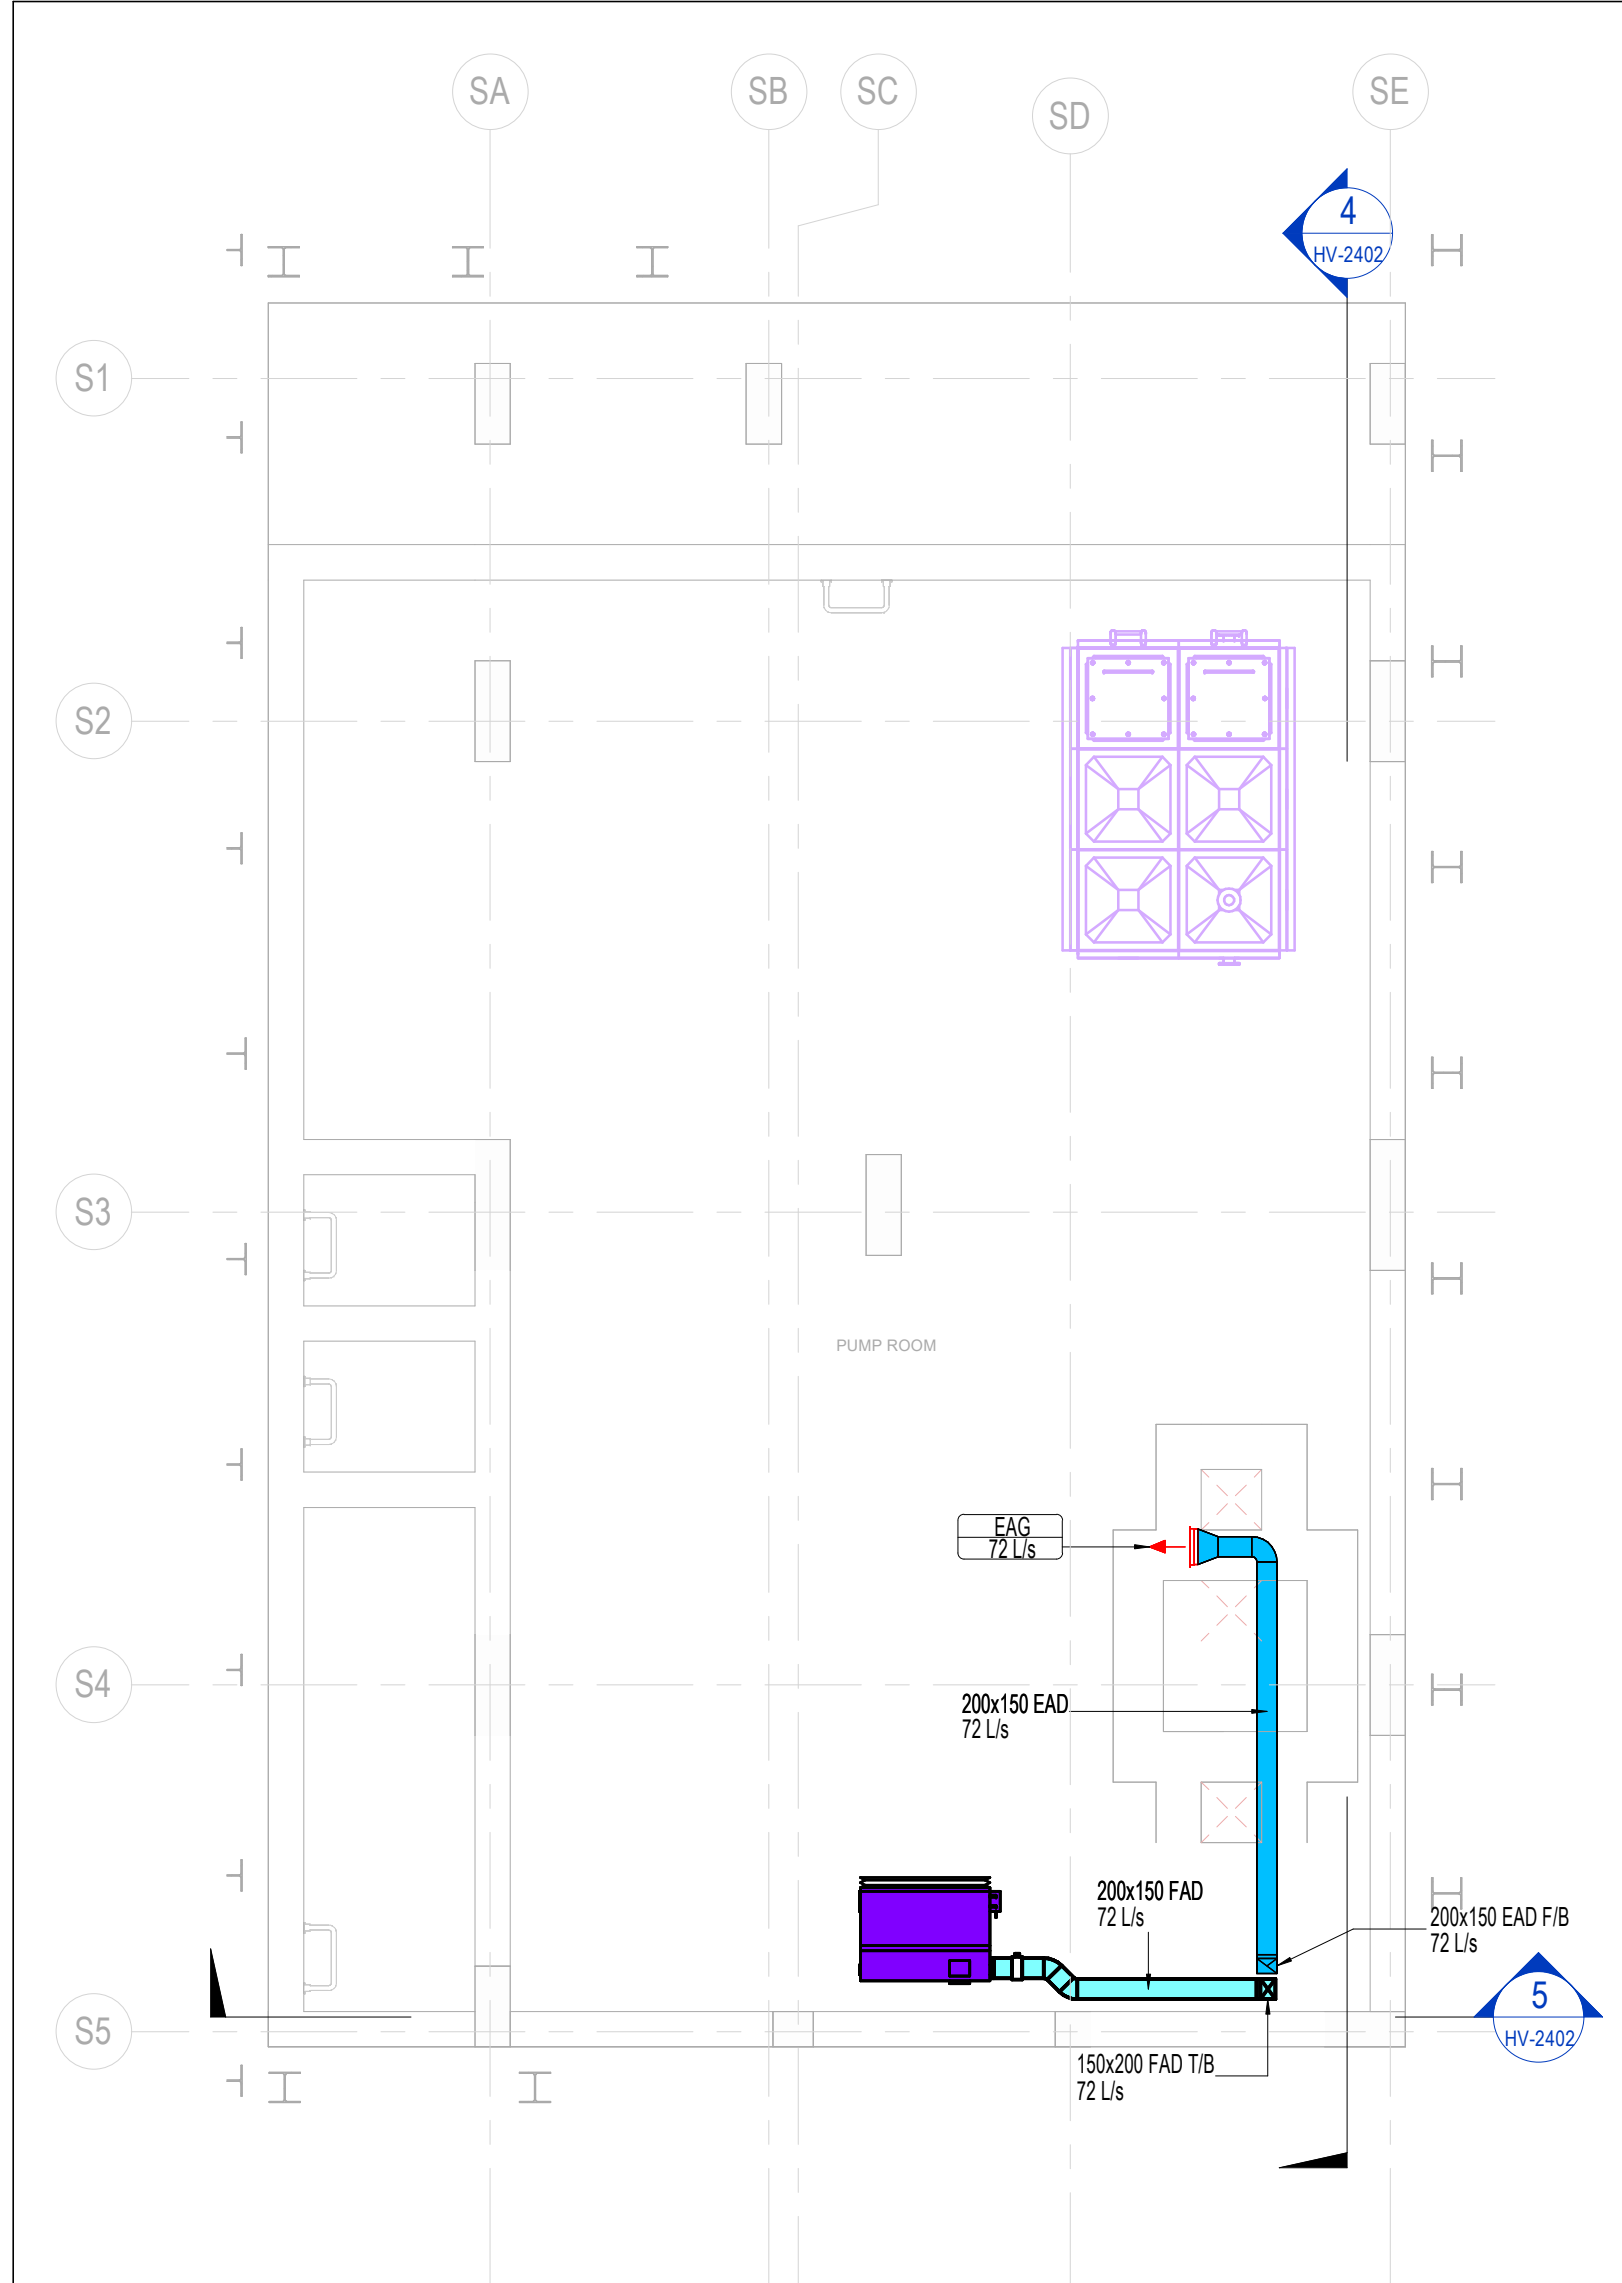


1 BASEMENT FLOOR VENTILATION LAYOUT
1 : 75

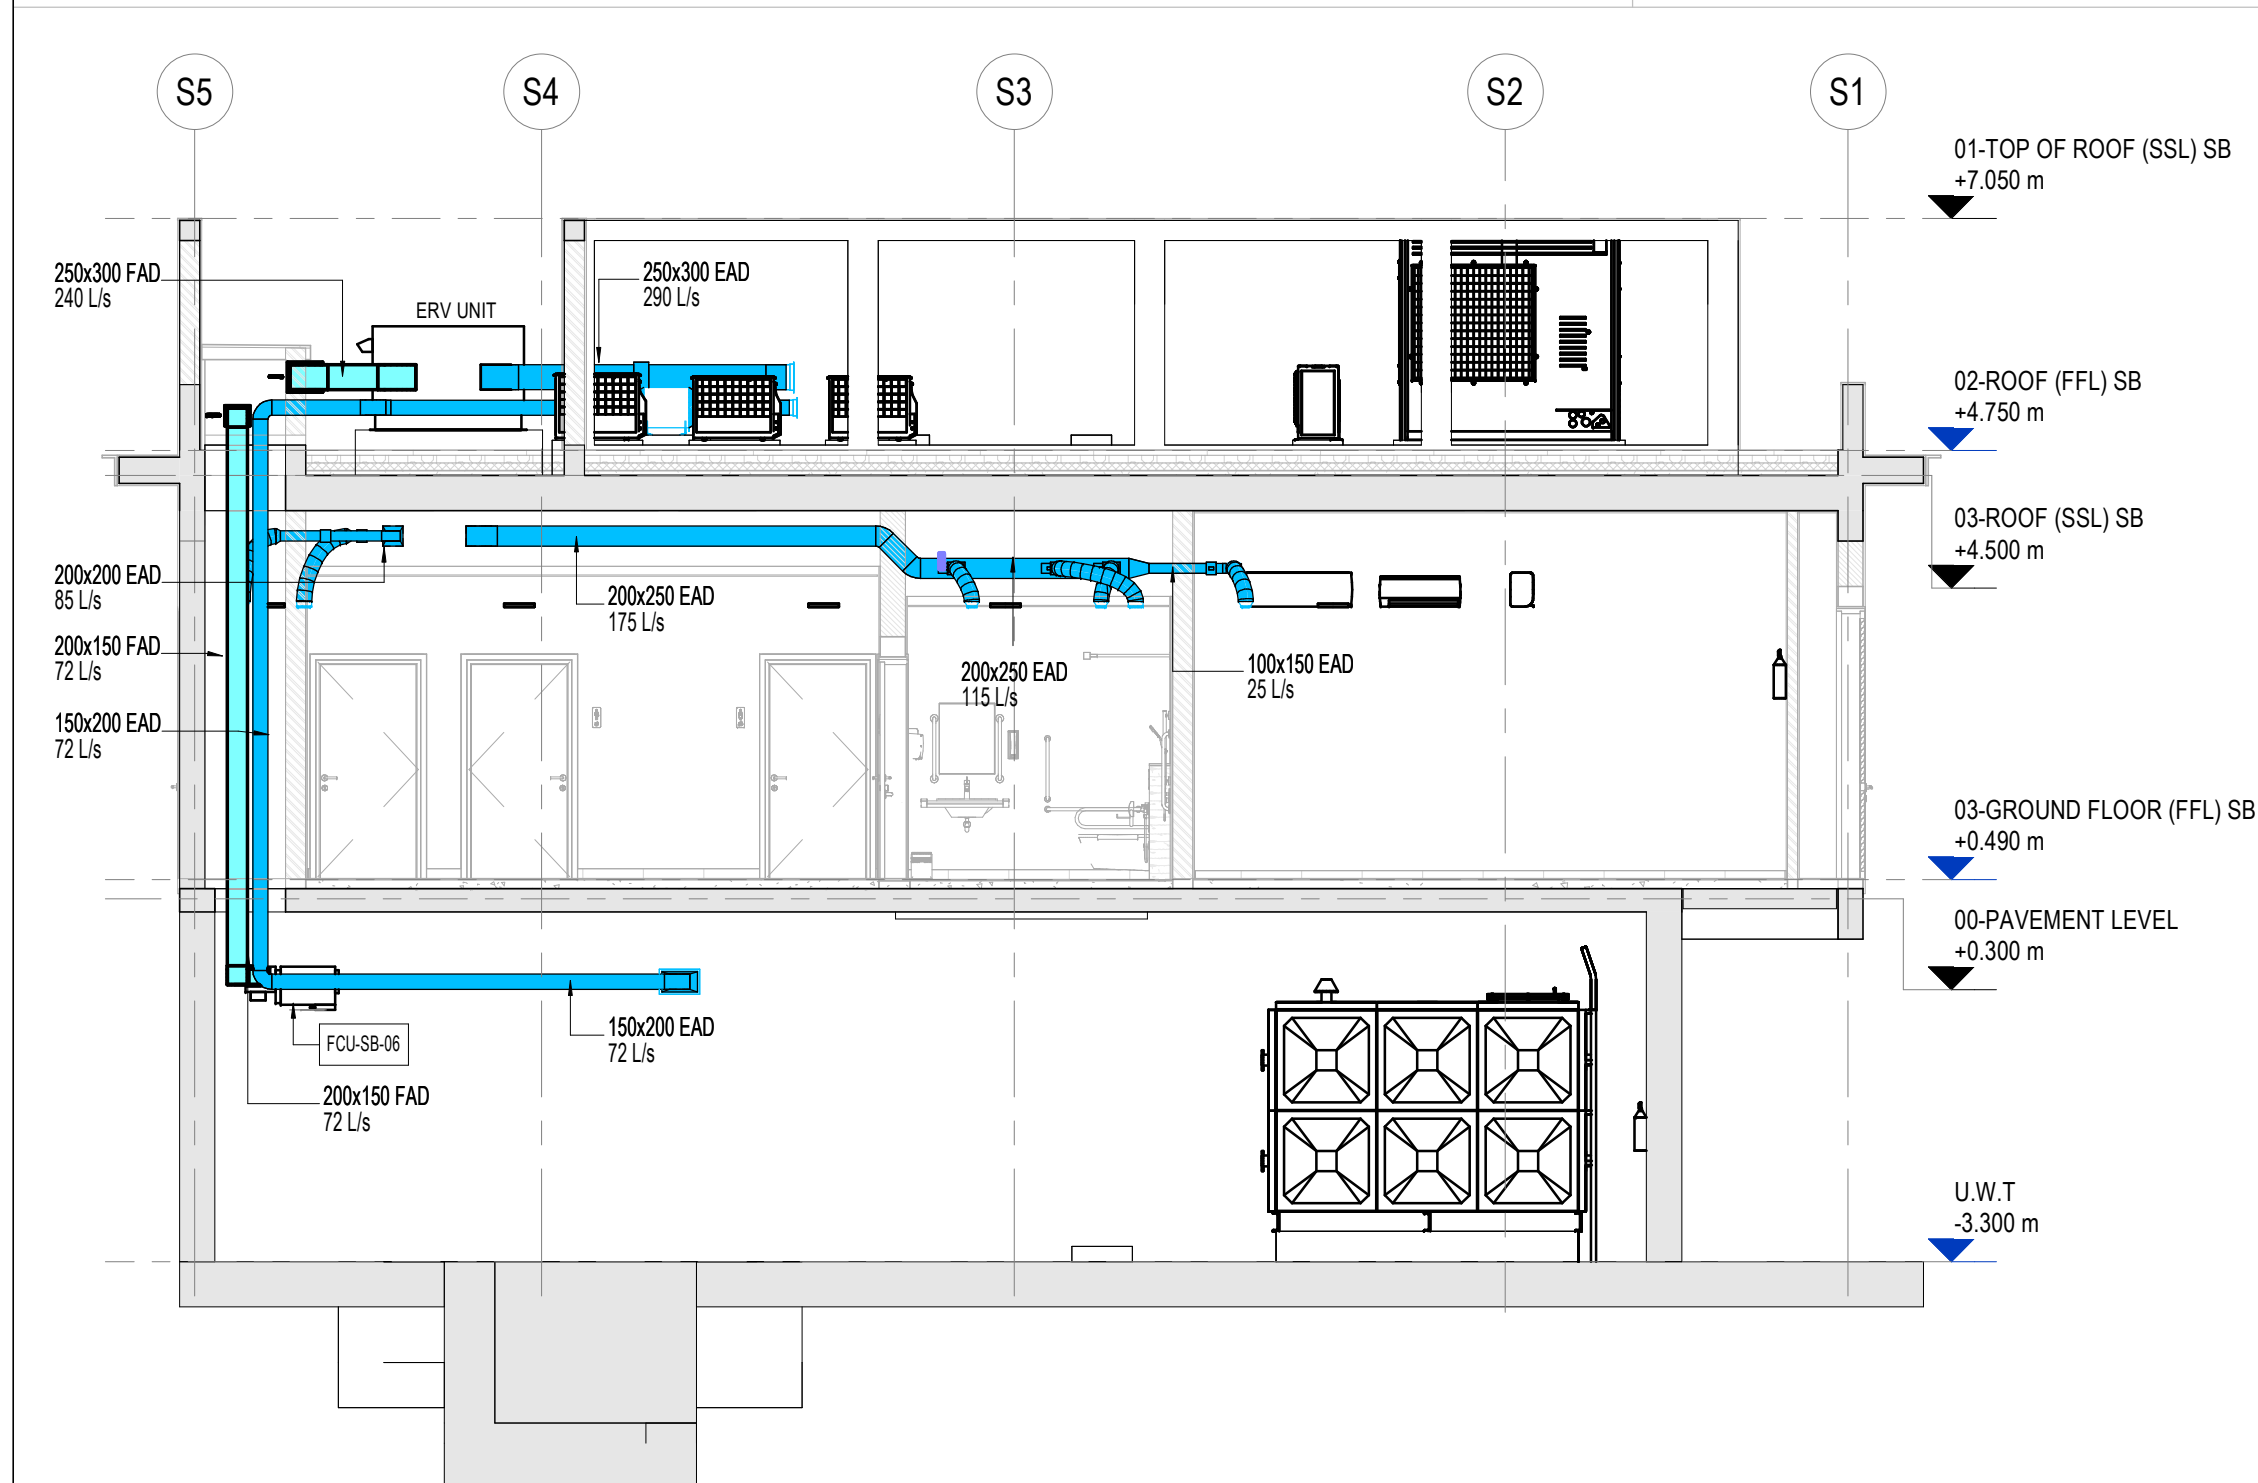


4 SERVICE BLOCK VENTILATION SECTION 01
1 : 75

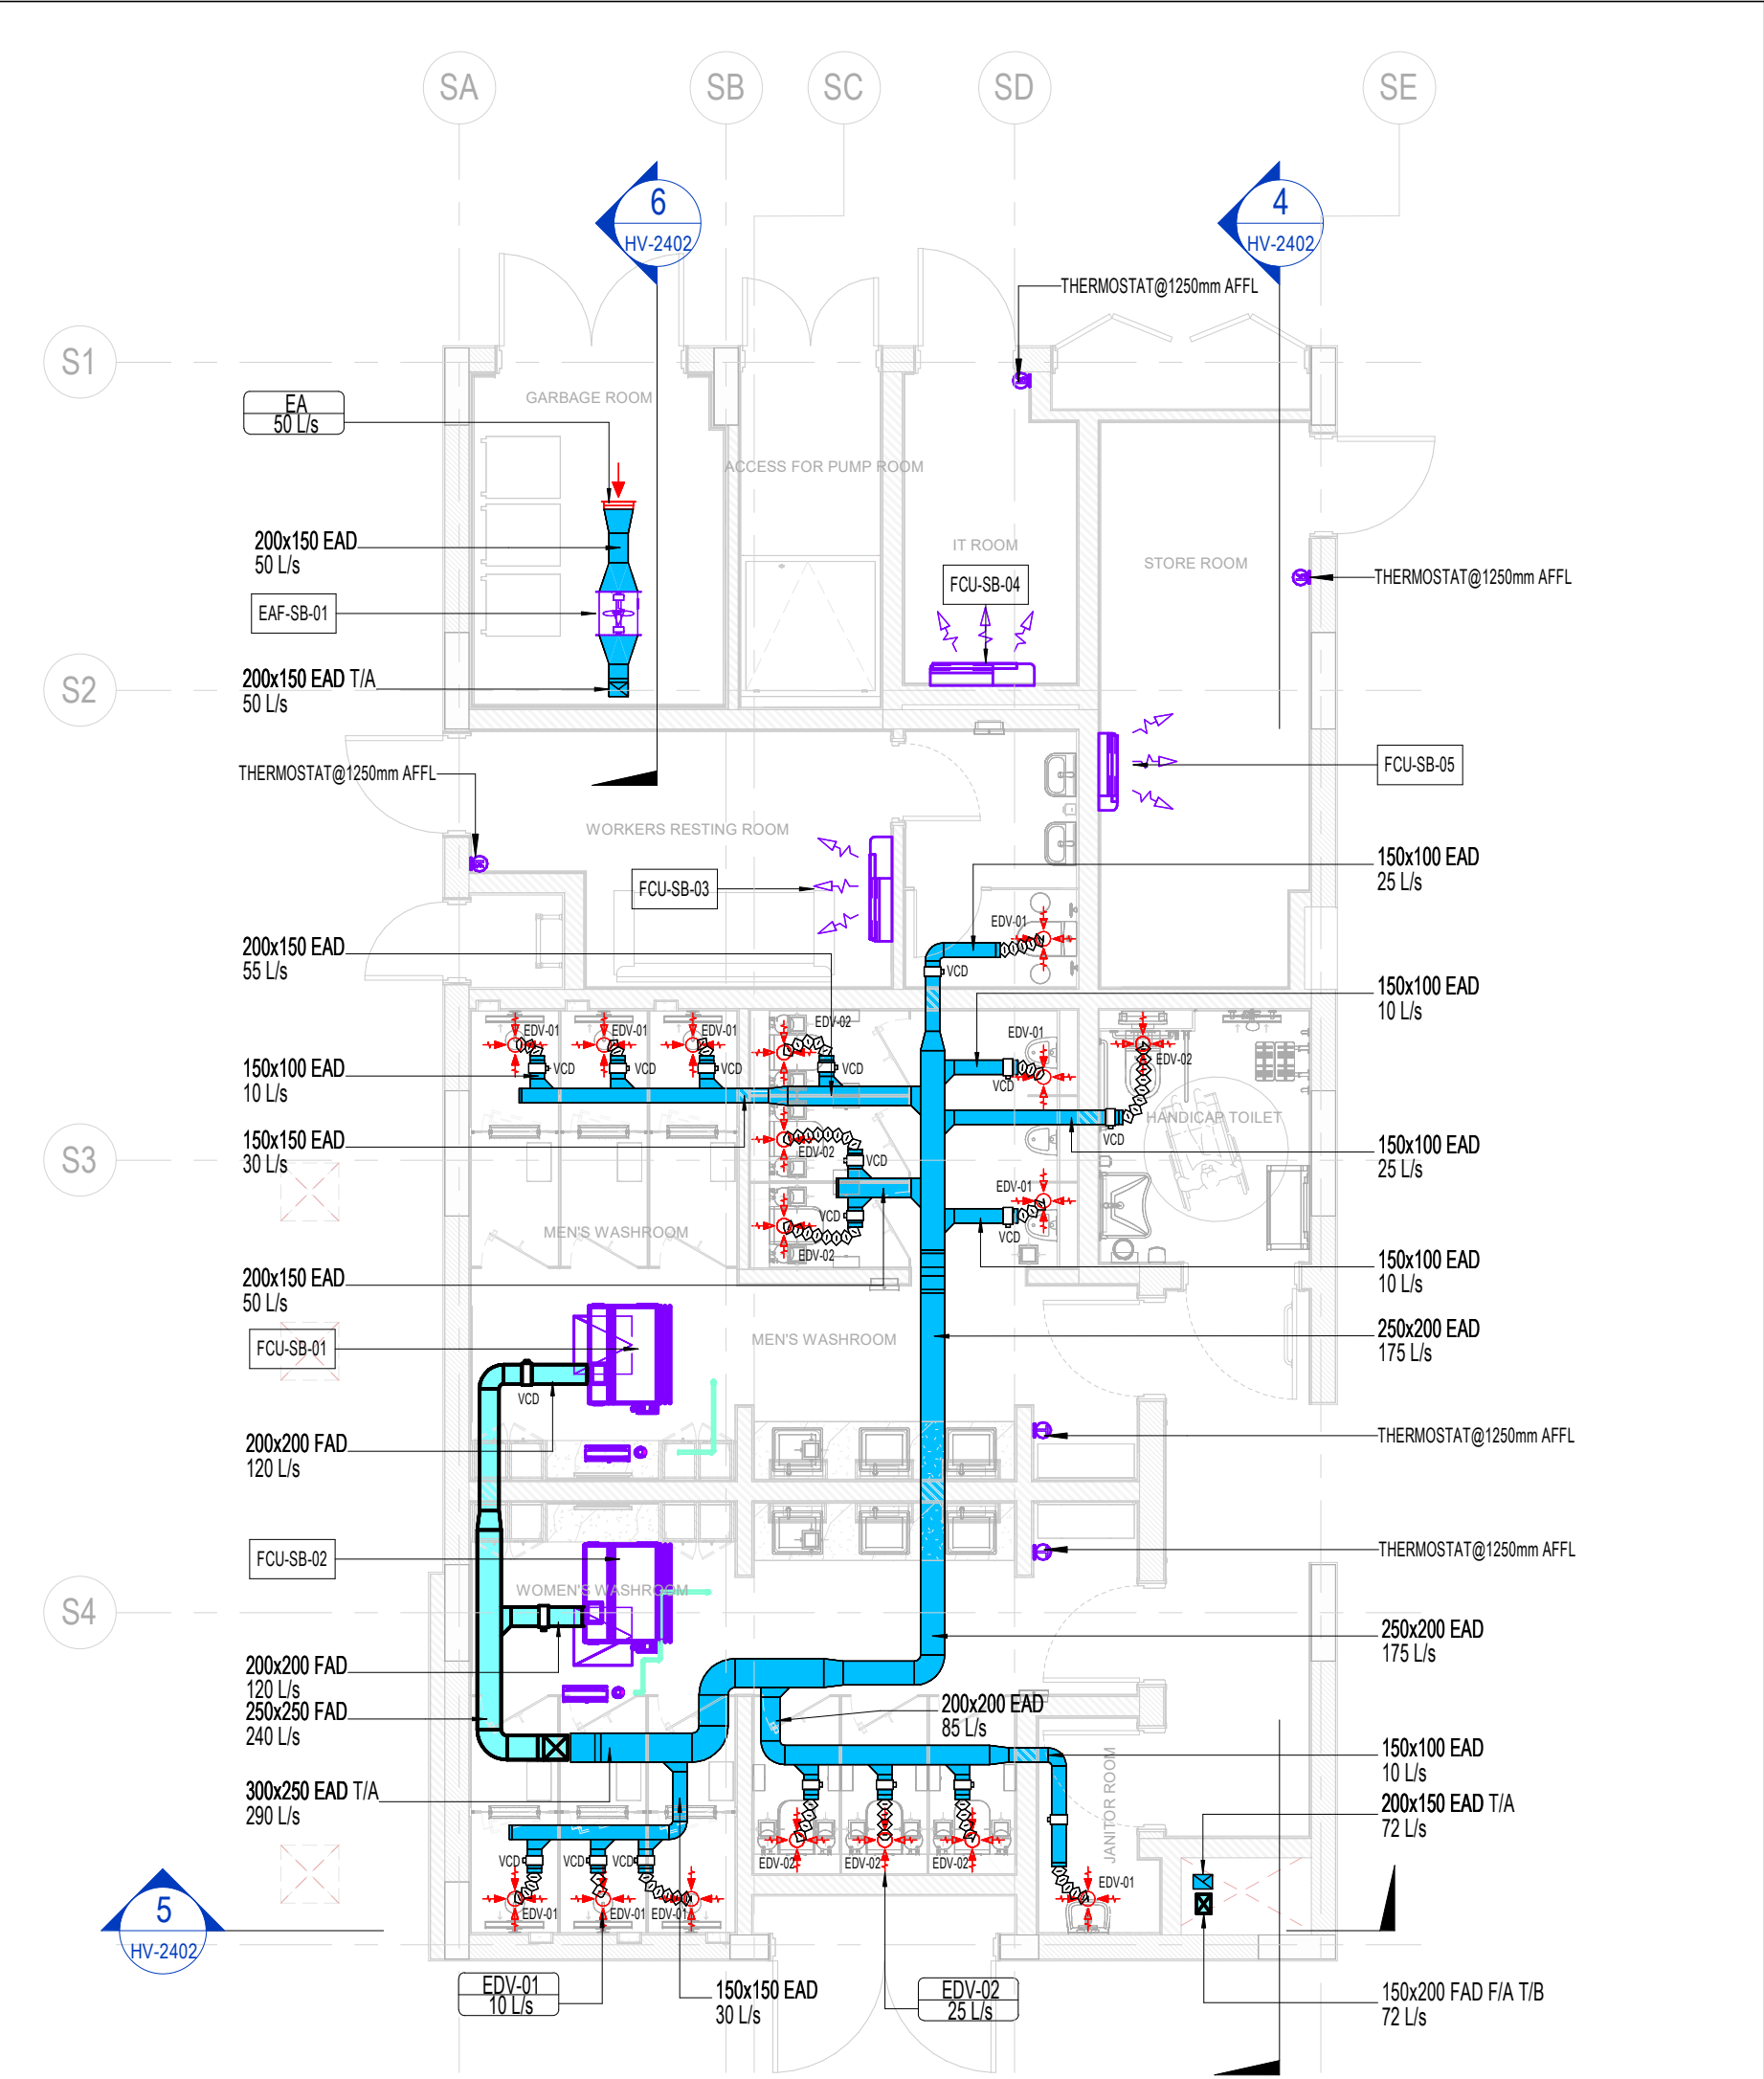

2 GROUND FLOOR VENTILATION LAYOUT-SERVICE BLOCK
1 : 75

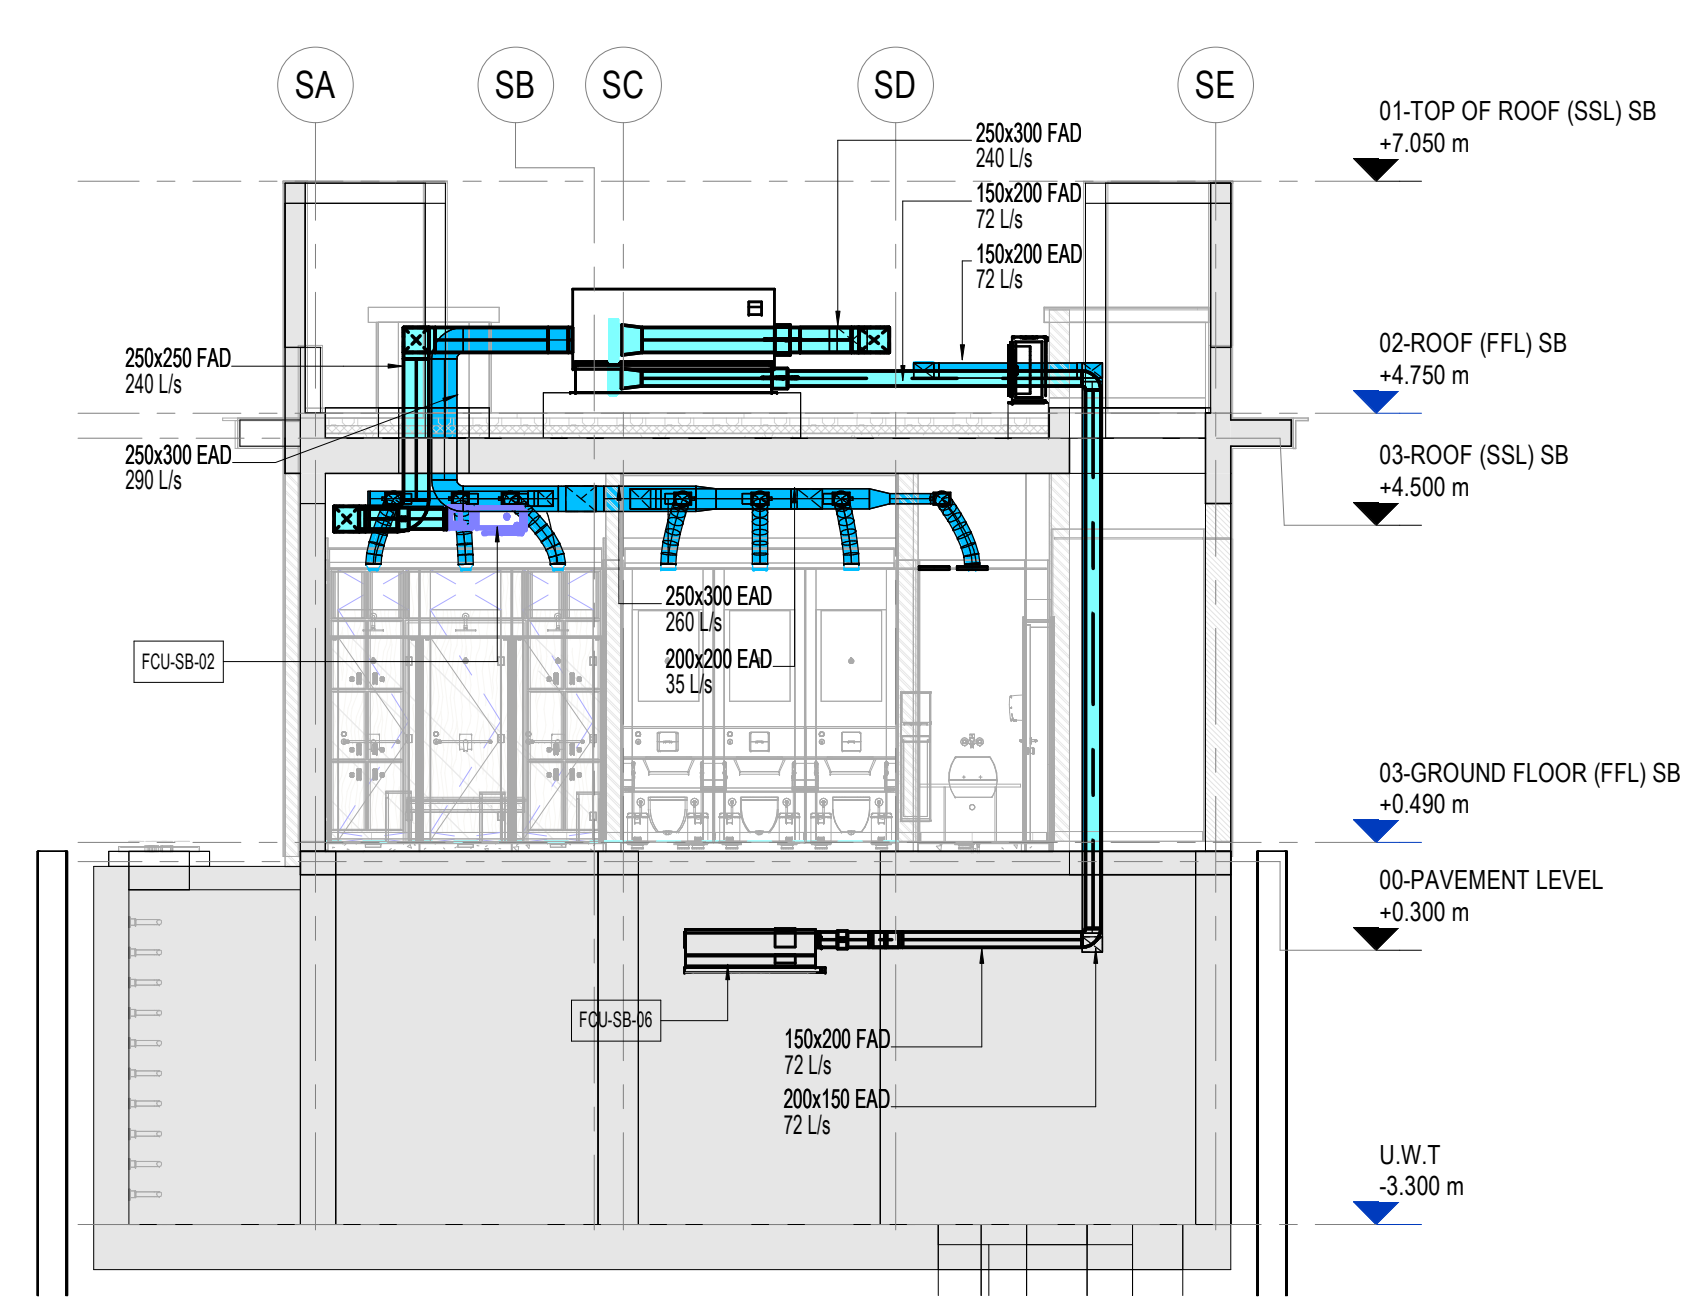


5 SERVICE BLOCK VENTILATION SECTION 02
1 : 75

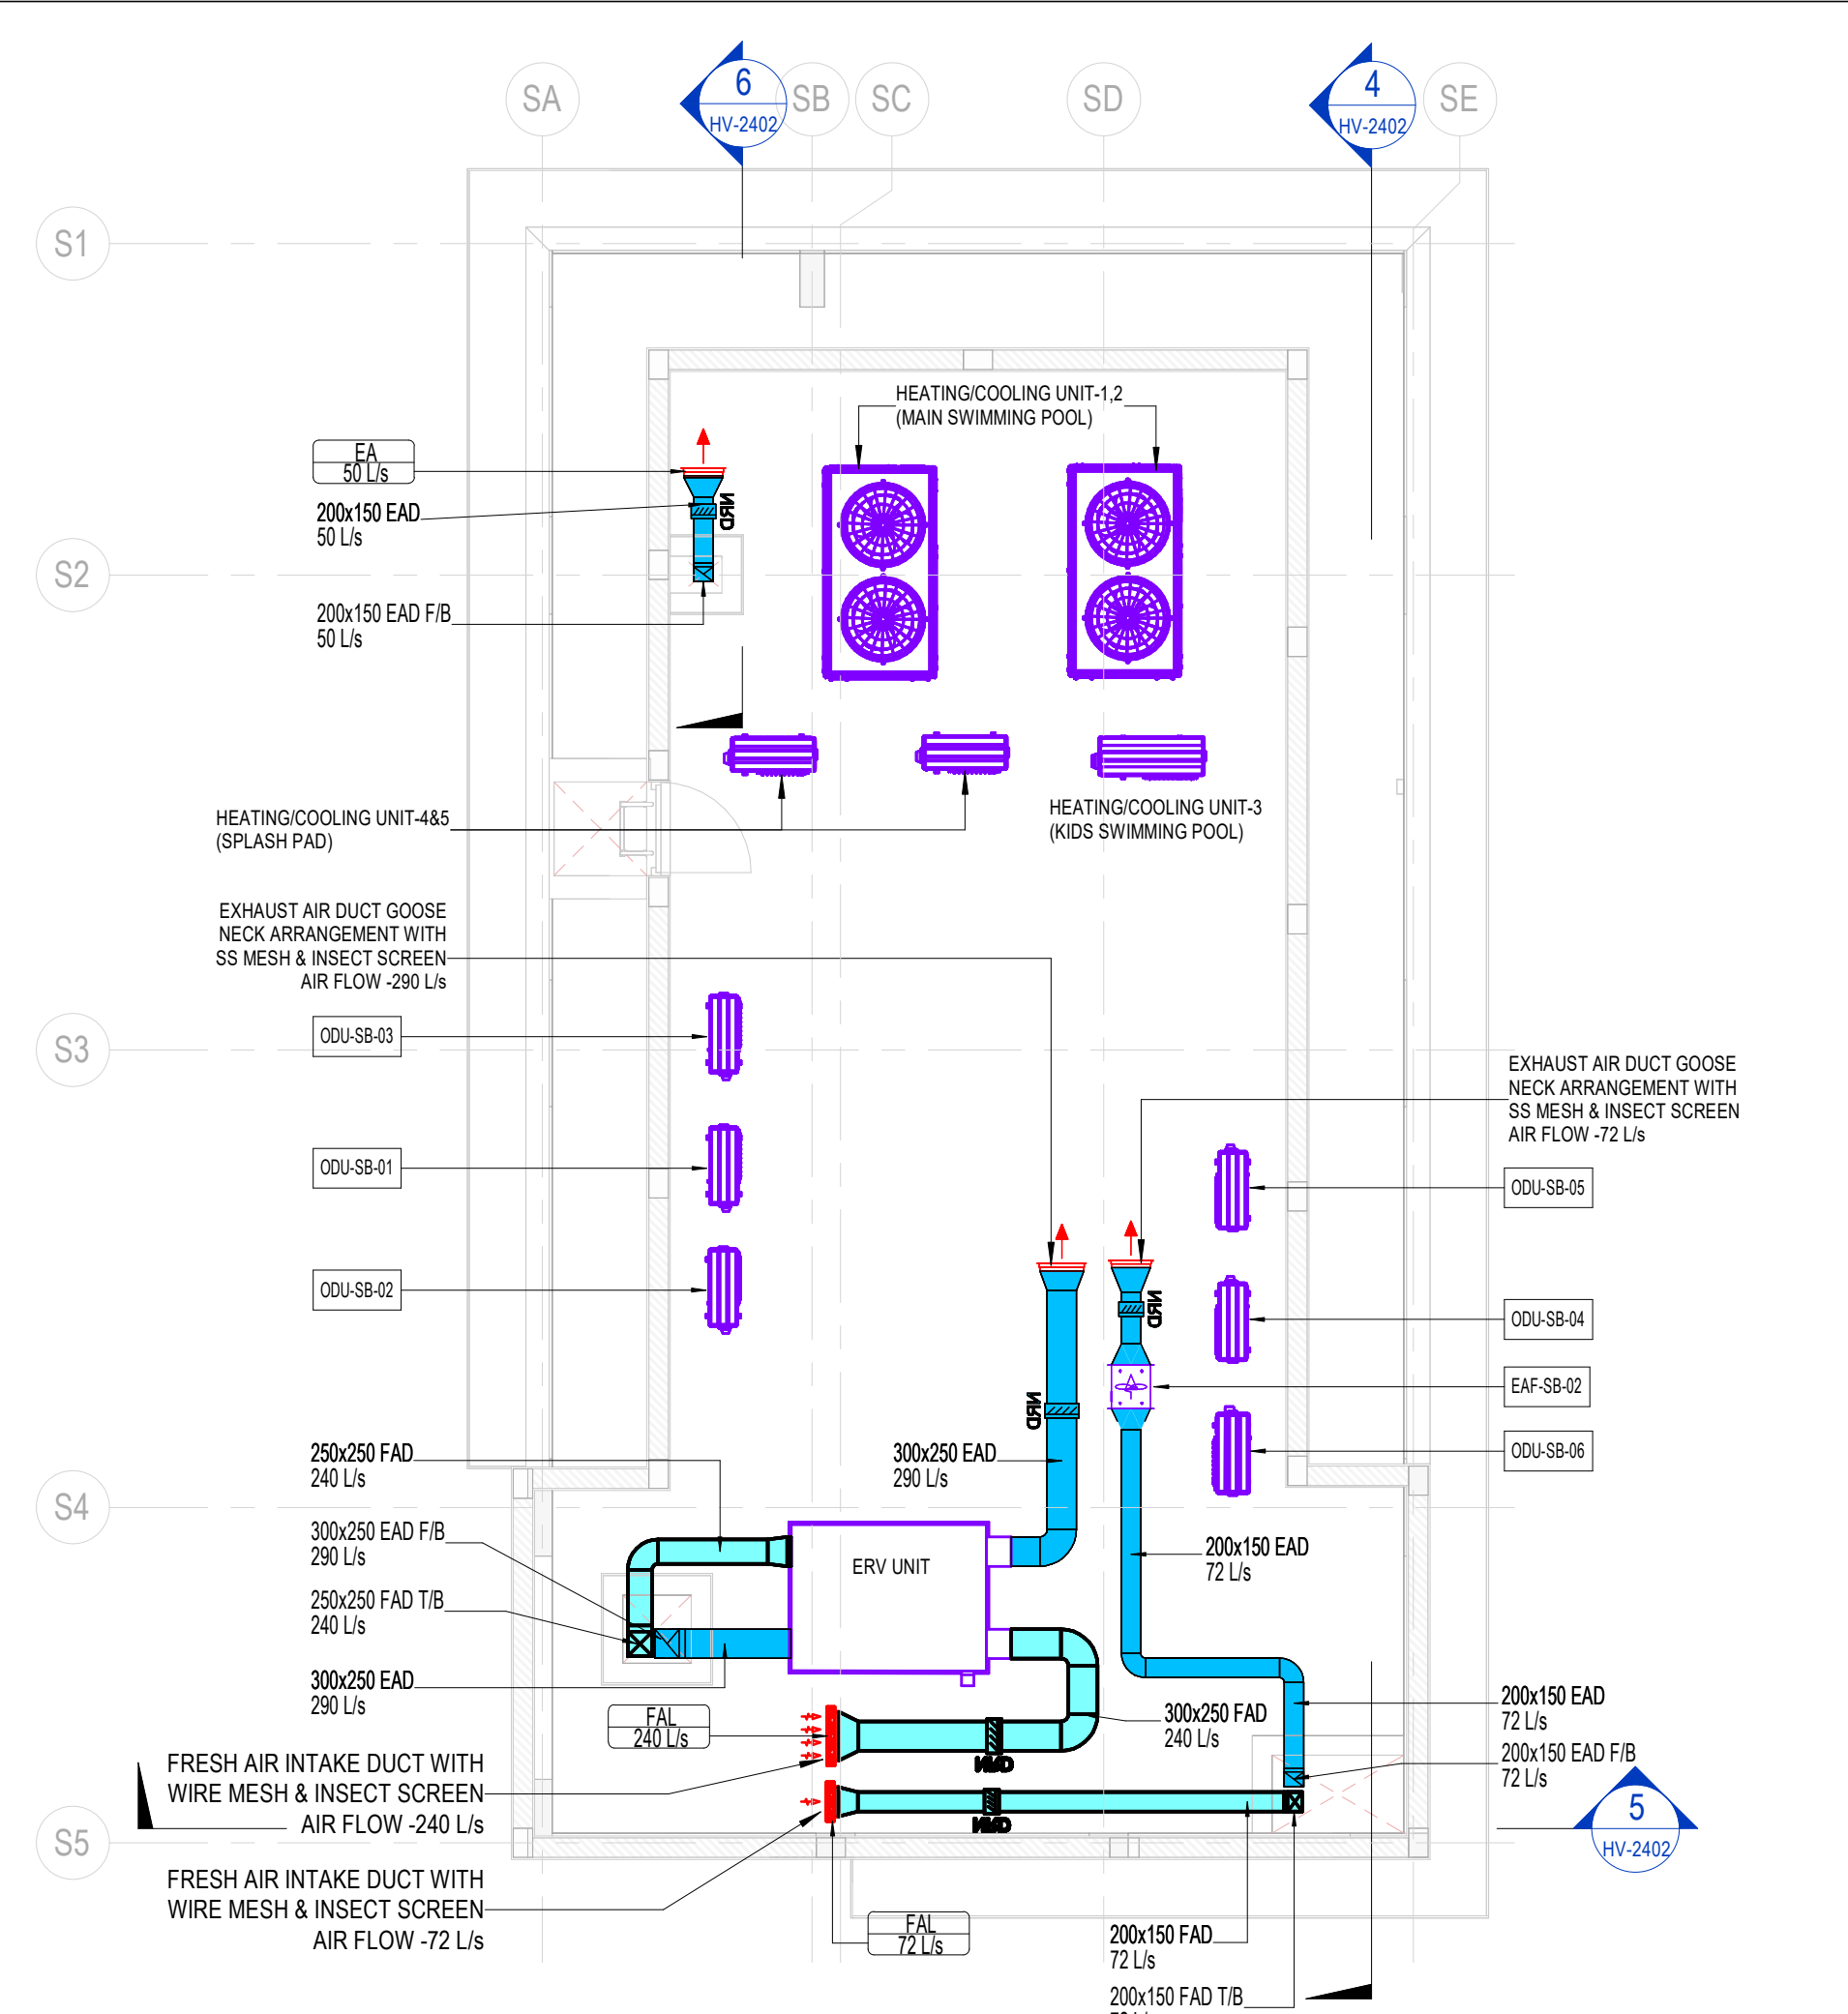


3 ROOF FLOOR VENTILATION LAYOUT-SERVICE BLOCK
1 : 75

EXTRACT DISC VALVE SCHEDULE			
UNIT NO.	DESCRIPTION	AIR OUTLET SIZE (mm)	CAPACITY RANGE (LPS)
EDV-01	EXTRACT DISCVLVE	Ø 100	0 ~ 12.5 L/s
EDV-02	EXTRACT DISC. VALVE	Ø 200	12.5 ~ 25 L/s

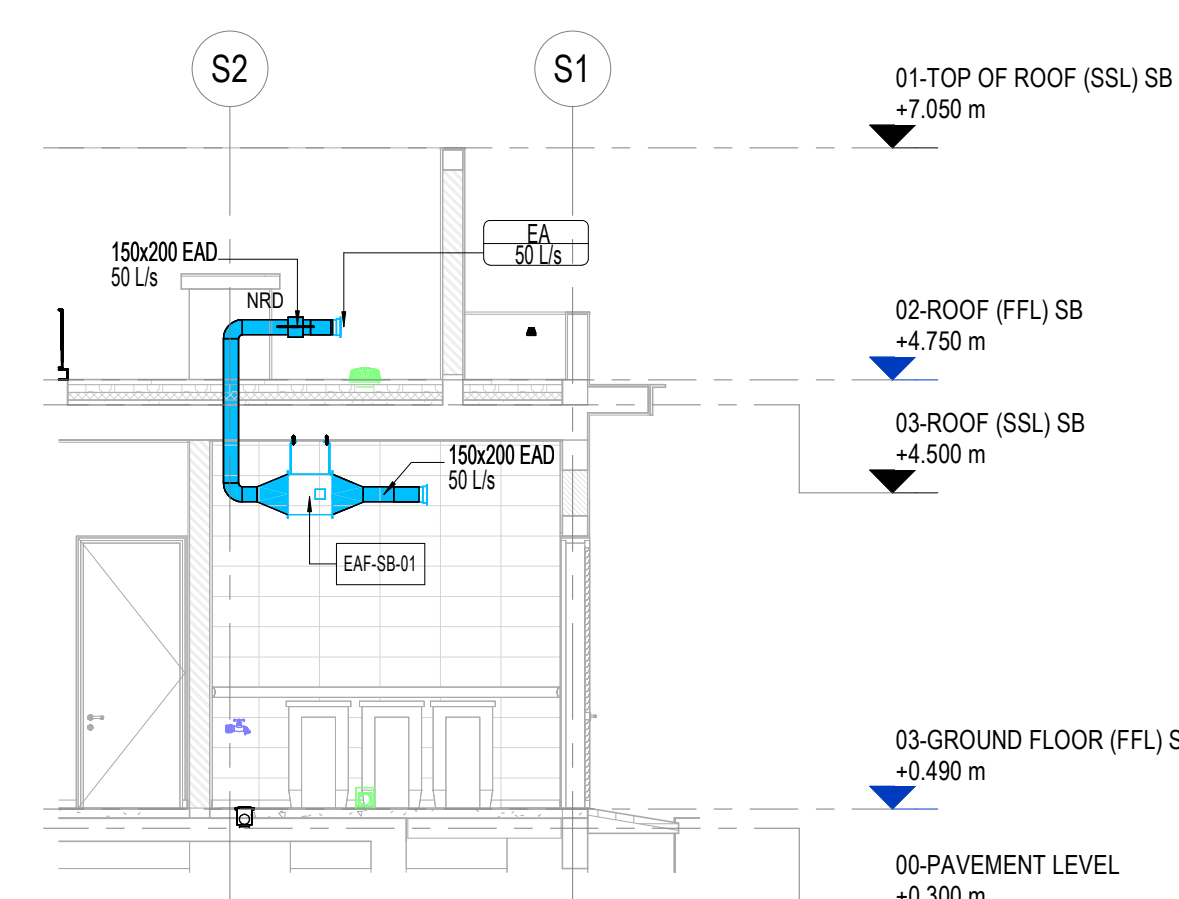

6 SERVICE BLOCK VENTILATION SECTION 03
1 : 75

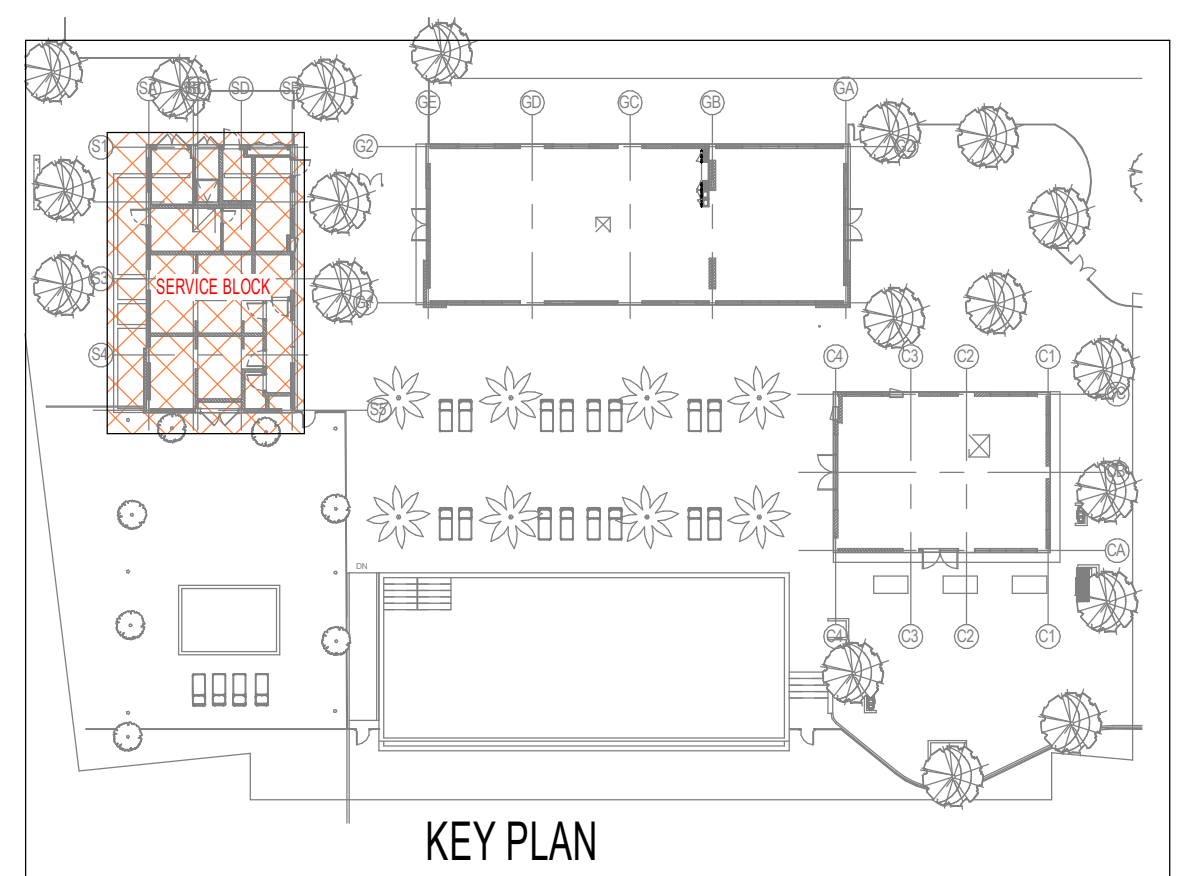

Key Plan

General Notes :

- Do not Scale The Drawings. Follow (The MM) Written Dimensions Unless Otherwise Mentioned.
- Each Drawing Shall be Read in Conjunction With all Other Drawings Specification & the General Standard Details. In Case of Any Discrepancies Bring it to the Knowledge of Engineer and Same to be Resolved Prior to Execution of Work.
- Dimensions Shown on These Drawings are Structural Dimensions. Unless Noted Otherwise.
- All Levels Indicated On These Drawings are Levels as per the the Survey Datum, Same Should be Verified at Site Prior to Execution of Work.
- All Levels Indicated On These Drawings are Based On Design Level, Which is Equivalent to Datum Level and Same Should be Verified at Site Prior to Execution of Work.

AB

TENDER DRAWINGS

اريف و بينطوك

00

10/03/2026

LSG

TENDER SUBMISSION

00

16/01/2026

LSG

DETAILED DESIGN SUBMISSION

00

31/10/2025

LSG

SCHEMATIC DESIGN SUBMISSION

00

15/10/2025

LSG

SCHEMATIC SUBMISSION-50%

00

01/09/2025

LSG

CONCEPT DESIGN SUBMISSION

No.

Date

Initials

Description

REVISIONS / ISSUE

THIS DRAWING MUST NOT BE REPRODUCED IN WHOLE OR IN PART WITHOUT THE PRIOR APPROVAL OF ARIF & BINTOAK

Status

TENDER SUBMISSION

Client

EMAAR

Lead Consultant

اريف و بينطوك
Arif & BintOak
consulting architects & engineers
POST BOX 5078 DUBAI- UAE TEL: 04-337288 FAX: 04-337030
POST BOX 5081 DUBAI- UAE TEL: 04-337030 arif@arifbintoak.com.ae

Project Title:

Proposed Residential Townhouses and Standalone Villas
TH-1, TH-2, and TH-3 at Grand Polo Club & Resort, Dubai, UAE

Discipline:

MECHANICAL

Drawing title:

SERVICE BLOCK
GROUND & FIRST FLOOR
VENTILATION LAYOUT

Architectural Engineer

Electrical Engineer

Structural Engineer

MUSTAFA ABID

MARWAN MOHD.

RIHAM RAMADAN

Registration # 80847

Registration # 80102

Registration # 105892

Scale(s):

Date:

Project no:

As Indicated

10/03/2026

1857

Drawn by:

Checked:

Approved:

LSG

MAV

MRM

Drawing Number:

GPCR-TH02-AB-DRG-ZZZ-MEC-HV-2402-00

This 2D drawing is extracted from 3D BIM Model

3/9/2026 10:02:40 AM

© AB 1 A1 Title Block - BIM Standard Ver: 2.0