



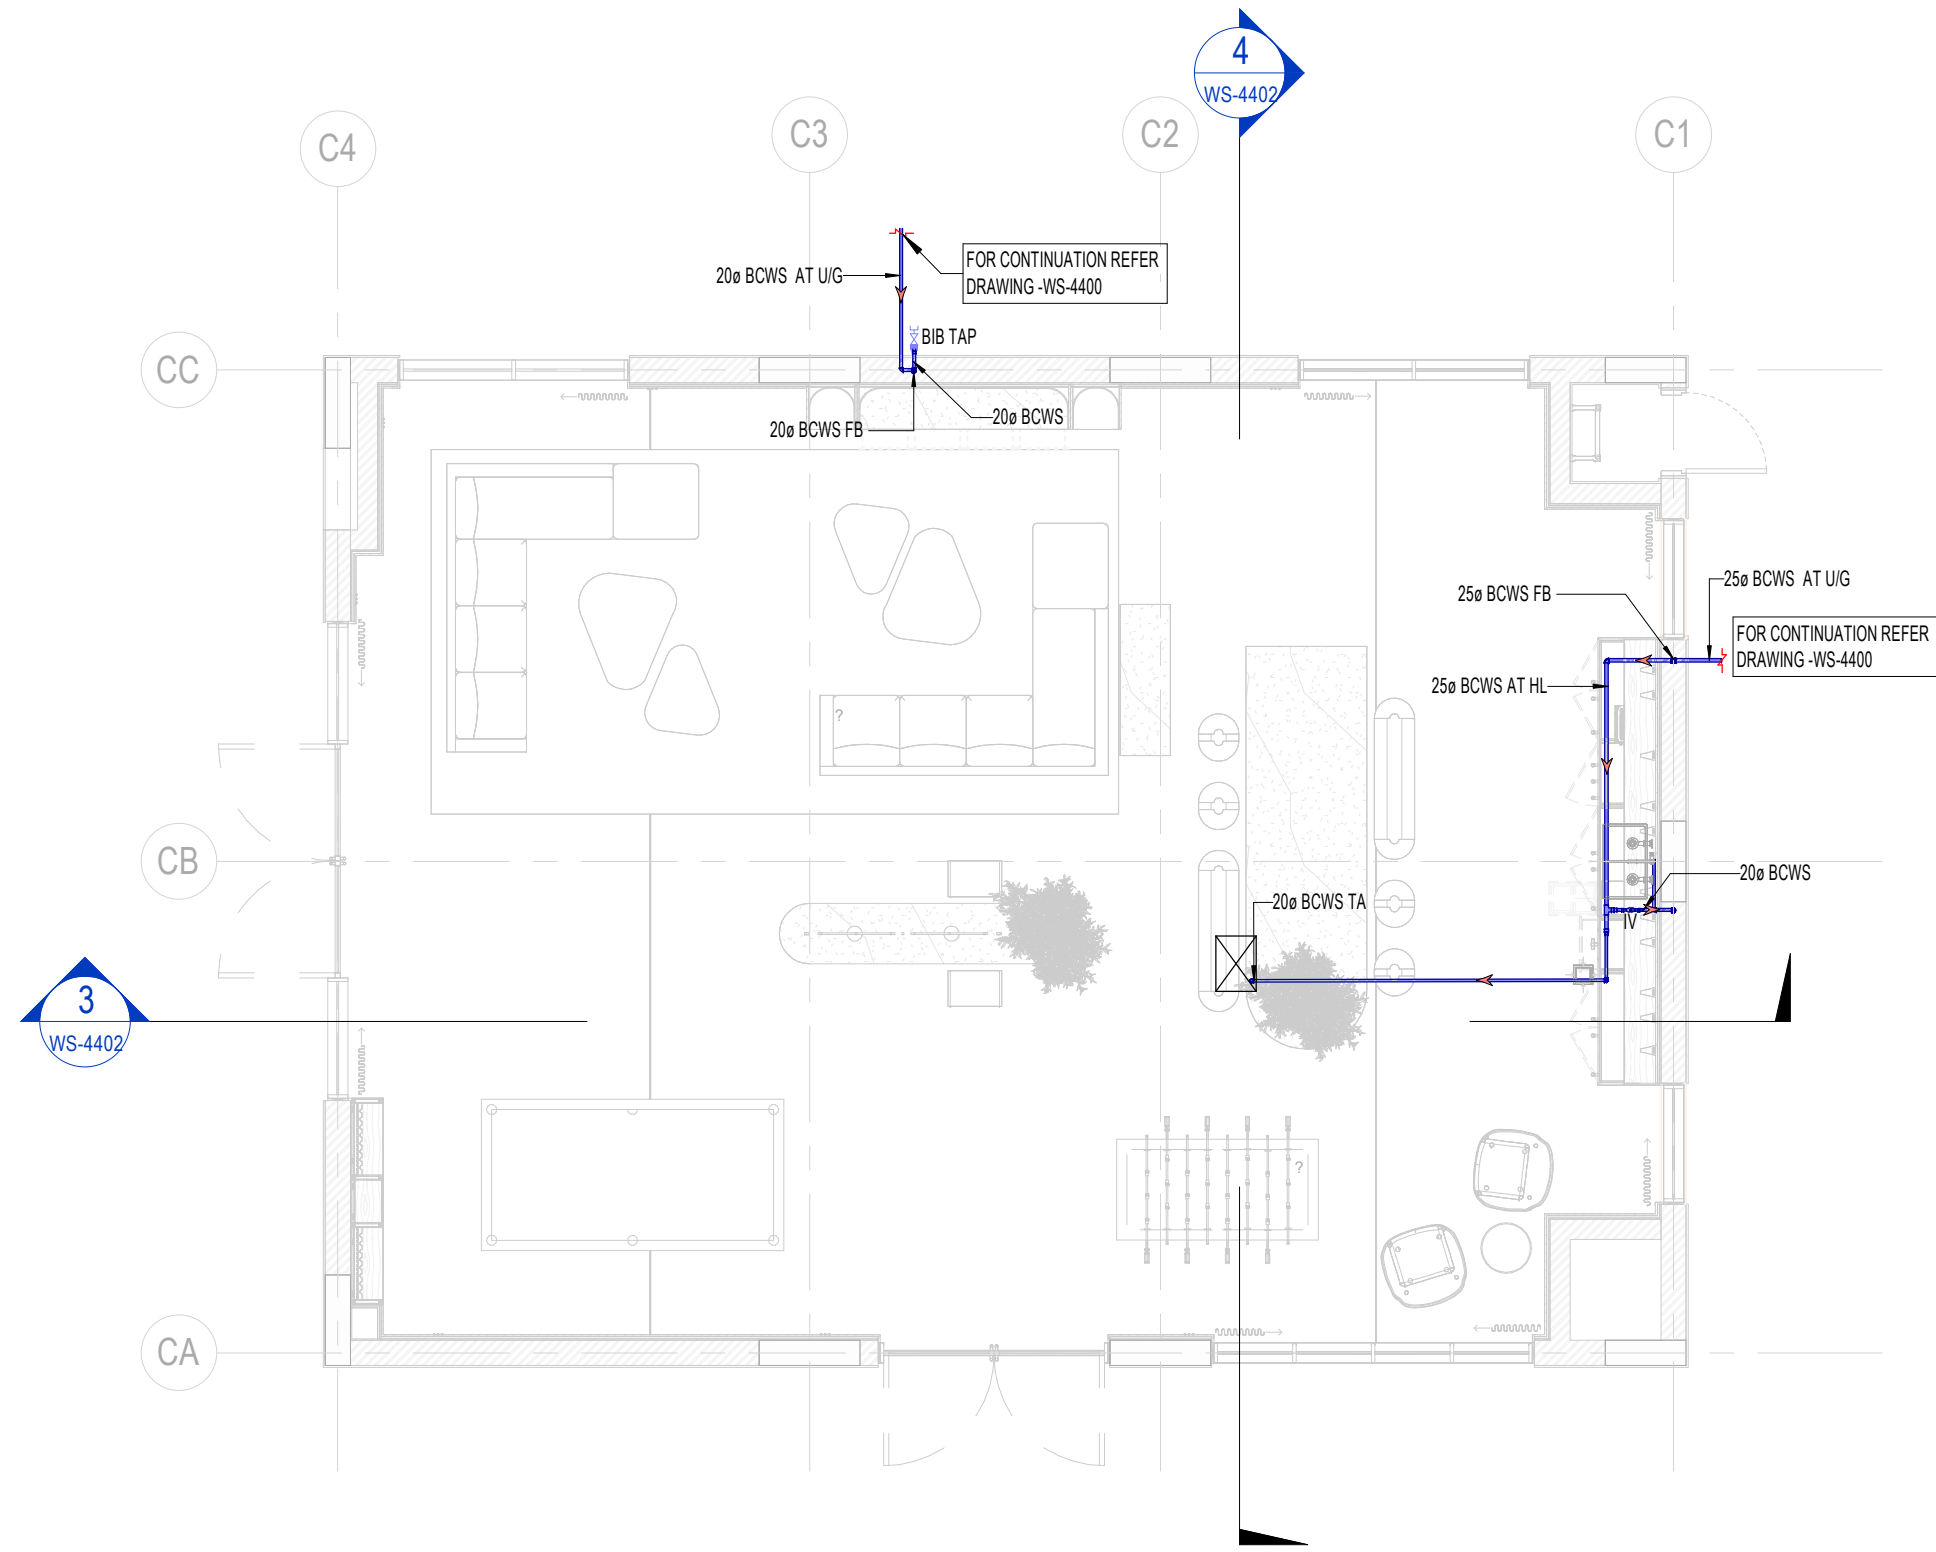


GROUND FLOOR WATER SUPPLY LAYOUT-COMMUNITY HALL

1 : 75

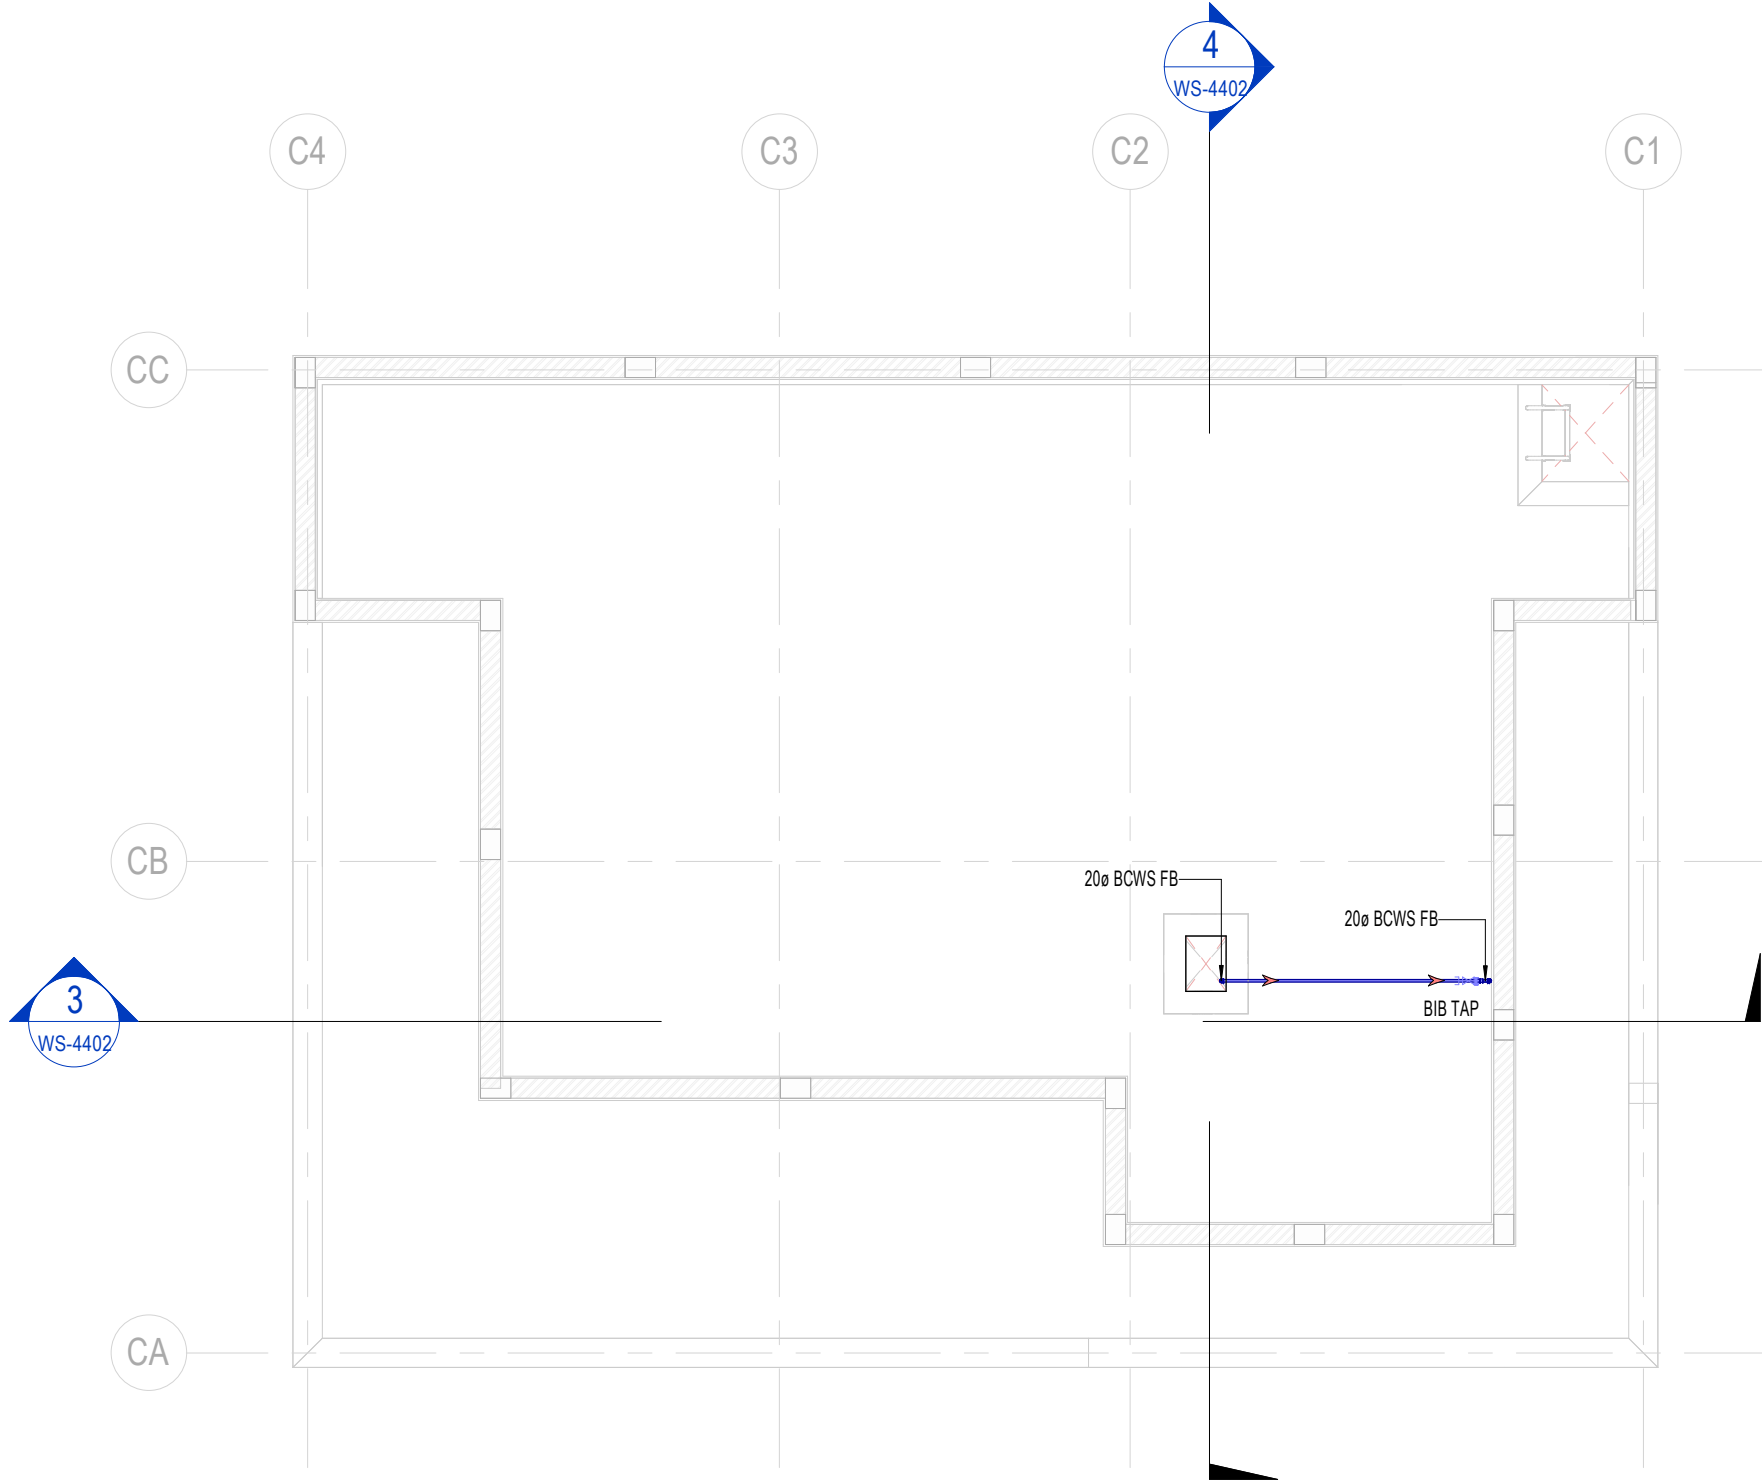


ROOF FLOOR WATER SUPPLY LAYOUT-COMMUNITY HALL

1 : 75

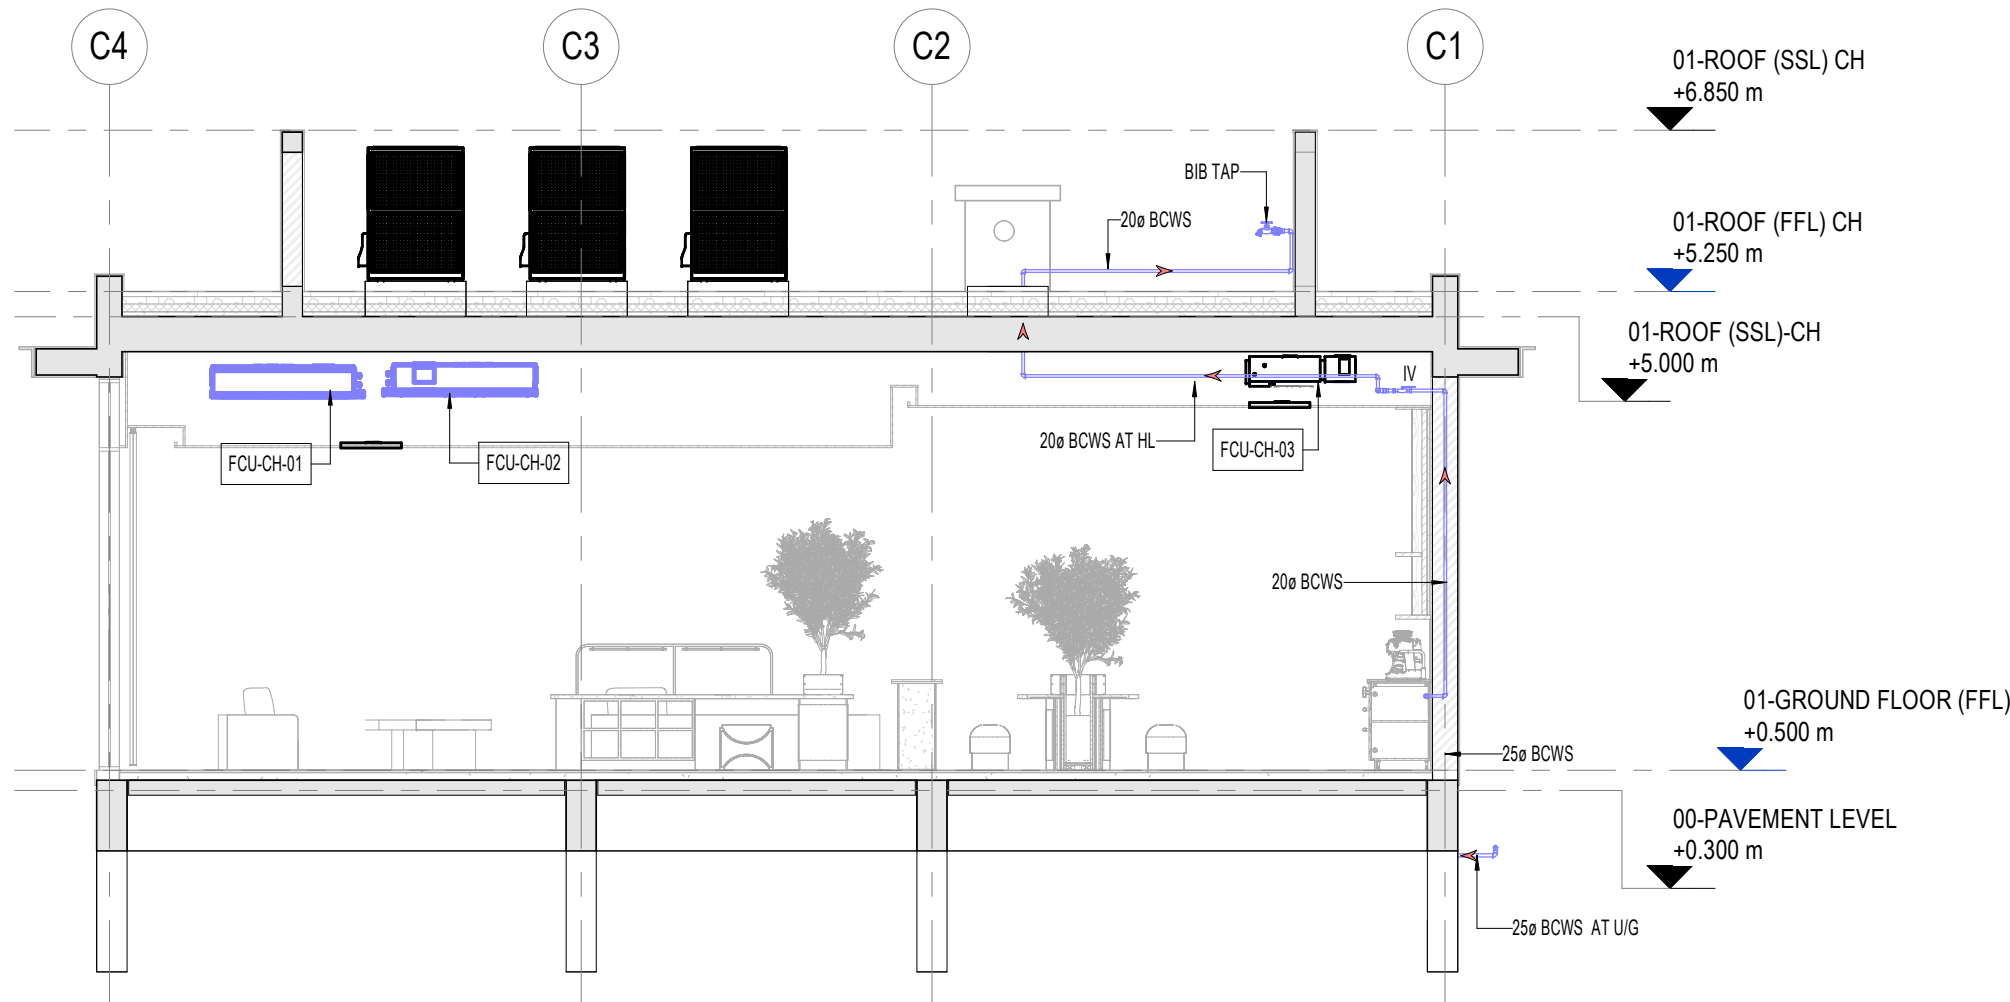


COMMUNITY HALL WATER SUPPLY SECTION 01

1 : 75

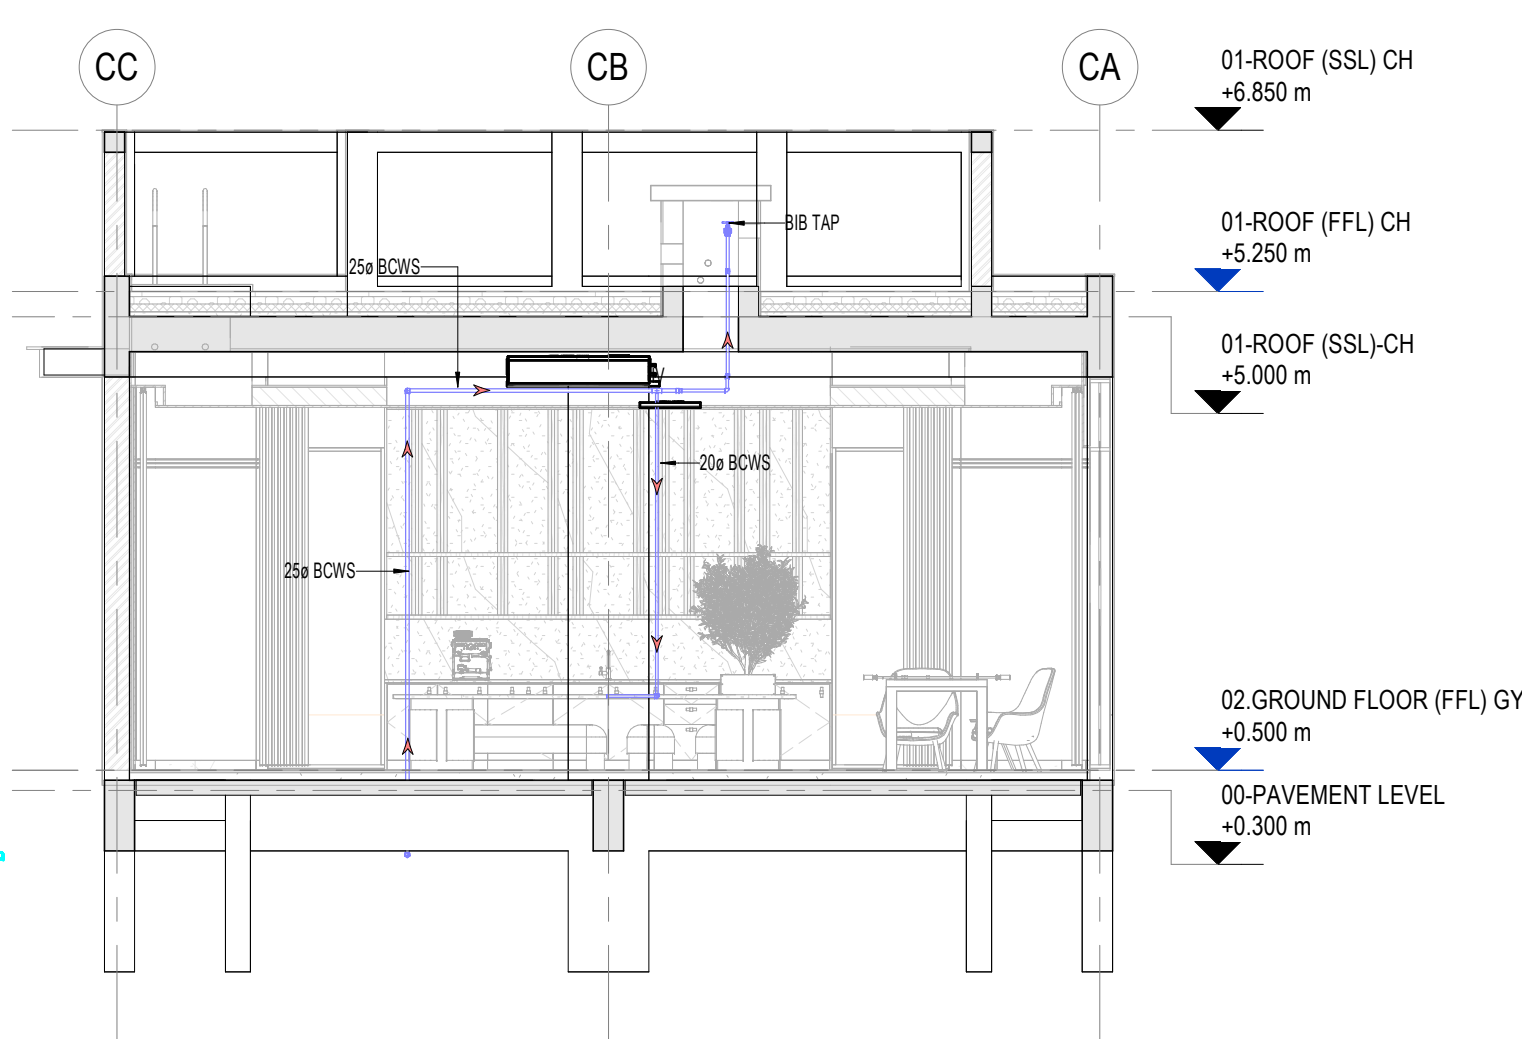

COMMUNITY HALL WATER SUPPLY SECTION 02

1 : 75

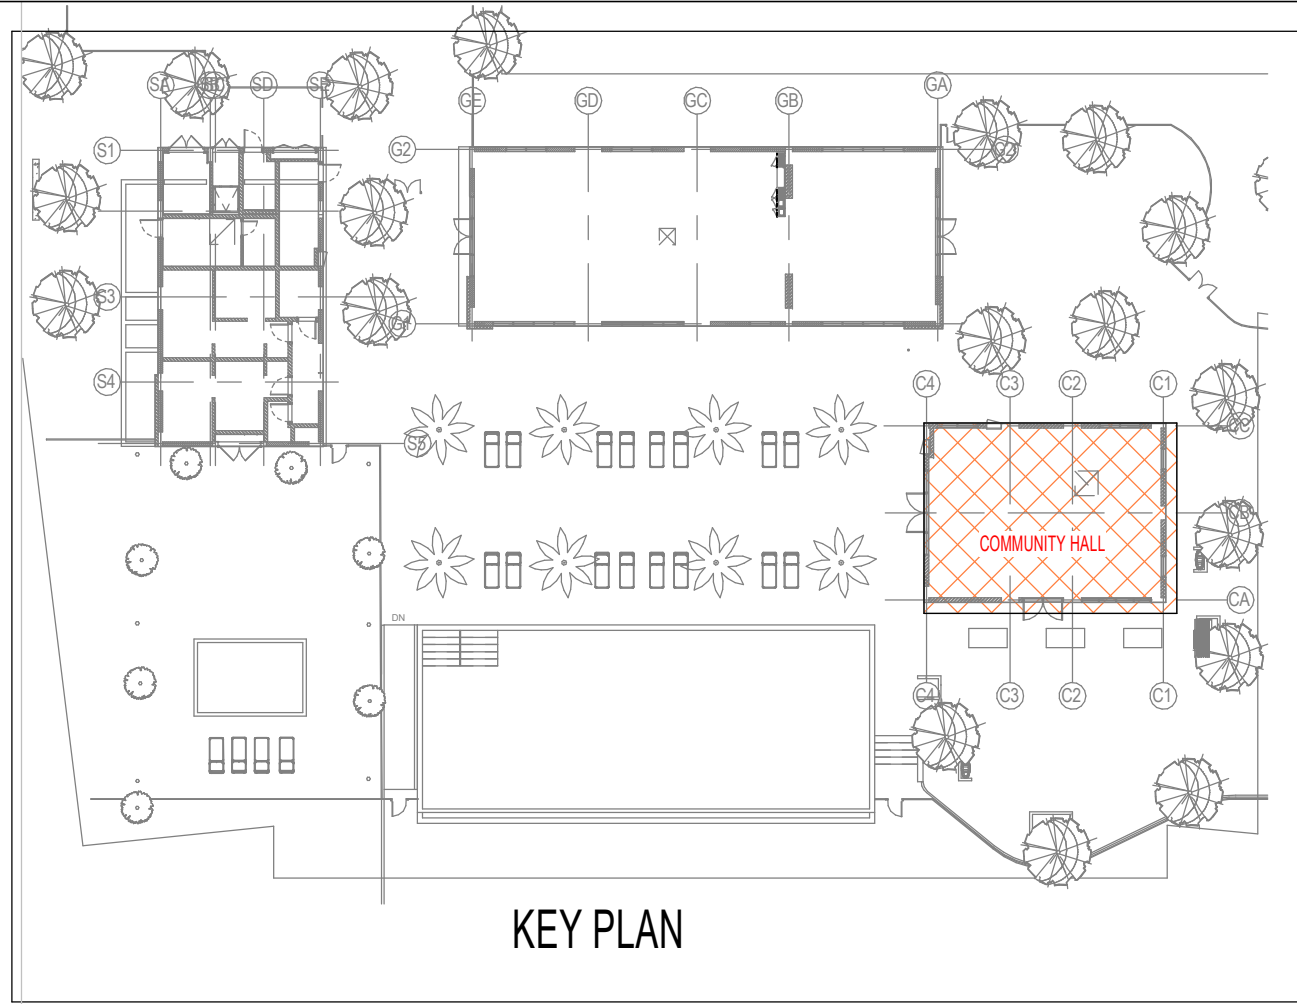


KEY PLAN

NOTE:  
THE PIPE SIZES ON DRAWINGS ARE BASED ON  
NOMINAL INTERNAL DIAMETER OF PPR PIPES  
CONTRACTOR TO PROVIDE OUTSIDE PPR PIPES  
DIAMETER ON SHOP DRAWINGS.  
EXTERNAL BIBTAP SHALL BE LOCKABLE TYPE.

| LEGENDS |                                    |
|---------|------------------------------------|
| CWS     | COLD WATER SUPPLY                  |
| HWS     | HOT WATER SUPPLY                   |
| GCWS    | GRAVITY COLD WATER SUPPLY          |
| BCWS    | BOOSTER COLD WATER SUPPLY          |
| CWTP    | COLD WATER TRANSFER PIPE           |
| WHA     | WATER HAMMER ARRESTER              |
| EWB     | ELECTRIC WATER HEATER              |
| IV      | ISOLATING VALVE                    |
| DRV     | DOUBLE REGULATING VALVE            |
| NRV     | NON RETURN VALVE                   |
| ST      | STRAINER                           |
| NC      | NORMALLY CLOSED VALVE              |
| NO      | NORMALLY OPENED VALVE              |
| WM      | WATER METER                        |
| BFP     | BACK FLOW PREVENTER                |
| TMV     | THERMOSTAT MIXING VALVE            |
| FA      | FROM ABOVE                         |
| FB      | FROM BELOW                         |
| TA      | TO ABOVE                           |
| TB      | TO BELOW                           |
| FB TA   | FROM BELOW TO ABOVE                |
| FA TB   | FROM ABOVE TO BELOW                |
| DTLL    | DOWN TO LOW LEVEL                  |
| RTHL    | RISE TO HIGH LEVEL                 |
|         | BOOSTER PUMP SET (10DUTY+1STANDBY) |

| PLUMBING FIXTURES FLOW |                                  |
|------------------------|----------------------------------|
| FIXTURE TYPE           | MAXIMUM FLOW RATE                |
| SHOWERHEADS            | 8 L/Min.                         |
| HAND WASHBASINS        | 6 L/Min.                         |
| KITCHEN SINKS          | 7 L/Min.                         |
| DUEL FLUSH TOILETS     | 6 L Full Flush<br>3 L Part Flush |

Key Plan

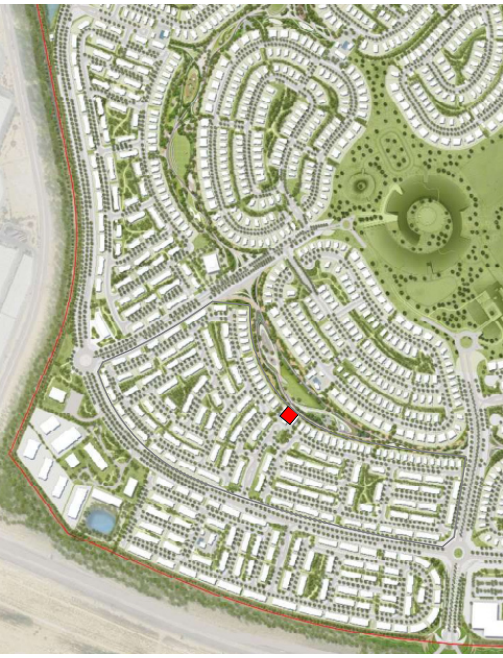

General Notes :

- Do not Scale The Drawings. Follow (The MM) Written Dimensions Unless Otherwise Mentioned.
- Each Drawing Shall be Read in Conjunction With all Other Drawings Specification & the General Standard Details. In Case of Any Discrepancies Bring it to the Knowledge of Engineer and Same to be Resolved Prior to Execution of Work.
- Dimensions Shown on These Drawings are Structural Dimensions. Unless Noted Otherwise.
- All Levels Indicated On These Drawings are Levels as per the Survey Datum, Same Should be Verified at Site Prior to Execution of Work.
- All Levels Indicated On These Drawings are Based On Design Level, Which is Equivalent to Datum Level and Same Should be Verified at Site Prior to Execution of Work.



| No. | Date       | Initials | Description                 |
|-----|------------|----------|-----------------------------|
| 00  | 10/03/2024 | LSG      | TENDER SUBMISSION           |
| 00  | 16/01/2024 | LSG      | DETAILED DESIGN SUBMISSION  |
| 00  | 31/10/2025 | LSG      | SCHEMATIC DESIGN SUBMISSION |
| 00  | 15/10/2025 | LSG      | SCHEMATIC SUBMISSION-50%    |
| 00  | 01/09/2025 | LSG      | CONCEPT DESIGN SUBMISSION   |

REVISIONS / ISSUE

THIS DRAWING MUST NOT BE REPRODUCED IN WHOLE OR IN PART WITHOUT THE PRIOR APPROVAL OF ARIF & BINTOAK

Status: TENDER SUBMISSION

Client: EMAAR

Lead Consultant: Arif & BintOak

Project Title: Proposed Residential Townhouses and Standalone Villas TH-1, TH-2, and TH-3 at Grand Polo Club & Resort, Dubai, UAE

Discipline: MECHANICAL

Drawing title: COMMUNITY HALL GROUND & ROOF FLOOR WATER SUPPLY LAYOUT

| Architectural Engineer                              | Electrical Engineer  | Structural Engineer   |
|-----------------------------------------------------|----------------------|-----------------------|
| MUSTAFA ABID                                        | MARWAN MOHD.         | RIHAM RAMADAN         |
| Registration # 5847                                 | Registration # 60102 | Registration # 105092 |
| Scale(s): As indicated                              | Date: 10/03/2026     | Project no: 1857      |
| Drawn by: LSG                                       | Checked: MAV         | Approved: MRM         |
| Drawing Number: GPCR-TH02-AB-DRG-ZZZ-MEC-WS-4402-00 |                      |                       |