


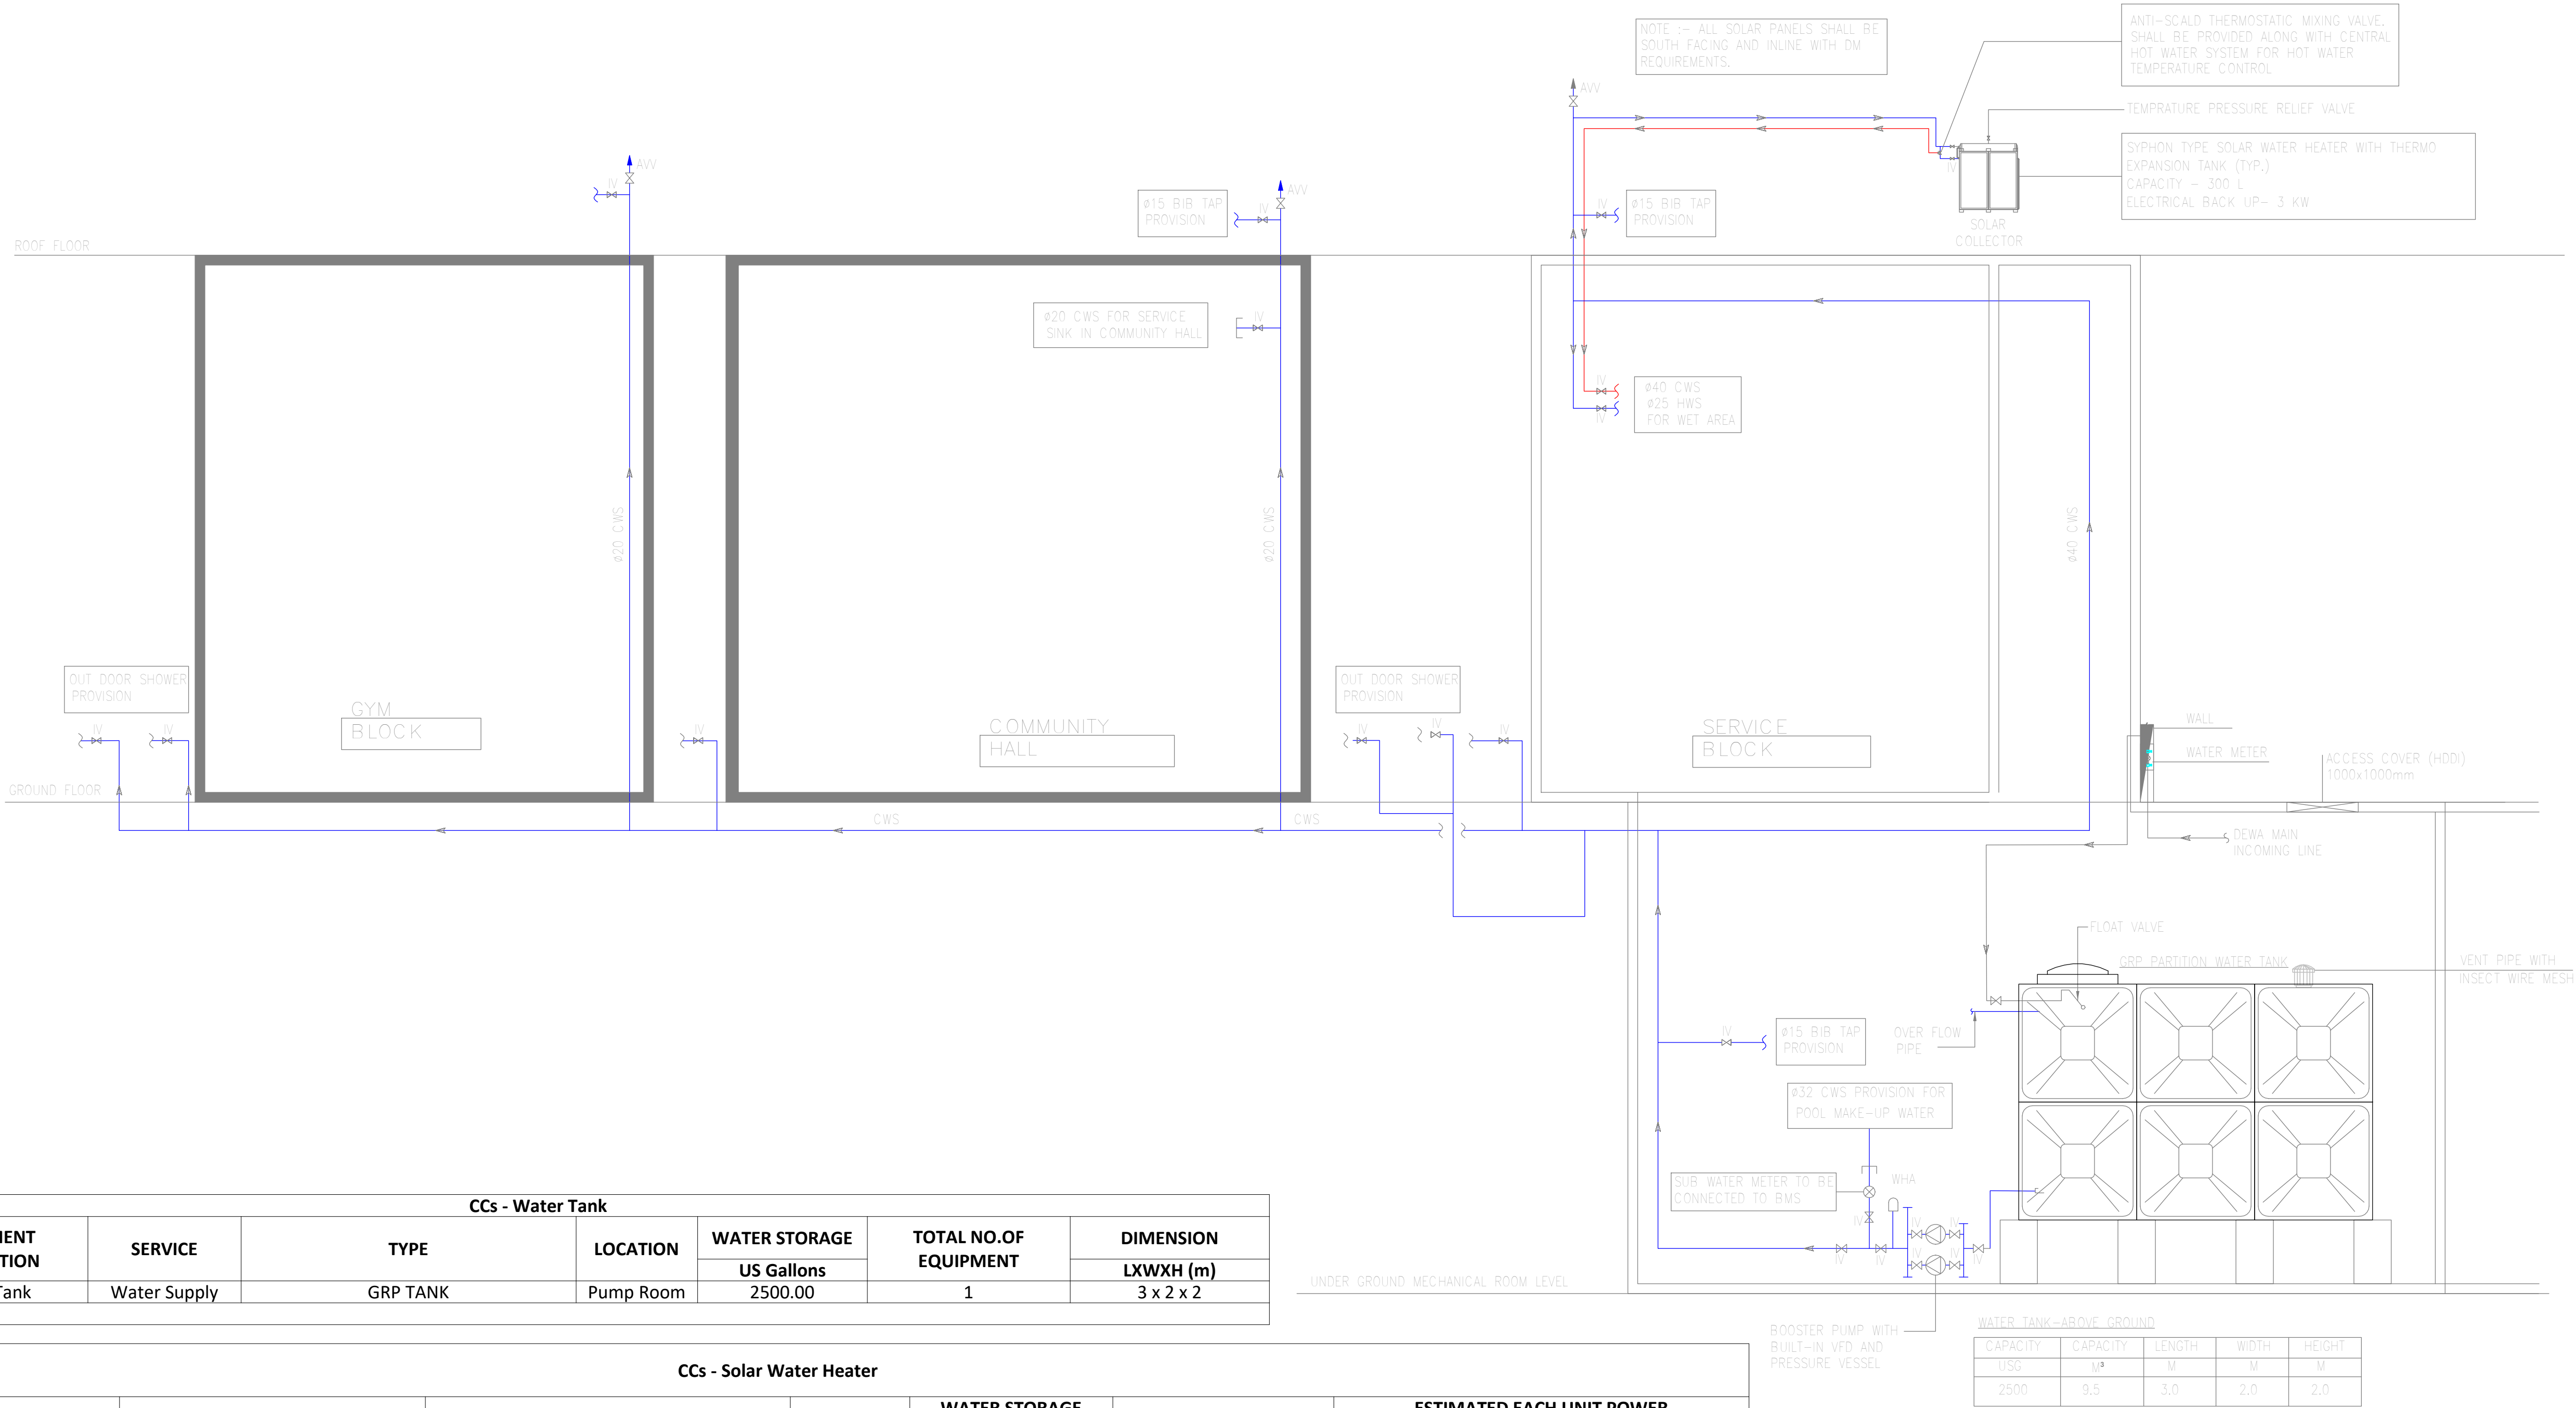


CCs - Water Tank							
SI No	EQUIPMENT DESCRIPTION	SERVICE	TYPE	LOCATION	WATER STORAGE	TOTAL NO.OF EQUIPMENT	DIMENSION
					US Gallons		LXWXH (m)
1	Water Tank	Water Supply	GRP TANK	Pump Room	2500.00	1	3 x 2 x 2

CCs - Solar Water Heater							
SI No	EQUIPMENT DESCRIPTION	SERVICE	TYPE	LOCATION	WATER STORAGE	TOTAL NO.OF EQUIPMENT	ESTIMATED EACH UNIT POWER
					LITERS		kW
1	Water Heater	Hot domestic water	Solar water heater with an electrical backup	Roof	300.00	1	3


CCs PUMP SCHEDULE											
SI No	EQUIPMENT DESCRIPTION	SERVICE	TYPE	LOCATION	FLOW	HEAD	TOTAL NO.OF PUMP SETS	NO.OF PUMPS			REMARK
					(L/s)	(m)		DUTY	ASSIST	S/BY	
1	Water Booster pump	Water Booster pumps	Compact Horizontal End Suction Built In VFD	Pump room	1.60	30	1	1	0	1	Skid Mounted Smart Starter Panel, pump shall be Built In VFD, Controlled by PLC of the packaged unit, with a built in pressure vessel.
2	Sump Pumps	Sump pit	Submerssible Pump	Pump room	1.20	15	1	1	0	1	Controlled by Level Switch
NOTES:											
1 - CONTRACTOR SHALL PROVIDE THE PUMP HEAD CALCULATION BASED ON INSTALLED PIPING CONNECTIONS, FITTINGS AS PER SITE CONDITION FOR ENGINEERS APPROVAL.											

Key Plan

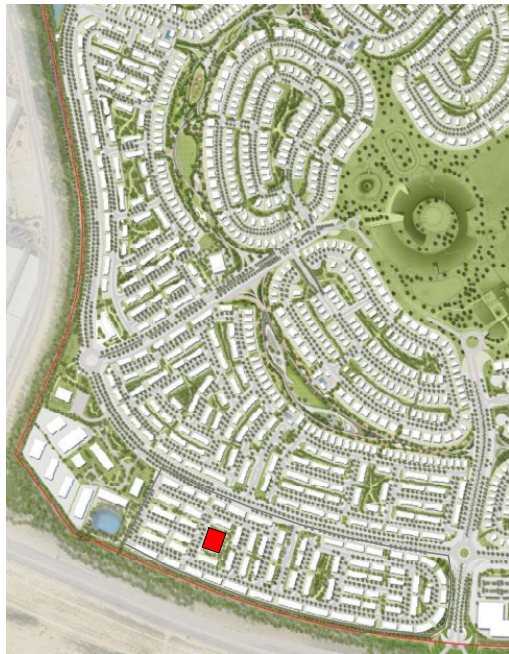

General Notes :

01. Do not Scale The Drawings. Follow (The MM) Written Dimensions Unless Otherwise Mentioned.
02. Each Drawing Shall be Read in Conjunction With all Other Drawings Specification & the General Standard Details. In Case of Any Discrepancies Bring it to the Knowledge of Engineer and Same to be Resolved Prior to Execution of Work.
03. Dimensions Shown on These Drawings are Structural Dimensions. Unless Noted Otherwise.
04. All Levels Indicated On These Drawings are Levels as per the Survey Datum, Same Should be Verified at Site Prior to Execution of Work.
05. All Levels Indicated On These Drawings are Based On Design Level, Which is Equivalent to Datum Level and Same Should be Verified at Site Prior to Execution of Work.

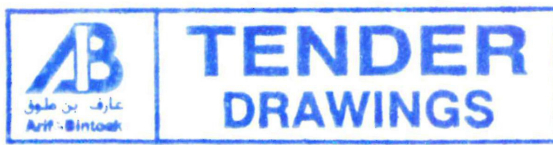

00	10/03/2026	LSG	TENDER SUBMISSION
00	16/01/2026	LSG	DETAILED DESIGN SUBMISSION
00	31/10/2025	LSG	SCHEMATIC DESIGN SUBMISSION
00	15/10/2025	LSG	SCHEMATIC SUBMISSION-50%
00	01/09/2025	LSG	CONCEPT DESIGN SUBMISSION

REVISIONS / ISSUE

THIS DRAWING MUST NOT BE REPRODUCED IN WHOLE OR IN PART WITHOUT THE PRIOR APPROVAL OF ARIF & BINTOAK

TENDER SUBMISSION

Client

EMAAR

Lead Consultant

المستشارون:
Arif & Bintook
consulting architects & engineers
POST BOX 5070 DUBAI UAE TEL: 04-3372886 FAX: 04-3372832
POST BOX 62081 ABU DHABI UAE TEL: 02-6246600 - arif@arifbintook.net.ae

Project Title:

Proposed Residential Townhouses and Standalone Villas
TH-01, TH-02, and TH-03 at Grand Polo Club & Resort, Dubai, UAE

Discipline: **MECHANICAL**

Drawing title:

COMMUNITY CENTER WATER SUPPLY RISER DIAGRAM

Architectural Engineer: MUSTAFA ABID

Electrical Engineer: MARWAN MOHD.

Structural Engineer: RIHAM RAMADAN

Registration # 5847

Registration # 60102

Registration # 105092

Scale(s): 1 : 1

Date: 10/03/2026

Project no: 1857

Drawn by: LSG

Checked: MAV

Approved: MRM

Drawing Number: GPCR-TH02-AB-DRG-ZZZ-MEC-WS-4404-00